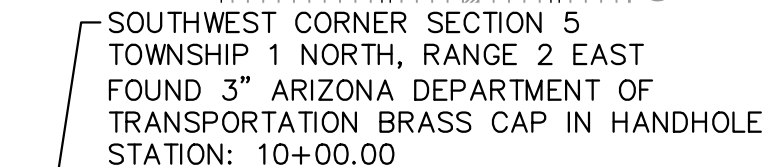


[illegible]

SOUTH QUARTER CORNER SECTION 5
TOWNSHIP 1 NORTH, RANGE 2 EAST
FOUND 3" MARICOPA COUNTY BRASS
CAP IN HANDHOLE
STATION: 36+58.98

1. ALL SEWER LINES MUST MAINTAIN AT LEAST 3 FEET OF BACKFILL COVER.
2. CONTRACTOR MUST PERFORM DEFLECTION TEST OF THE TOTAL LENGTH OF ALL SEWER LINES MADE OF FLEXIBLE MATERIALS TO ENSURE THAT THE INSTALLATION MEETS OR EXCEEDS THE MANUFACTURER'S RECOMMENDATIONS AND RECORD THE RESULTS.
3. CONTRACTOR MUST TEST EACH SEGMENT OF THE SEWER LINE FOR LEAKAGE USING AN APPLICABLE METHOD LOCATED IN THE ARIZONA ADMINISTRATIVE CODE R18-9-E301-D-2-J, AND RECORD THE RESULTS.
4. CONTRACTOR MUST TEST THE TOTAL LENGTH OF THE SEWER LINE FOR UNIFORM SLOPE BY LAMP LIGHTING, REMOTE CAMERA OR SIMILAR METHOD APPROVED BY THE ARIZONA DEPARTMENT OF ENVIRONMENTAL QUALITY, AND RECORD THE RESULTS.
5. CONTRACTOR SHALL TEST MANHOLES USING ONE OF THE METHODS SPECIFIED IN THE ARIZONA ADMINISTRATIVE CODE R18-9-E301-D-3-F, AND RECORD THE RESULTS.
6. CONTRACTOR SHALL PERFORM MANHOLE TESTING UNDER THE ARIZONA ADMINISTRATIVE CODE R18-9-E301-D-3-F AFTER INSTALLATION OF THE MANHOLE CONE TO VERIFY WATERTIGHTNESS OF THE MANHOLE FROM THE TOP OF THE CONE DOWN.
7. KIMLEY-HORN AND ASSOCIATES, INC. (KHA) HAS BEEN RETAINED TO OBSERVE THE SEWER CONSTRUCTION AND SIGN, SEAL, AND SUBMIT AN ENGINEER'S CERTIFICATE OF COMPLETION TO ARIZONA DEPARTMENT OF ENVIRONMENTAL QUALITY IN A FORMAT APPROVED BY THE DEPARTMENT CONTAINING ITEMS LISTED IN THE ARIZONA ADMINISTRATIVE CODE R18-9-E301-E-1. CONTRACTOR SHALL NOTIFY KHA (602 944-5500) 48 HOURS PRIOR TO SEWER MAIN EXCAVATION, INSTALLATION, OR TESTING.
8. CONTRACTOR TO VERIFY SIZES AND INVERTS OF EXISTING SEWER AND CONTACT DESIGN ENGINEER IF DIFFERENT FROM SHOWN.
9. SEE GRADING PLAN FOR PROPOSED SURFACE ELEVATIONS.
10. STATIONS AND OFFSETS ARE BASED ON VAN BUREN STREET CENTERLINE.

I HEREBY CERTIFY THAT THE "RECORD DRAWING"
MEASUREMENTS AS SHOWN HEREON WERE MADE UNDER
MY SUPERVISION OR AS NOTED AND ARE CORRECT TO
THE BEST OF MY KNOWLEDGE AND BELIEF.

ARIZONA REGISTERED ENGINEER/LAND SURVEYOR DATE

	AREA	DEMAND RATE	AVERAGE DAY DEMAND	PEAK FLOW
BUILDING F	301,711 SF	25 GPD/1,000 SF	7,550 GPD (5.24 GPM)	20.88 GPM (30,067 GPD)
BUILDING G	295,586 SF	25 GPD/1,000 SF	7,400 GPD (5.14 GPM)	20.46 GPM (29,462 GPD)
BUILDING H	227,107 SF	25 GPD/1,000 SF	5,700 GPD (3.96 GPM)	15.76 GPM (22,694 GPD)

PEAK FLOW INCLUDES A DRY WEATHER PEAKING FACTOR OF 3.62 AND WET WEATHER/INFILTRATION FACTOR OF 10%



PER SURVEY INNOVATION GROUP, THE BASIS OF BEARING IS:
THE SOUTH LINE OF THE SOUTHWEST QUARTER OF SECTION 5 AS
SHOWN IN BOOK 821, PAGE 45 MARICOPA COUNTY RECORDS. SAID
LINE BEARS SOUTH 87 DEGREES 46 MINUTES 44 SECONDS EAST.

PER SURVEY INNOVATION GROUP THE BENCHMARK IS:
PRIMARY
FOUND 3" CITY OF PHOENIX BRASS CAP IN HANDHOLE AT THE
INTERSECTION OF 51ST AVENUE AND VAN BUREN STREET.
ELEVATION = 1058.039 (CITY OF PHOENIX, NGVD29)

SECONDARY
S.R.V.U.A. BRASS CAP ON SOUTH SIDE OF IRRIGATION BOX, ON
SOUTHWEST CORNER OF THE INTERSECTION OF 51ST AVENUE AND
ROOSEVELT STREET
ELEVATION = 1069.115 (CITY OF PHOENIX, NGVD29)

SHEET INDEX		
NO.	SHEET	TITLE
1	UT1	COVER SHEET
2-3	UT2-UT3	UTILITY PLAN


NOTE TO CONTRACTOR:
KIMLEY-HORN AND ASSOCIATES HAS
BEEN CONTRACTED TO OBSERVE THE
INSTALLATION AND TESTING OF THE
ON-SITE PRIVATE SEWER MAIN.
CONTRACTOR SHALL CONTACT
KIMLEY-HORN AND ASSOCIATES 48
HOURS PRIOR TO SEWER MAIN
INSTALLATION, EXCAVATION, AND TESTING.

<u>CIVIL ENGINEER</u>	<u>ARCHITECT</u>
KIMLEY-HORN AND ASSOCIATES, INC.	CALVIN J. COATSWORTH ARCHITECTS, PC
1661 EAST CAMELBACK ROAD,	1574 GULF ROAD PMB 212
SUITE 400	POINT ROBERTS, WA 98281
PHOENIX, AZ 85016	PH: (949) 833-1930
PH: (602) 944-5500	CONTACT: CALVIN COATSWORTH, AIA
CONTACT: TRAVER JONES, PE	

<u>LAND SURVEYOR</u>	<u>OWNER</u>
SURVEY INNOVATION GROUP, INC 22425 N 16TH STREET, SUITE 1 PHOENIX, AZ 85024 PH: (480) 922-0708 CONTACT: JARED HANSMANN, RLS	SOUTHERN CROSS, LLC 3131 E. CAMELBACK RD, STE 310 PHOENIX, AZ 85016 OFFICE: (602) 279-3999 CONTACT: TOM TAIT, SR.

OWNER
SOUTHERN CROSS, LLC
3131 E. CAMELBACK RD, STE 310
PHOENIX, AZ 85016
OFFICE: (602) 279-3999
CONTACT: TOM TAIT, SR.

1. ALL PIPE ELEVATIONS ARE INVERT ELEVATIONS UNLESS OTHERWISE NOTED.
2. ADD 1000' TO ALL ELEVATIONS.
3. ALL PVC C900 PIPE AND FITTINGS SHALL CONFORM TO NSF 61.

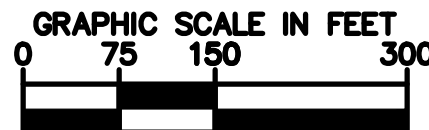

LPRM: _____
KIVA: 20-4327
SDEV: 2007995
QS: 11-15
ZONING: A-1, A-2



Kimley»»Horn

CAPROCK PARTNERS



1 AVE, 555 N. 55TH AVE, & 5400 W. VAN
BUREN STREET

COVER SHEET

PHOENIX, ARIZONA 85043

PROJECT No. 291367006
SCALE (H): 1"=150'
SCALE (V): NONE
DRAWN BY: CAF
DESIGN BY: BEQ
CHECK BY: TMJ
DATE: 07/30/24



UT1


1 OF 3 SH

K:\PKI_Owl\291367006 -- Project Lima\CAD\Improvement Plans\Phase 3\3670060U_P13.dwg, layout:UT2 Jul 30, 2024 -- 4:34pm Ashton,Dial



- NOTES:**
1. STATIONS AND OFFSETS ARE BASED ON THE VAN BUREN STREET CENTERLINE.
 2. ALL PIPE ELEVATIONS ARE INVERT ELEVATIONS UNLESS OTHERWISE NOTED.
 3. ADD 1000' TO ALL ELEVATIONS.
 4. ALL PVC C900 PIPE AND FITTINGS SHALL CONFORM TO NSF 61.

1. INSTALL 3" SCH 40 PVC WATER SERVICE, LENGTH PER PLAN. 3' MINIMUM COVER.
2. DOMESTIC WATER BUILDING CONNECTION, REF MEP PLANS FOR CONTINUATION.
3. 1-1/2" IRRIGATION WATER METER TO BE INSTALLED IN EXISTING METER BOX BY CITY FORCES PER COP STD DET P1342 AND P1363.
4. 2" DOMESTIC WATER METER TO BE INSTALLED IN EXISTING METER BOX BY CITY FORCES PER COP STD DET P1342 AND P1363.
5. INSTALL 1-1/2" FEBCO LF 825Y IRRIGATION WATER BACKFLOW PREVENTOR OR APPROVED EQUAL, PER COP STD DET P1354. REF LANDSCAPE PLANS FOR PROTECTIVE CAGE DETAILS AND CONTINUATION.
6. INSTALL 3" WATTS SERIES 957 DOMESTIC WATER BACKFLOW PREVENTOR, OR APPROVED EQUAL, PER COP STD DET P1351. REF LANDSCAPE PLANS FOR PROTECTIVE CAGE DETAILS.
7. CONNECT TO EXISTING WATER SERVICE SUB. CONTRACTOR SHALL POTHOLE EXISTING WATER MAIN TO VERIFY LOCATION AND ELEVATION PRIOR TO CONSTRUCTION. CONTACT ENGINEER IN CASE OF ANY DISCREPANCIES.
8. INSTALL 2" SCH 40 PVC IRRIGATION SERVICE, LENGTH PER PLAN. 3' MINIMUM COVER.
9. INSTALL 2" SCH 40 PVC WATER SERVICE, LENGTH PER PLAN. 3' MINIMUM COVER.

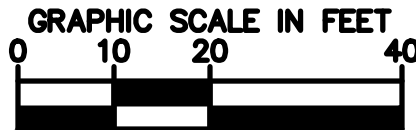

675 N. 55TH AVE., 555 N 55TH AVE, & 5400 W. VAN
BUREN STREET
UTILITY PLAN
PHOENIX, ARIZONA 85043

PROJECT No.
291367006
SCALE (H): 1"=20'
SCALE (V): NONE
DRAWN BY: CAF
DESIGN BY: BEQ
CHECK BY: TMJ
DATE: 07/30/24



UT2
2 OF 3 SHEETS

Kimley»»Horn
© 2024 KIMLEY-HORN AND ASSOCIATES, INC.
1661 EAST CAMELBACK ROAD, SUITE 400
Phoenix, Arizona 85016 (602) 944-5500

