

BUILDING E
19,880 S.F.
15,000 S.F. LARGE GARAGE - 1ST FLR
4,480 S.F. GARAGE MEZZANINES
400 S.F. ELECTRICAL
10 UNITS

POTENTIAL INTERNAL GATED
DRIVEWAY CONNECTION IF WESTERN
LOT IS USED BY FINISH LINE

PROPOSED PROPERTY LINE

ELEC. ROOM, TYP.

FDC, TYP.

FIRE PUMP ROOM, TYP.

TELESCOPING
SECURITY GATE WITH
KEY SWITCH / PRE-
EMPTION SENSOR

PROPOSED WASHING STATION
WITH GREASE, OIL AND SAND
INTERCEPTORS - FINAL
LOCATION TBD.

UTILITY EASEMENT

BUILDING C
18,542 S.F.
13,200 S.F. LARGE GARAGE - 1ST FLR
3,936 S.F. GARAGE MEZZANINES
1,040 S.F. SMALL GARAGE
366 S.F. ELECTRICAL
10 UNITS

BUILDING A
67,530 S.F.
(EXCLUDES INTERIOR AISLE)
41,234 S.F. LARGE GARAGE - 1ST FLR
11,788 S.F. GARAGE MEZZANINES
10,525 S.F. OFFICE / LOUNGE
3,391 S.F. 3RD FLOOR PATIO
592 S.F. ELECTRICAL
25 UNITS

BUILDING B
19,190 S.F.
14,400 S.F. LARGE GARAGE - 1ST FLR
4,296 S.F. GARAGE MEZZANINES
494 S.F. ELECTRICAL
8 UNITS

EXISTING
BUILDING - N.I.C.

EXISTING ADJACENT
DRIVE ENTRY

1' VEHICULAR
NON-ACCESS EASEMENT

STANDARD PARKING
SPACE DIMENSION, TYP.

FIRE TURNING RADIUS, TYP.
(25' INNER/ 49' OUTSIDE / 55' BUCKET SWING)

ACCESSIBLE PARKING
SPACE DIMENSION, TYP.

(2) BIKE RACKS (4 SPACES)

12' WATER EASEMENT (TO BE
REMOVED OR RELOCATED)

6' WIDE SIDEWALK - TYP.

ACCESSIBLE PATH OF
TRAVEL FROM PUBLIC WAY

PROPOSED DRIVE ENTRY TO
ALIGN WITH EXISTING
(REQUIRES VNAE MODIFICATION)

3' PARKING
SCREEN WALL, TYP.

20' STREET LANDSCAPING

FIRE RISER ROOM

DROP-OFF ZONE

GATES WITH KEY SWITCH /
PRE-EMPTION SENSOR, TYP.

PERIMETER DRIVE

PROVIDE 8' SIDEWALK
ALONG PERIMETER DRIVE

1' VEHICULAR
NON-ACCESS EASEMENT

8' P.U.E.


20' STREET LANDSCAPING

PROVIDE 8' SIDEWALK
ALONG PERIMETER DRIVE

WATER EASEMENT

EMERGENCY
ACCESS GATE WITH
KEY SWITCH / PRE-
EMPTION SENSOR

PROPOSED PARKING
CONFIGURATION FOR
SOUTH PARCEL

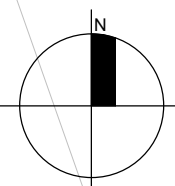

PROJECT DATA

AUTO CLUB - EAST LOT

PROJECT ADDRESS:	17600 N PERIMETER DR 100 SCOTTSDALE 85255
OWNER:	FINISH LINE AUTO CLUB 3080 AIRWAY AVE. COSTA MESA, CA 92626 TONY PRINCE
ARCHITECT:	LGE DESIGN GROUP 1200 NORTH 52ND STREET PHOENIX, AZ 85008 STUDIO DIRECTOR: MARK S. CONE
PROJECT SCOPE:	APPROXIMATELY 92,502 SF OF: AUTO CONDOS (67 TOTAL UNITS) 13,916 SF OF: OFFICE / CLUBHOUSE
ASSESSOR PARCEL NO.:	215-07-230
CURRENT ZONING:	I-1 PCD
PROPOSED ZONING:	I-1 PCD
SITE AREA:	+/- 293,754 S.F. (6.74 AC)
FAR - MAX:	0.80 = 235,003 S.F.
FAR - PROPOSED:	0.46 = 136,003 S.F.
*IN CONFORMANCE WITH THE I-1 DEVELOPMENT STANDARDS	
STORIES:	(3) STORY (BUILDING A) (1) STORY (BUILDING B) (1) STORY (BUILDING C) (1) STORY (BUILDING D) (1) STORY (BUILDING E)
GROSS BUILDING S.F.:	136,003 S.F. TOTAL 67,491 S.F. (BUILDING A) 19,173 S.F. (BUILDING B) 18,509 S.F. (BUILDING C) 10,903 S.F. (BUILDING D) 19,927 S.F. (BUILDING E)
LOT COVERAGE:	37%
OCCUPANCY:	A / S-1
CONSTRUCTION TYPE:	V-B W/ A.F.E.S.
BUILDING HEIGHT:	49'-0" (BUILDING A) 32'-0" (BUILDING B) 32'-0" (BUILDING C) 32'-0" (BUILDING D) 32'-0" (BUILDING E)

PROJECT DESCRIPTION:

THE FINISH LINE AUTO CLUB PROJECT CONSISTS OF FIVE BUILDINGS (GARAGES WITH AN OFFICE AND CLUB SPACE) ON A 6.74 ACRE SITE LOCATED ON N PERIMETER DRIVE WHICH CURRENTLY HAS ONE BUILDING.

REQUIRED PARKING:

CLUB (LOUNGE & PATIO)	11,537 S.F. / 250:	47 SPACES
OFFICE: 2,379 S.F. / 300=		8 SPACES
STORAGE (150 UNITS): 68 UNITS/50 =		2 SPACES
TOTAL REQUIRED=		57 SPACES

PROVIDED PARKING=	105 SPACES
REGULAR PARKING=	99 SPACES

ACCESSIBLE PARKING REQUIRED=	106'0.04 = 5
ACCESSIBLE PARKING PROVIDED=	6 SPACES

REQUIRED EV CHARGING (4% OF PARKING):	106'0.04 = 5
PROVIDED EV CHARGING:	6 SPACES

REQUIRED EV CAPABLE (10% OF PARKING):	106'0.10 = 11
11 EV CAPABLE SPACES PROVIDED *FINAL LOCATIONS TBD	


SCOTTSDALE P&D NOTES

PROPOSED LAND DIVISION WILL REQUIRE A PRELIMINARY PLAT FILE APPROVAL DURING THE DR PHASE OF PROJECT AND THEN A FINAL PLAT FILE APPROVAL DURING CONSTRUCTION PLAN PHASE OF PROJECT.

GENERAL DRAWING NOTES

- REFER TO THE A0.X SERIES DRAWINGS FOR ARCHITECTURAL GENERAL NOTES, DRAWING, REFERENCE AND MATERIAL SYMBOLS AS WELL AS ABBREVIATIONS USED ON THIS DRAWING.
- FOR BASIC LIFE SAFETY AND CODE INFORMATION APPLYING TO THIS PROJECT, REFER TO G.X SERIES LOCATED PER THE PROJECT SHEET INDEX.
- REFER TO A2.X.X SERIES FOR ARCHITECTURAL FLOOR PLANS, ROOF PLANS, & TILT WALL COORDINATION INFORMATION.
- REFER TO AND COORDINATE WITH CIVIL, LANDSCAPE, STRUCTURAL, MECHANICAL, AND ELECTRICAL DRAWINGS FOR ADDITIONAL SITE INFORMATION NOT SHOWN ON THIS DRAWING.
- SITE SCREEN WALLS A MAXIMUM 8'-0" ABOVE THE HIGHEST FINISHED GRADE OF THE PARKING AREA OR STREET CURB, WHICHEVER IS HIGHER.
- REFER TO AND COORDINATE WITH CIVIL DRAWINGS FOR ALL FINISH GRADES.
- REFER TO A4.X.X SERIES DRAWINGS FOR ENLARGED EXTERIOR ELEVATIONS, BUILDING SECTIONS, TILT WALL ELEVATIONS, & WALL SECTIONS.

VICINITY MAP

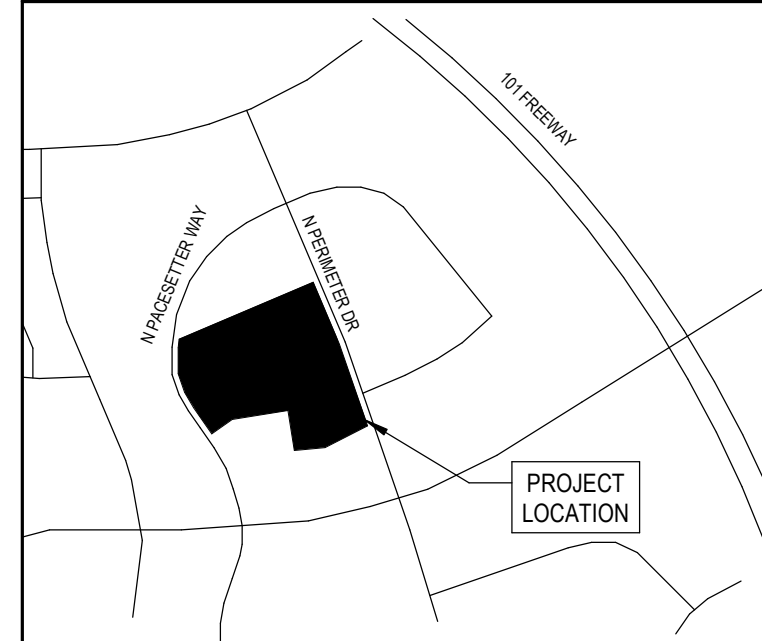

GRAPHIC LEGEND

SYMBOL:	DESCRIPTION:
	MAIN ENTRY / EXIT
	FIRE HYDRANT - COORDINATE LOCATIONS WITH CIVIL DRAWINGS
	FIRE LANE (FIRE ACCESSIBILITY SITE PLAN). COORDINATE FINAL LOCATIONS W/ CIVIL
	INDICATES NEW SITEWORK
	INDICATES ADJACENT EXISTING SITE CONDITIONS
	INDICATES PROPERTY LINE
	LIGHT POLE. COORDINATE W/ ELECTRICAL DRAWINGS

FINISH LINE AUTO

17600 N PERIMETER DR #100
SCOTTSDALE, AZ 85255

LGE DESIGNBUILD

#	REVISION	DATE
---	----------	------

DR Submit 8/21/25

NOT FOR CONSTRUCTION

SHEET TITLE:

ARCHITECTURAL SITE PLAN - OVERALL


ISSUE DATE: 06/25/25

DRAWN BY: LGE DESIGN GROUP

CHECKED BY: --

PROJECT No: --


A1.1.1

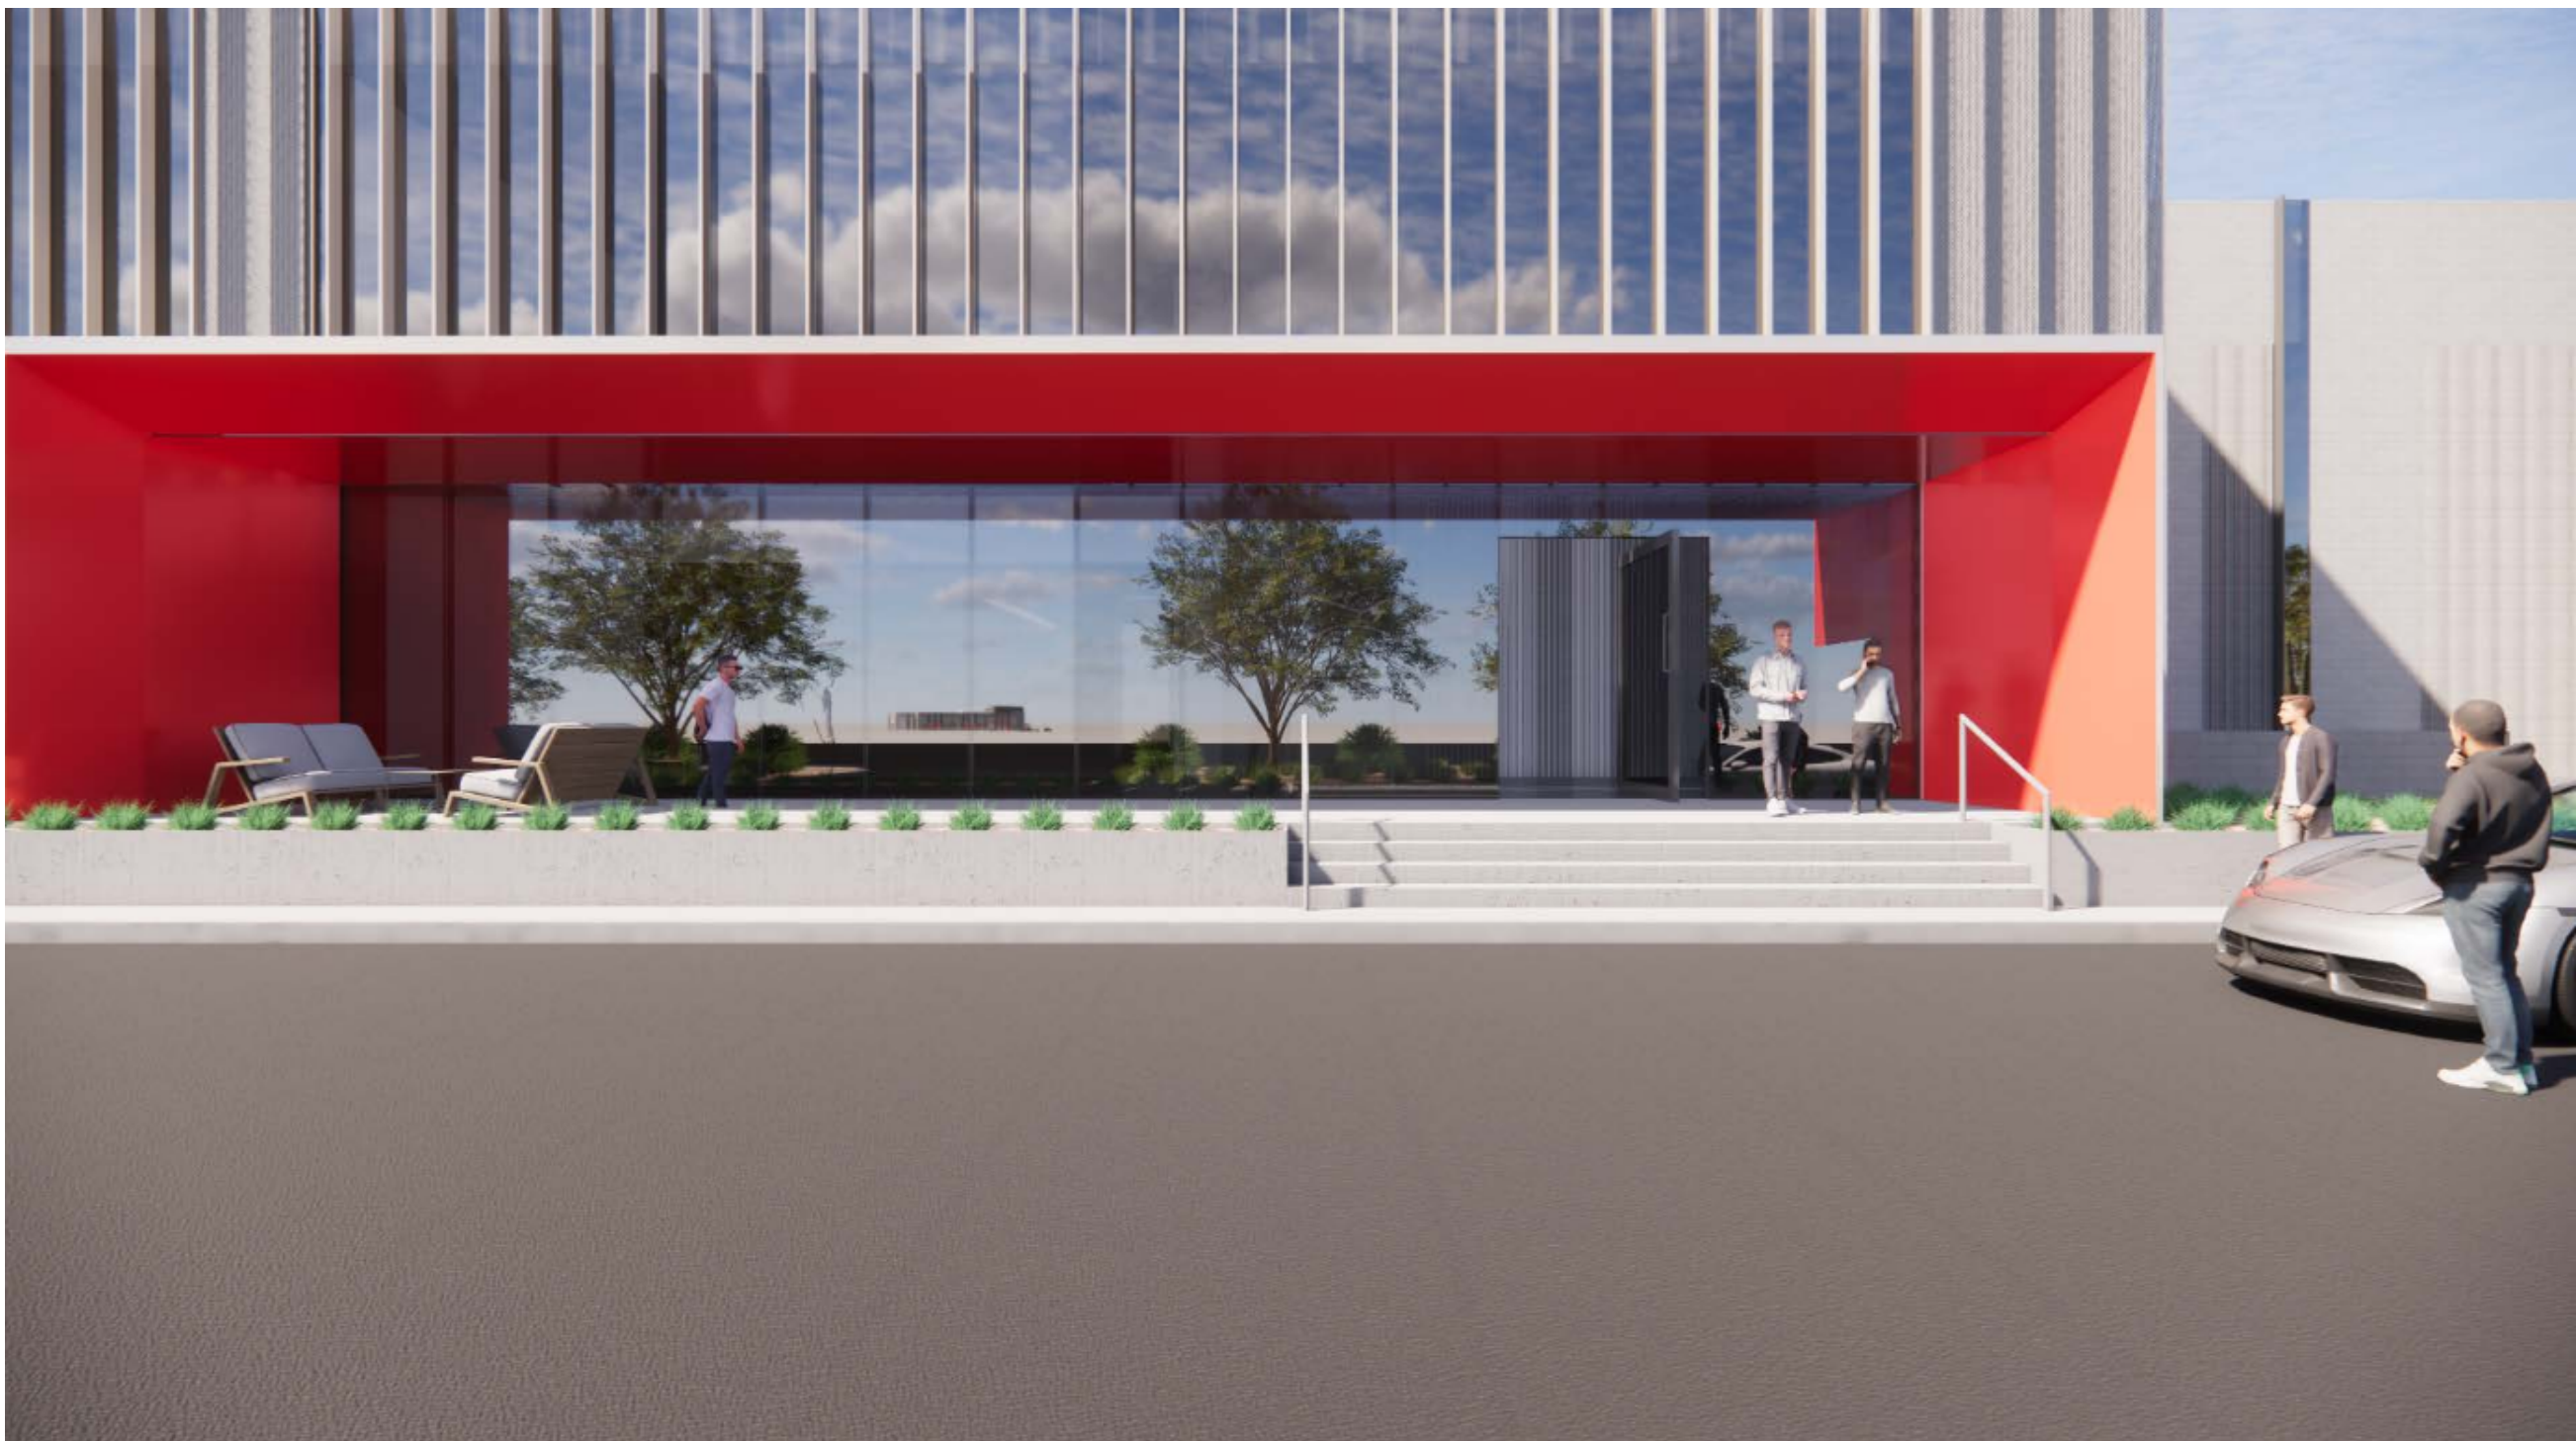


#	REVISION	DATE
DR Submittal		8/21/25

NOT FOR CONSTRUCTION


SHEET TITLE:	PERSPECTIVES
ISSUE DATE:	08/21/25
DRAWN BY:	LGE DESIGN GROUP
CHECKED BY:	Checker
PROJECT No:	--

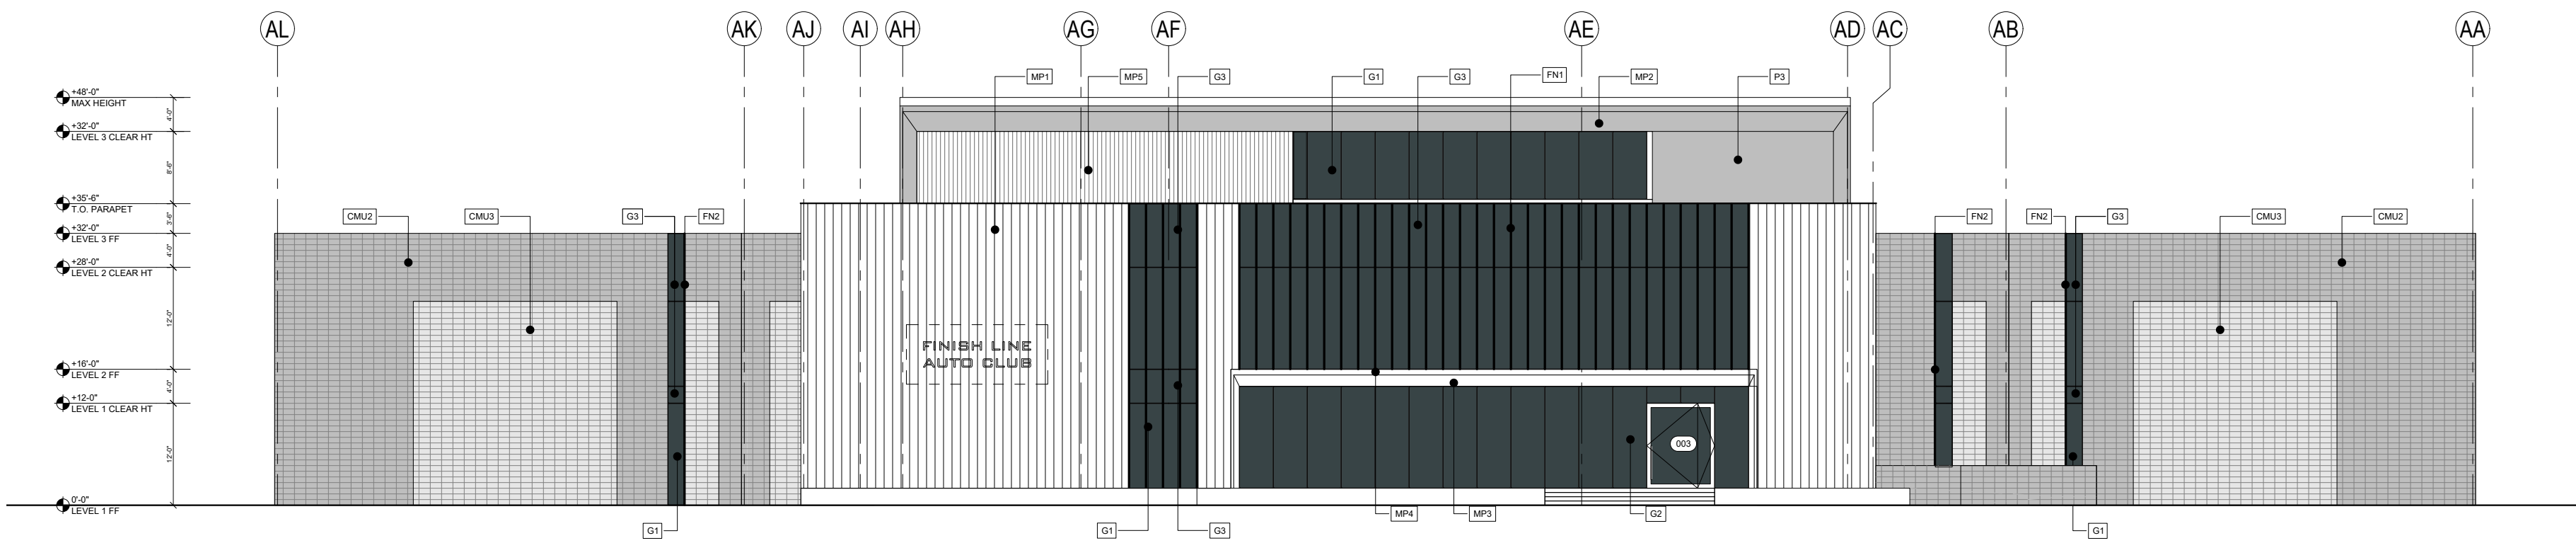


04 EAST ELEVATION - BUILDING A
SCALE: 1/16" = 1'-0"

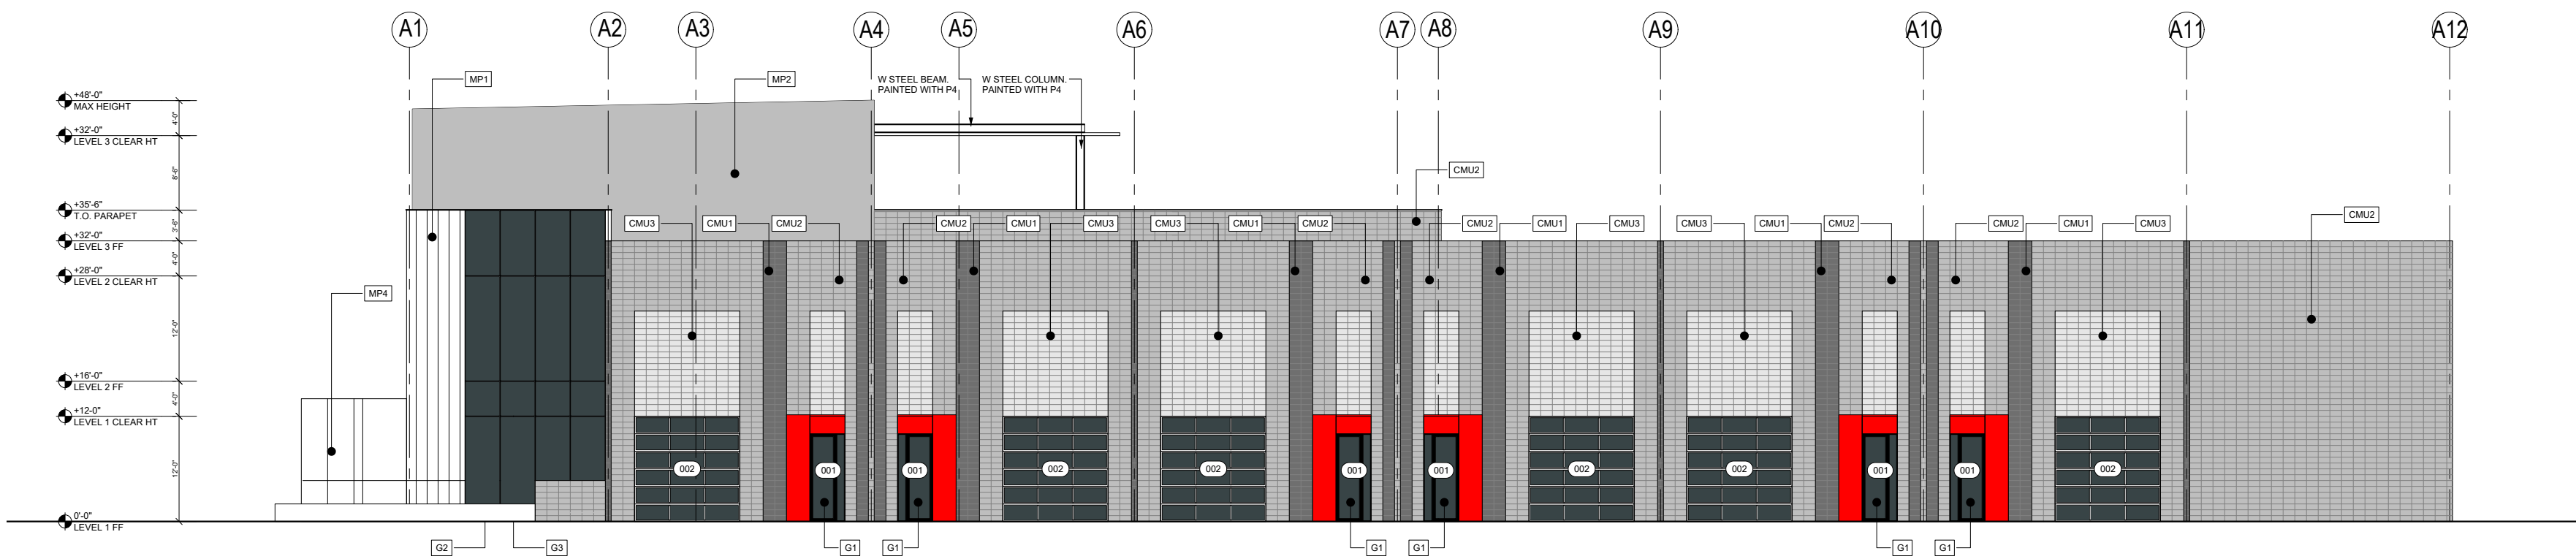

03 NORTH ELEVATION - BUILDING A
SCALE: 1/16" = 1'-0"

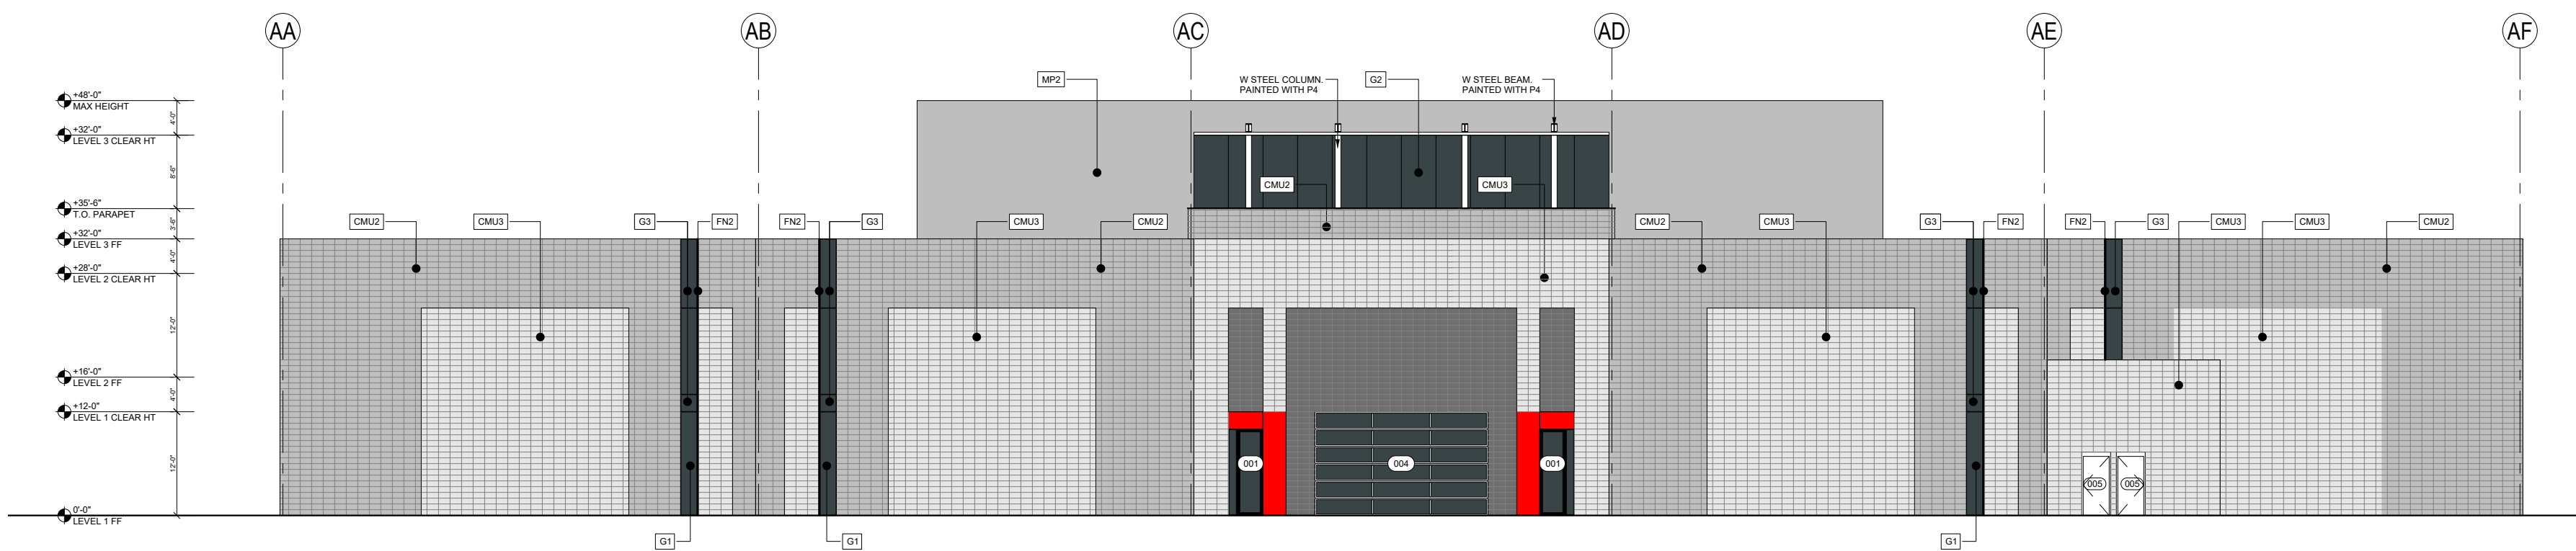

02 WEST ELEVATION - BUILDING A
SCALE: 1/16" = 1'-0"

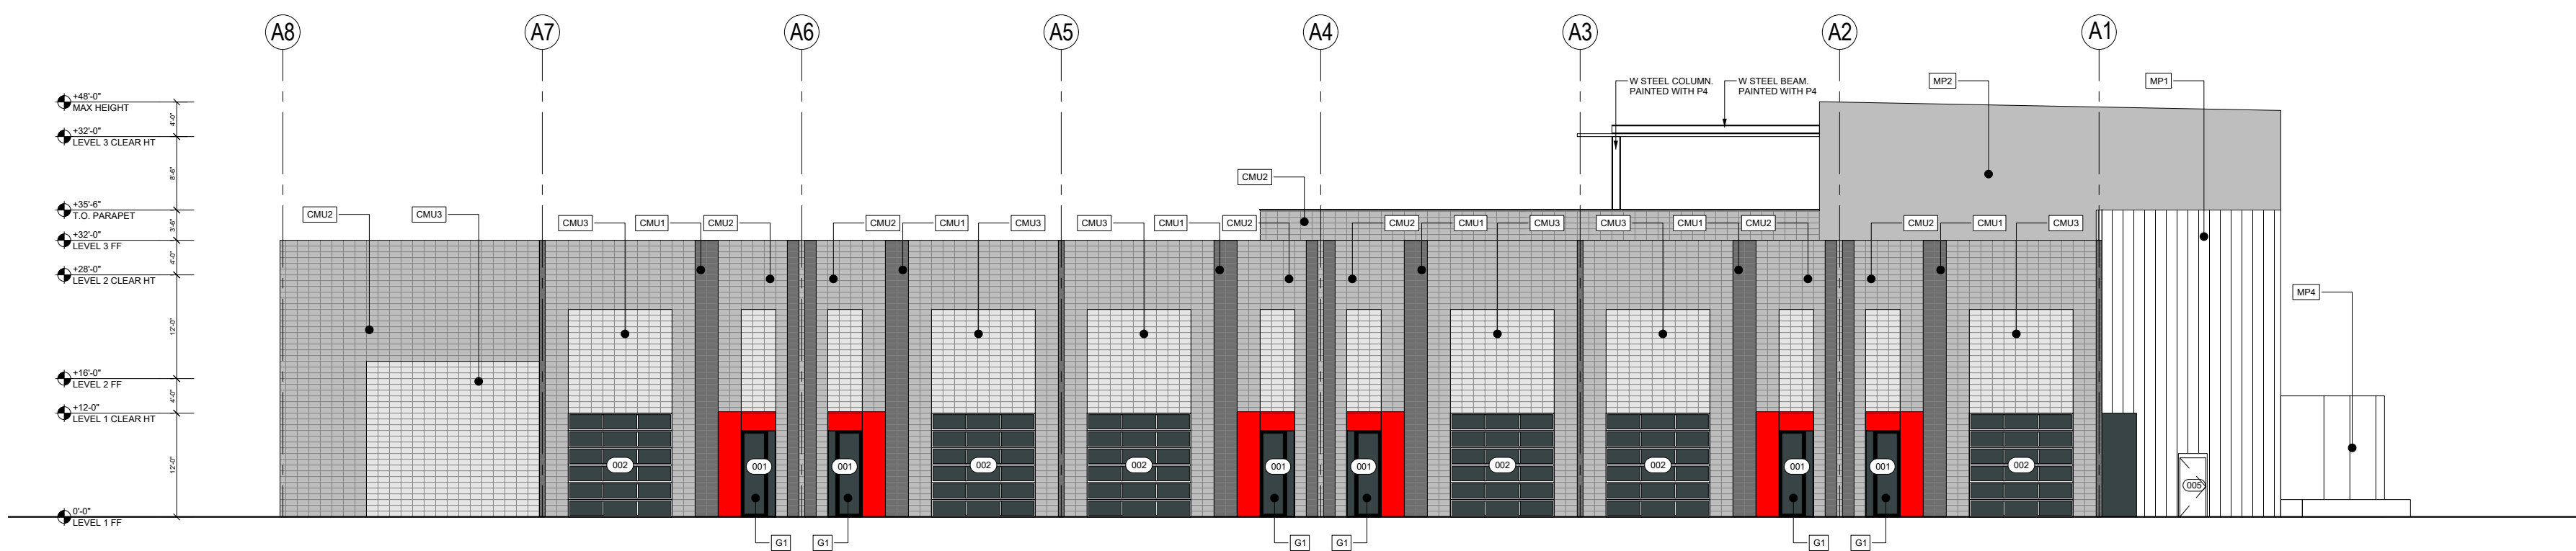

01 SOUTH ELEVATION - BUILDING A
SCALE: 1/16" = 1'-0"

EXTERIOR MATERIAL KEY

- MP1 LIGHT GREY PERFORATED AND CORRUGATED METAL PANEL. MI-2810 WHITE SILVER, VISAGE
- MP2 DARK METAL PANEL - MI-2011 DARK GREY: COLOR, VISAGE BY LUMABUILT
- MP3 RED METAL PANEL (INNER ENTRY CANOPY). SL-1852 CARDINAL RED, VISAGE BY LUMABUILT
- MP4 LIGHT GREY METAL PANEL (OUTER ENTRY CANOPY). MI-2810 WHITE SILVER, VISAGE BY LUMABUILT
- MP5 DARK CORRUGATED METAL PANEL - MI-2011 DARK GREY: COLOR, VISAGE BY LUMABUILT

- CMU1 8"x8"x16" CMU
SMOOTH FACE STACK BOND INTEGRAL COLOR MASONRY
COLOR: "BLACK CANYON" BY SUPERLITE
- CMU2 8"x8"x16" CMU
SMOOTH FACE STACK BOND INTEGRAL COLOR MASONRY
COLOR: "PEBBLE BEACH" BY SUPERLITE
- CMU3 8"x8"x16" CMU
SMOOTH FACE STACK BOND INTEGRAL COLOR MASONRY
COLOR: "MALIBU SAND" BY SUPERLITE
- CMU4 8"x8"x16" CMU
SCORED SPLIT FACE STACK BOND INTEGRAL COLOR MASONRY
COLOR: "BLACK CANYON" BY SUPERLITE

PAINT

- P1 PAINT KEY:
DUN EDWARDS COLD MORNING DE6365
- P2 DUNN EDWARDS COVERED IN PLATINUM DE6367
- P3 DUNN EDWARDS DARK GRAY DEGR60
- P4 DUN EDWARDS BLACK DEA002
- P5 DUNN EDWARDS RED POWER DEA108

MISC. ARCHITECTURAL ELEMENTS

- FN1 VERTICAL LOUVERS
ANODIZED ALUMINUM FINS, 1.5" WIDE X 8" DEEP
- FN2 VERTICAL LOUVERS
ANODIZED BLACK ([P4]) ALUMINUM FINS 1.5" WIDE X 8" DEEP


FINISH LINE AUTO CLUB

UPDATE
PRICING SET
NOT TO BE USED
FOR CONSTRUCTION


SHEET TITLE:	ELEVATIONS - BUILDING A
ISSUE DATE:	03/25/25
DRAWN BY:	AE
CHECKED BY:	RH
PROJECT No.:	000000

SHEET:


A4.1A

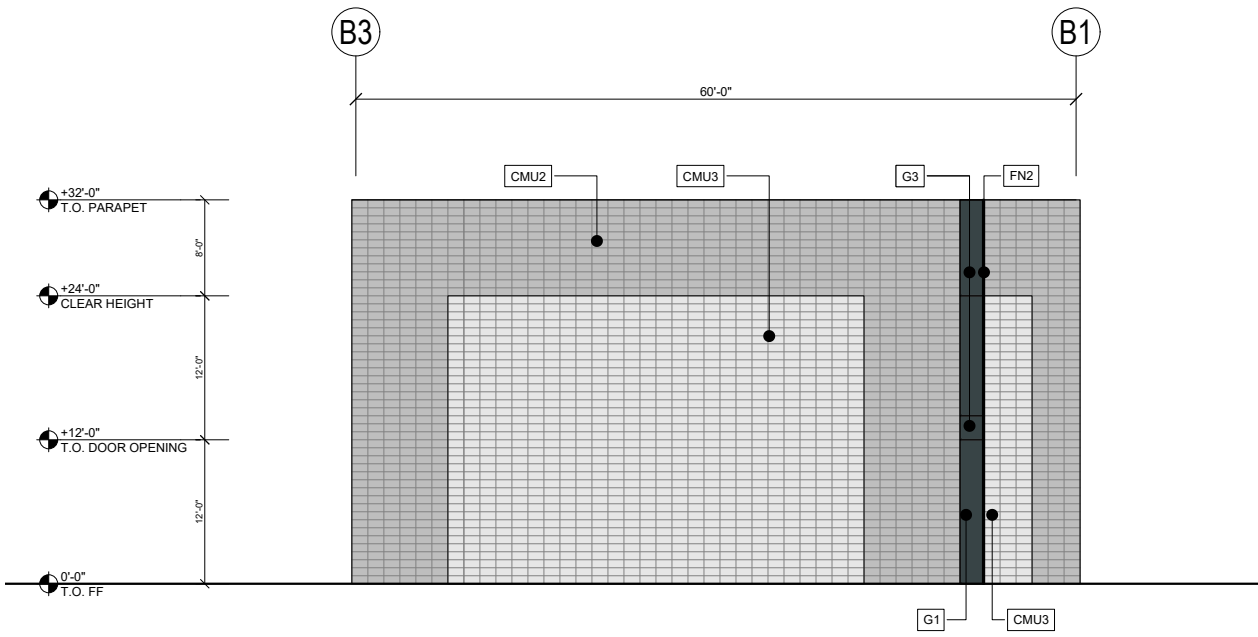


04 SOUTH ELEVATION - BUILDING B
SCALE: 1/16" = 1'-0"

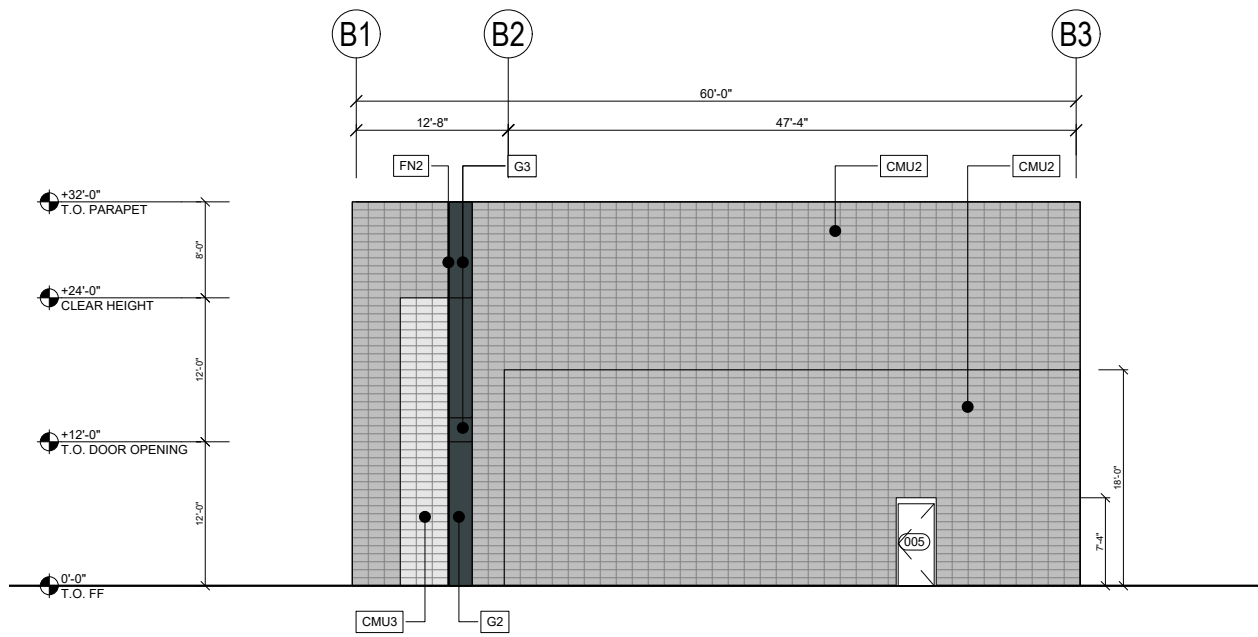

03 NORTH ELEVATION - BUILDING B
SCALE: 1/16" = 1'-0"

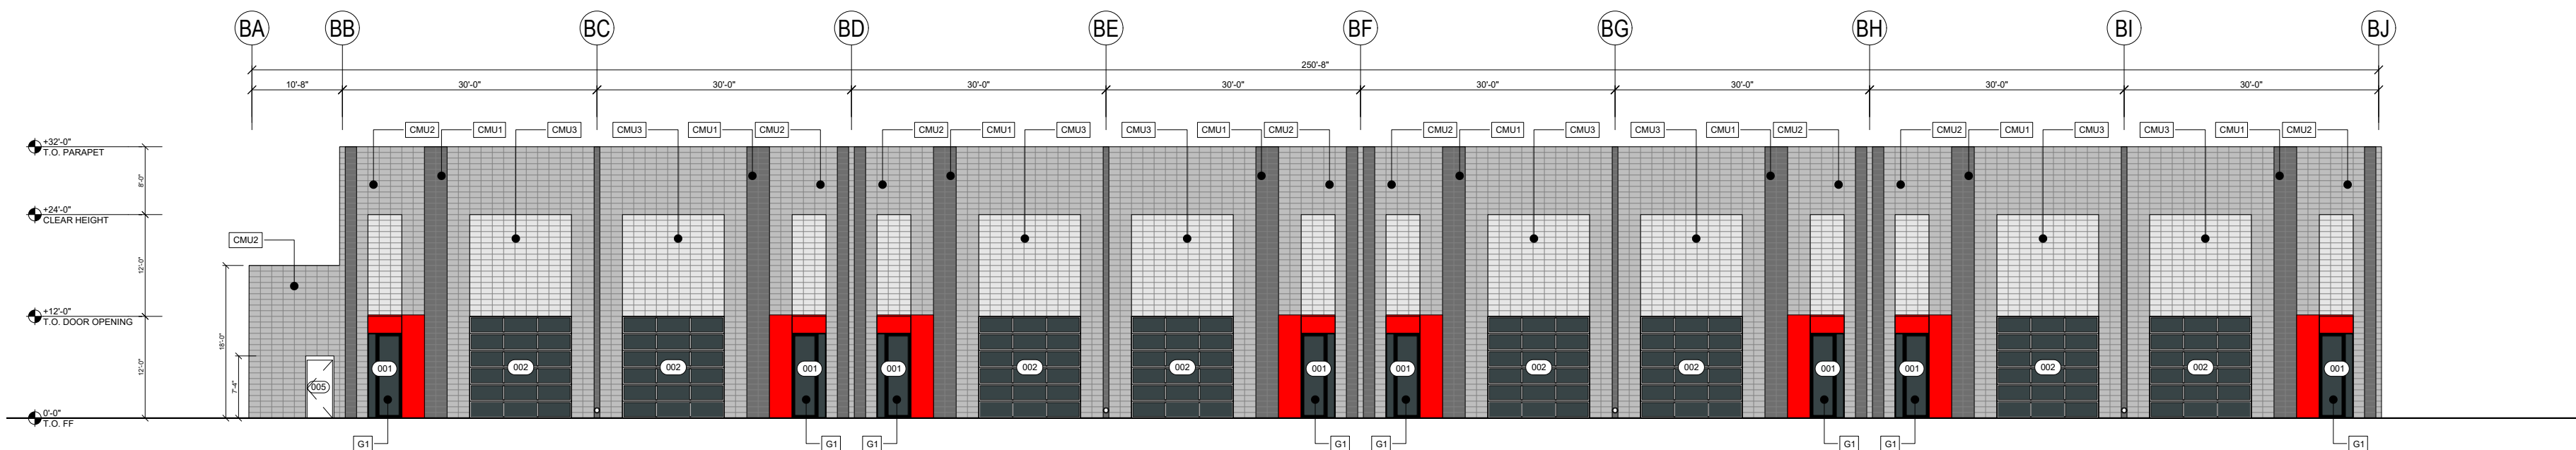

02 WEST ELEVATION - BUILDING B
SCALE: 1/16" = 1'-0"

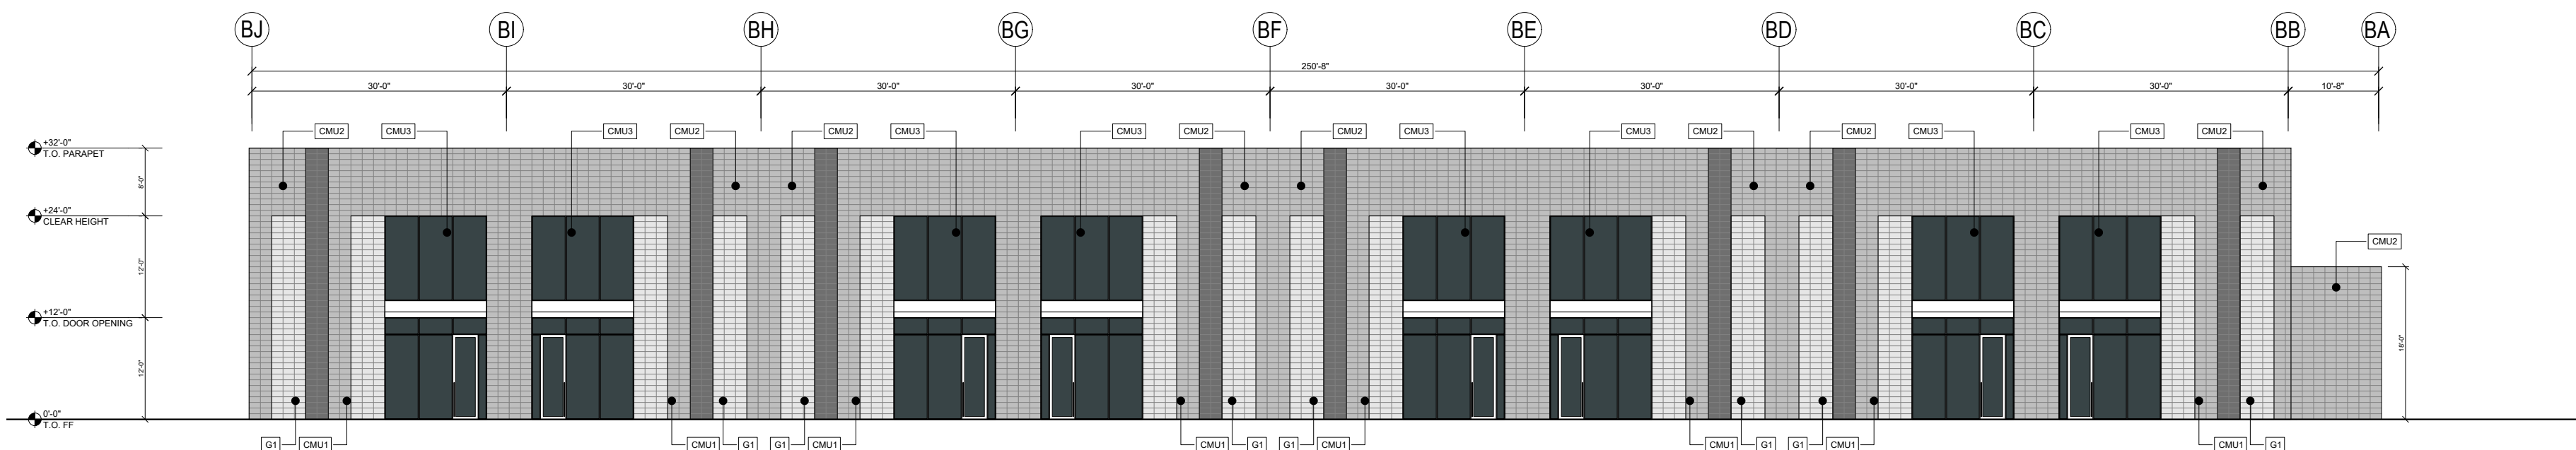

01 EAST ELEVATION - BUILDING B
SCALE: 1/16" = 1'-0"

EXTERIOR MATERIAL KEY

- MP1 LIGHT GREY PERFORATED AND CORRUGATED METAL PANEL. MI-2810 WHITE SILVER, VISAGE
- MP2 DARK METAL PANEL - MI-2011 DARK GREY: COLOR, VISAGE BY LUMABUILT
- MP3 RED METAL PANEL (INNER ENTRY CANOPY). SL-1852 CARDINAL RED, VISAGE BY LUMABUILT
- MP4 LIGHT GREY METAL PANEL (OUTER ENTRY CANOPY). MI-2810 WHITE SILVER, VISAGE BY LUMABUILT
- MP5 DARK CORRUGATED METAL PANEL - MI-2011 DARK GREY: COLOR, VISAGE BY LUMABUILT

- CMU1 8"X8"x16" CMU
SMOOTH FACE STACK BOND INTEGRAL COLOR MASONRY
COLOR: "BLACK CANYON" BY SUPERLITE
- CMU2 8"X8"x16" CMU
SMOOTH FACE STACK BOND INTEGRAL COLOR MASONRY
COLOR: "PEBBLE BEACH" BY SUPERLITE
- CMU3 8"X8"x16" CMU
SMOOTH FACE STACK BOND INTEGRAL COLOR MASONRY
COLOR: "MALIBU SAND" BY SUPERLITE
- CMU4 8"X8"x16" CMU
SCORED SPLIT FACE STACK BOND INTEGRAL COLOR
MASONRY
COLOR: "BLACK CANYON" BY SUPERLITE


PAINT

- P1 PAINT KEY:
DUN EDWARDS COLD MORNING DE6365
- P2 DUNN EDWARDS COVERED IN PLATINUM DE6367
- P3 DUNN EDWARDS DARK GRAY DEGR60
- P4 DUN EDWARDS BLACK DEA002
- P5 DUNN EDWARDS RED POWER DEA108


MISC. ARCHITECTURAL ELEMENTS

- FN1 VERTICAL LOUVERS
ANODIZED ALUMINUM FINS, 1.5" WIDE X 8" DEEP
- FN2 VERTICAL LOUVERS
ANODIZED BLACK ([P4]) ALUMINUM FINS 1.5" WIDE X 8" DEEP


FINISH LINE AUTO CLUB

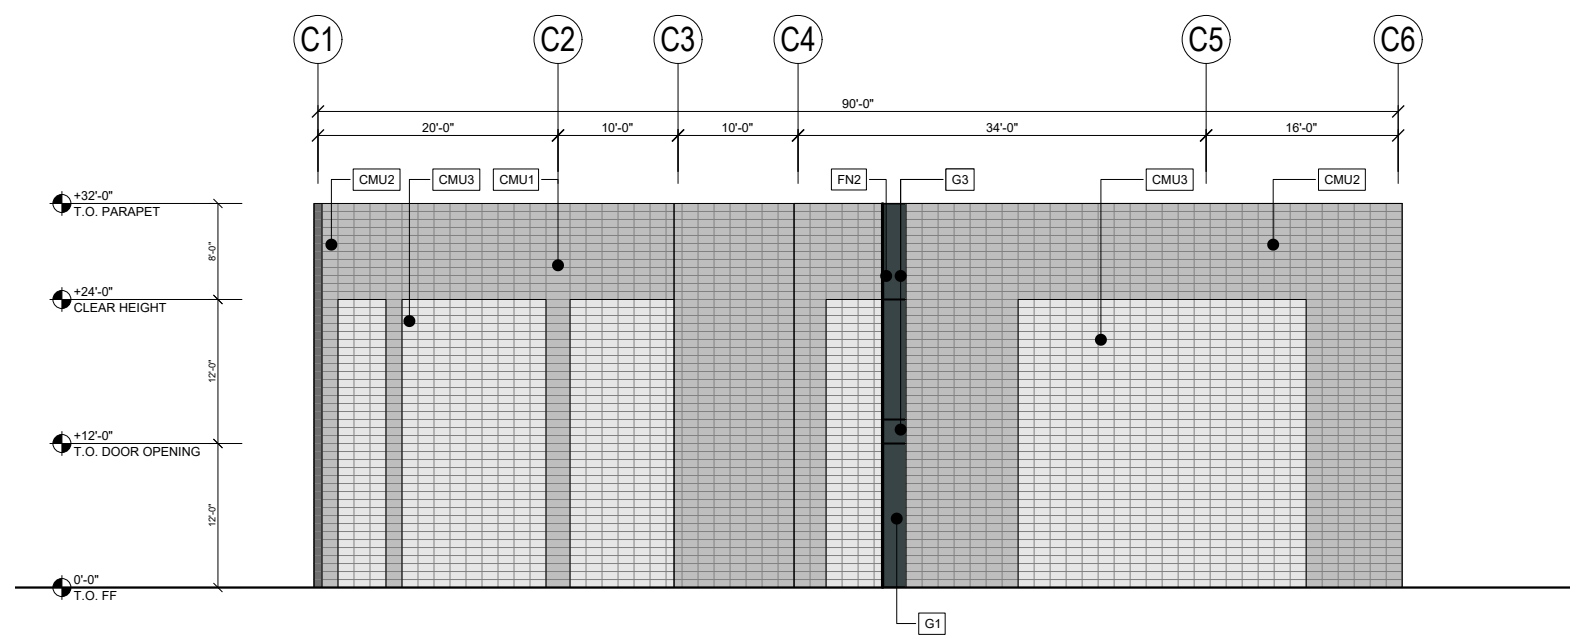


01 SOUTH ELEVATION - BUILDING C
SCALE: 1/16" = 1'-0"

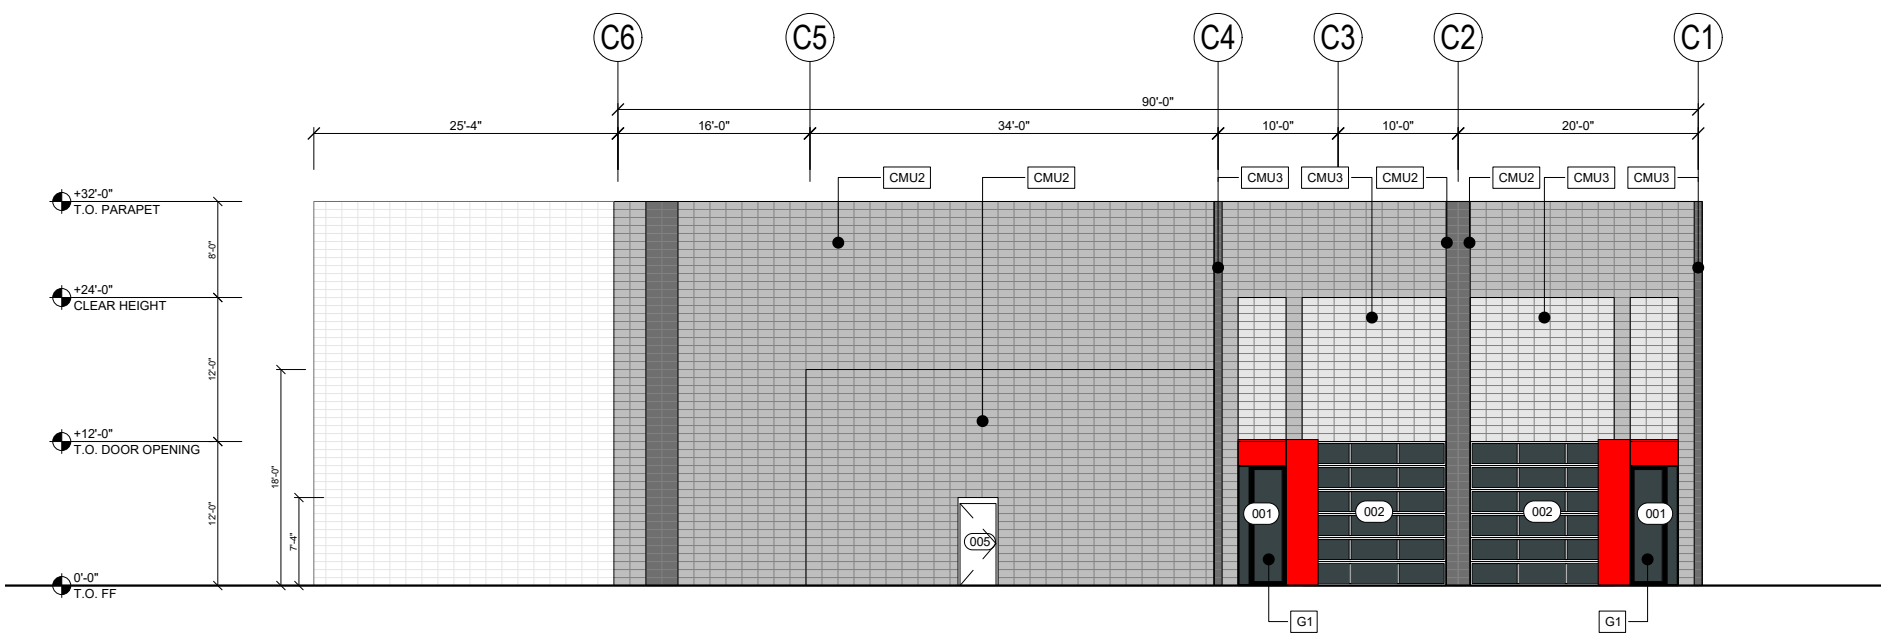

03 NORTH ELEVATION - BUILDING C
SCALE: 1/16" = 1'-0"

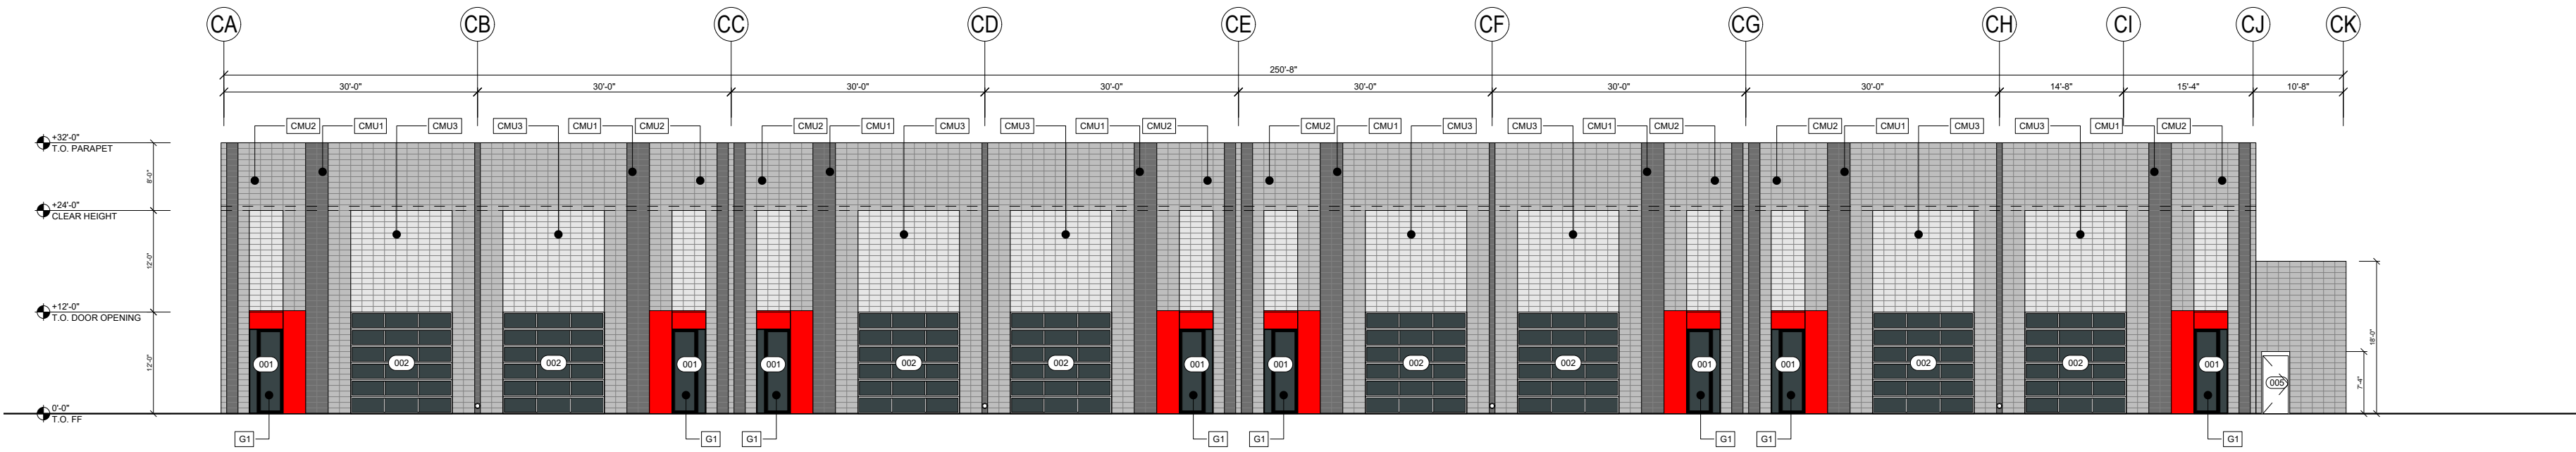

02 EAST ELEVATION - BUILDING C
SCALE: 1/16" = 1'-0"

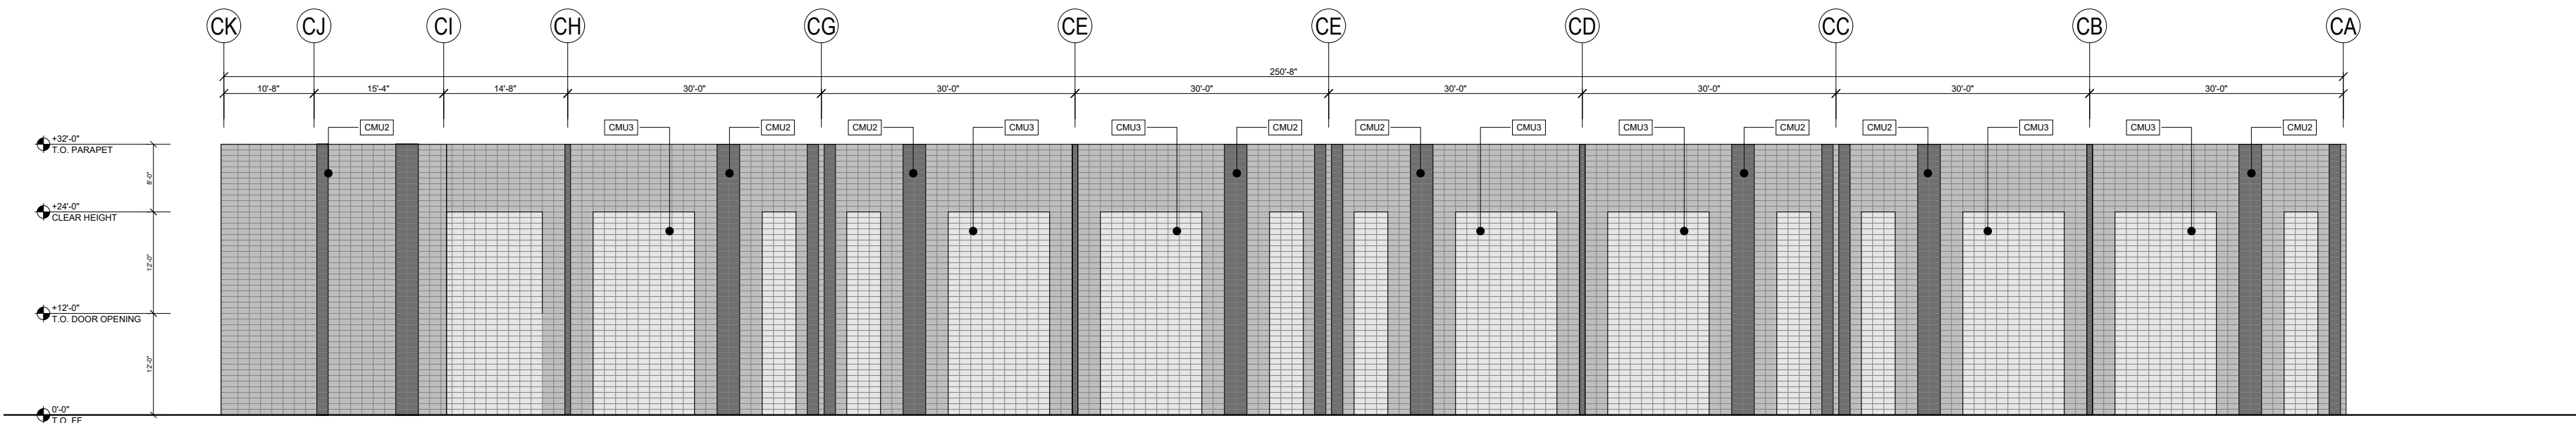

01 WEST ELEVATION - BUILDING C
SCALE: 1/16" = 1'-0"

EXTERIOR MATERIAL KEY

- MP1 LIGHT GREY PERFORATED AND CORRUGATED METAL PANEL - MI-2810 WHITE SILVER, VISAGE
- MP2 DARK METAL PANEL - MI-2011 DARK GREY: COLOR, VISAGE BY LUMABUILT
- MP3 RED METAL PANEL (INNER ENTRY CANOPY). SL-1852 CARDINAL RED, VISAGE BY LUMABUILT
- MP4 LIGHT GREY METAL PANEL (OUTER ENTRY CANOPY). MI-2810 WHITE SILVER, VISAGE BY LUMABUILT
- MP5 DARK CORRUGATED METAL PANEL - MI-2011 DARK GREY: COLOR, VISAGE BY LUMABUILT

- CMU1 8"X8"x16" CMU
SMOOTH FACE STACK BOND INTEGRAL COLOR MASONRY
COLOR: "BLACK CANYON" BY SUPERLITE
- CMU2 8"X8"x16" CMU
SMOOTH FACE STACK BOND INTEGRAL COLOR MASONRY
COLOR: "PEBBLE BEACH" BY SUPERLITE
- CMU3 8"X8"x16" CMU
SMOOTH FACE STACK BOND INTEGRAL COLOR MASONRY
COLOR: "MALIBU SAND" BY SUPERLITE
- CMU4 8"X8"x16" CMU
SCORED SPLIT FACE STACK BOND INTEGRAL COLOR
MASONRY
COLOR: "BLACK CANYON" BY SUPERLITE

PAINT

- P1 PAINT KEY:
DUN EDWARDS COLD MORNING DE6365
- P2 DUNN EDWARDS COVERED IN PLATINUM DE6367
- P3 DUNN EDWARDS DARK GRAY DEGR60
- P4 DUN EDWARDS BLACK DEA002
- P5 DUNN EDWARDS RED POWER DEA108

MISC. ARCHITECTURAL ELEMENTS

- FN1 VERTICAL LOUVERS
ANODIZED ALUMINUM FINS, 1.5" WIDE X 8" DEEP
- FN2 VERTICAL LOUVERS
ANODIZED BLACK ([P4]) ALUMINUM FINS 1.5" WIDE X 8" DEEP

FINISH LINE AUTO CLUB

LGE | DESIGNGROUP

1200 N. 52nd Street ■ Phoenix, AZ ■ 85008
P: 480.966.4001

LGE | DESIGNBUILD

NUMBER	REVISION	DATE
--------	----------	------

UPDATE
PRICING SET
NOT TO BE USED
FOR CONSTRUCTION

SHEET TITLE:
ELEVATIONS - BUILDING D

ISSUE DATE: 03/25/25

DRAWN BY: AE


CHECKED BY: RH

PROJECT No.: 000000


SHEET:

A4.1C


17600 PERIMETER DR 100
SCOTTSDALE, AZ 85255

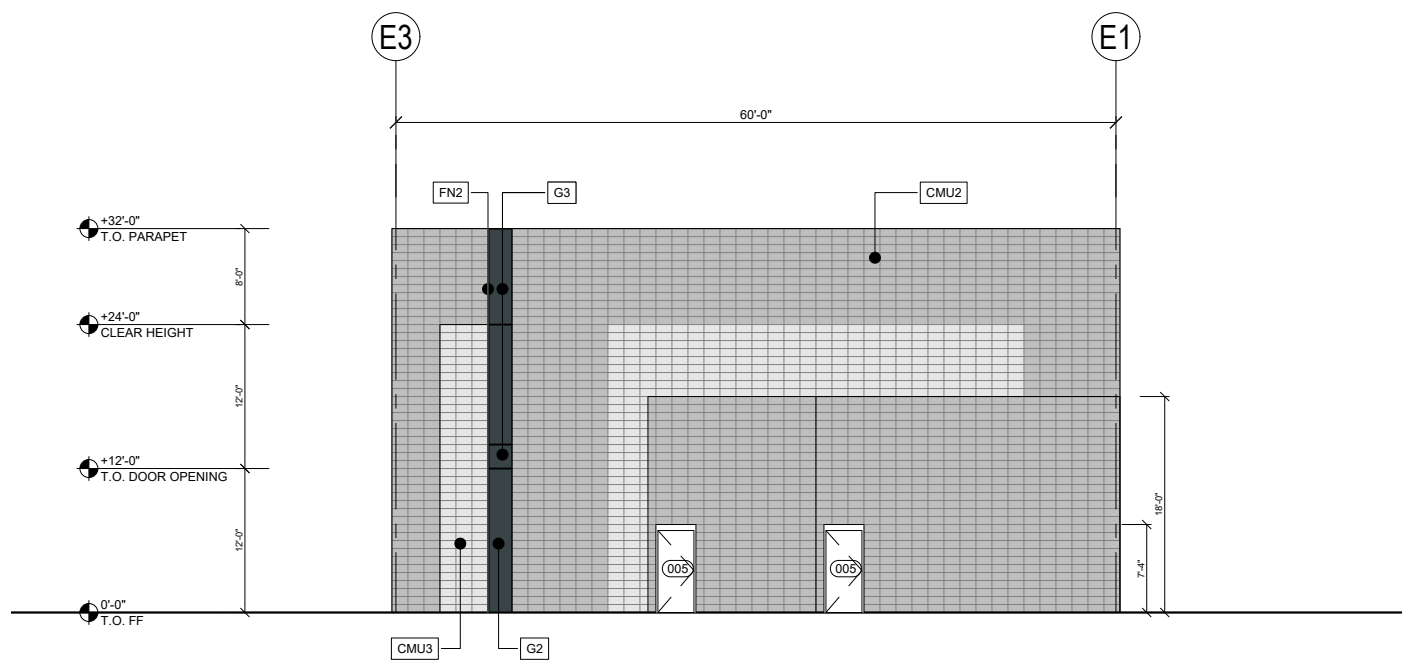


04 EAST ELEVATION - BUILDING E
SCALE: 1/16" = 1'-0"

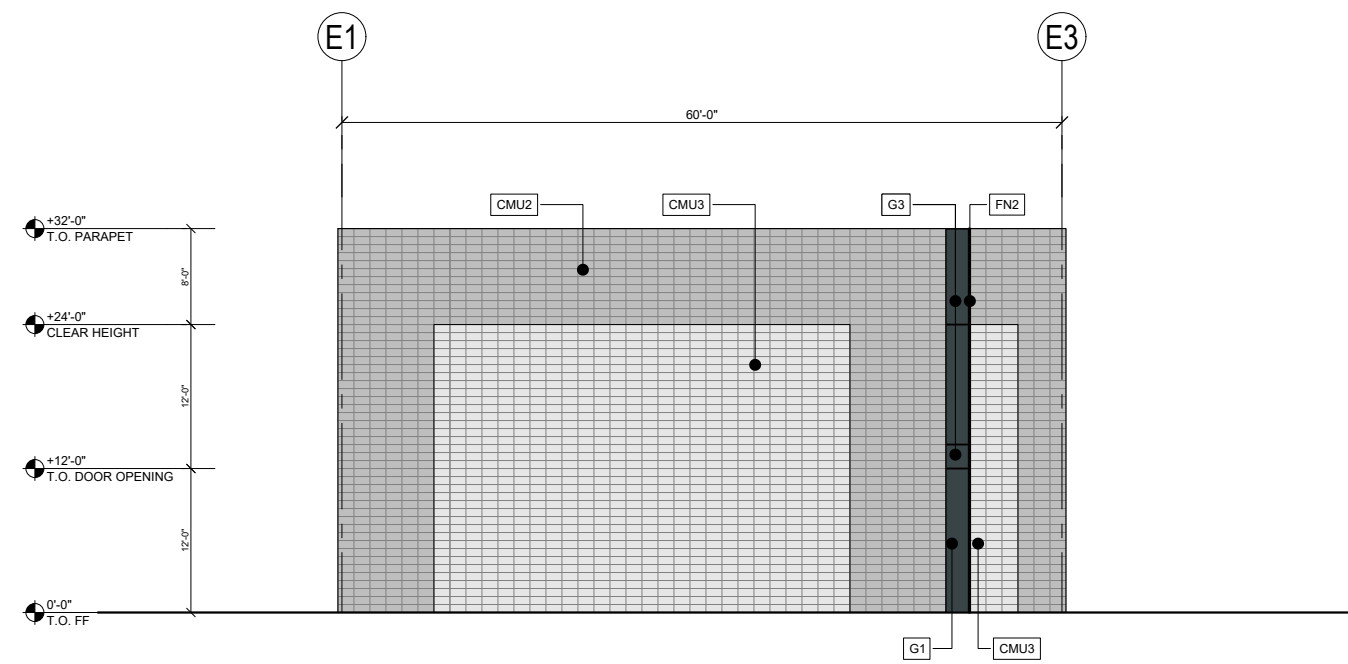

03 WEST ELEVATION - BUILDING E
SCALE: 1/16" = 1'-0"

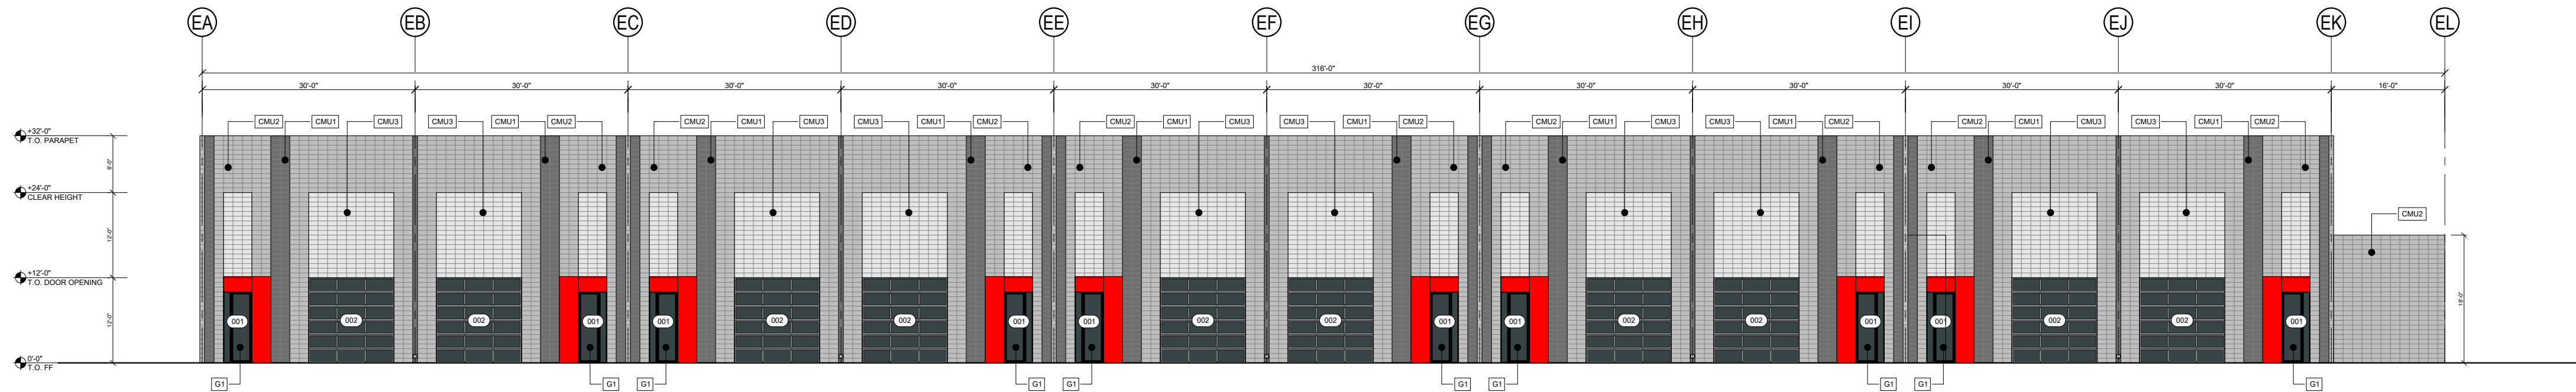

02 SOUTH ELEVATION - BUILDING E
SCALE: 1/16" = 1'-0"

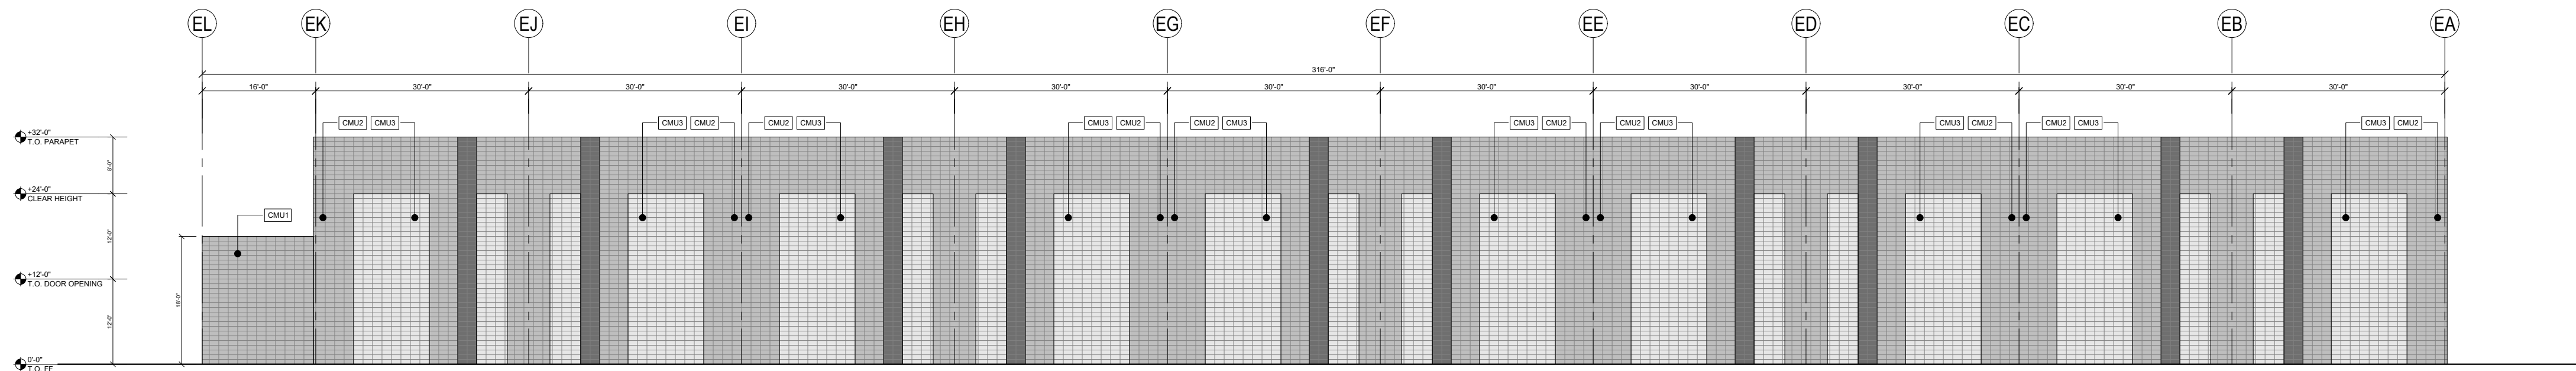

01 NORTH ELEVATION - BUILDING E
SCALE: 1/16" = 1'-0"

EXTERIOR MATERIAL KEY

- MP1 LIGHT GREY PERFORATED AND CORRUGATED METAL PANEL - MI-2810 WHITE SILVER, VISAGE
- MP2 DARK METAL PANEL - MI-2011 DARK GREY: COLOR, VISAGE BY LUMABUILT
- MP3 RED METAL PANEL (INNER ENTRY CANOPY). SL-1852 CARDINAL RED, VISAGE BY LUMABUILT
- MP4 LIGHT GREY METAL PANEL (OUTER ENTRY CANOPY). MI-2810 WHITE SILVER, VISAGE BY LUMABUILT
- MP5 DARK CORRUGATED METAL PANEL - MI-2011 DARK GREY: COLOR, VISAGE BY LUMABUILT


- CMU1 8"X8"x16" CMU
SMOOTH FACE STACK BOND INTEGRAL COLOR MASONRY
COLOR: "BLACK CANYON" BY SUPERLITE
- CMU2 8"X8"x16" CMU
SMOOTH FACE STACK BOND INTEGRAL COLOR MASONRY
COLOR: "PEBBLE BEACH" BY SUPERLITE
- CMU3 8"X8"x16" CMU
SMOOTH FACE STACK BOND INTEGRAL COLOR MASONRY
COLOR: "MALIBU SAND" BY SUPERLITE
- CMU4 8"X8"x16" CMU
SCORED SPLIT FACE STACK BOND INTEGRAL COLOR MASONRY
COLOR: "BLACK CANYON" BY SUPERLITE

PAINT

- P1 PAINT KEY:
DUN EDWARDS COLD MORNING DE6365
- P2 DUNN EDWARDS COVERED IN PLATINUM DE6367
- P3 DUNN EDWARDS DARK GRAY DEGR60
- P4 DUN EDWARDS BLACK DEA002
- P5 DUNN EDWARDS RED POWER DEA108

MISC. ARCHITECTURAL ELEMENTS

- FN1 VERTICAL LOUVERS
ANODIZED ALUMINUM FINS, 1.5" WIDE X 8" DEEP
- FN2 VERTICAL LOUVERS
ANODIZED BLACK ([P4]) ALUMINUM FINS 1.5" WIDE X 8" DEEP

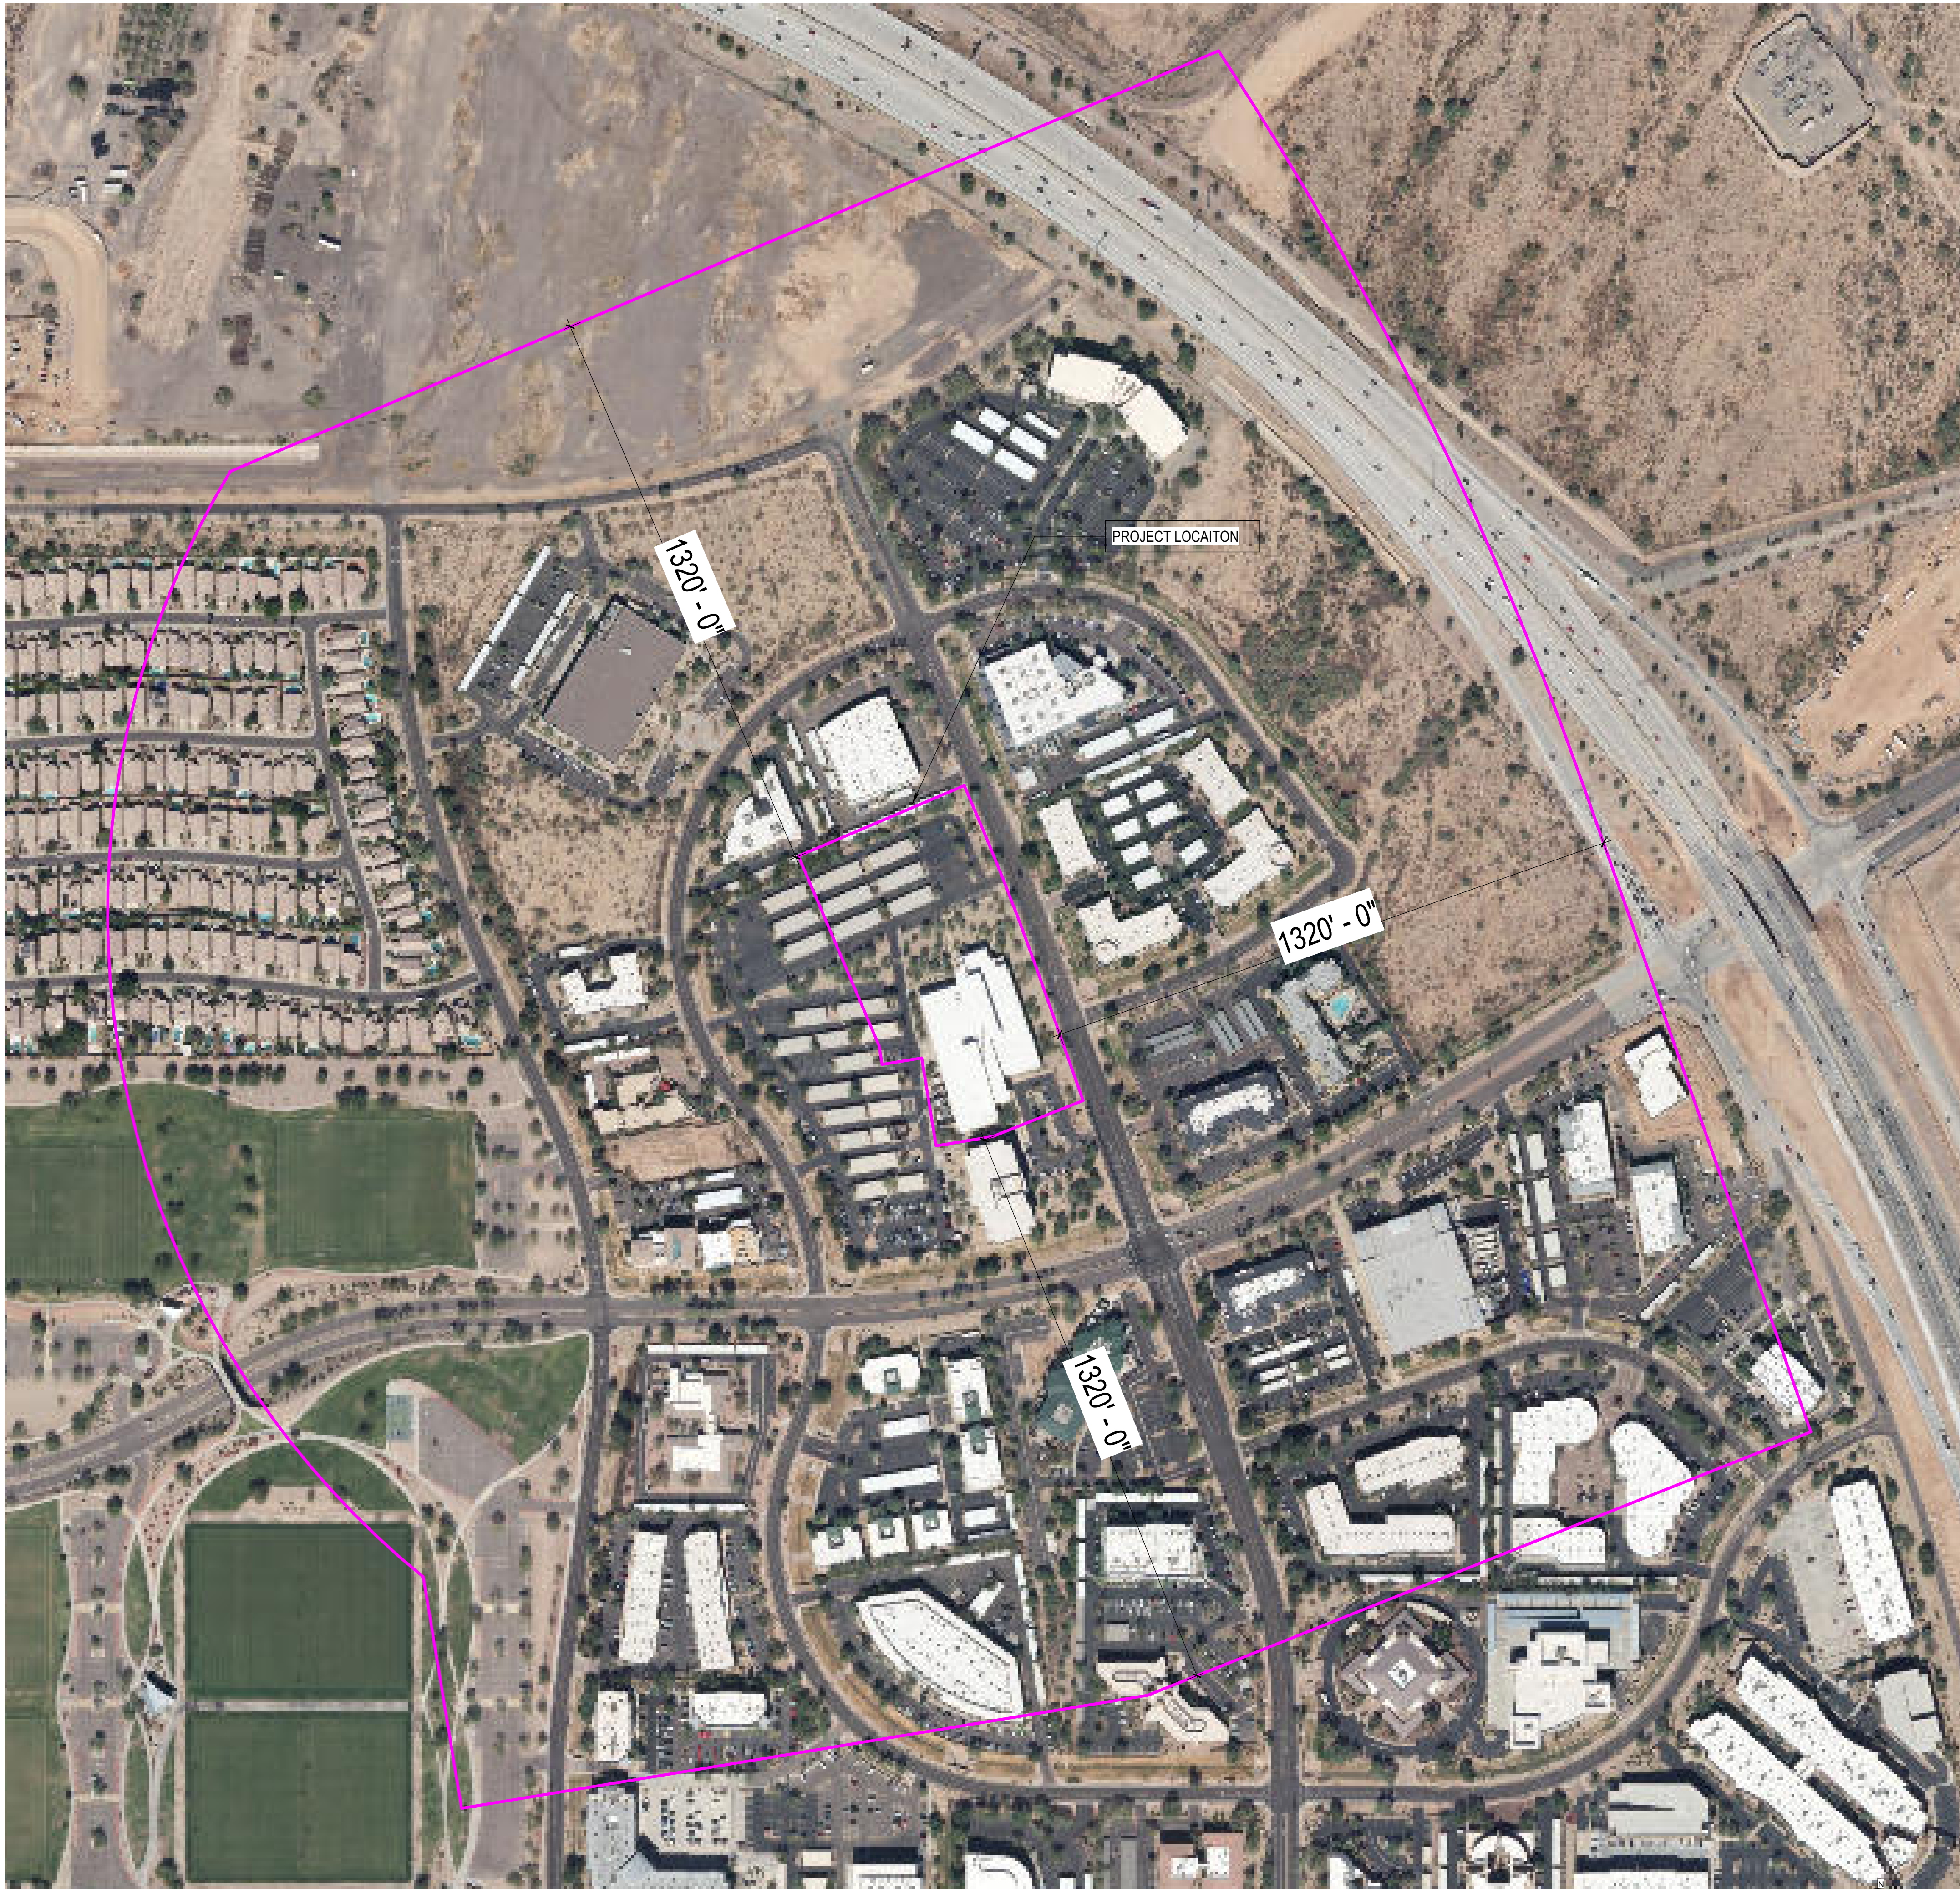

1 ARCHITECTURAL SITE PLAN W/ AERIAL
1" = 200'-0"

PROJECT DATA

AUTO CLUB	
PROJECT ADDRESS:	17600 N PERIMETER DR 100 SCOTTSDALE 85255
OWNER:	FINISH LINE AUTO CLUB 3080 AIRWAY AVE. COSTA MESA, CA 92626 TONY PRINCIPLE
ARCHITECT:	LGE DESIGN GROUP 1200 NORTH 52ND STREET PHOENIX, AZ 85008 STUDIO DIRECTOR: MARK S. CONE
PROJECT SCOPE:	APPROXIMATELY 92,502 SF OF: AUTO CONDOS (67 TOTAL UNITS) 13,916 SF OF: OFFICE / CLUBHOUSE
ASSESSOR PARCEL NO.:	215-07-230
CURRENT ZONING:	I-1 PCD
PROPOSED ZONING:	I-1 PCD
SITE AREA:	+/- 293,754 S.F. (6.74 AC)
FAR - MAX:	0.80 = 235,003 S.F.
FAR - PROPOSED:	0.42= 125,504 S.F. *IN CONFORMANCE WITH THE I-1 DEVELOPMENT STANDARDS
STORIES:	(3) STORY (BUILDING A) (1) STORY (BUILDING B) (1) STORY (BUILDING C) (1) STORY (BUILDING D) (1) STORY (BUILDING E)
GROSS BUILDING S.F.:	125,504 S.F. TOTAL 63,020 S.F. (BUILDING A) 17,877 S.F. (BUILDING B) 17,337 S.F. (BUILDING C) 8,712 S.F. (BUILDING D) 18,558 S.F. (BUILDING E)
LOT COVERAGE:	33.2%
OCCUPANCY:	A / S-1
CONSTRUCTION TYPE:	V-B W/ A.F.E.S.
BUILDING HEIGHT:	49'-0" (BUILDING A) 32'-0" (BUILDING B) 32'-0" (BUILDING C) 32'-0" (BUILDING D) 32'-0" (BUILDING E)

PROJECT DESCRIPTION:
THE FINISH LINE AUTO CLUB PROJECT CONSISTS OF FIVE BUILDINGS (GARAGES WITH AN OFFICE AND CLUB SPACE) ON A 6.74 ACRE SITE LOCATED ON N PERIMETER DRIVE WHICH CURRENTLY HAS ONE BUILDING.

<u>REQUIRED PARKING:</u>	
CLUB (LOUNGE & PATIO)	11,537 S.F./250= 47 SPACES
OFFICE: 2,379 S.F./300=	8 SPACES
STORAGE (150 UNITS): 67 UNITS/50 =	2 SPACES
TOTAL REQUIRED=	57 SPACES
PROVIDED PARKING=	105 SPACES
REGULAR PARKING=	99 SPACES
ACCESSIBLE PARKING REQUIRED=	106'0.04 = 5
ACCESSIBLE PARKING PROVIDED=	6 SPACES
REQUIRED EV CHARGING (4% OF PARKING):	106'0.04 = 5
PROVIDED EV CHARGING:	6 SPACES
REQUIRED EV CAPABLE (10% OF PARKING):	106'0.10 = 11
11 EV CAPABLE SPACES PROVIDED	*FINAL LOCATIONS TBD


GRAPHIC LEGEND

SYMBOL:	DESCRIPTION:
▶	MAIN ENTRY / EXIT
⦿	FIRE HYDRANT - COORDINATE LOCATIONS WITH CIVIL DRAWINGS
- - - - -	FIRE LANE (FIRE ACCESSIBILITY SITE PLAN), COORDINATE FINAL LOCATIONS W/ CIVIL
— — — — —	INDICATES NEW SITEWORK
— — — — —	INDICATES ADJACENT EXISTING SITE CONDITIONS
- . - . -	INDICATES PROPERTY LINE
□ □ □ □ □	LIGHT POLE, COORDINATE W/ ELECTRICAL DRAWINGS

GENERAL DRAWING NOTES

- REFER TO THE A0.X SERIES DRAWINGS FOR ARCHITECTURAL GENERAL NOTES, DRAWING, REFERENCE AND MATERIAL SYMBOLS AS WELL AS ABBREVIATIONS USED ON THIS DRAWING.
- FOR BASIC LIFE SAFETY AND CODE INFORMATION APPLYING TO THIS PROJECT, REFER TO G.X SERIES LOCATED PER THE PROJECT SHEET INDEX.
- REFER TO A2.X.X SERIES FOR ARCHITECTURAL FLOOR PLANS, ROOF PLANS, & TILT WALL COORDINATION INFORMATION
- REFER TO AND COORDINATE WITH CIVIL, LANDSCAPE, STRUCTURAL, MECHANICAL AND ELECTRICAL DRAWINGS FOR ADDITIONAL SITE INFORMATION NOT SHOWN ON THIS DRAWING.
- SITE SCREEN WALLS A MAXIMUM 8'-0" ABOVE THE HIGHEST FINISHED GRADE OF THE PARKING AREA OR STREET CURB, WHICHEVER IS HIGHER
- REFER TO AND COORDINATE WITH CIVIL DRAWINGS FOR ALL FINISH GRADES.
- REFER TO A4.X.X SERIES DRAWINGS FOR ENLARGED EXTERIOR ELEVATIONS, BUILDING SECTIONS, TILT WALL ELEVATIONS, & WALL SECTIONS


VICINITY MAP

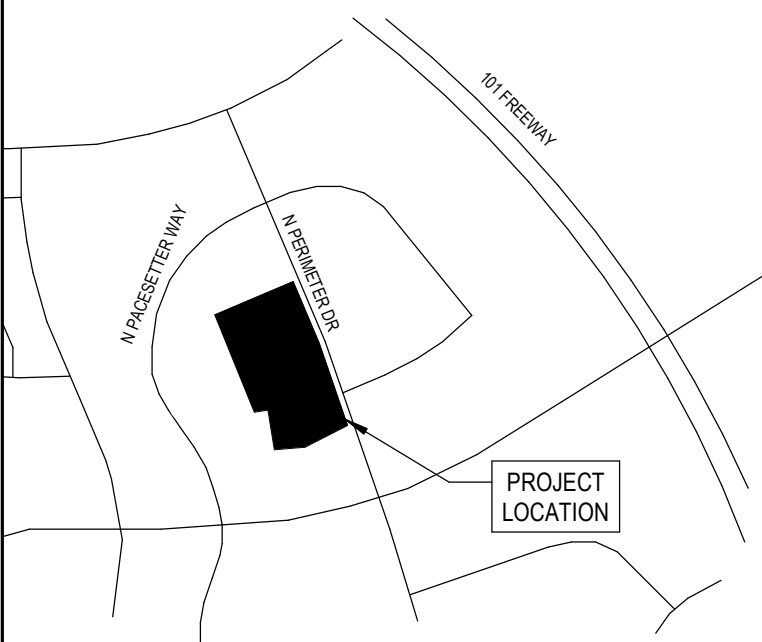

#	REVISION	DATE

NOT FOR CONSTRUCTION

SHEET TITLE:	ARCHITECTURAL SITE PLAN W/ AERIAL
ISSUE DATE:	04/11/25
DRAWN BY:	LGE DESIGN GROUP
CHECKED BY:	--
PROJECT No:	--

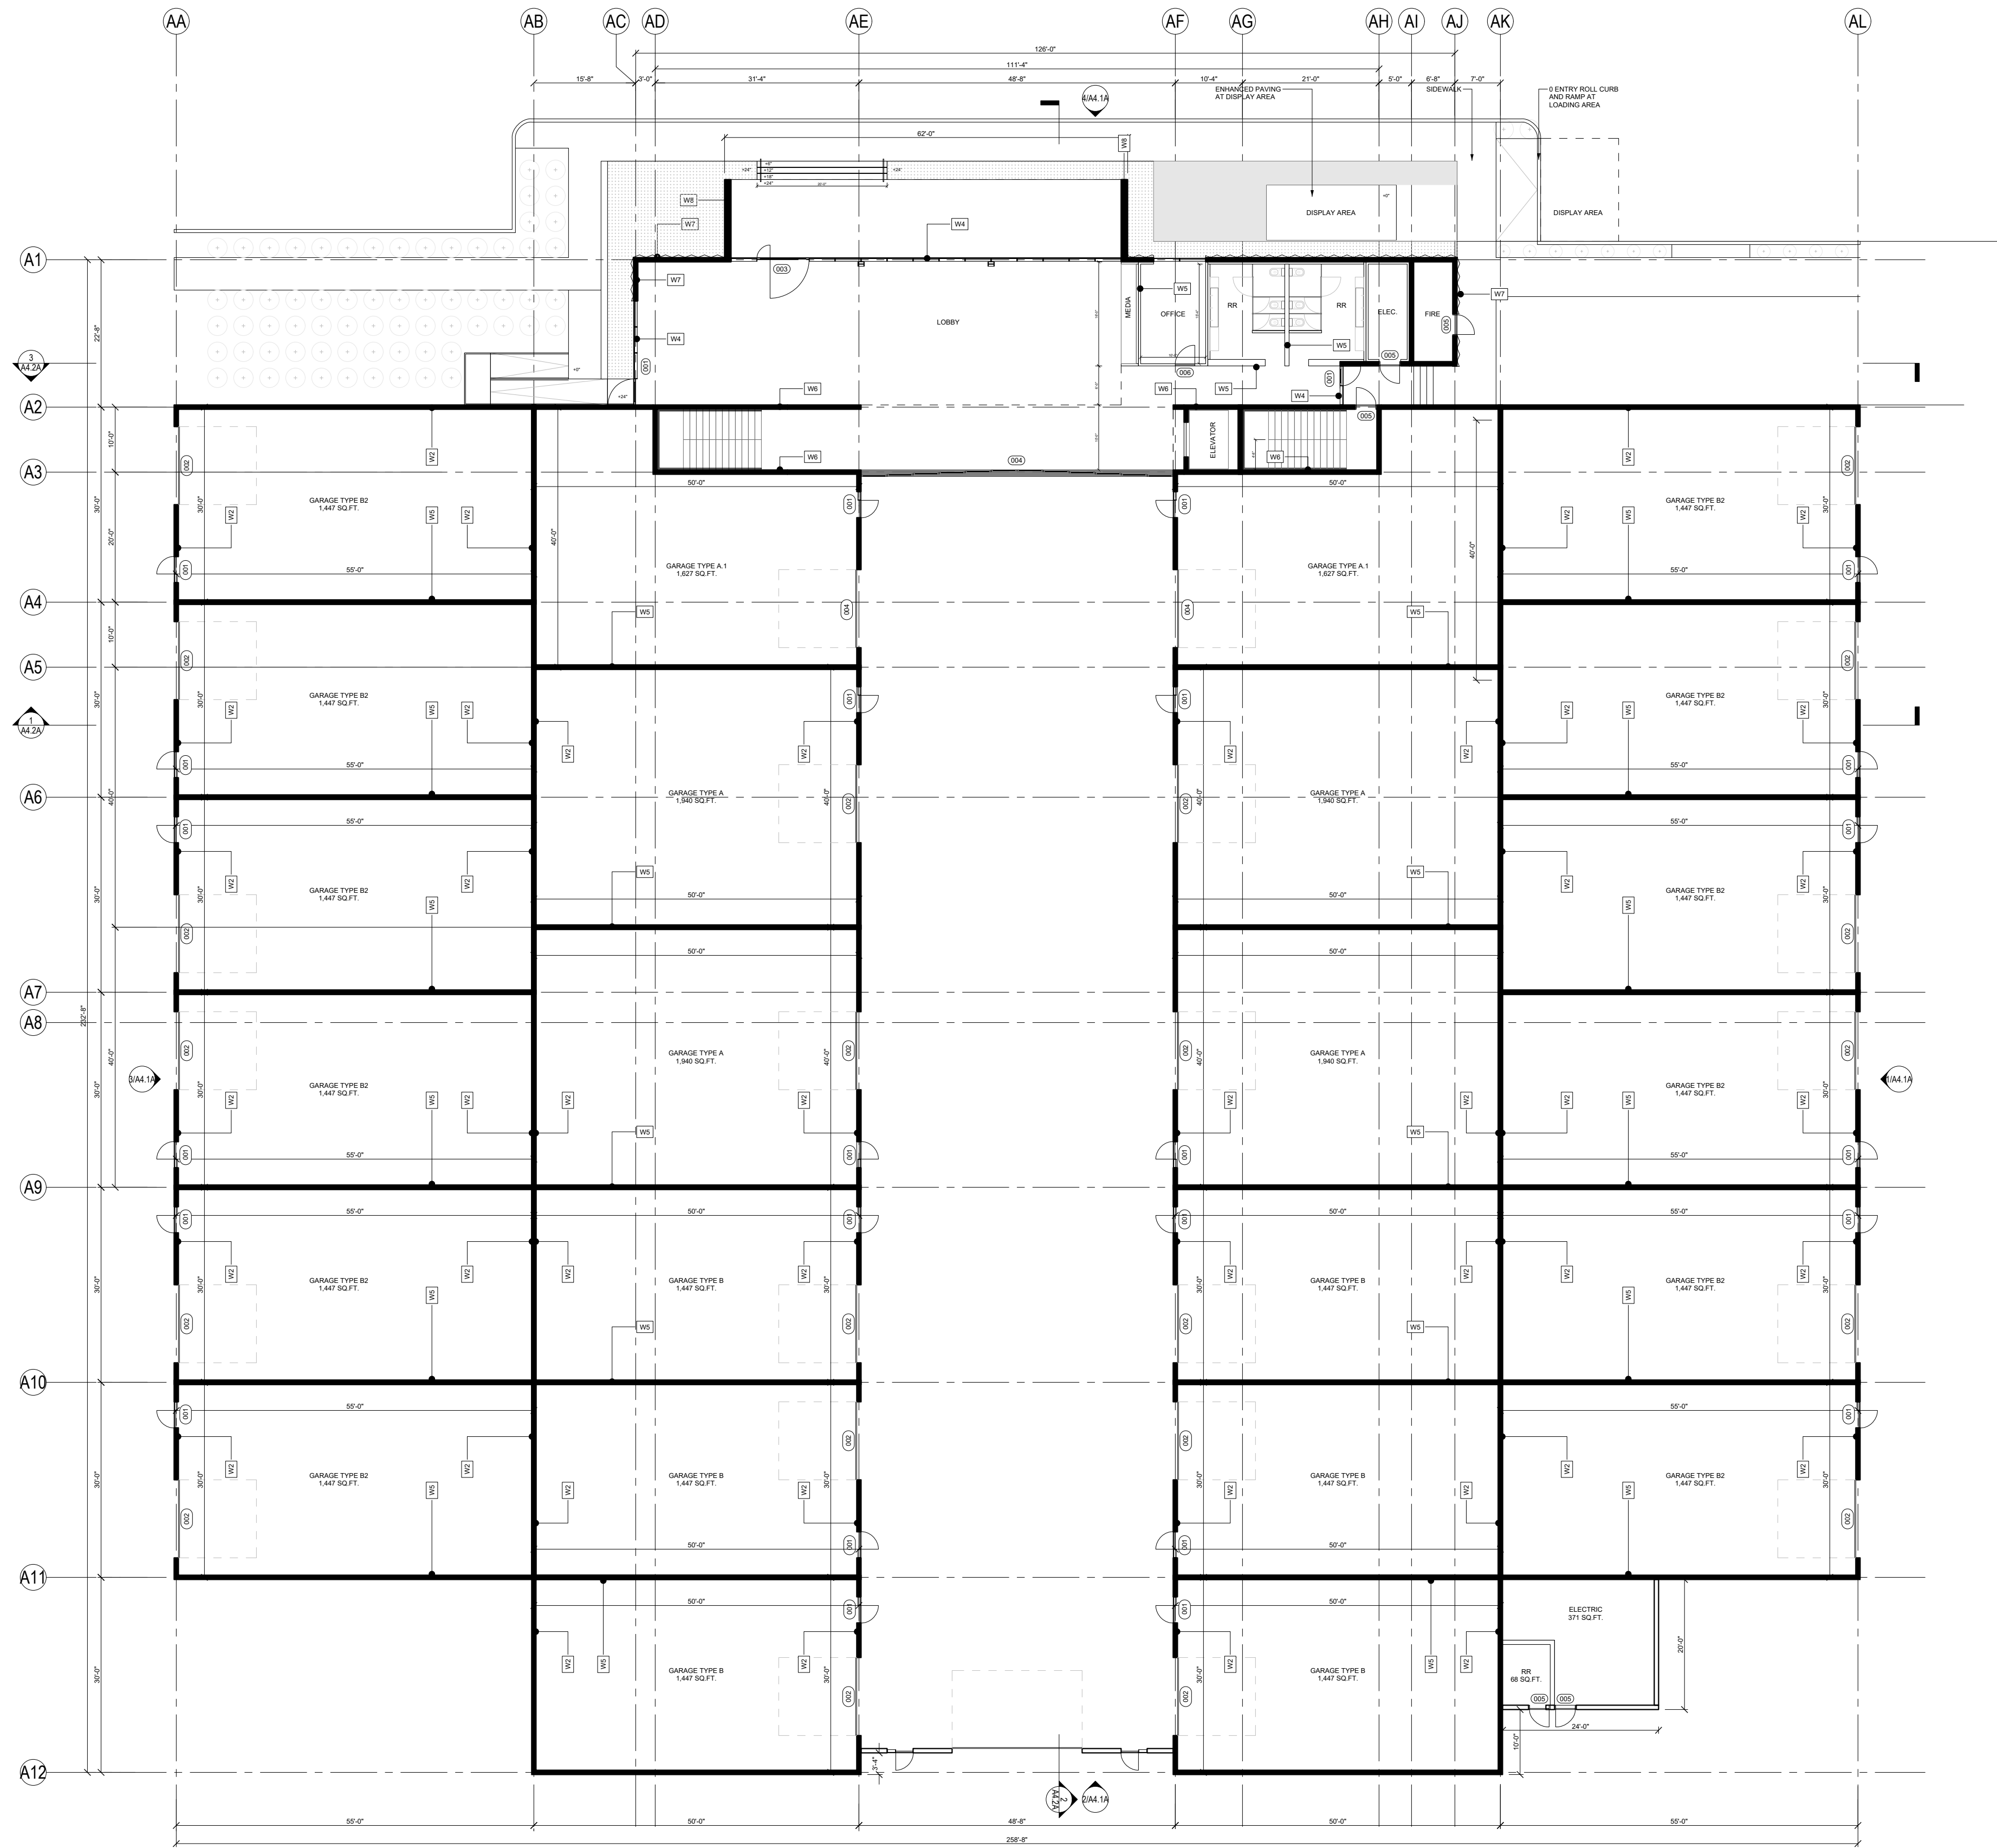


EXTERIOR WALLS

EXTERIOR WALL ASSEMBLY KEY:

- W1 METAL PANEL CLAD 8" CMU EXTERIOR WALL WITH [P1] PAINTED GYP INTERIOR
- W2 8" CMU EXTERIOR WALL WITH [P1] PAINTED GYP INTERIOR
- W3 EXTERIOR STEEL FRAME STOREFRONT, [P4] + [G1] FINISH.
- W4 GLASS CURTAIN WALL ASSEMBLY, NATURAL FINISH + [G2]
- W5 INTERIOR STEEL FRAME ASSEMBLY, GYP ON BOTH SIDES PAINTED WITH [P1]
- W6 8" CMU WALL UNFINISHED
- W7 PERFORATED METAL PANEL RAIN SCREEN CLAD 8" CMU EXTERIOR WALL WITH PAINTED GYP INTERIOR
- W8 METAL PANEL CLAD 8" CMU EXTERIOR WALL WITH [MP3] CLAD INTERIOR

01 PLAN - BUILDING A
SCALE: 1/16" = 1'-0"

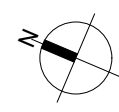

FINISH LINE AUTO CLUB

17600 PERIMETER DR 100
SCOTTSDALE, AZ 85255

LGE | DESIGNBUILD

NUMBER	REVISION	DATE

UPDATE


PRICING SET
NOT TO BE USED
FOR CONSTRUCTION

SHEET TITLE:	PLAN - BUILDING A
ISSUE DATE:	03/25/25
DRAWN BY:	AE
CHECKED BY:	RH
PROJECT No.:	000000
SHEET:	000000

A2.1A

LGE | DESIGNGROUP

1200 N. 52nd Street ■ Phoenix, AZ ■ 85008
P. 480.966.4001

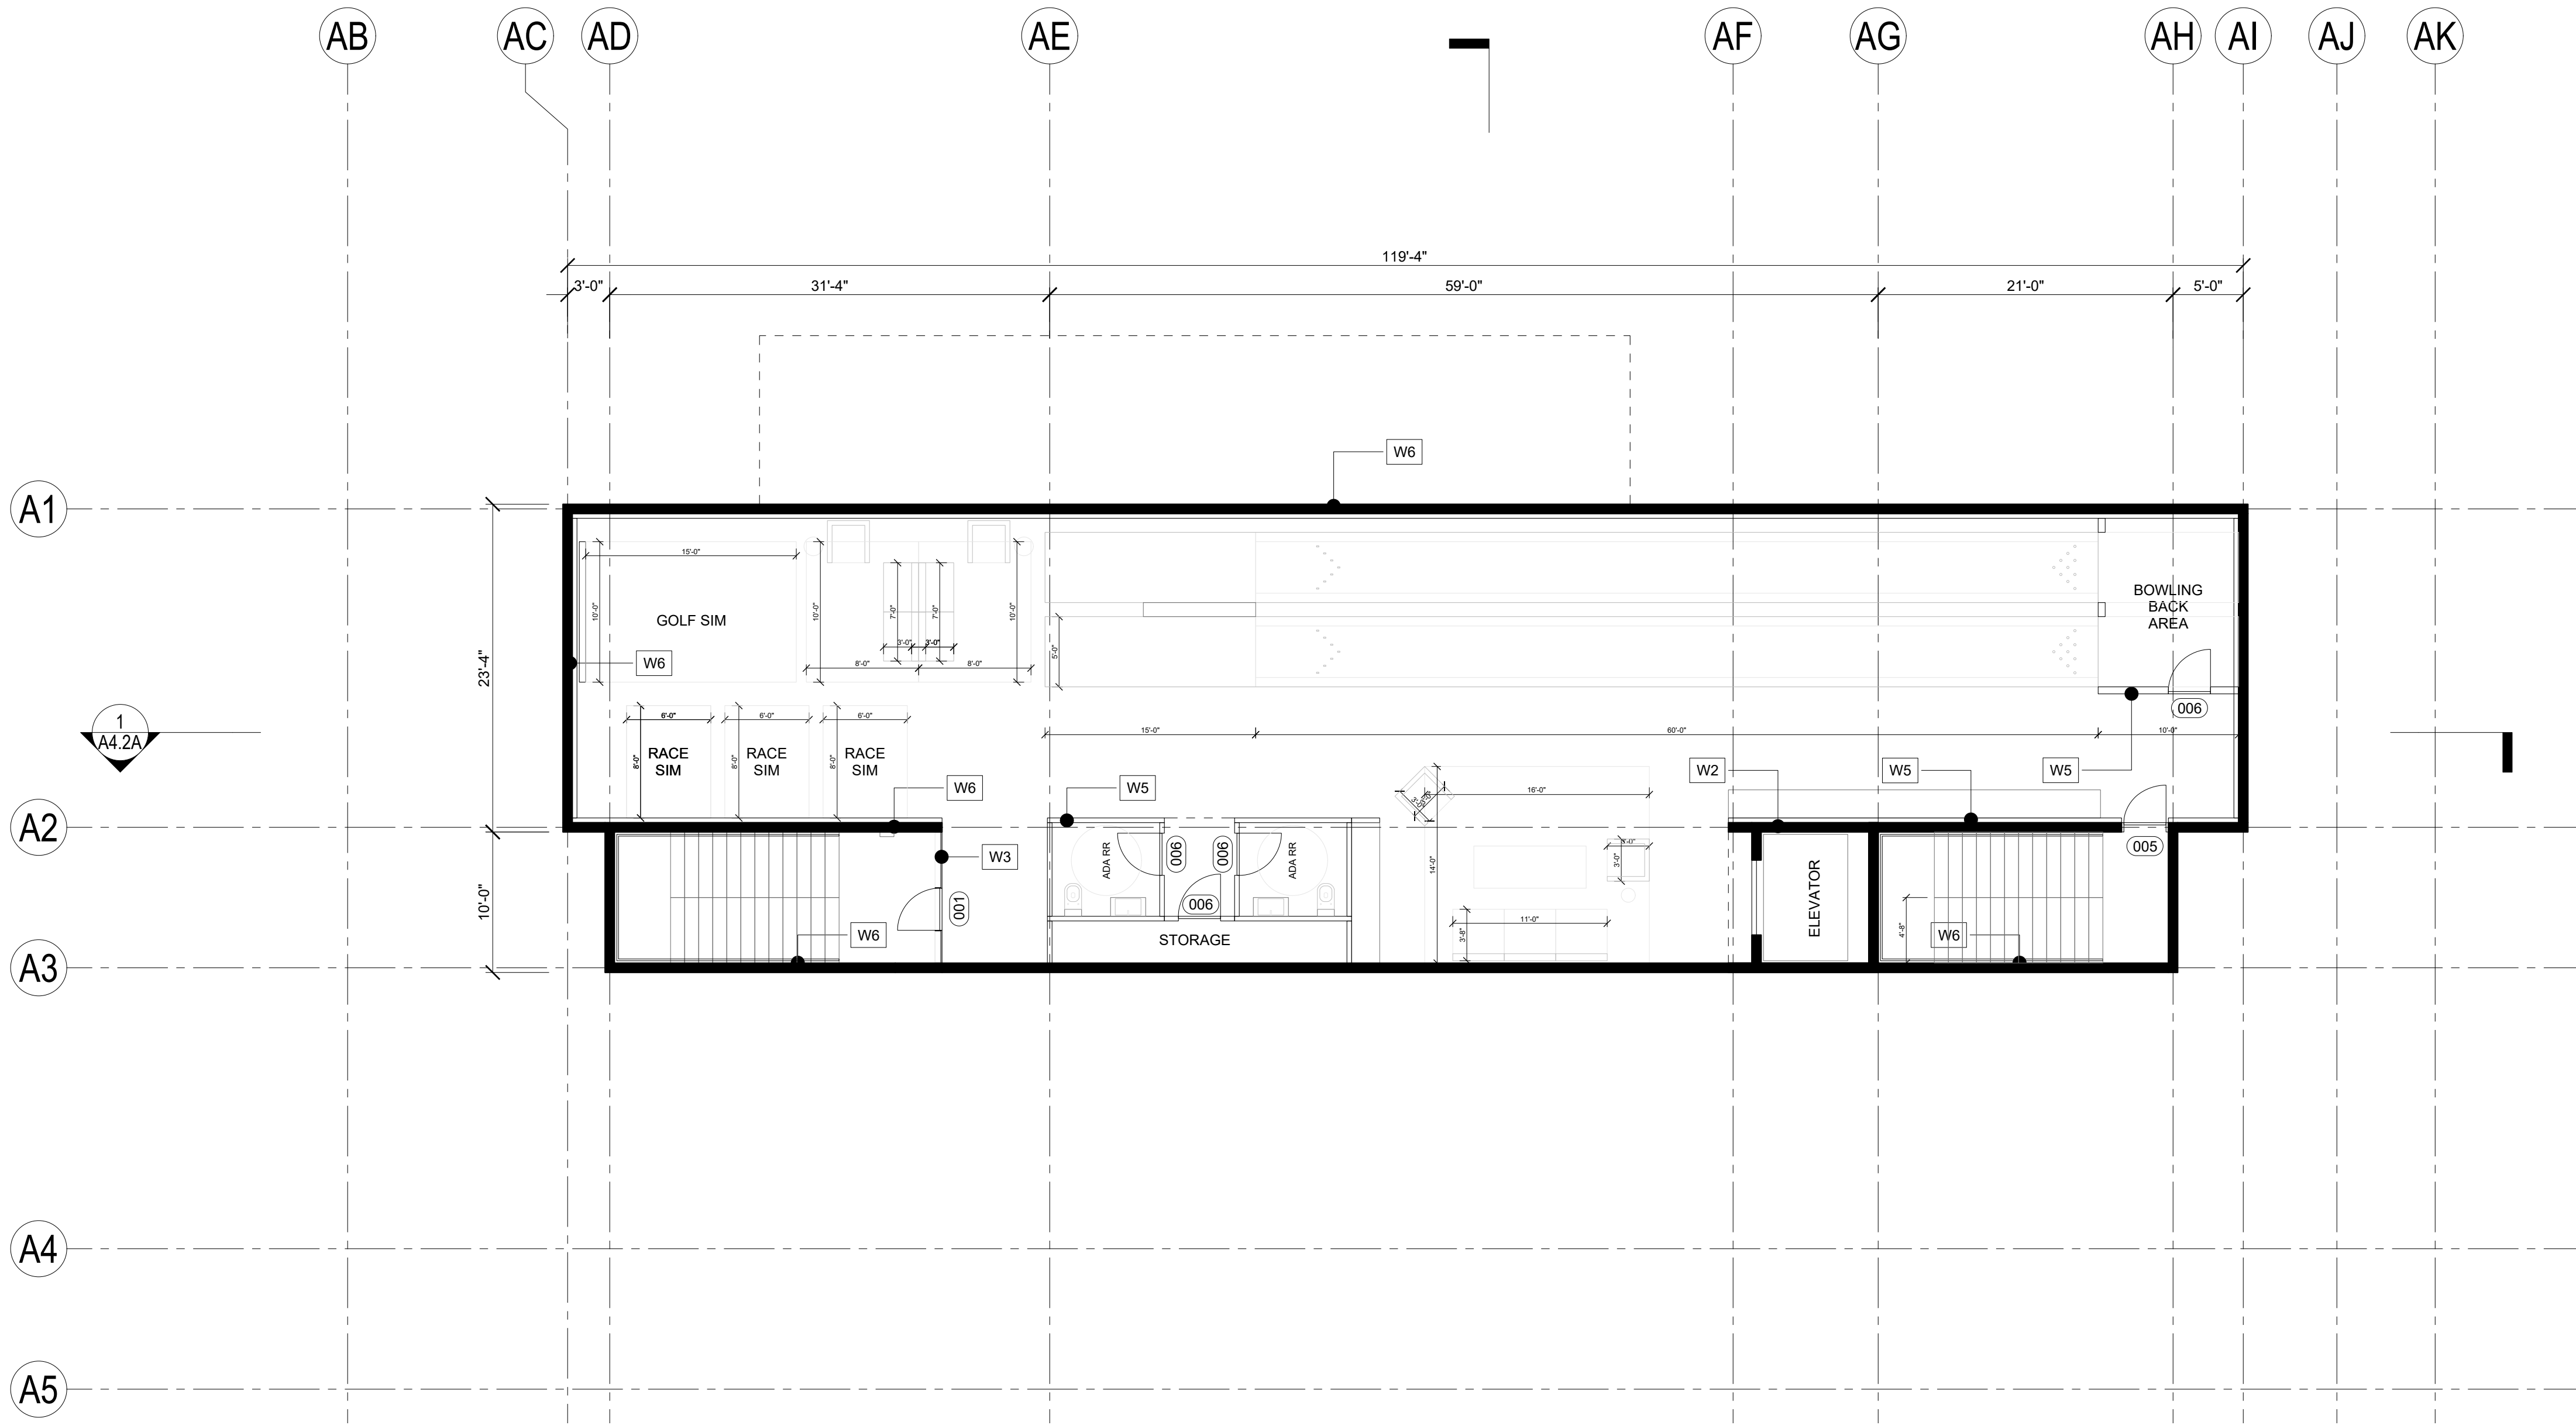

EXTERIOR WALLS

EXTERIOR WALL ASSEMBLY KEY:

- W1

METAL PANEL CLAD 8" CMU EXTERIOR WALL WITH [P1] PAINTED GYP INTERIOR
- W2

8" CMU EXTERIOR WALL WITH [P1] PAINTED GYP INTERIOR
- W3

EXTERIOR STEEL FRAME STOREFRONT, [P4] + [G1] FINISH.
- W4

GLASS CURTAIN WALL ASSEMBLY, NATURAL FINISH + [G2]
- W5


INTERIOR STEEL FRAME ASSEMBLY, GYP ON BOTH SIDES PAINTED WITH [P1]
- W6

8" CMU WALL UNFINISHED
- W7

PERFORATED METAL PANEL RAIN SCREEN CLAD 8" CMU EXTERIOR WALL WITH PAINTED GYP INTERIOR
- W8

METAL PANEL CLAD 8" CMU EXTERIOR WALL WITH [MP3] CLAD INTERIOR

01 PLAN - CLUBHOUSE LOWER LEVEL
SCALE: 1/8" = 1'-0"

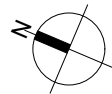

CLIMATE ZONE	1		2		3		4 EXCEPT MARINE		5 AND MARINE 4		6
	All other	Group R	All other	Group R	All other	Group R	All other	Group R	All other	Group R	All other
Insulation entirely above roof deck	R-20ci	R-25ci	R-25ci	R-25ci	R-25ci	R-25ci	R-30ci	R-30ci	R-30ci	R-30ci	R-30ci
Metal buildings ^a	R-19 + R-11 LS	R-19 + R-11 LS	R-19 + R11 LS	R-19 + R-11 LS	R-19 + R-11 LS	R-19 + R-11 LS	R-19 + R-11 LS	R-19 + R-11 LS	R-19 + R-11 LS	R-25 + R-11 LS	
Attic and other	R-38	R-38	R-38	R-38	R-38	R-38	R-38	R-38	R-38	R-49	R-49
Walls, above grade											
Mass ^b	R-5.7ci ^c	R-5.7ci ^c	R-5.7ci ^c	R-7.6ci	R-7.6ci	R-9.5ci	R-9.5ci	R-11.4ci	R-11.4ci	R-13.3ci	R-13.3ci
Metal building	R-13 + R-6.5ci	R-13 + R-6.5ci	R-13 + R-6.5ci	R-13 + R-13ci	R-13 + R-6.5ci	R-13 + R-13ci	R-13 + R-13ci	R-13 + R-13ci	R-13 + R-13ci	R-13 + R-13ci	R-13 + R-13ci
Metal framed	R-13 + R-5ci	R-13 + R-5ci	R-13 + R-5ci	R-13 + R-7.5ci	R-13 + R-7.5ci	R-13 + R-7.5ci	R-13 + R-7.5ci	R-13 + R-7.5ci	R-13 + R-7.5ci	R-13 + R-7.5ci	R-13 + R-7.5ci
Wood framed and other	R-13 + R-3.8ci or R-20	R-13 + R-3.8ci or R-20	R-13 + R-3.8ci or R-20	R-13 + R-3.8ci or R-20	R-13 + R-3.8ci or R-20	R-13 + R-3.8ci or R-20	R-13 + R-3.8ci or R-20	R-13 + R-3.8ci or R-20	R-13 + R-3.8ci or R-20	R-13 + R-7.5ci or R-20 + R-3.8ci	R-13 + R-7.5ci or R-20 + R-3.8ci
Walls, below grade											
Below-grade wall ^d	NR	NR	NR	NR	NR	NR	R-7.5ci	R-7.5ci	R-7.5ci	R-7.5ci	R-7.5ci
Floors											
Mass ^e	NR	NR	R-6.3ci	R-8.3ci	R-10ci	R-10ci	R-10ci	R-10ci	R-10ci	R-12.5ci	R-12.5ci
Joist/framing	NR	NR	R-30	R-30	R-30	R-30	R-30	R-30	R-30	R-30	R-30
Slab-on-grade floors											
Unheated slabs	NR	NR	NR	NR	NR	NR	R-10 for 24" below	R-10 for 24" below	R-10 for 24" below	R-10 for 24" below	R-10 for 24" below
Heated slabs ^f	R-7.5 for 12" below + R-5full slab	R-7.5 for 12" below + R-5full slab	R-7.5 for 12" below + R-5full slab	R-7.5 for 12" below + R-5full slab	R-10 for 24" below + R-5full slab	R-10 for 24" below + R-5full slab	R-15 for 24" below + R-5full slab	R-15 for 24" below + R-5full slab	R-15 for 36" below + R-5full slab	R-15 for 36" below + R-5full slab	R-15 for 36" below + R-5full slab
Opaque doors											
Nonswinging	R-4.75	R-4.75	R-4.75	R-4.75	R-4.75	R-4.75	R-4.75	R-4.75	R-4.75	R-4.75	R-4.75

For SI: 1 inch = 25.4 mm; 1 pound per square foot = 4.88 kg/m²; 1 pound per cubic foot = 16 kg/m³.
ci = Continuous insulation, NR = No Requirement, LS = Liner System.
^a Assembly descriptions can be found in ANSI/ASHRAE/ESNA Appendix A.
^b Where using R-value compliance method, a thermal spacer block shall be provided; otherwise use the U-factor compliance method in Table C402.1.4.
^c R-5.7ci is allowed to be substituted with concrete block walls complying with ASTM C90, ungrouted or partially grouted at 92 inches or less on center vertically and 48 inches or less on center horizontally with ungrouted cores filled with materials having a maximum thermal conductivity of 0.44 Btu-in/h·ft²·°F.
^d Where heated slabs are below grade, below-grade walls shall comply with the exterior insulation requirements for heated slabs.
^e Mass Floor/Ceiling top assemblies with Section C402.2.4.6.

FINISH LINE AUTO CLUB

LGE

DESIGNGROUP

1200 N. 52nd Street ■ Phoenix, AZ ■ 85008
P. 480.966.4001

17600 PERIMETER DR 100
SCOTTSDALE, AZ 85255

LGE | DESIGNBUILD


NUMBER REVISION DATE

UPDATE

PRICING SET
NOT TO BE USED
FOR CONSTRUCTION

SHEET TITLE:
PLAN - CLUBHOUSE LOWER LEVEL
ISSUE DATE: 03/25/25
DRAWN BY: AE
CHECKED BY: RH
PROJECT No.: 000000
SHEET:

A2.2A

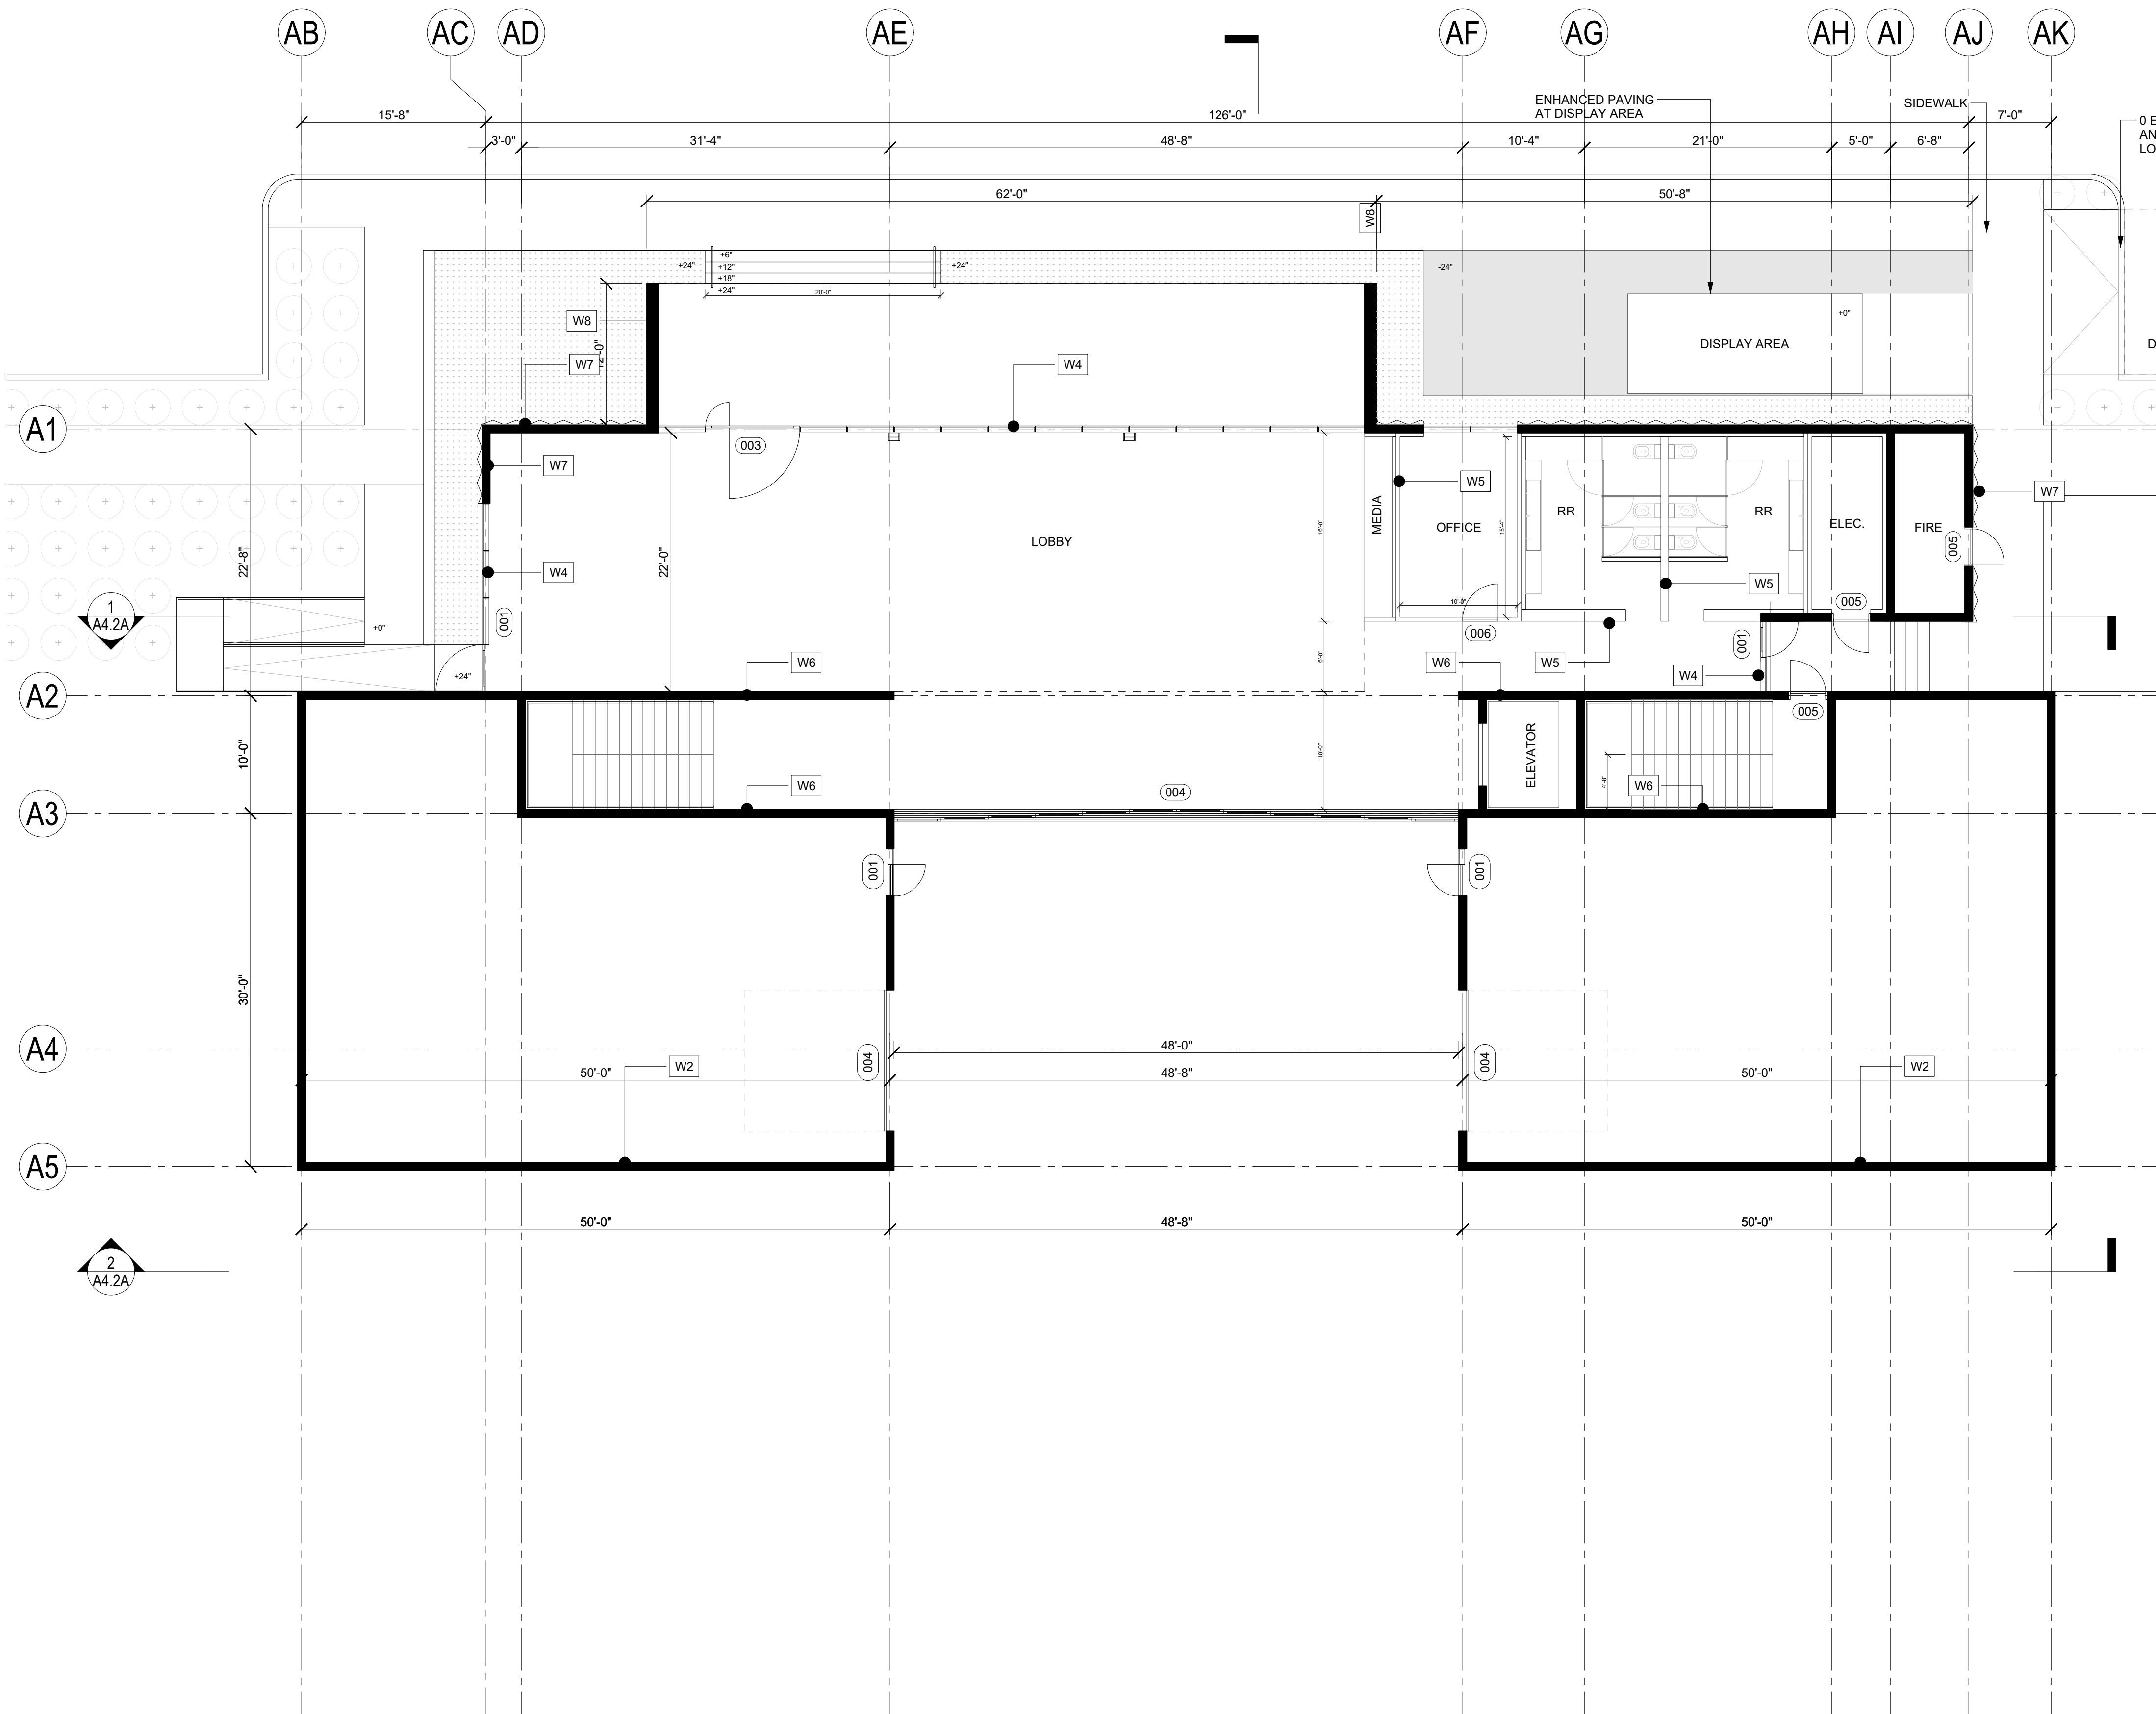


EXTERIOR WALLS

EXTERIOR WALL ASSEMBLY KEY:

- W1 METAL PANEL CLAD 8" CMU EXTERIOR WALL WITH [P1] PAINTED GYP INTERIOR
- W2 8" CMU EXTERIOR WALL WITH [P1] PAINTED GYP INTERIOR
- W3 EXTERIOR STEEL FRAME STOREFRONT, [P4] + [G1] FINISH.
- W4 GLASS CURTAIN WALL ASSEMBLY, NATURAL FINISH + [G2]
- W5 INTERIOR STEEL FRAME ASSEMBLY, GYP ON BOTH SIDES PAINTED WITH [P1]
- W6 8" CMU WALL UNFINISHED
- W7 PERFORATED METAL PANEL RAIN SCREEN CLAD 8" CMU EXTERIOR WALL WITH PAINTED GYP INTERIOR
- W8 METAL PANEL CLAD 8" CMU EXTERIOR WALL WITH [MP3] CLAD INTERIOR

01 PLAN - CLUBHOUSE LEVEL 1
SCALE: 1/8" = 1'-0"

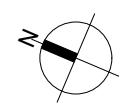

FINISH LINE AUTO CLUB

17600 PERIMETER DR 100
SCOTTSDALE, AZ 85255

LGE | DESIGNBUILD

NUMBER	REVISION	DATE

UPDATE
PRICING SET
NOT TO BE USED
FOR CONSTRUCTION

SHEET TITLE:
PLAN - CLUBHOUSE LEVEL 1

ISSUE DATE: 03/25/25

DRAWN BY: AE

CHECKED BY: RH


PROJECT No.: 000000

SHEET:

A2.3A

LGE | DESIGNGROUP

1200 N. 52nd Street ■ Phoenix, AZ 85008
P: 480.966.4001

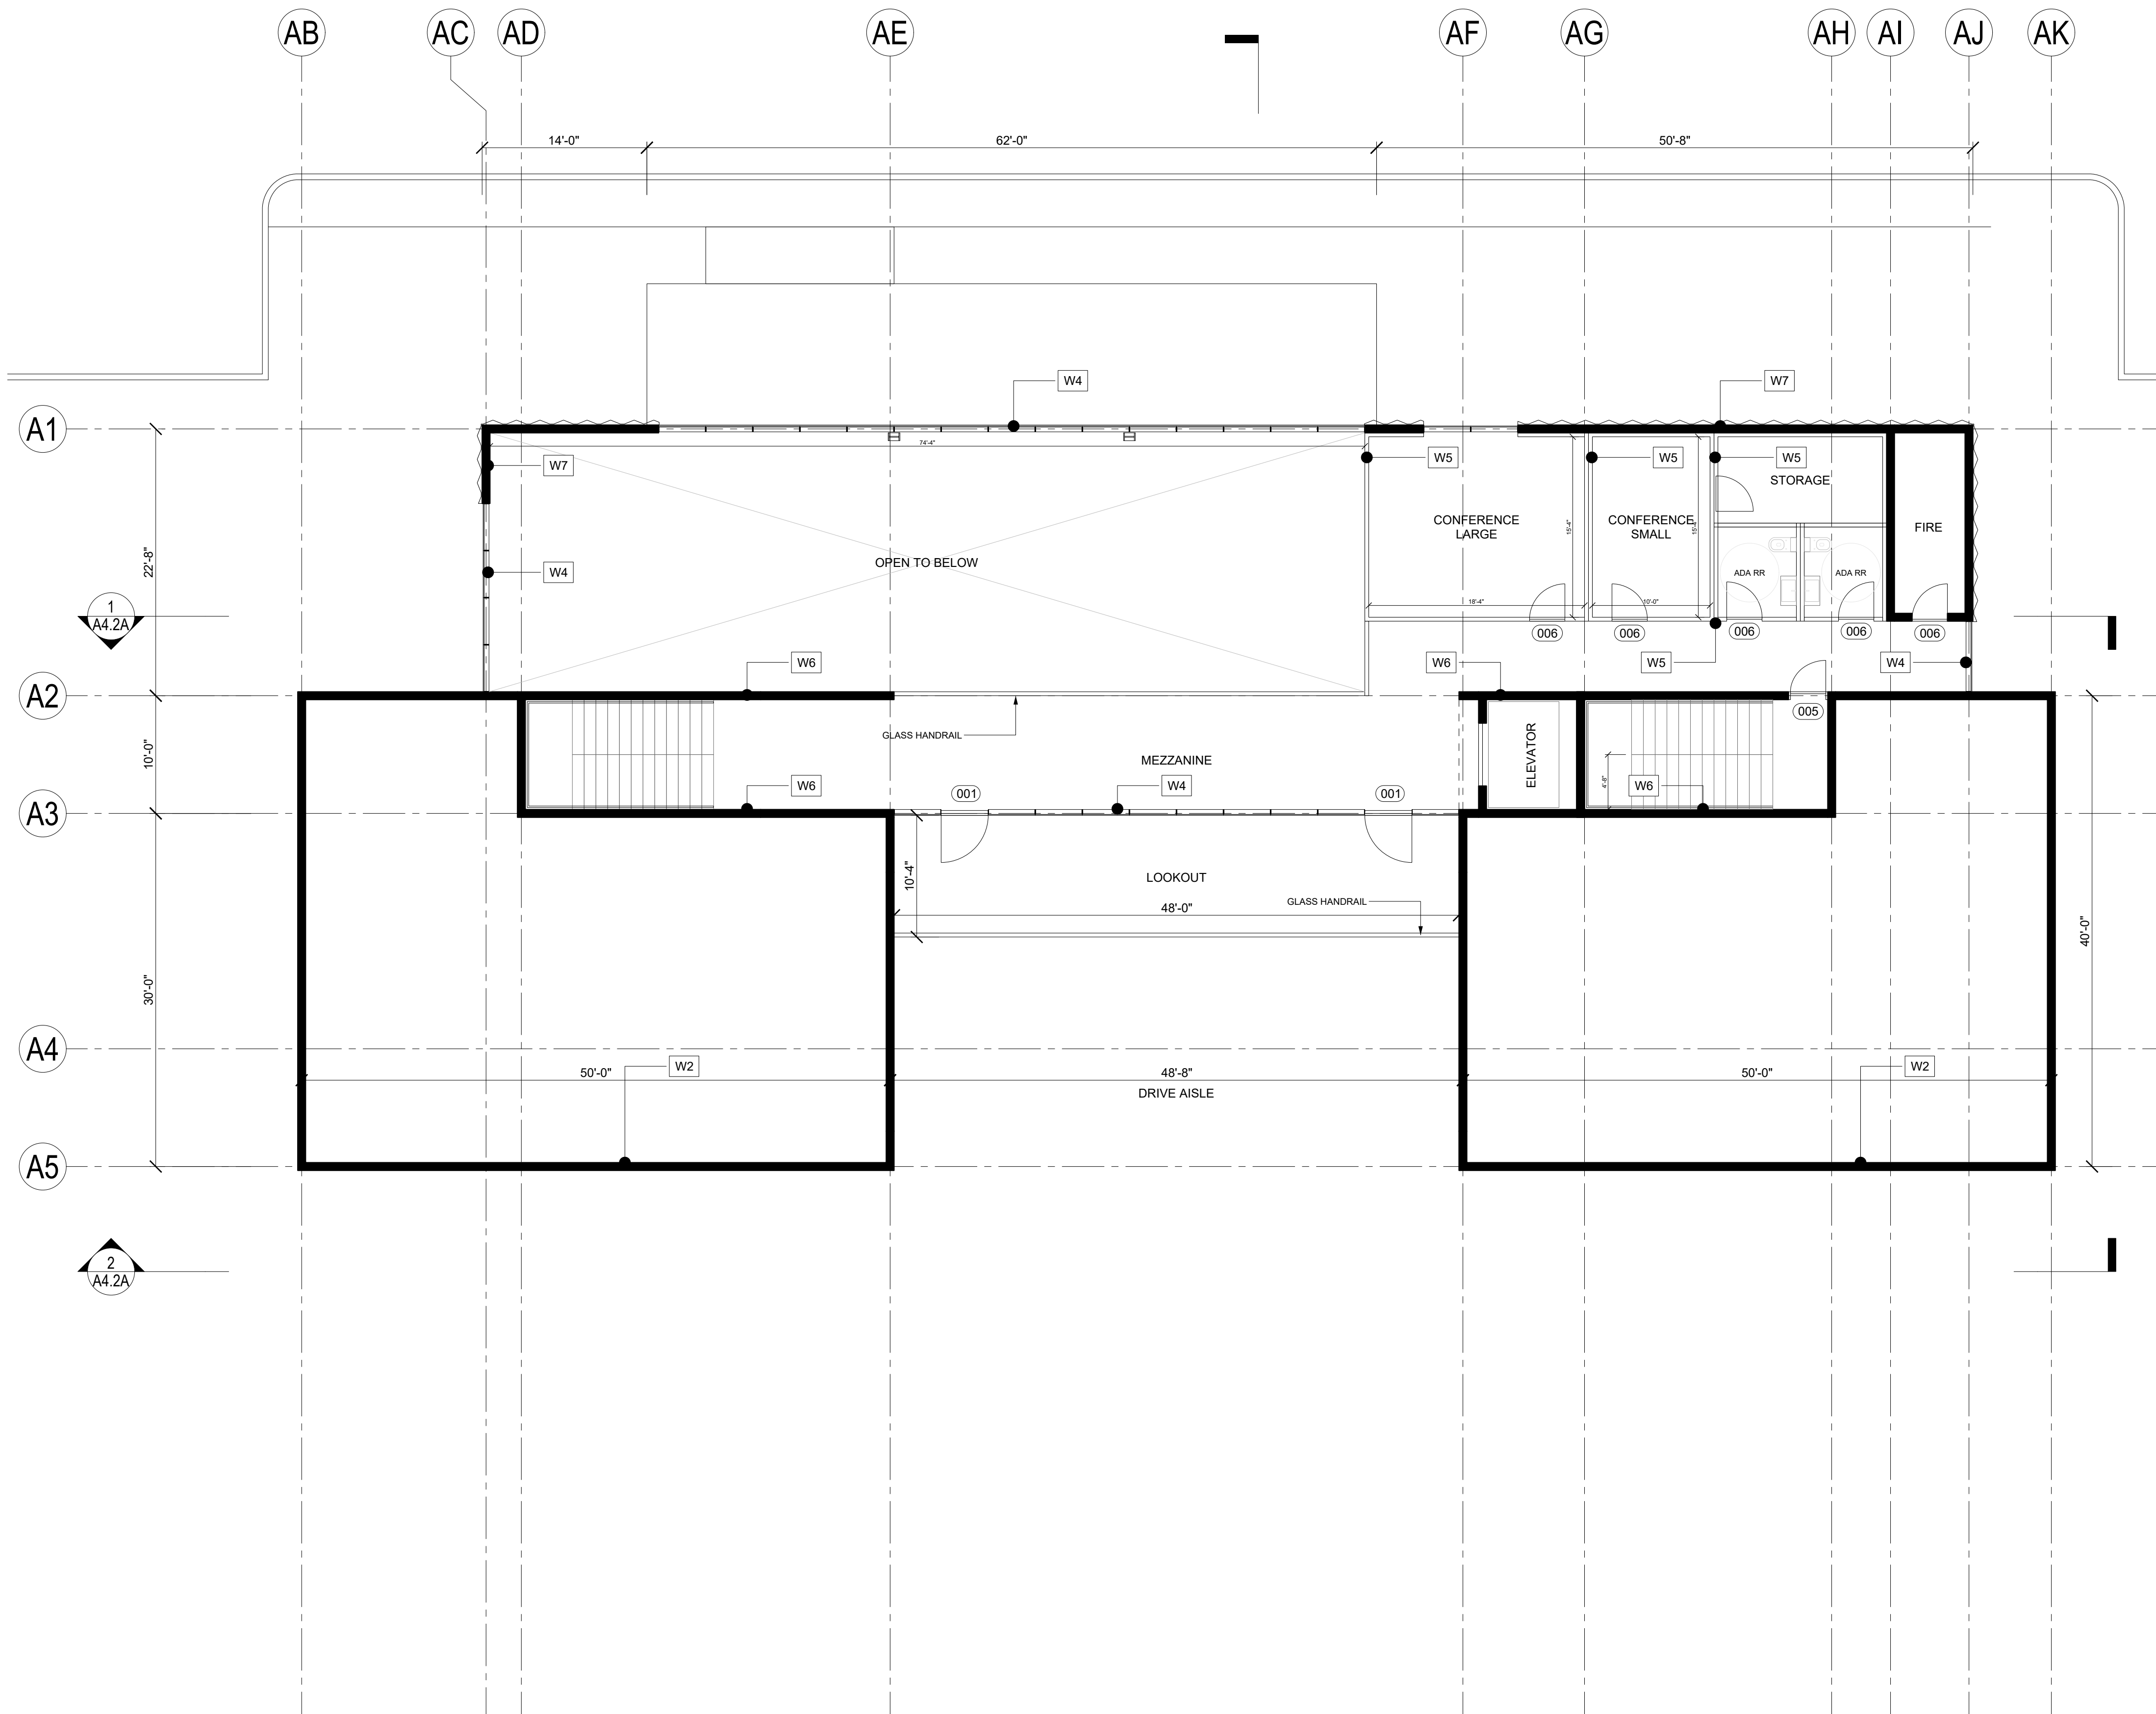


EXTERIOR WALLS

EXTERIOR WALL ASSEMBLY KEY:

- | | |
|----|--|
| W1 | METAL PANEL CLAD 8" CMU EXTERIOR WALL WITH [P1] PAINTED GYP INTERIOR |
| W2 | 8" CMU EXTERIOR WALL WITH [P1] PAINTED GYP INTERIOR |
| W3 | EXTERIOR STEEL FRAME STOREFRONT, [P4] + [G1] FINISH. |
| W4 | GLASS CURTAIN WALL ASSEMBLY, NATURAL FINISH + [G2] |
| W5 | INTERIOR STEEL FRAME ASSEMBLY, GYP ON BOTH SIDES PAINTED WITH [P1] |
| W6 | 8" CMU WALL UNFINISHED |
| W7 | PERFORATED METAL PANEL RAIN SCREEN CLAD 8" CMU EXTERIOR WALL WITH PAINTED GYP INTERIOR |
| W8 | METAL PANEL CLAD 8" CMU EXTERIOR WALL WITH [MP3] CLAD INTERIOR |

01 PLAN - CLUBHOUSE LEVEL 2
SCALE: 1/8" = 1'-0"

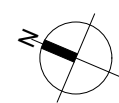

FINISH LINE AUTO CLUB

17600 PERIMETER DR 100
SCOTTSDALE, AZ 85255

LGE | DESIGNBUILD

NUMBER	REVISION	DATE
--------	----------	------


UPDATE
PRICING SET
NOT TO BE USED
FOR CONSTRUCTION

SHEET TITLE:
PLAN - CLUBHOUSE LEVEL 2
ISSUE DATE: 03/25/25
DRAWN BY: AE
CHECKED BY: RH
PROJECT No.: 000000
SHEET:

A2.4A

LGE | DESIGNGROUP

1200 N. 52nd Street ■ Phoenix, AZ 85008
P: 480.966.4001

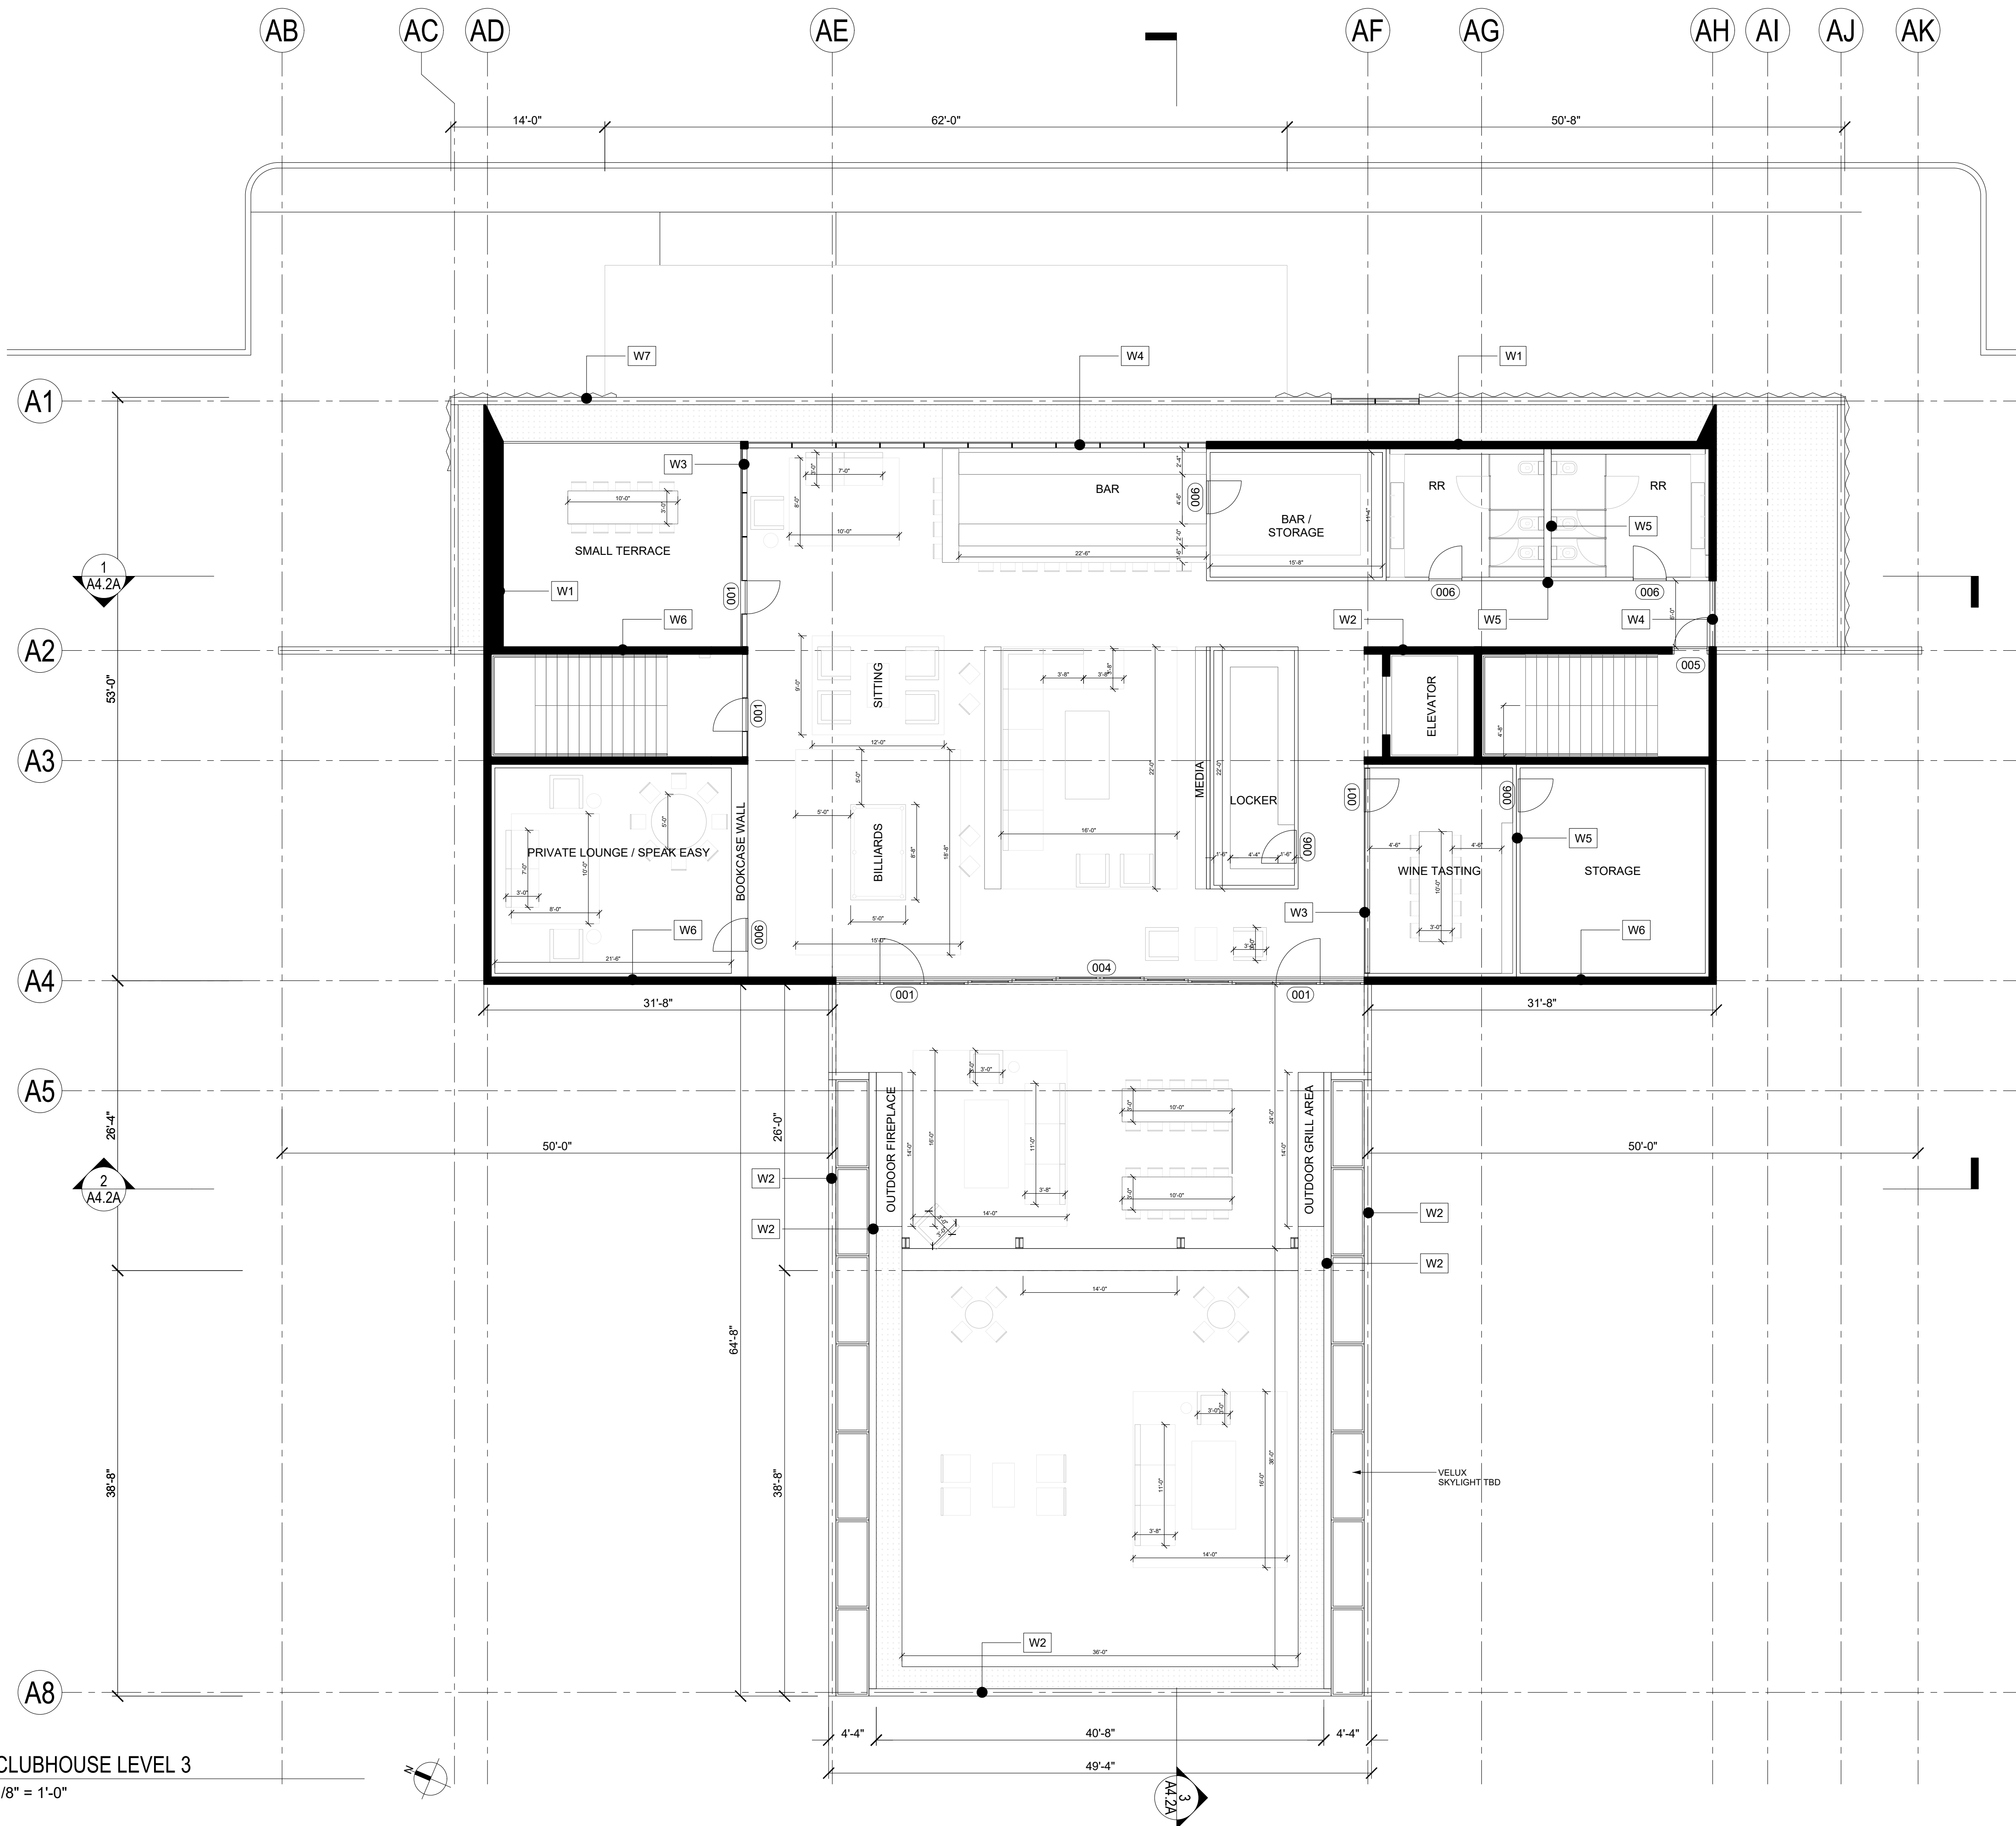

EXTERIOR WALLS

EXTERIOR WALL ASSEMBLY KEY:

- W1 METAL PANEL CLAD 8" CMU EXTERIOR WALL WITH [P1] PAINTED GYP INTERIOR
- W2 8" CMU EXTERIOR WALL WITH [P1] PAINTED GYP INTERIOR
- W3 EXTERIOR STEEL FRAME STOREFRONT, [P4] [G1] FINISH.
- W4 GLASS CURTAIN WALL ASSEMBLY, NATURAL FINISH + [G2]
- W5 INTERIOR STEEL FRAME ASSEMBLY, GYP ON BOTH SIDES PAINTED WITH [P1]
- W6 8" CMU WALL UNFINISHED
- W7 PERFORATED METAL PANEL RAIN SCREEN CLAD 8" CMU EXTERIOR WALL WITH PAINTED GYP INTERIOR
- W8 METAL PANEL CLAD 8" CMU EXTERIOR WALL WITH [MP3] CLAD INTERIOR

01 PLAN - CLUBHOUSE LEVEL 3
SCALE: 1/8" = 1'-0"

FINISH LINE AUTO CLUB

17600 PERIMETER DR 100
SCOTTSDALE, AZ 85255

LGE | DESIGNBUILD

NUMBER	REVISION	DATE
--------	----------	------

UPDATE

PRICING SET
NOT TO BE USED
FOR CONSTRUCTION



SHEET TITLE:	
PLAN - CLUBHOUSE LEVEL 3	
ISSUE DATE:	03/25/25
DRAWN BY:	AE
CHECKED BY:	RH
PROJECT No.:	000000
SHEET:	

A2.5A

LGE | DESIGNGROUP

1200 N. 52nd Street ■ Phoenix, AZ ■ 85008
P. 480.966.4001

01 ROOF PLAN - BUILDING A
SCALE: 1/16" = 1'-0"

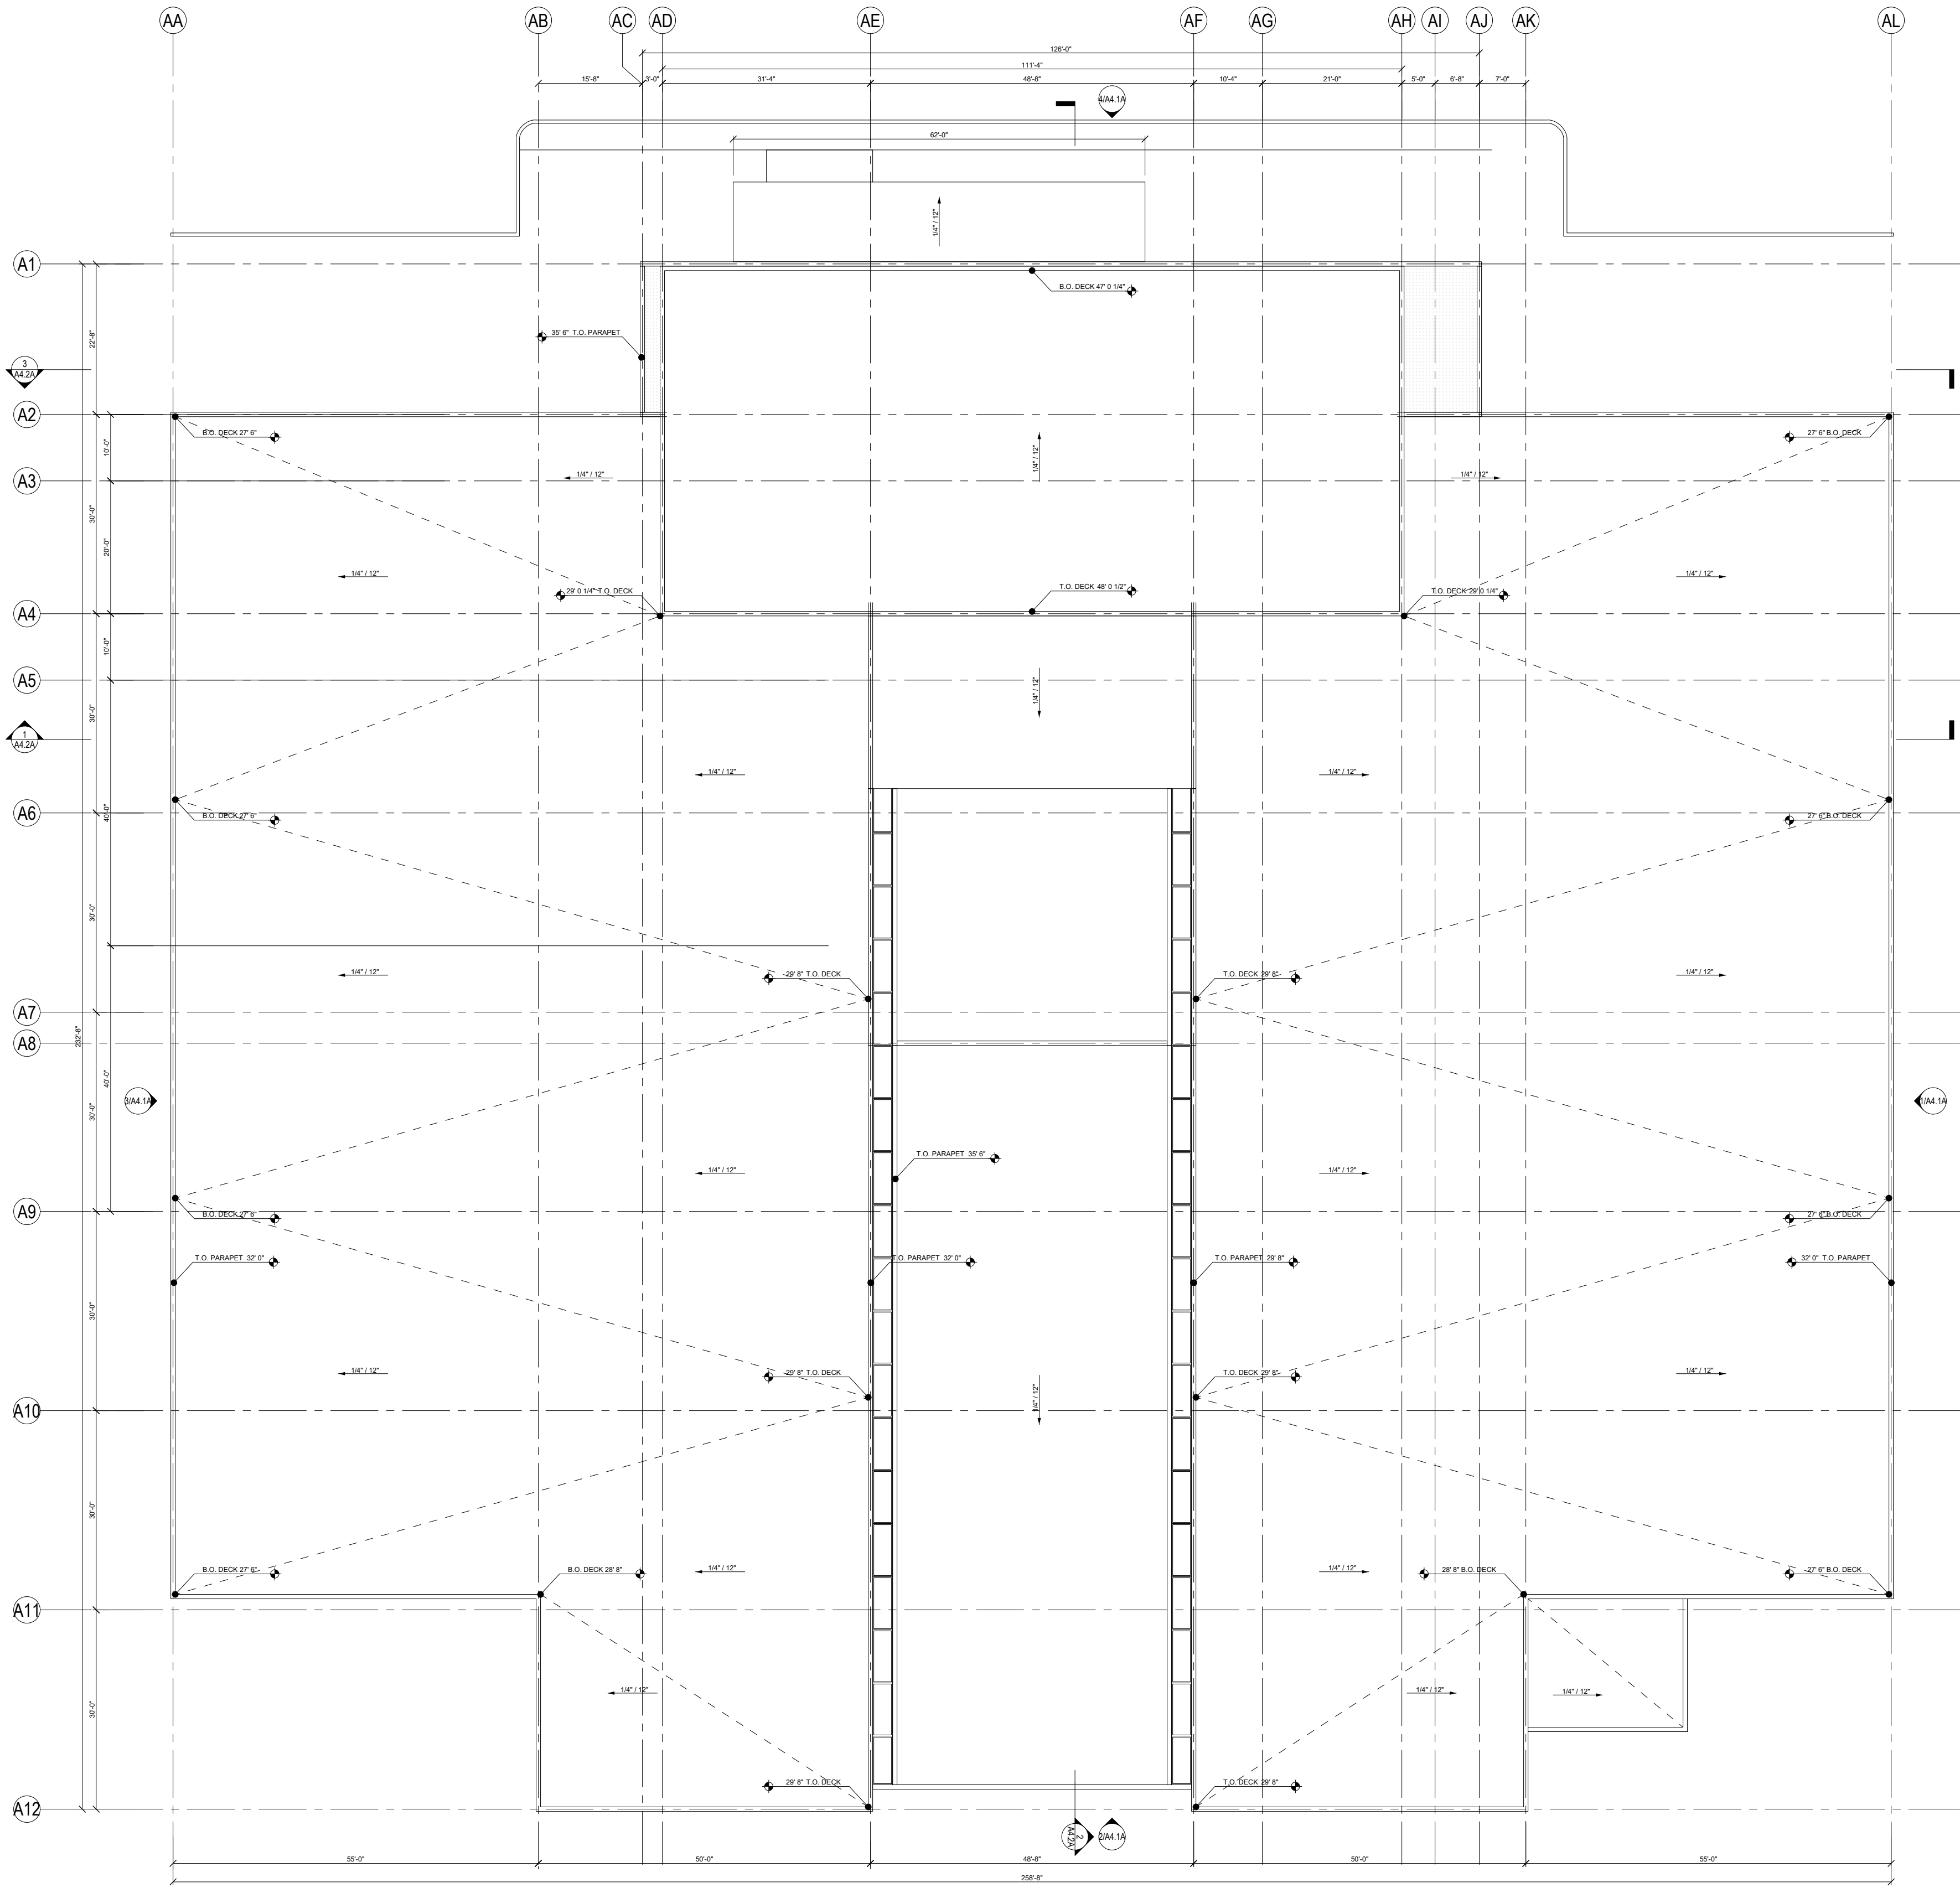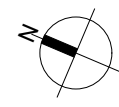

FINISH LINE AUTO CLUB

17600 PERIMETER DR 100
SCOTTSDALE, AZ 85255

LGE | DESIGNBUILD

NUMBER	REVISION	DATE
--------	----------	------

UPDATE

PRICING SET
NOT TO BE USED
FOR CONSTRUCTION


SHEET TITLE:
ROOF PLAN - BUILDING A
ISSUE DATE: 03/25/25
DRAWN BY: AE
CHECKED BY: RH
PROJECT No.: 000000
SHEET:

A3.1A


LGE | DESIGNGROUP

1200 N. 52nd Street ■ Phoenix, AZ 85008

P: 480.966.4001

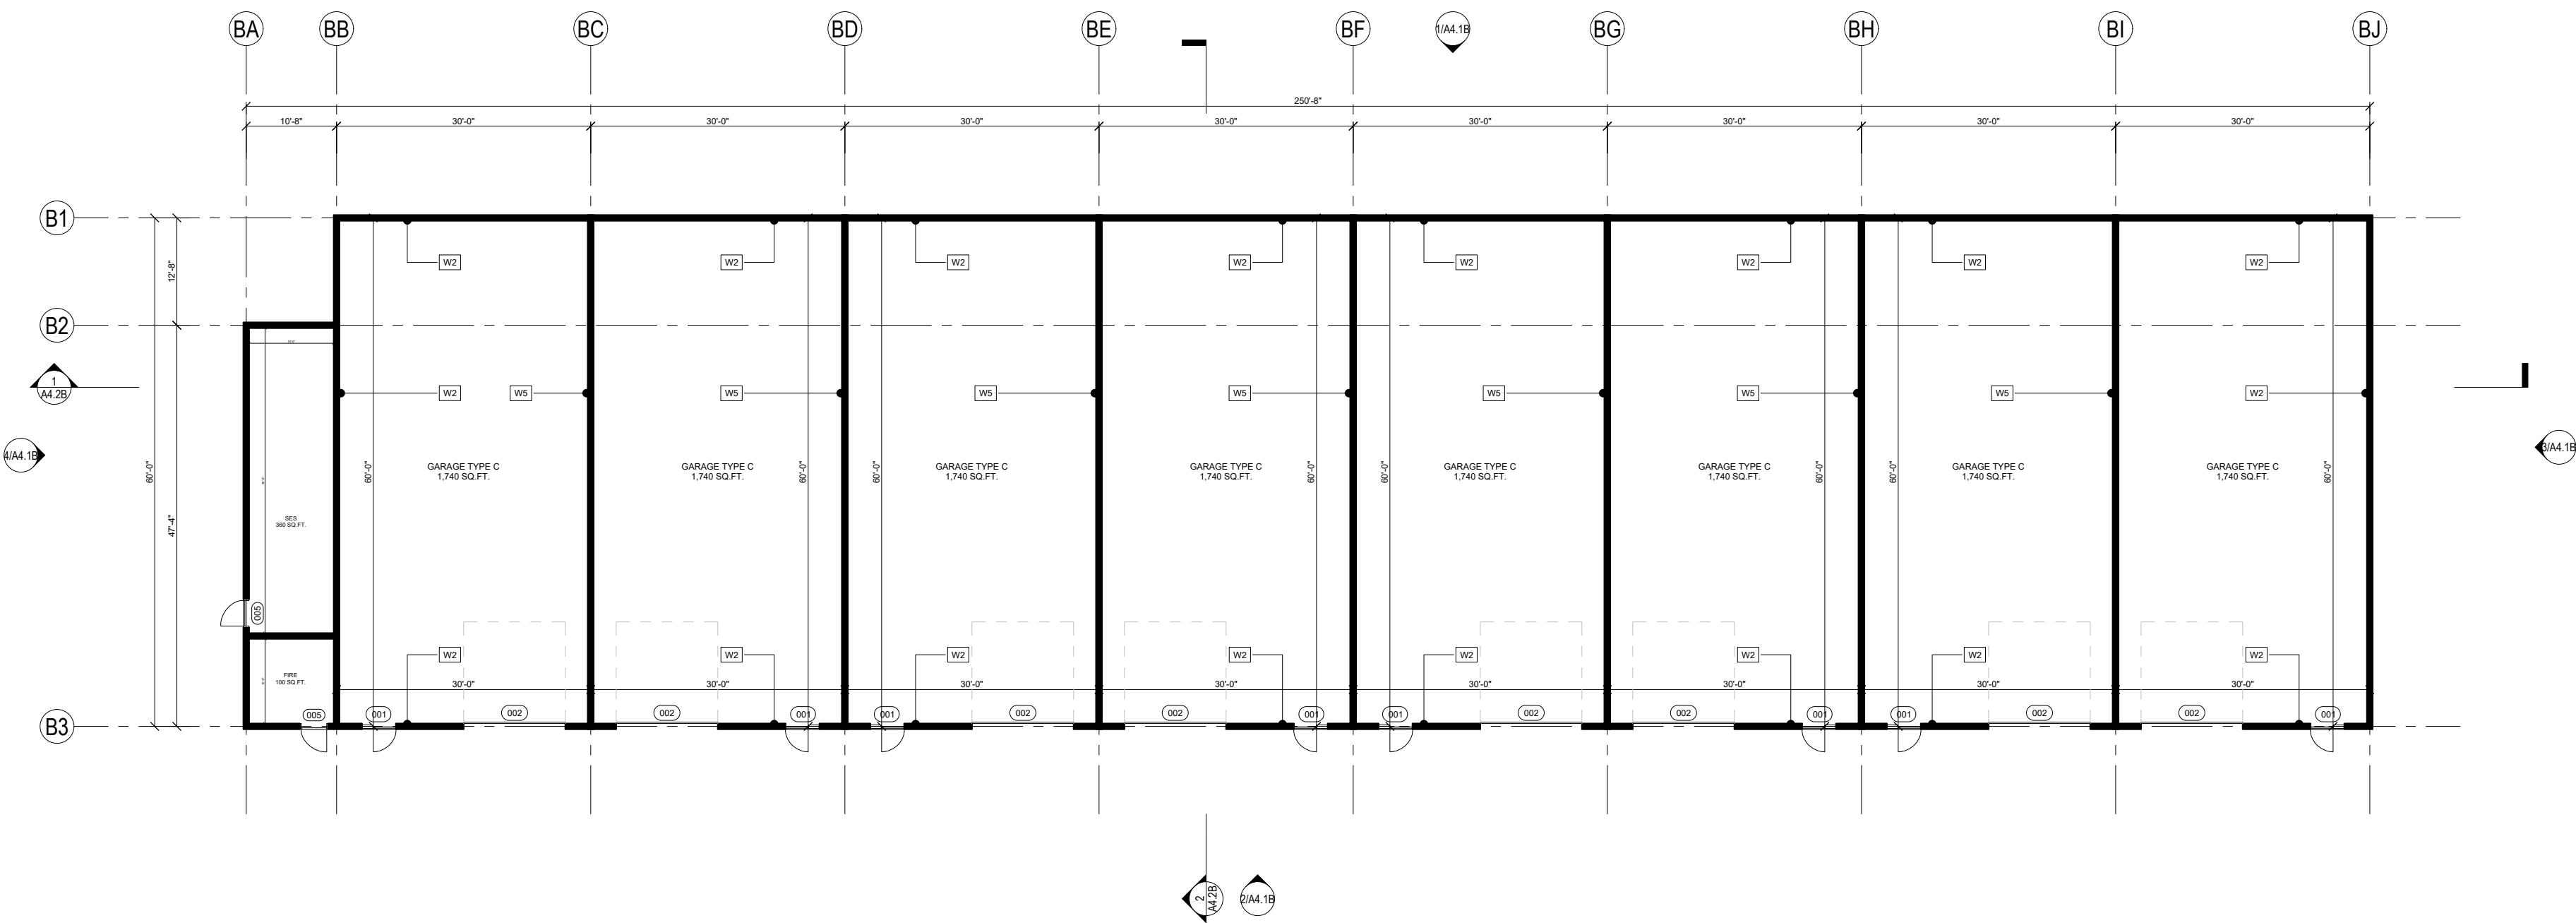

01 PLAN - BUILDING B
SCALE: 1/16" = 1'-0"

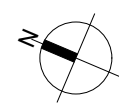

EXTERIOR WALLS

EXTERIOR WALL ASSEMBLY KEY:

- | | |
|----|--|
| W1 | METAL PANEL CLAD 8" CMU EXTERIOR WALL WITH [P1] PAINTED GYP INTERIOR |
| W2 | 8" CMU EXTERIOR WALL WITH [P1] PAINTED GYP INTERIOR |
| W3 | EXTERIOR STEEL FRAME STOREFRONT. [P4] + [G1] FINISH. |
| W4 | GLASS CURTAIN WALL ASSEMBLY. NATURAL FINISH + [G2] |
| W5 | INTERIOR STEEL FRAME ASSEMBLY. GYP ON BOTH SIDES PAINTED WITH [P1] |
| W6 | 8" CMU WALL UNFINISHED |
| W7 | PERFORATED METAL PANEL RAIN SCREEN CLAD 8" CMU EXTERIOR WALL WITH PAINTED GYP INTERIOR |
| W8 | METAL PANEL CLAD 8" CMU EXTERIOR WALL WITH [MP3] CLAD INTERIOR |

LGE | DESIGNGROUP

1200 N. 52nd Street ■ Phoenix, AZ 85008
P: 480.966.4001

FINISH LINE AUTO CLUB

17600 PERIMETER DR 100
SCOTTSDALE, AZ 85255

LGE | DESIGNBUILD


NUMBER	REVISION	DATE
--------	----------	------

UPDATE
PRICING SET
NOT TO BE USED
FOR CONSTRUCTION


SHEET TITLE:	PLAN - BUILDING E
ISSUE DATE:	03/25/25
DRAWN BY:	AE
CHECKED BY:	RH
PROJECT No.:	000000

SHEET:

A2.1B

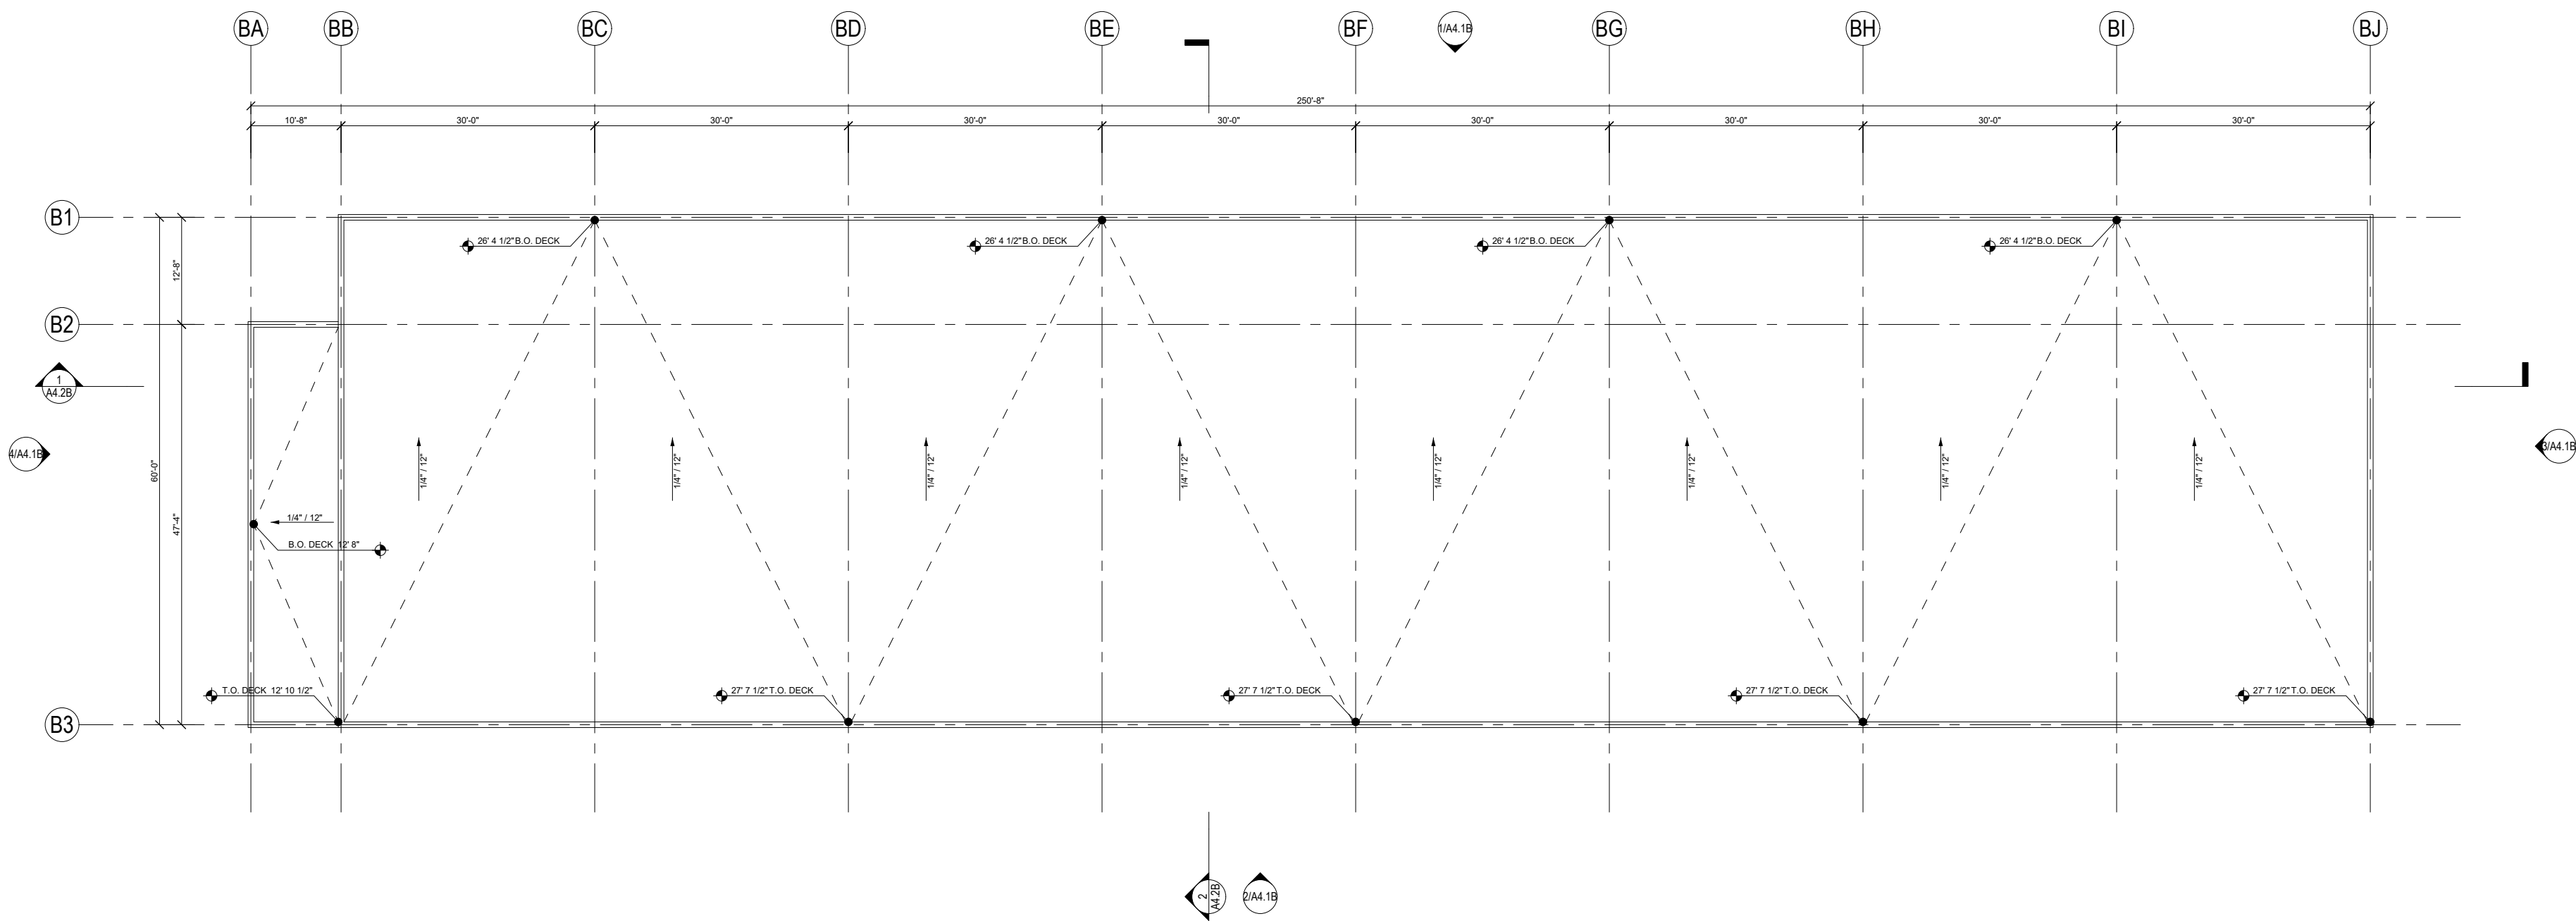

01 ROOF PLAN - BUILDING B
SCALE: 1/16" = 1'-0"

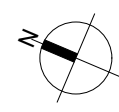

FINISH LINE AUTO CLUB

17600 PERIMETER DR 100
SCOTTSDALE, AZ 85255

LGE | DESIGNBUILD

NUMBER	REVISION	DATE
--------	----------	------

UPDATE
PRICING SET
NOT TO BE USED
FOR CONSTRUCTION

SHEET TITLE:
ROOF PLAN - BUILDING E
ISSUE DATE: 03/25/25
DRAWN BY: AE
CHECKED BY: RH
PROJECT No.: 000000
SHEET:


A3.1B

LGE | DESIGNGROUP

1200 N. 52nd Street ■ Phoenix, AZ ■ 85008
P: 480.966.4001



01 PLAN - BUILDING C
SCALE: 1/16" = 1'-0"

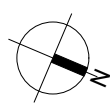

EXTERIOR WALLS

EXTERIOR WALL ASSEMBLY KEY:

- W1 METAL PANEL CLAD 8" CMU EXTERIOR WALL WITH [P1] PAINTED GYP INTERIOR
- W2 8" CMU EXTERIOR WALL WITH [P1] PAINTED GYP INTERIOR
- W3 EXTERIOR STEEL FRAME STOREFRONT. [P4] + [G1] FINISH.
- W4 GLASS CURTAIN WALL ASSEMBLY. NATURAL FINISH + [G2]
- W5 INTERIOR STEEL FRAME ASSEMBLY. GYP ON BOTH SIDES PAINTED WITH [P1]
- W6 8" CMU WALL UNFINISHED
- W7 PERFORATED METAL PANEL RAIN SCREEN CLAD 8" CMU EXTERIOR WALL WITH PAINTED GYP INTERIOR
- W8 METAL PANEL CLAD 8" CMU EXTERIOR WALL WITH [MP3] CLAD INTERIOR

FINISH LINE AUTO CLUB

17600 PERIMETER DR 100
SCOTTSDALE, AZ 85255



NUMBER	REVISION	DATE


UPDATE

PRICING SET
NOT TO BE USED
FOR CONSTRUCTION


SHEET TITLE:	PLAN - BUILDING C
ISSUE DATE:	03/25/25
DRAWN BY:	AE
CHECKED BY:	RH
PROJECT No.:	000000
SHEET:	A2.1C



1200 N. 52nd Street ■ Phoenix, AZ 85008
P. 480.966.4001

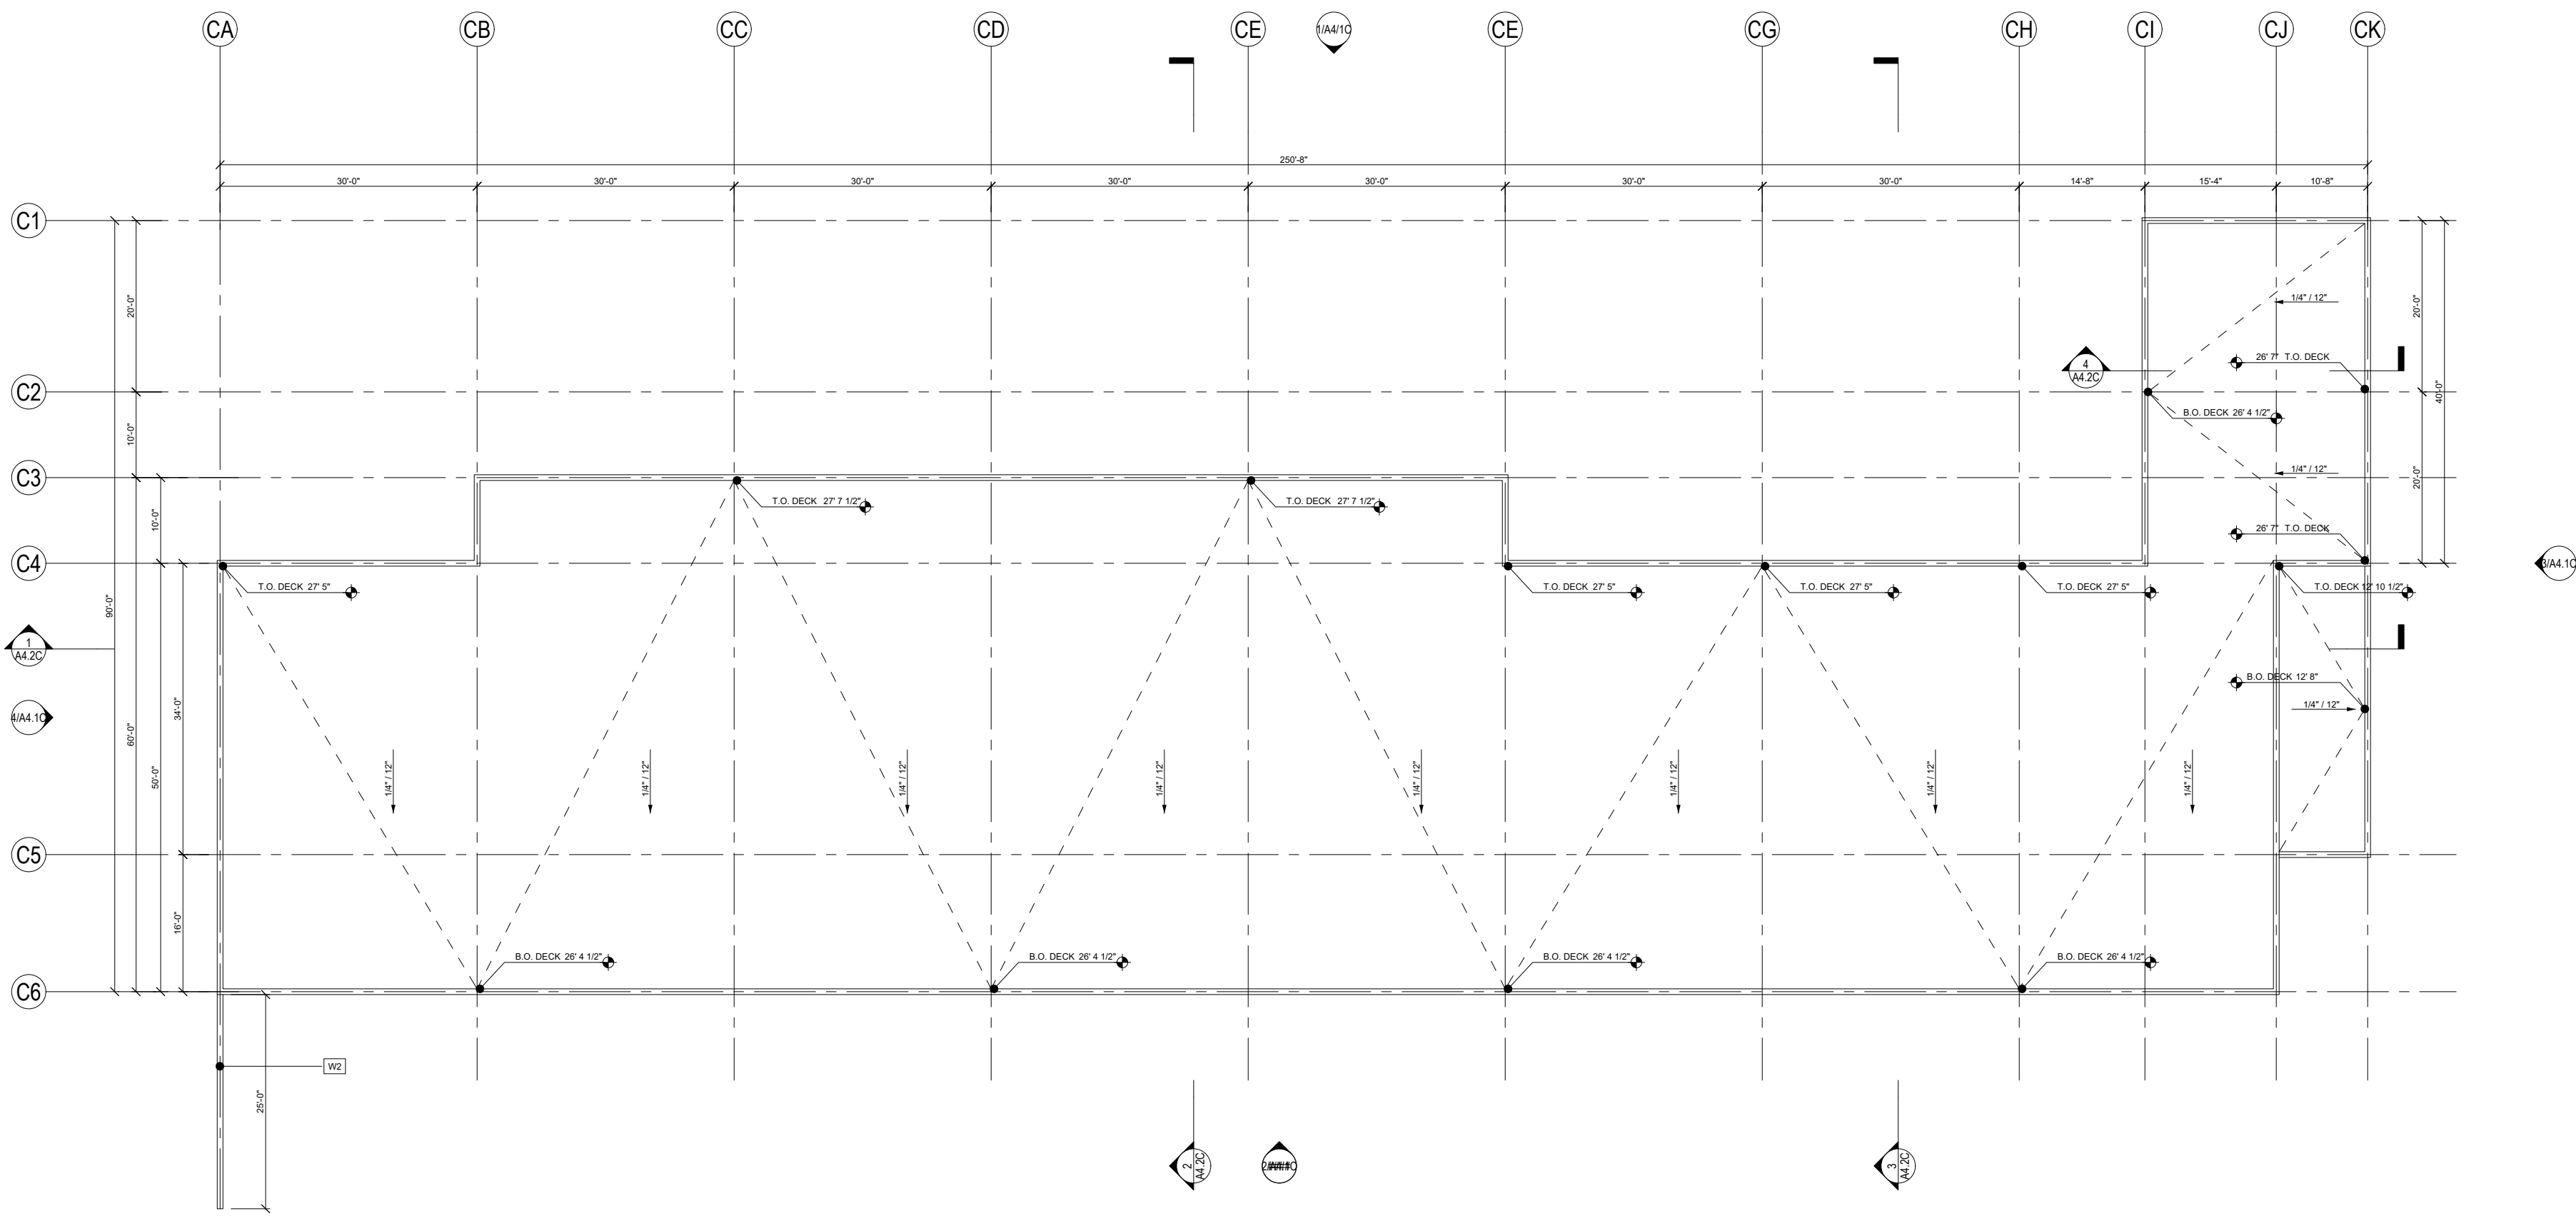

01 ROOF PLAN - BUILDING C
SCALE: 1/16" = 1'-0"

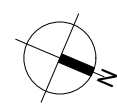

FINISH LINE AUTO CLUB

17600 PERIMETER DR 100
SCOTTSDALE, AZ 85255


LGE | DESIGNBUILD

NUMBER	REVISION	DATE


UPDATE
PRICING SET
NOT TO BE USED
FOR CONSTRUCTION

SHEET TITLE:
ROOF PLAN - BUILDING D
ISSUE DATE: 03/25/25
DRAWN BY: AE
CHECKED BY: RH
PROJECT No.: 000000
SHEET:

A3.1C

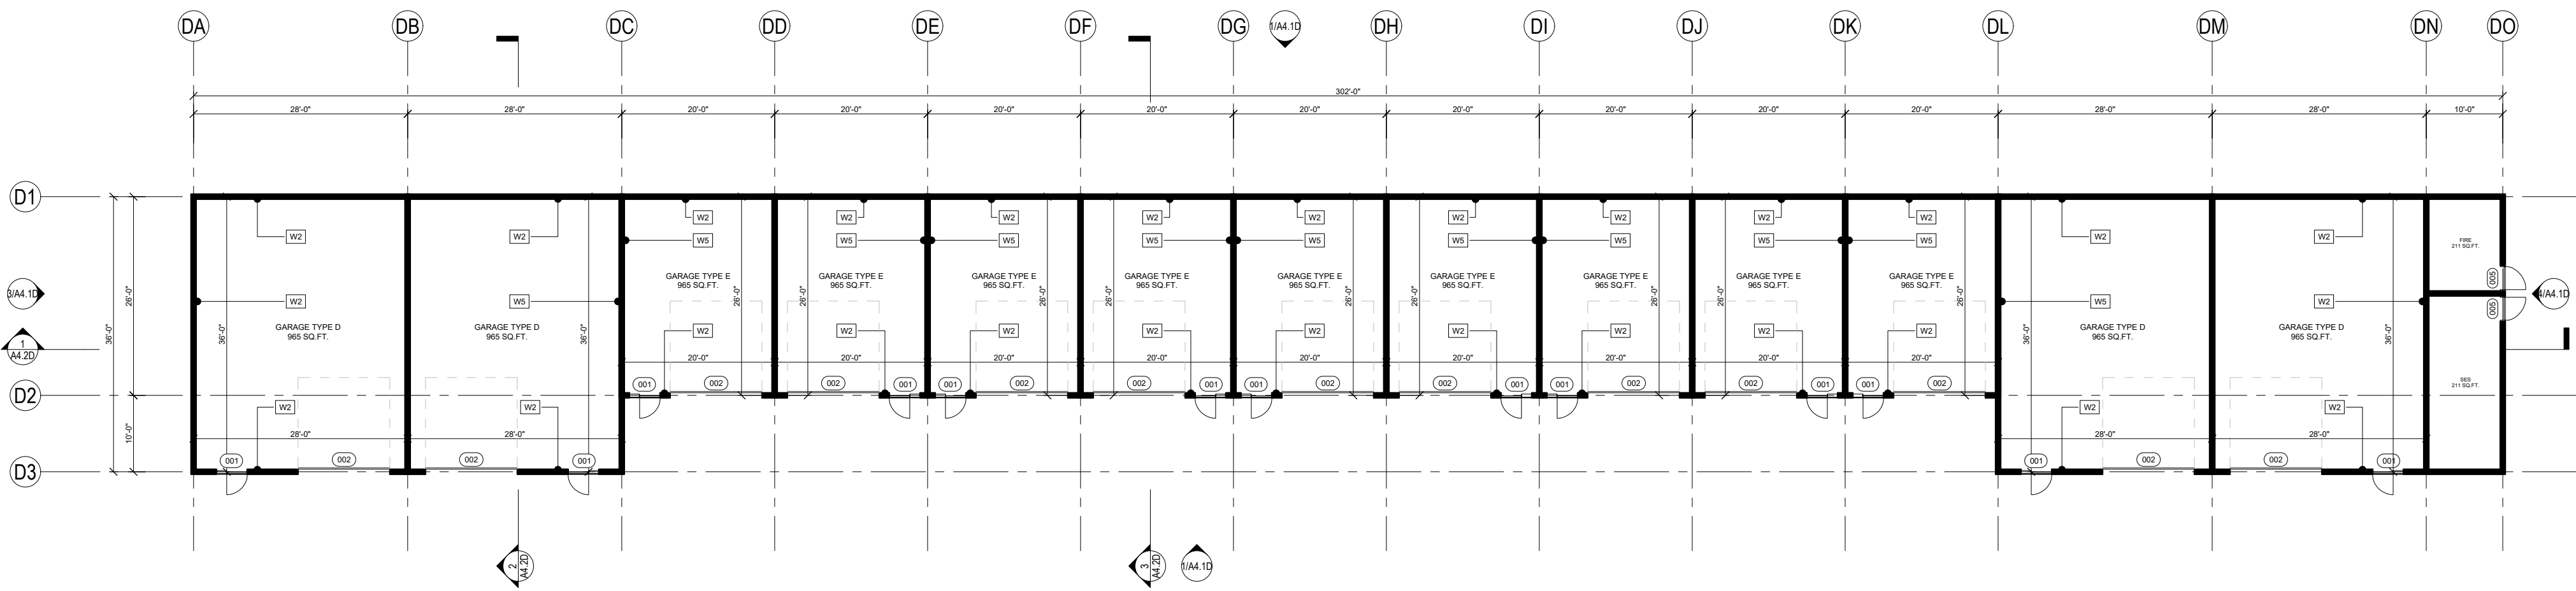

01 PLAN - BUILDING D
SCALE: 1/16" = 1'-0"

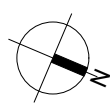

EXTERIOR WALLS

EXTERIOR WALL ASSEMBLY KEY:

- W1 METAL PANEL CLAD 8" CMU EXTERIOR WALL WITH [P1] PAINTED GYP INTERIOR
- W2 8" CMU EXTERIOR WALL WITH [P1] PAINTED GYP INTERIOR
- W3 EXTERIOR STEEL FRAME STOREFRONT. [P4] + [G1] FINISH.
- W4 GLASS CURTAIN WALL ASSEMBLY. NATURAL FINISH + [G2]
- W5 INTERIOR STEEL FRAME ASSEMBLY. GYP ON BOTH SIDES PAINTED WITH [P1]
- W6 8" CMU WALL UNFINISHED
- W7 PERFORATED METAL PANEL RAIN SCREEN CLAD 8" CMU EXTERIOR WALL WITH PAINTED GYP INTERIOR
- W8 METAL PANEL CLAD 8" CMU EXTERIOR WALL WITH [MP3] CLAD INTERIOR

FINISH LINE AUTO CLUB

17600 PERIMETER DR 100
SCOTTSDALE, AZ 85255

LGE | DESIGNBUILD


NUMBER	REVISION	DATE
--------	----------	------

UPDATE
PRICING SET
NOT TO BE USED
FOR CONSTRUCTION


SHEET TITLE:
PLAN - BUILDING C
ISSUE DATE: 03/25/25
DRAWN BY: AE
CHECKED BY: RH
PROJECT No.: 000000
SHEET:

A2.1D

LGE | DESIGNGROUP
1200 N. 52nd Street ■ Phoenix, AZ 85008
P. 480.966.4001

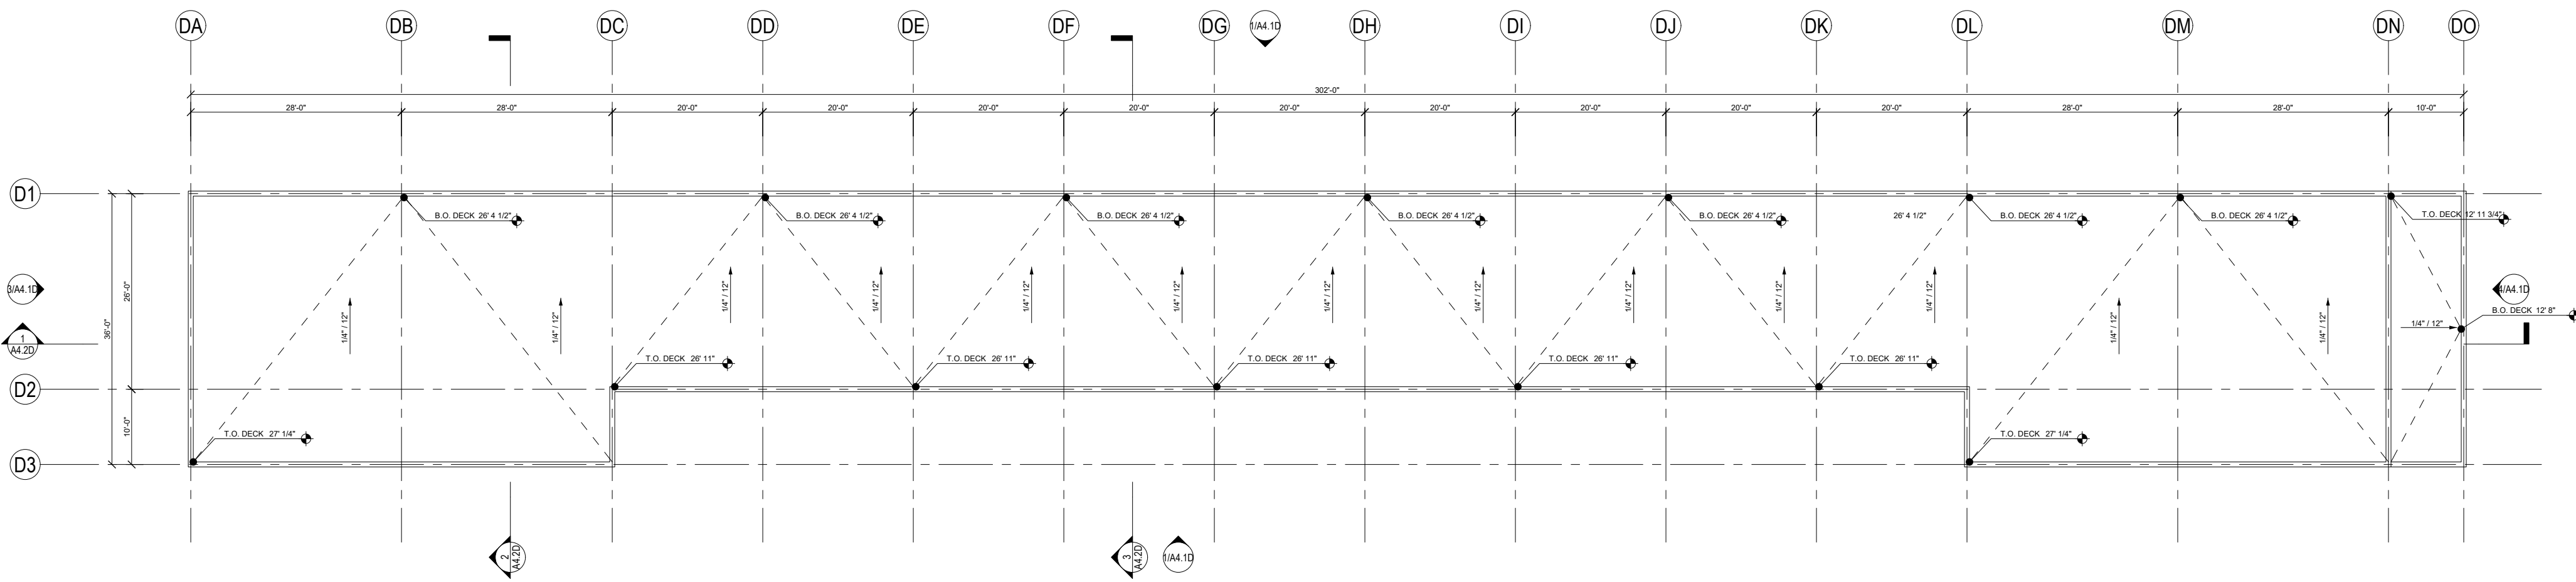

01 ROOF PLAN - BUILDING D
SCALE: 1/16" = 1'-0"

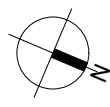

FINISH LINE AUTO CLUB

17600 PERIMETER DR 100
SCOTTSDALE, AZ 85255

LGE | DESIGNBUILD

NUMBER	REVISION	DATE
--------	----------	------


UPDATE
PRICING SET
NOT TO BE USED
FOR CONSTRUCTION

SHEET TITLE:
ROOF PLAN - BUILDING C
ISSUE DATE: 03/25/25
DRAWN BY: AE
CHECKED BY: RH
PROJECT No.: 000000
SHEET:

A3.1D


LGE | DESIGNGROUP

1200 N. 52nd Street ■ Phoenix, AZ ■ 85008
P: 480.966.4001

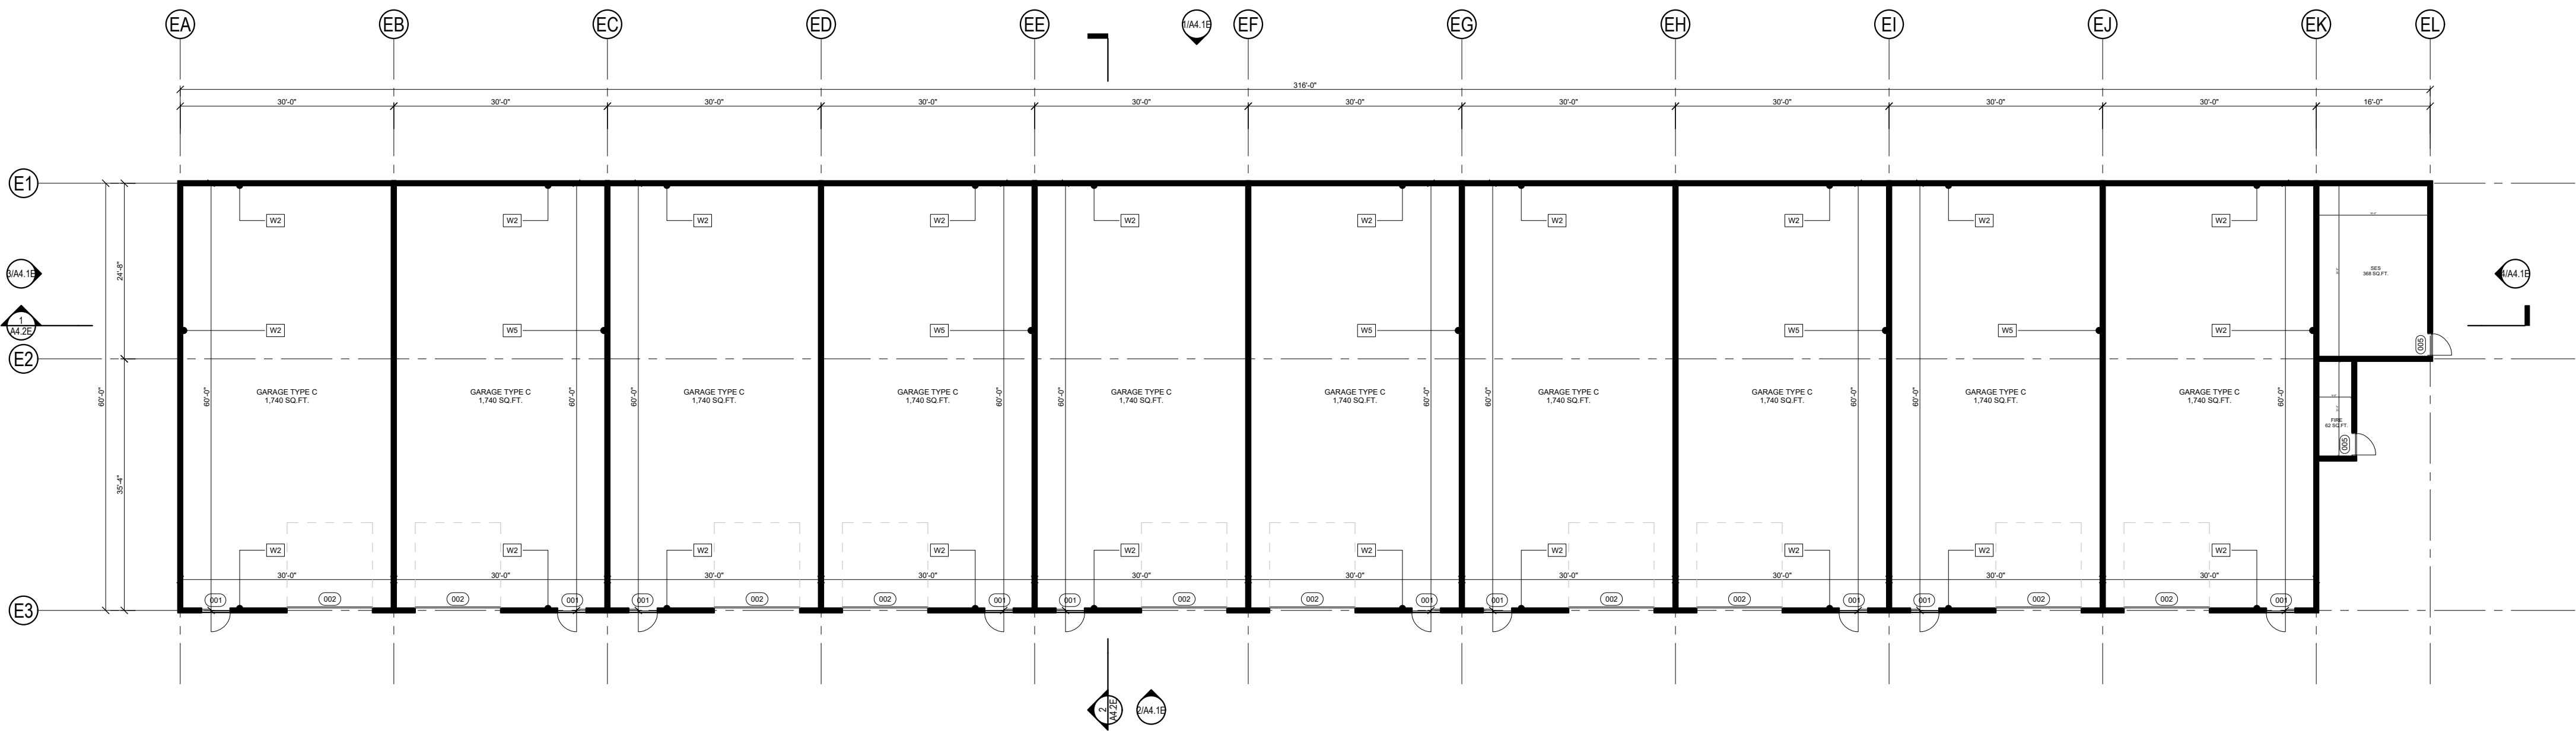

01

PLAN - BUILDING E
SCALE: 1/16" = 1'-0"

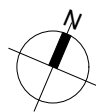

EXTERIOR WALLS

EXTERIOR WALL ASSEMBLY KEY:

- W1 METAL PANEL CLAD 8" CMU EXTERIOR WALL WITH [P1] PAINTED GYP INTERIOR
- W2 8" CMU EXTERIOR WALL WITH [P1] PAINTED GYP INTERIOR
- W3 EXTERIOR STEEL FRAME STOREFRONT. [P4] + [G1] FINISH.
- W4 GLASS CURTAIN WALL ASSEMBLY. NATURAL FINISH + [G2]
- W5 INTERIOR STEEL FRAME ASSEMBLY. GYP ON BOTH SIDES PAINTED WITH [P1]
- W6 8" CMU WALL UNFINISHED
- W7 PERFORATED METAL PANEL RAIN SCREEN CLAD 8" CMU EXTERIOR WALL WITH PAINTED GYP INTERIOR
- W8 METAL PANEL CLAD 8" CMU EXTERIOR WALL WITH [MP3] CLAD INTERIOR

FINISH LINE AUTO CLUB

17600 PERIMETER DR 100
SCOTTSDALE, AZ 85255

LGE | DESIGNBUILD

NUMBER	REVISION	DATE
--------	----------	------


UPDATE
PRICING SET
NOT TO BE USED
FOR CONSTRUCTION

SHEET TITLE:
PLAN - BUILDING B
ISSUE DATE: 03/25/25
DRAWN BY: AE
CHECKED BY: RH
PROJECT No.: 000000
SHEET:

A2.1E


LGE | DESIGNGROUP

1200 N. 52nd Street ■ Phoenix, AZ 85008
P. 480.966.4001

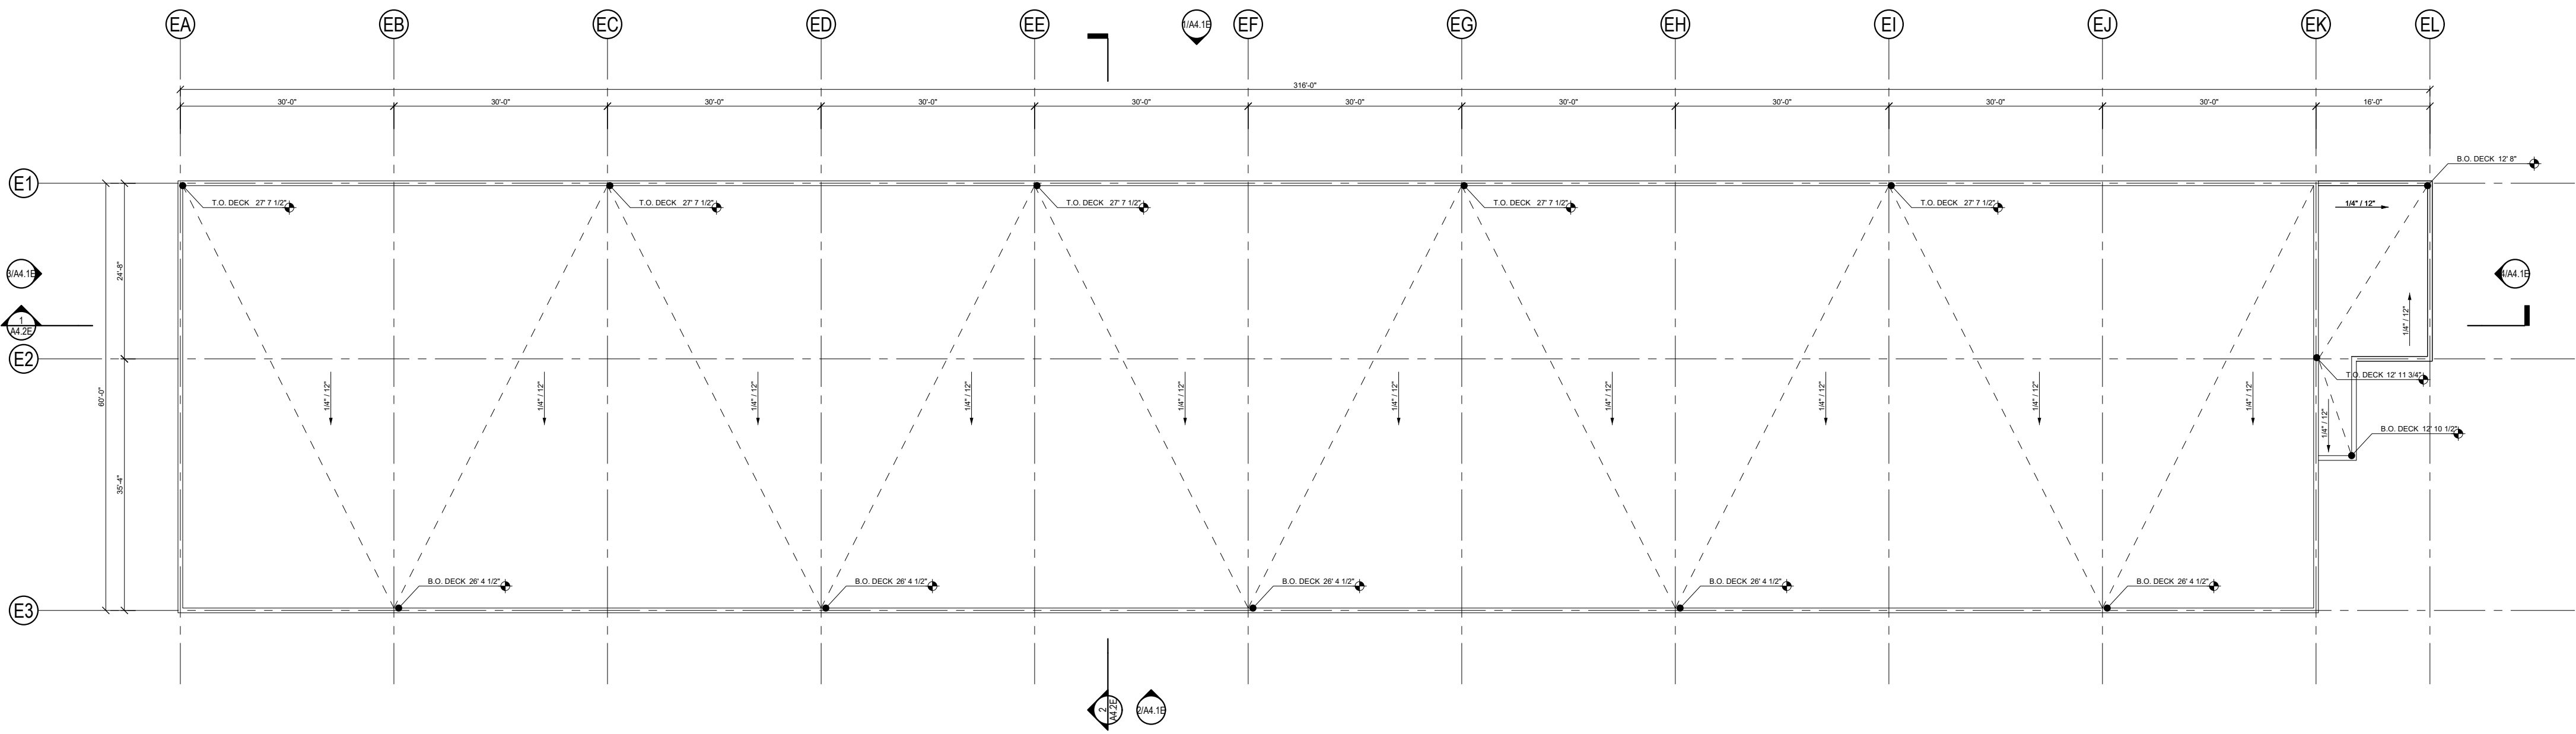

01

ROOF PLAN - BUILDING E
SCALE: 1/16" = 1'-0"

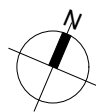

FINISH LINE AUTO CLUB

17600 PERIMETER DR 100
SCOTTSDALE, AZ 85255

LGE | DESIGNBUILD

NUMBER	REVISION	DATE
--------	----------	------

UPDATE

PRICING SET
NOT TO BE USED
FOR CONSTRUCTION

SHEET TITLE:
ROOF PLAN - BUILDING B
ISSUE DATE: 03/25/25
DRAWN BY: AE
CHECKED BY: RH
PROJECT No.: 000000
SHEET:

A3.1E

LGE | DESIGNGROUP

1200 N. 52nd Street ■ Phoenix, AZ 85008
P: 480.966.4001

CITY OF SCOTTSDALELANDSCAPE NOTES:

AN AUTOMATIC IRRIGATION SYSTEM WILL BE INSTALLED GUARANTEEING 100% COVERAGE TO ALL LANDSCAPE AREAS.

ALL LANDSCAPE AREAS WILL BE TOP-DRESSED WITH A 2" DEPTH OF DECOMPOSED GRANITE.

PROVIDE 8% SLOPE AWAY FROM WALK OR CURB FOR 5' ALONG ALL STREETS.

ALL RIGHT OF WAYS ADJACENT TO THIS PROPERTY SHALL BE LANDSCAPED AND MAINTAINED BY THE PROPERTY OWNER

ANY EXISTING LANDSCAPE MATERIALS INCLUDING TREES DAMAGED OR DESTROYED AS A RESULT OF THIS CONSTRUCTION SHALL BE REPLACED, TO THE SATISFACTION OF CITY STAFF, WITH LIKE KIND AND SIZE PRIOR TO RECEIVING A CERTIFICATE OF OCCUPANCY.

AREAS WITHIN THE SIGHT DISTANCE TRIANGLES IS TO BE CLEAR OF LANDSCAPING, SIGNS, OR OTHER VISIBILITY OBSTRUCTIONS WITH A HEIGHT GREATER THAN 1'-6". TREES WITHIN THE SAFETY TRIANGLE SHALL HAVE A CANOPY THAT BEGINS AT 8 FEET IN HEIGHT UPON INSTALLATION. ALL HEIGHTS ARE MEASURED FROM NEAREST STREET LINE ELEVATION.

ALL RIGHT-OF-WAY ADJACENT TO THIS PROPERTY SHALL BE LANDSCAPED AND MAINTAINED BY THE PROPERTY OWNER.

ALL SLOPES ON SITE ARE 4:1 MAX
NO TURF AREAS ARE TO BE PROVIDED.

SEE ARCHITECTURAL SITE PLAN FOR SETBACK DIMENSIONS.

SEE ARCHITECTURAL FOR SITE LIGHTING LOCATIONS. SEE ELECT. DRAWINGS FOR ALL LIGHTING SPECIFICATIONS.

SEE ARCHITECTURAL FOR SITE WALL ELEVATIONS, COLORS

SEE CIVIL DRAWINGS FOR ALL RETENTION AREAS, SECTIONS, AND SLOPE RATIOS.

SEE ARCHITECTURAL FOR BIKE RACK DETAILS.

ALL SIGNS REQUIRE SEPARATE APPROVALS & PERMITS.

"SETBACK ALL SPRAY & STREAM TYPE IRRIGATION HEADS 1'-0" FROM BACK OF CURB OR SIDEWALK TO REDUCE OVER SPRAY".

A MINIMUM 50 PERCENTAGE (UNLESS OTHERWISE STIPULATED BY THE DEVELOPMENT REVIEW BOARD, and/or THE ZONING ORDINANCE REQUIREMENTS) OF THE PROVIDED TREES SHALL BE MATURE TREES, PURSUANT TO THE CITY OF SCOTTSDALE'S ZONING ORDINANCE ARTICLE X, SECTION 10.301, AS DEFINED IN THE CITY OF SCOTTSDALE'S ZONING ORDINANCE ARTICLE III, SECTION 3.100.

A SINGLE TRUNK TREE'S CALIPER SIZE, THAT IS TO BE EQUAL TO OR LESS THAN 4-INCHES, SHALL BE DETERMINED BY UTILIZING THE SMALLEST DIAMETER OF THE TRUNK 6-INCHES ABOVE FINISHED GRADE ADJACENT TO THE TRUNK.

A TREE CALIPER SIZE, FOR SINGLE TRUNK TREES WHICH HAVE A DIAMETER GREATER THAN 4-INCHES, SHALL BE DETERMINED BY UTILIZING THE SMALLEST DIAMETER OF THE TRUNK 12-INCHES ABOVE FINISHED GRADE ADJACENT TO THE TRUNK.

A MULTI TRUNK TREE'S CALIPER SIZE IS MEASURED AT 6-INCHES ABOVE THE LOCATION THAT THE TRUNK SPLITS ORIGINATES, OR 6-INCHES ABOVE FINISHED GRADE OF ALL TRUNKS ORIGINATE FROM THE SOIL.

RETENTION/DETENSION BASINS SHALL BE CONSTRUCTED SOLELY FROM THE APPROVED CIVIL PLANS. ANY ALTERATION OF THE APPROVED DESIGN (ADDITIONAL FILL, BOULDERS, ECT.) SHALL REQUIRE ADDITIONAL FINAL PLANS STAFF REVIEW AND APPROVAL.

NO LIGHTING IS APPROVED WITH THE SUBMITTAL

THE LANDSCAPE SPECIFICATION SECTION(S) OF THESE PLANS HAVE NOT REVIEWED AND SHALL NOT BE A PART OF THE CITY OF SCOTTSDALE'S APPROVAL.

NEW LANDSCAPING, INCLUDING SALVAGED PLANT MATERIAL, AND LANDSCAPING INDICATED TO REMAIN, WHICH IS DESTROYED, DAMAGED, OR EXPIRES DURING CONSTRUCTION SHALL BE REPLACED WITH LIKE SIZE, KIND, AND QUALITY PRIOR TO THE ISSUANCE OF THE CERTIFICATE OF OCCUPANCY / LETTER OF ACCEPTANCE TO THE SATISFACTION OF THE INSPECTION SERVICES STAFF.

THORNY TREES, SHRUBS, AND CACTI SHALL BE PLANTED SO THAT THEIR MATURE SIZE/CANOPY WILL BE AT LEAST 4 FEET AWAY FROM ANY WALKWAYS OR PARKING AREA CURBING. PLEASE REFER TO DSPM SEC. 2-1.501.L.

T.J. McQUEEN & ASSOCIATES, INC.
LANDSCAPE ARCHITECTURE
URBAN DESIGN
SITE PLANNING
27166
TIMOTHY J. McQUEEN
08.15.25
10446 N. 74th Street, Suite 150
Scottsdale, Arizona 85258
P.(602)265-0320
EMAIL: timmcqueen@tjma.net

T.J. McQUEEN & ASSOCIATES, INC. LANDSCAPE ARCHITECTURE (TJMA) EXPRESSLY RESERVES ITS COMMON LAW COPYRIGHT & ALL OTHER RIGHTS IN THESE PLANS AND THESE PLANS AND ANY INSTRUMENTS THEREOF SHALL BE REPRODUCED, COPIED, OR COPIED IN ANY FORM OR MANNER WITHOUT WRITTEN PERMISSION FROM T.J. McQUEEN & ASSOCIATES, INC. ANY REPRODUCTION OR COPIING WITHOUT THE WRITTEN PERMISSION OF T.J. McQUEEN & ASSOCIATES, INC. IS PROHIBITED.

LANDSCAPE LEGEND

- CERCIDIUM FLORIDUM
BLUE PALO VERDE
36" BOX 2" CALIP., 6.5T, 4.5W (34)
- PROSOPIS 'RIO-SALADO'
HYBRID THORLESS MESQUITE
24" BOX 1.5" CALIP., 6T, 3.5W (13)
- OLNEYA TESOTA
IRONWOOD
36" BOX 2" CALIP., 7T, 4W (20)
- CAESALPINIA CACALACO
CASCALOTE
24" BOX 1.5" CALIP.(MULTI) 4T, 3.5W (66)
- AGAVE DESMETTIANA
SMOOTH AGAVE
5 GALLON (90)
- EXISTING SHRUB TO
REMAIN IN PLACE
PROTECT FROM CONSTRUCTION (105)
- PACHYCREUS MARGINATUS
MEXICAN FENCE POST
3-STALK GROUPING (2.5', 2', 1' TALL) (18)
- EREMOPHILA MACULATA
VALENTINE EMU BUSH
5 GALLON (347)
- ECHINOCACTUS GRISONII
GOLDEN BARREL CACTUS
10" ROUND (MATCHING) (60)
- LEUCOPHYLLUM FRUTESCENS
'GREEN CLOUD'
5 GALLON (134)
- TECOMA 'ORANGE JUBILEE'
ORANGE JUBILEE
5 GALLON (82)
- EREMOPHILA GLABRA
'MINGENW GOLD'
5 GALLON (72)
- LANTANA MONTEVIDENSIS
'GOLD MOUND'
1 GALLON (157)
- LANTANA MONTEVIDENSIS
TRAILING PURPLE
1 GALLON (198)
- HESPERALOE PARVIFLORA
RED YUCCA
5 GALLON (105)
- CAESALPINIA MEXICANA
MEXICAN BIRD OF PARADISE
5 GALLON (63)

1/2" SCREENED ROCK PROS MAHOGANY
DECOMPOSED GRANITE
2" DEPTH IN ALL LANDSCAPE AREAS

LANDSCAPE DATA:

NORTH PROPERTY LINE: 670'
TREES REQUIRED: 22 TREES
TREES PROVIDED: 33 TREES

WEST PROPERTY LINE: 510'
TREES REQUIRED: 17 TREES
TREES PROVIDED: 28 TREES

EAST PROPERTY LINE: 782'
TREES REQUIRED: 26 TREES
TREES PROVIDED: 34 TREES

SOUTH PROPERTY LINE: 955'
TREES REQUIRED: 32 TREES
TREES PROVIDED: 33 TREES


SITE AREA +/- 452,911 SQ.FT.
LANDSCAPE AREA REQUIRED: 67,936 SQ.FT. (15%)
LANDSCAPE AREA PROVIDED: 109,274 SQ.FT.(24%)

PARKING AREA +/- 50,434 SQ.FT.
LANDSCAPE AREA REQUIRED: 7,565 SQ.FT. (15%)
LANDSCAPE AREA PROVIDED: 8,988 SQ.FT.(17%)

178 PARKING STALLS:
TREES REQUIRED: 9 TREES
TREES PROVIDED: 41 TREES

NATIVE PLANT INVENTORY:

A NATIVE PLANT INVENTORY HAS BEEN PROVIDED
PER CITY OF SCOTTSDALE CRITERIA.
PER CITY OF SCOTTSDALE CRITERIA.

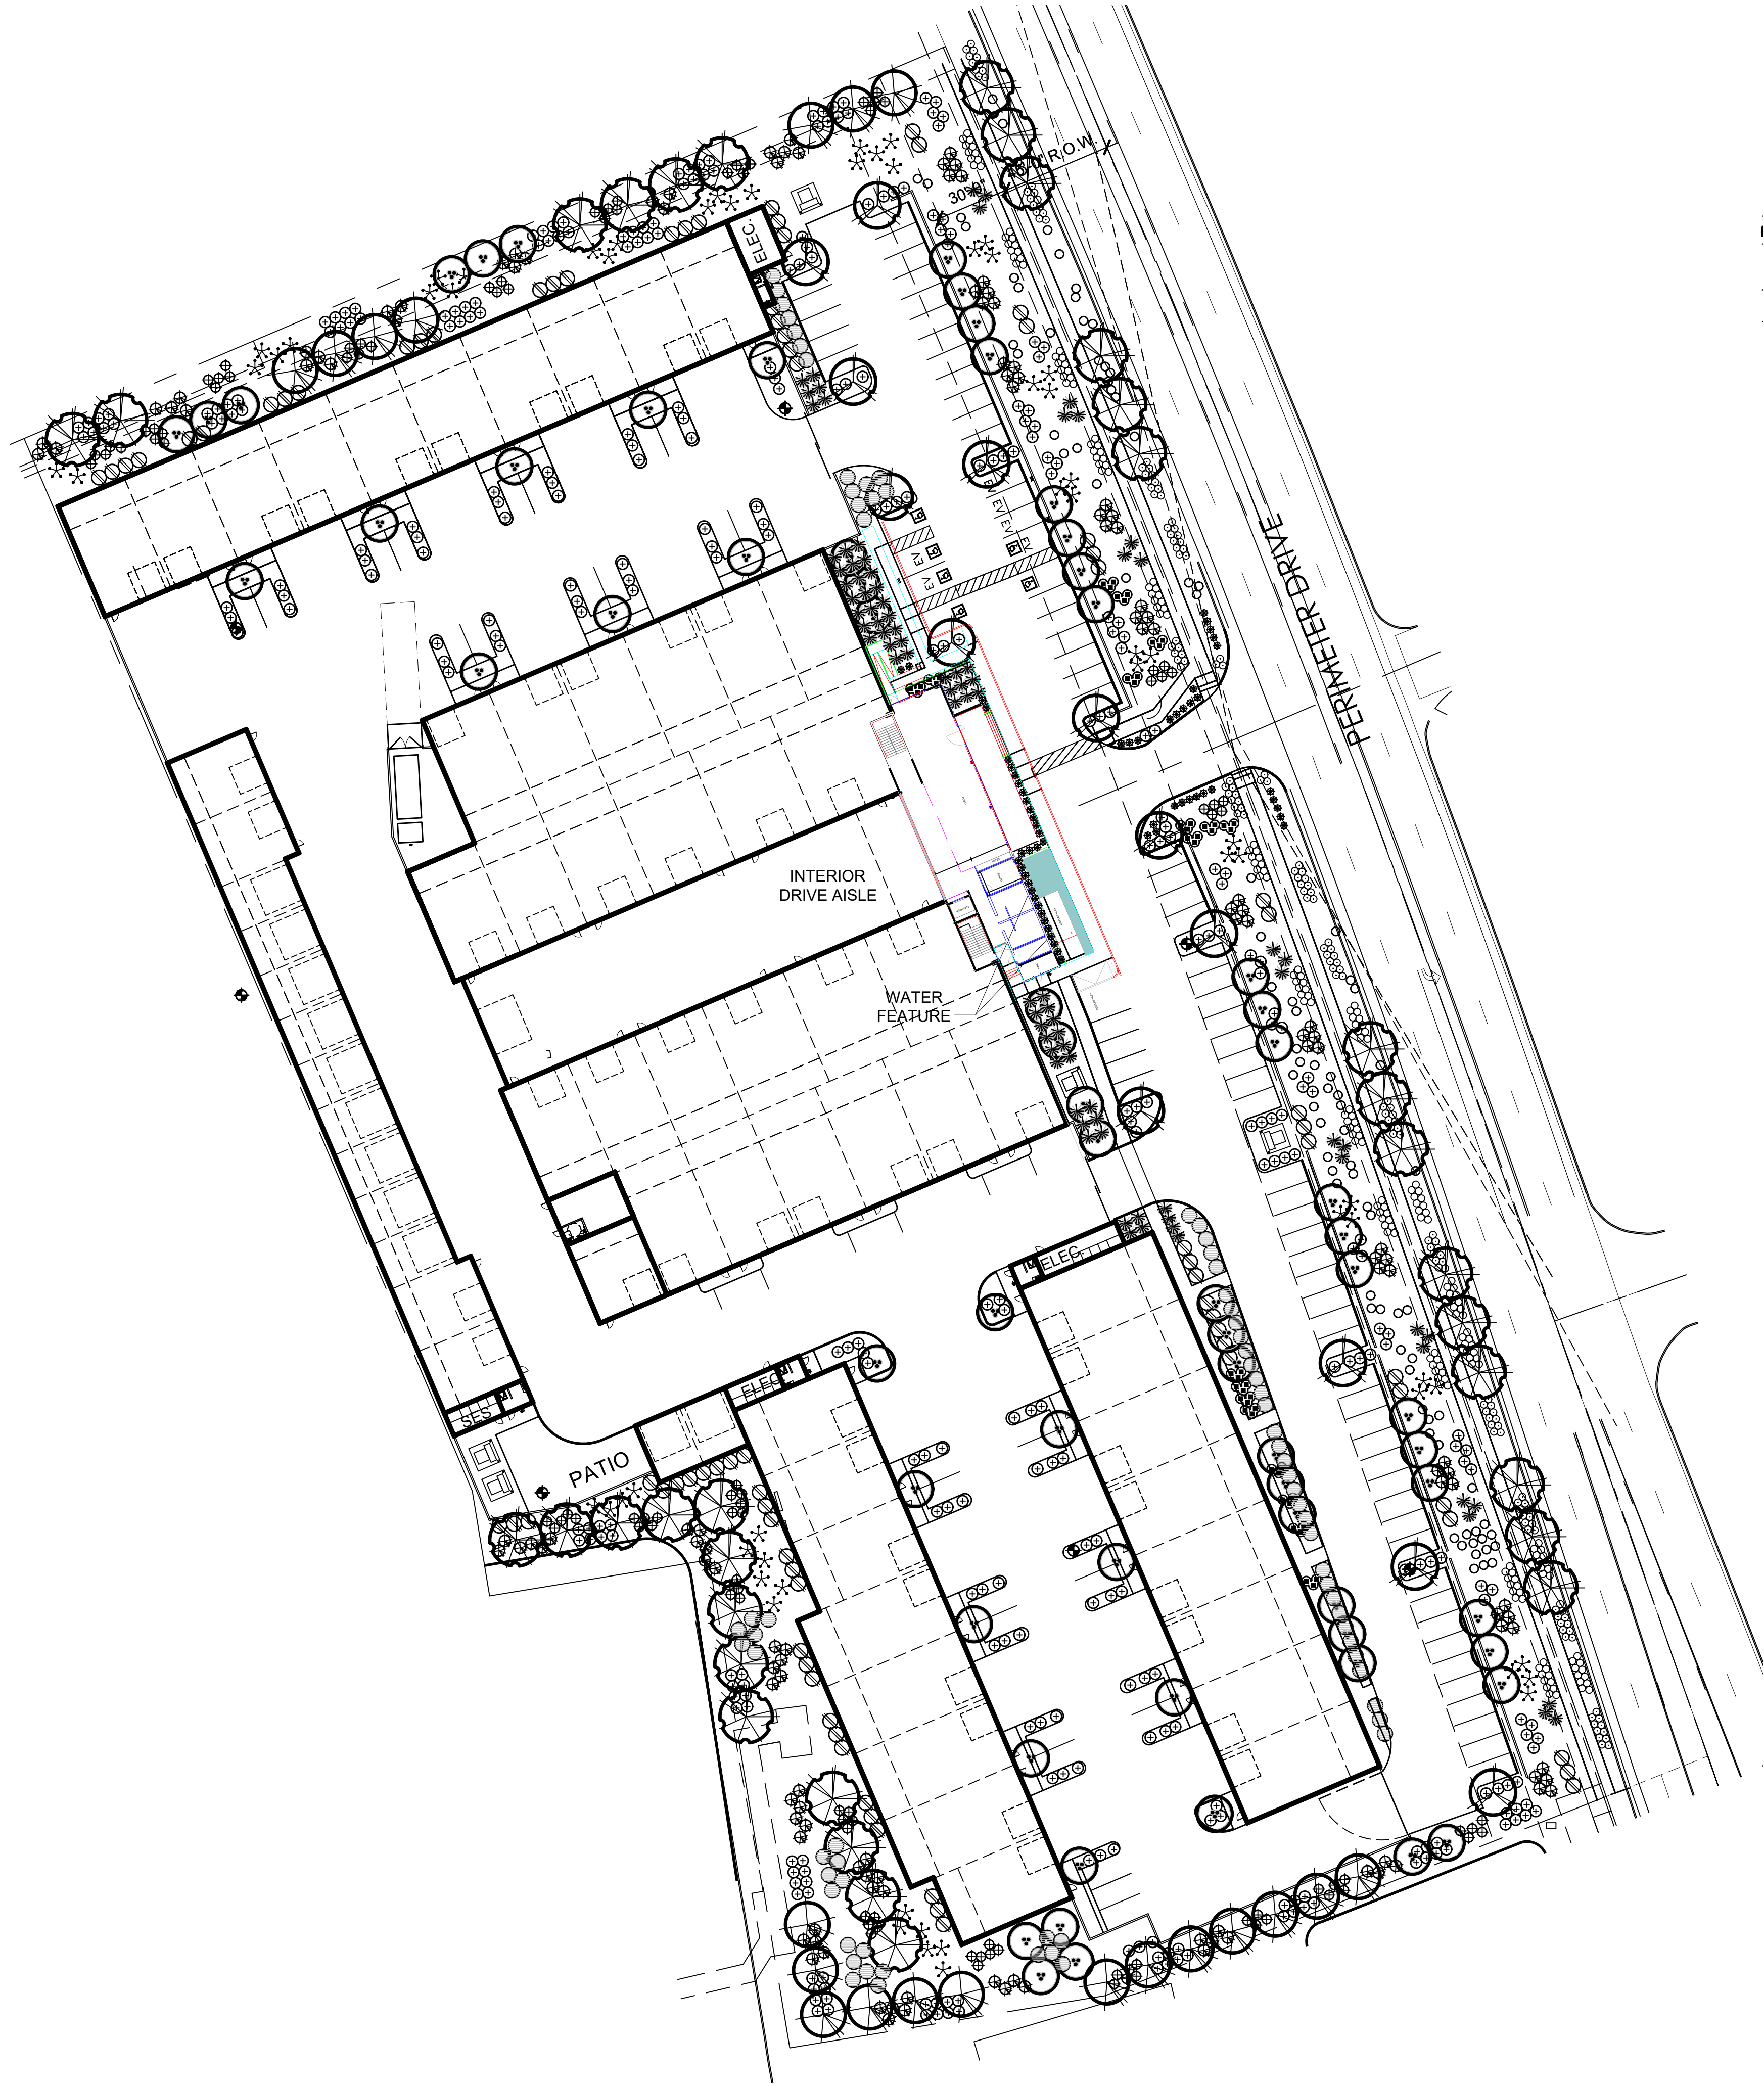




AREA CALCULATIONS	
AUTO CLUB - EAST LOT	
PROJECT DATA ZONING:	I-1 PCD
NET LOT AREA:	+/- 293,754 S.F.
BUILDING HEIGHT:	48'
F.A.R.	= MAX. 0.8 x (NET FLOOR AREA)
REQUIRED OPEN SPACE:	
TOTAL OPEN SPACE	
MAX. BUILDING HEIGHT	= 48' PROPOSED (52' ALLOWED)
FIRST 12' OF HEIGHT	= 10% x NET LOT AREA = .10 x 293,754 S.F. = 29,375 S.F.
NEXT 36' OF HEIGHT	= 0.004 x (NET LOT AREA) x 1' ADD. = 0.003 x (293,754) x 36' = 31,725 S.F.
OPEN SPACE REQUIRED: (NOT INCLUDING PARKING LOT LANDSCAPING)	= 29,375 + 31,725 = 61,100 S.F.
OPEN SPACE PROVIDED: (NOT INCLUDING PARKING LOT LANDSCAPING)	= 61,100 S.F.
REQ'D PARKING LANDSCAPING (NOT INCLUDING IN OPEN SPACE) 0.15' * 57,857 S.F.	= 8,678 S.F.
PROVIDED PARKING LOT LANDSCAPING (NOT INCLUDING IN OPEN SPACE)	= 8,680 S.F.


GRAPHIC LEGEND	
SYMBOL:	DESCRIPTION:
	DENOTES FRONT OPEN SPACE 23,490 S.F.
	DENOTES OTHER OPEN SPACE 48,274 S.F.
	DENOTES PARKING LOT LANDSCAPING 8,680 S.F.

1 OPEN SPACE PLAN Copy 1
1" = 50'-0"

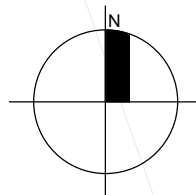




VIEW AT ROAD

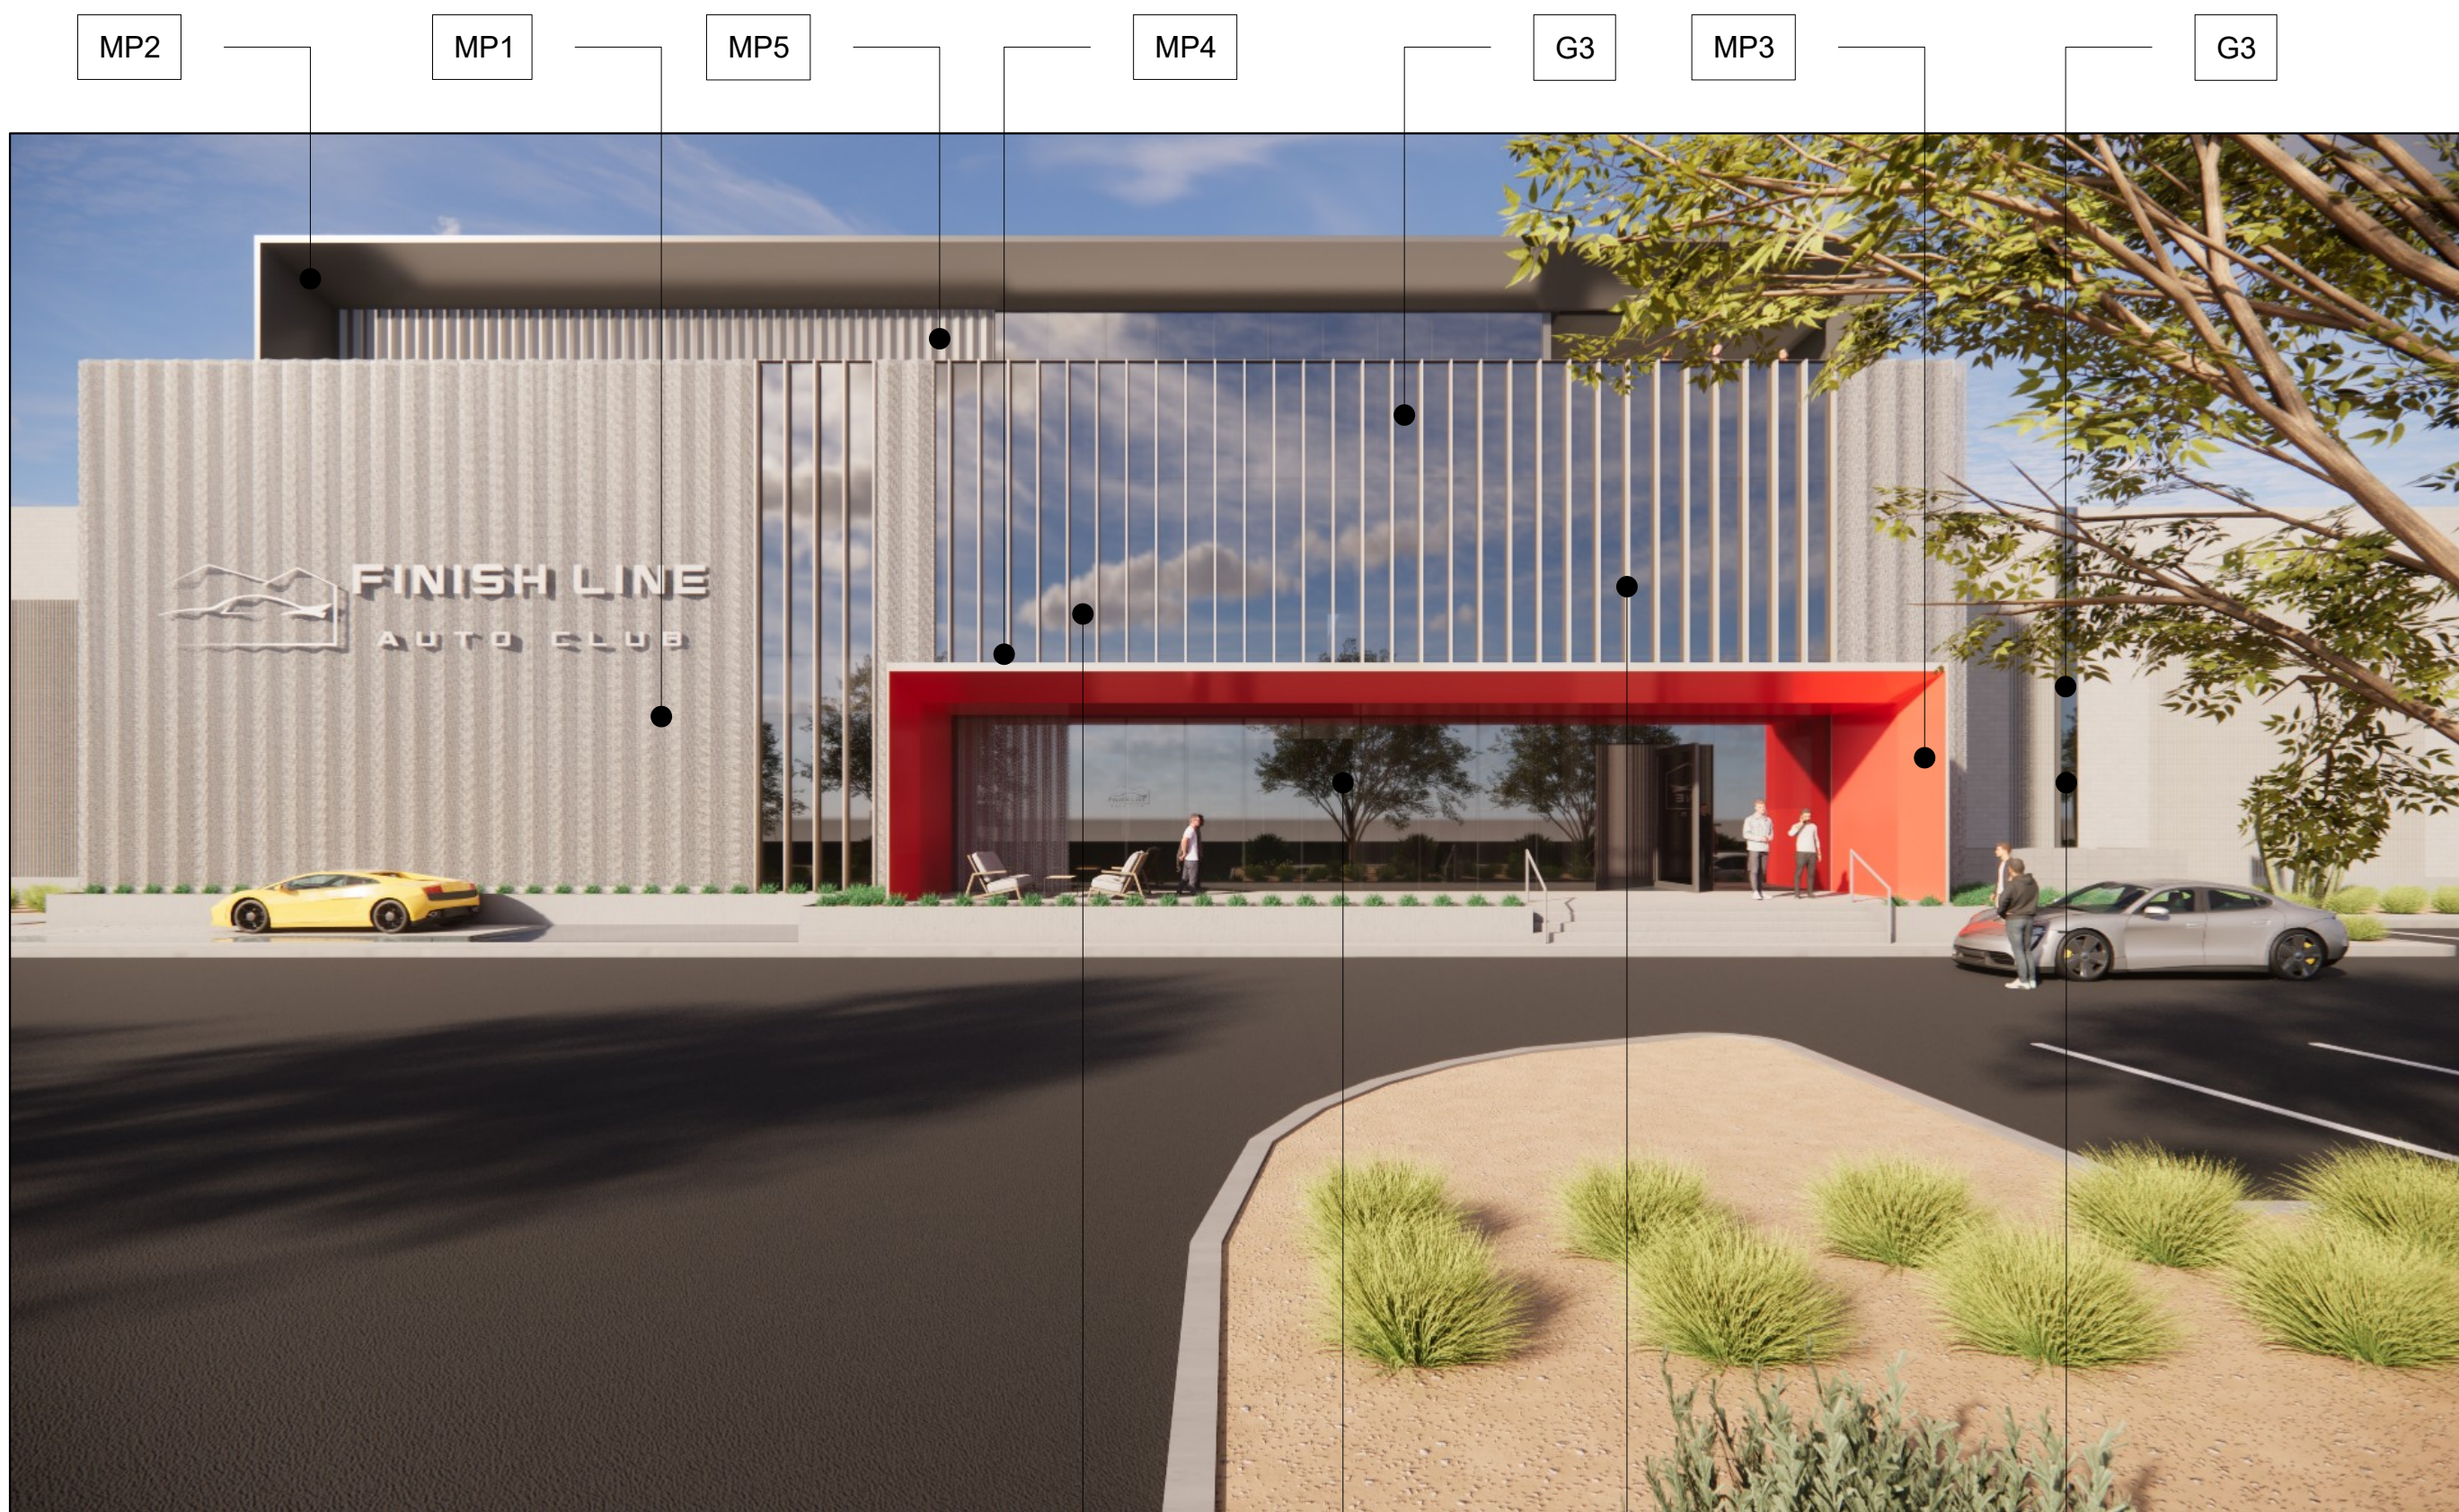

VIEW AT BUILDING ENTRY

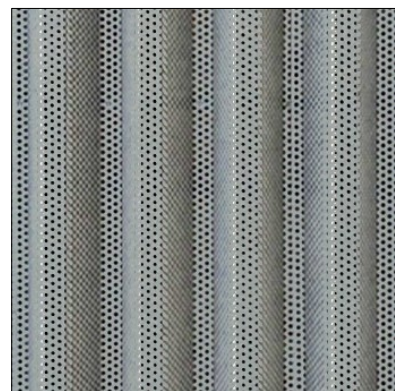

MP1



MP4



CMU2




P1



P4




MP2

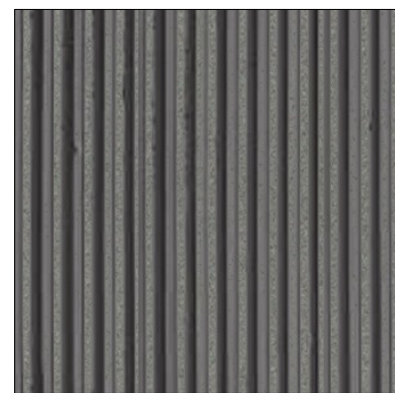

MP5



CMU3

 

P2



P5




MP3



CMU1



CMU4

 

P3

DOORS

DOOR KEY:

- 0013'x10" ALUMINUM STOREFRONT DOOR (GARAGE ENTRANCES). [P4] FINISH.
- 00212'X12' ALUMINUM GARAGE DOOR (INDIVIDUAL GARAGE UNITS). [P4] FINISH.
- 0038'X10' GLAZED ALUMINUM PIVOT DOOR. NATURAL FINISH.
- 00420'X12' ALUMINUM DRIVE AISLE GARAGE DOOR. [P4] FINISH.
- 00530" X 70" EXTERIOR STEEL DOOR. [P4] FINISH.
- 0063'X10' INTERIOR DOOR. [P1] FINISH.

EXTERIOR WALLS

EXTERIOR WALL ASSEMBLY KEY:

- W1METAL PANEL CLAD 8" CMU EXTERIOR WALL WITH [P1] PAINTED GYP INTERIOR
- W28" CMU EXTERIOR WALL WITH [P1] PAINTED GYP INTERIOR
- W3EXTERIOR STEEL FRAME STOREFRONT. [P4]+ [G1] FINISH.
- W4GLASS CURTAIN WALL ASSEMBLY. NATURAL FINISH + [G2]
- W5INTERIOR STEEL FRAME ASSEMBLY. GYP ON BOTH SIDES PAINTED WITH [P1]
- W68" CMU WALL UNFINISHED
- W7PERFORATED METAL PANEL RAIN SCREEN CLAD 8" CMU EXTERIOR WALL WITH PAINTED GYP INTERIOR
- W8METAL PANEL CLAD 8" CMU EXTERIOR WALL WITH [MP3] CLAD INTERIOR

EXTERIOR MATERIAL KEY

- MP1LIGHT GREY PERFORATED AND CORRUGATED METAL PANEL. MI-2810 WHITE SILVER, VISAGE
- MP2DARK METAL PANEL - MI-2011 DARK GREY: COLOR, VISAGE BY LUMABUILT
- MP3RED METAL PANEL (INNER ENTRY CANOPY). SL-1852 CARDINAL RED, VISAGE BY LUMABUILT
- MP4LIGHT GREY METAL PANEL (OUTER ENTRY CANOPY). MI-2810 WHITE SILVER, VISAGE BY LUMABUILT
- MP5DARK CORRUGATED METAL PANEL - MI-2011 DARK GREY: COLOR, VISAGE BY LUMABUILT

- CMU18"X8"x16" CMU SMOOTH FACE STACK BOND INTEGRAL COLOR MASONRY COLOR: "BLACK CANYON" BY SUPERLITE
- CMU28"X8"x16" CMU SMOOTH FACE STACK BOND INTEGRAL COLOR MASONRY COLOR: "PEBBLE BEACH" BY SUPERLITE
- CMU38"X8"x16" CMU SMOOTH FACE STACK BOND INTEGRAL COLOR MASONRY COLOR: "MALIBU SAND" BY SUPERLITE
- CMU48"X8"x16" CMU SCORED SPLIT FACE STACK BOND INTEGRAL COLOR MASONRY COLOR: "BLACK CANYON" BY SUPERLITE

PAINT

PAINT KEY:
DUN EDWARDS COLD MORNING DE6365

- P2DUNN EDWARDS COVERED IN PLATINUM DE6367
- P3DUNN EDWARDS DARK GRAY DEGR60
- P4DUN EDWARDS BLACK DEA002
- P5DUNN EDWARDS RED POWER DEA108

MISC. ARCHITECTURAL ELEMENTS

- FN1VERTICAL LOUVERS ANODIZED ALUMINUM FINS, 1.5" WIDE X 8" DEEP
- FN2VERTICAL LOUVERS ANODIZED BLACK ([P4]) ALUMINUM FINS 1.5" WIDE X 8" DEEP

GLAZING


GLAZING KEY:

- MATERIAL: 2"X6", 2"X4-1/2" ALUMINUM STOREFRONT
- G1ALUMINUM STOREFRONT GLASS. SOLARBAN 90, 1" INSULATED GLAZING LOW-E STARPHIRE+STARPHIRE
- G2GLASS CURTAIN WALL. SOLARBAN 90, 1" INSULATED GLAZING LOW-E STARPHIRE+STARPHIRE
- G3SPANDREL GLASS. SOLARBAN 90, 1" INSULATED GLAZING LOW-E STARPHIRE+STARPHIRE


NOTE: ALL GLAZING TO COMPLY WITH IBC 2406.



VIEW AT ROAD

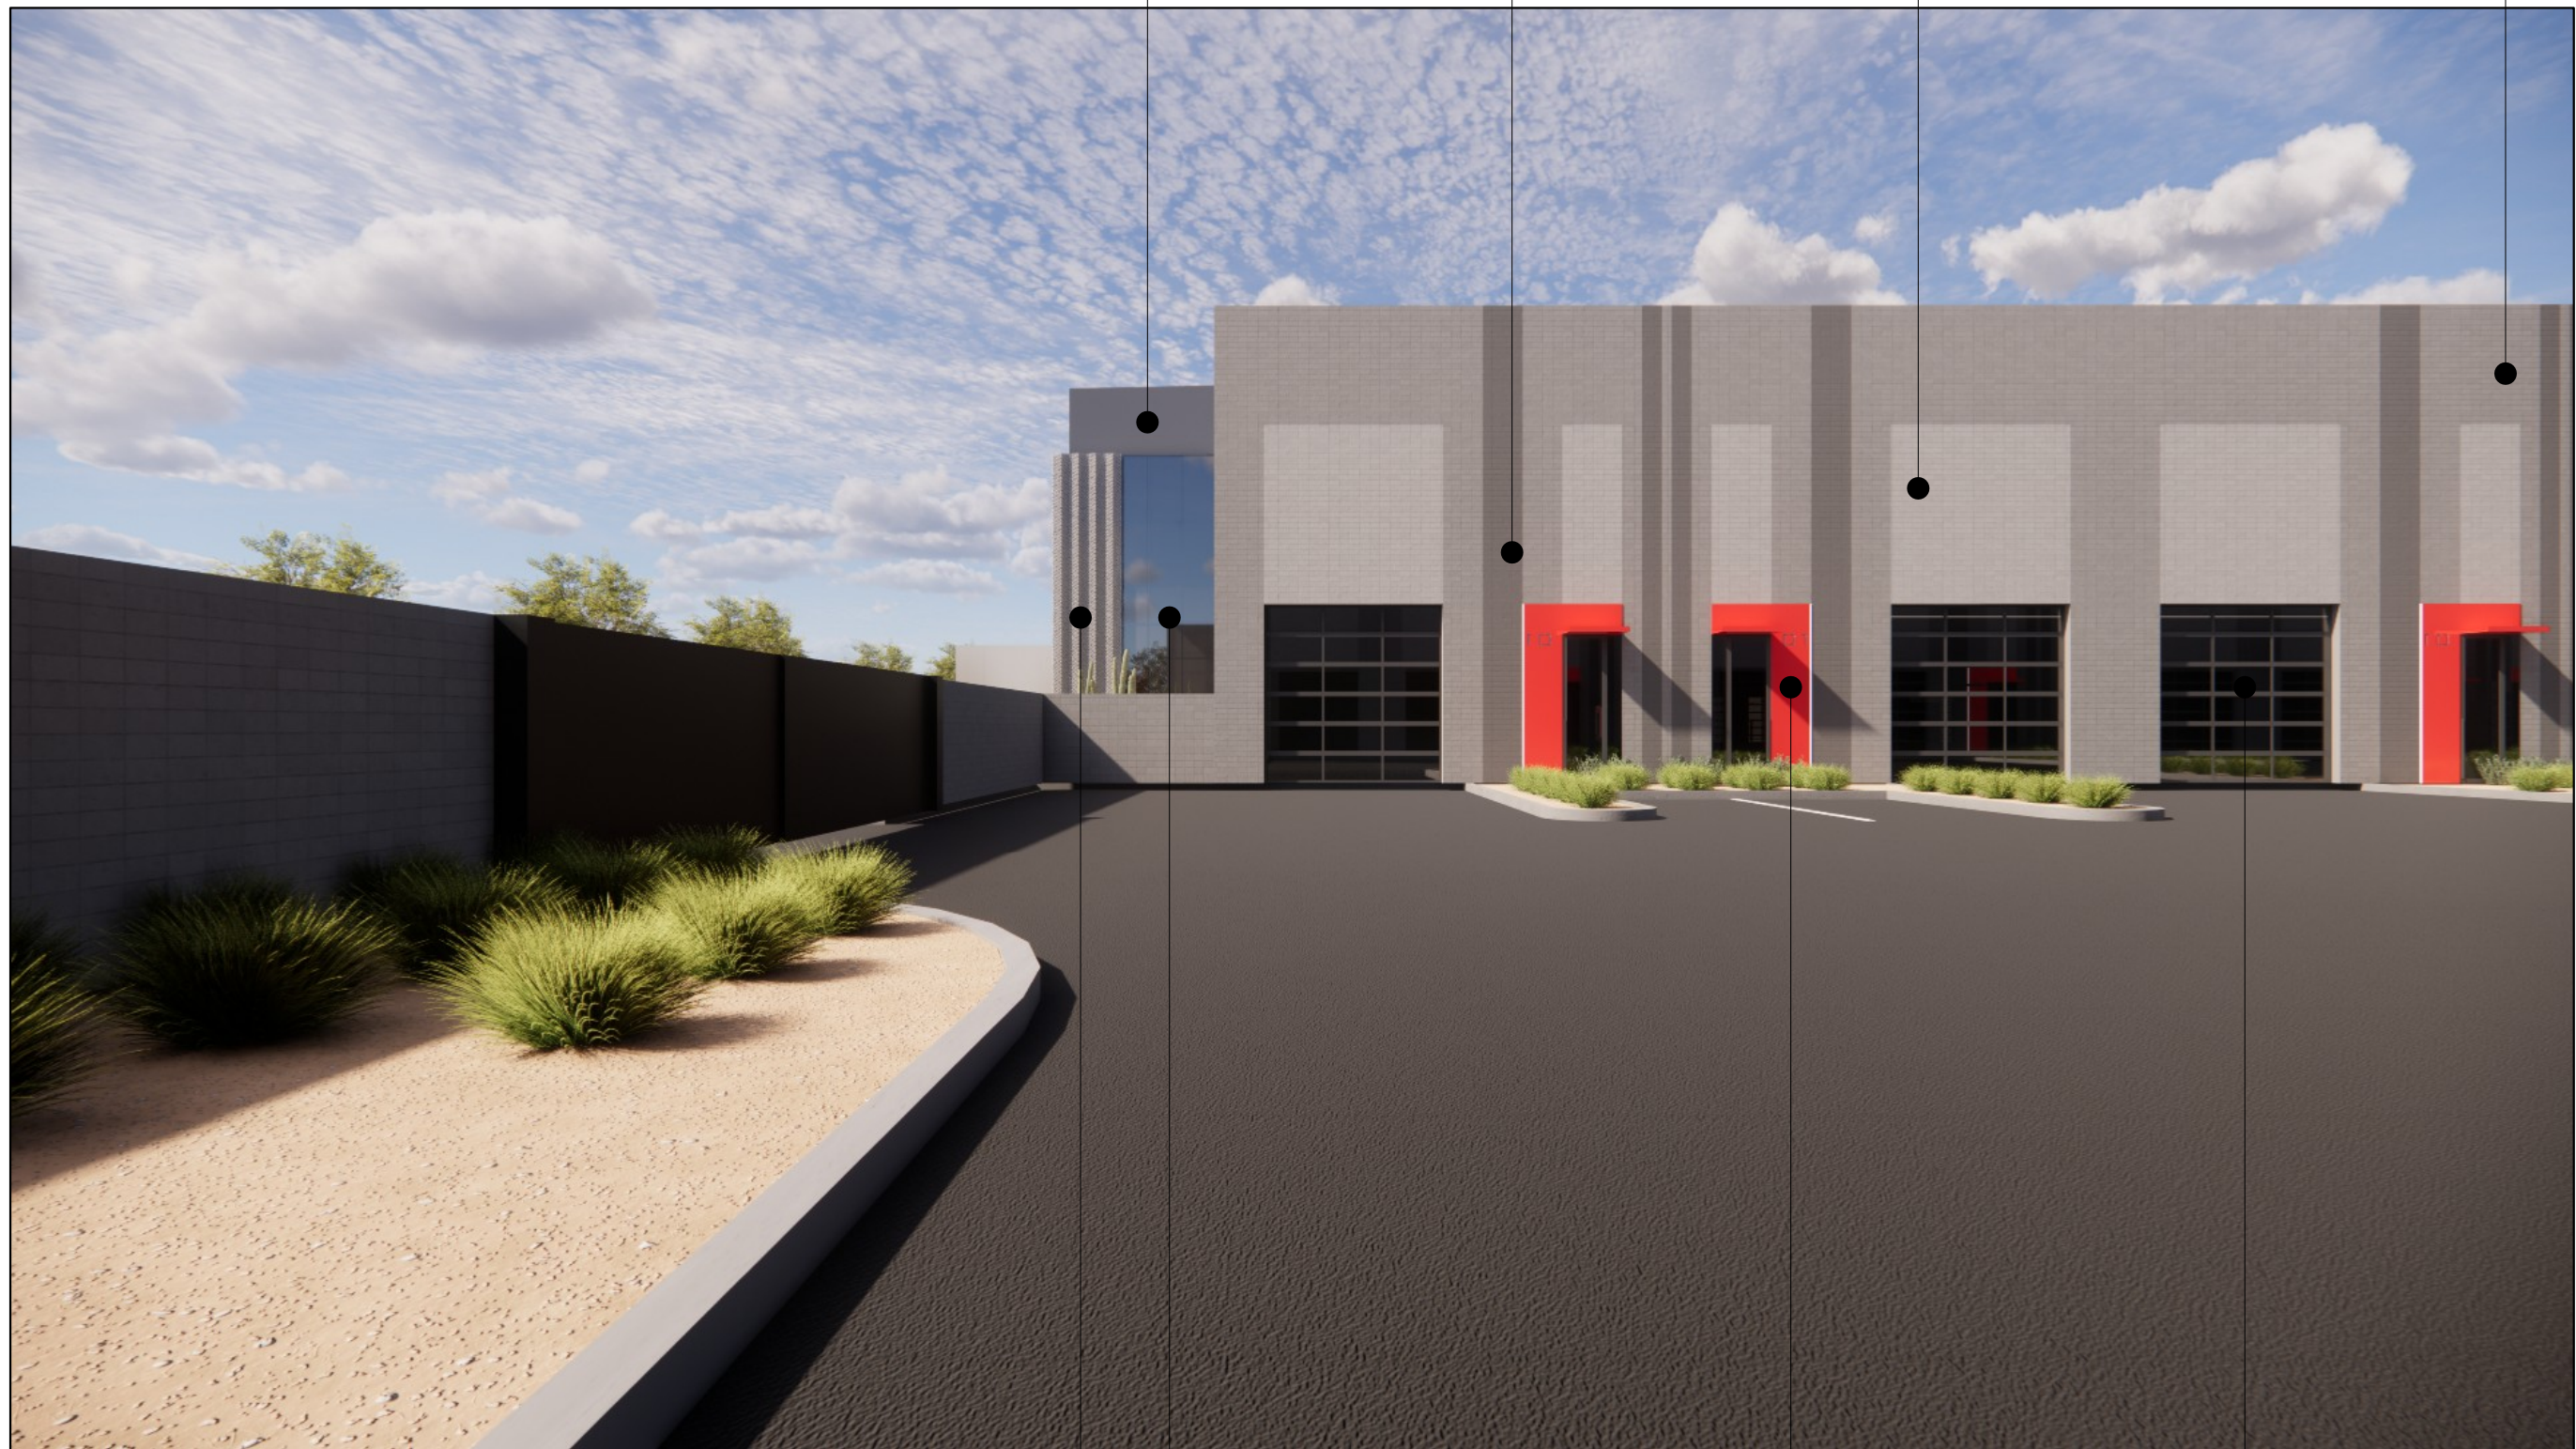

VIEW AT BUILDING ENTRY

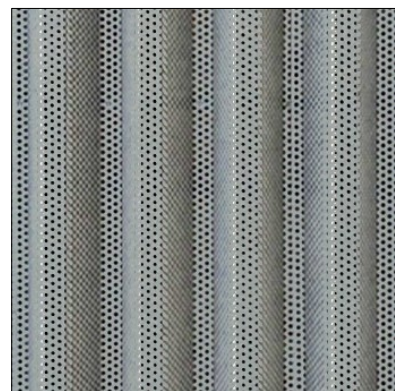

MP1




MP2



MP3



MP4

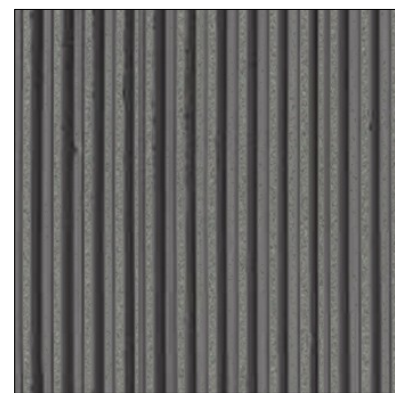

MP5



CMU1



CMU2




CMU3




CMU4



P1

 

P2

 

P3



P4



P5

DOORS

DOOR KEY:

- 001 3"x10" ALUMINUM STOREFRONT DOOR (GARAGE ENTRANCES). [P4] FINISH.
- 002 12'X12' ALUMINUM GARAGE DOOR (INDIVIDUAL GARAGE UNITS). [P4] FINISH.
- 003 8'X10' GLAZED ALUMINUM PIVOT DOOR. NATURAL FINISH.
- 004 20'X12' ALUMINUM DRIVE AISLE GARAGE DOOR. [P4] FINISH.
- 005 30" X 70" EXTERIOR STEEL DOOR. [P4] FINISH.
- 006 3'X10' INTERIOR DOOR. [P1] FINISH.

EXTERIOR WALLS

EXTERIOR WALL ASSEMBLY KEY:

- W1 METAL PANEL CLAD 8" CMU EXTERIOR WALL WITH [P1] PAINTED GYP INTERIOR
- W2 8" CMU EXTERIOR WALL WITH [P1] PAINTED GYP INTERIOR
- W3 EXTERIOR STEEL FRAME STOREFRONT. [P4]+ [G1] FINISH.
- W4 GLASS CURTAIN WALL ASSEMBLY. NATURAL FINISH + [G2]
- W5 INTERIOR STEEL FRAME ASSEMBLY. GYP ON BOTH SIDES PAINTED WITH [P1]
- W6 8" CMU WALL UNFINISHED
- W7 PERFORATED METAL PANEL RAIN SCREEN CLAD 8" CMU EXTERIOR WALL WITH PAINTED GYP INTERIOR
- W8 METAL PANEL CLAD 8" CMU EXTERIOR WALL WITH [MP3] CLAD INTERIOR

EXTERIOR MATERIAL KEY

- MP1 LIGHT GREY PERFORATED AND CORRUGATED METAL PANEL. MI-2810 WHITE SILVER, VISAGE
- MP2 DARK METAL PANEL - MI-2011 DARK GREY: COLOR, VISAGE BY LUMABUILT
- MP3 RED METAL PANEL (INNER ENTRY CANOPY). SL-1852 CARDINAL RED, VISAGE BY LUMABUILT
- MP4 LIGHT GREY METAL PANEL (OUTER ENTRY CANOPY). MI-2810 WHITE SILVER, VISAGE BY LUMABUILT
- MP5 DARK CORRUGATED METAL PANEL - MI-2011 DARK GREY: COLOR, VISAGE BY LUMABUILT

- CMU1 8"X8"x16" CMU SMOOTH FACE STACK BOND INTEGRAL COLOR MASONRY COLOR: "BLACK CANYON" BY SUPERLITE
- CMU2 8"X8"x16" CMU SMOOTH FACE STACK BOND INTEGRAL COLOR MASONRY COLOR: "PEBBLE BEACH" BY SUPERLITE
- CMU3 8"X8"x16" CMU SMOOTH FACE STACK BOND INTEGRAL COLOR MASONRY COLOR: "MALIBU SAND" BY SUPERLITE
- CMU4 8"X8"x16" CMU SCORED SPLIT FACE STACK BOND INTEGRAL COLOR MASONRY COLOR: "BLACK CANYON" BY SUPERLITE

PAINT

PAINT KEY:

- P1 DUN EDWARDS COLD MORNING DE6365
- P2 DUNN EDWARDS COVERED IN PLATINUM DE6367
- P3 DUNN EDWARDS DARK GRAY DEGR60
- P4 DUN EDWARDS BLACK DEA002
- P5 DUNN EDWARDS RED POWER DEA108

MISC. ARCHITECTURAL ELEMENTS

- FN1 VERTICAL LOUVERS ANODIZED ALUMINUM FINS, 1.5" WIDE X 8" DEEP
- FN2 VERTICAL LOUVERS ANODIZED BLACK ([P4]) ALUMINUM FINS 1.5" WIDE X 8" DEEP

GLAZING

GLAZING KEY:

- MATERIAL: FRAMES
- G1 ALUMINUM STOREFRONT GLASS. SOLARBAN 90, 1" INSULATED GLAZING LOW-E STARPHIRE+STARPHIRE
 - G2 GLASS CURTAIN WALL. SOLARBAN 90, 1" INSULATED GLAZING LOW-E STARPHIRE+STARPHIRE
 - G3 SPANDREL GLASS. SOLARBAN 90, 1" INSULATED GLAZING LOW-E STARPHIRE+STARPHIRE

NOTE: ALL GLAZING TO COMPLY WITH IBC 2406.