


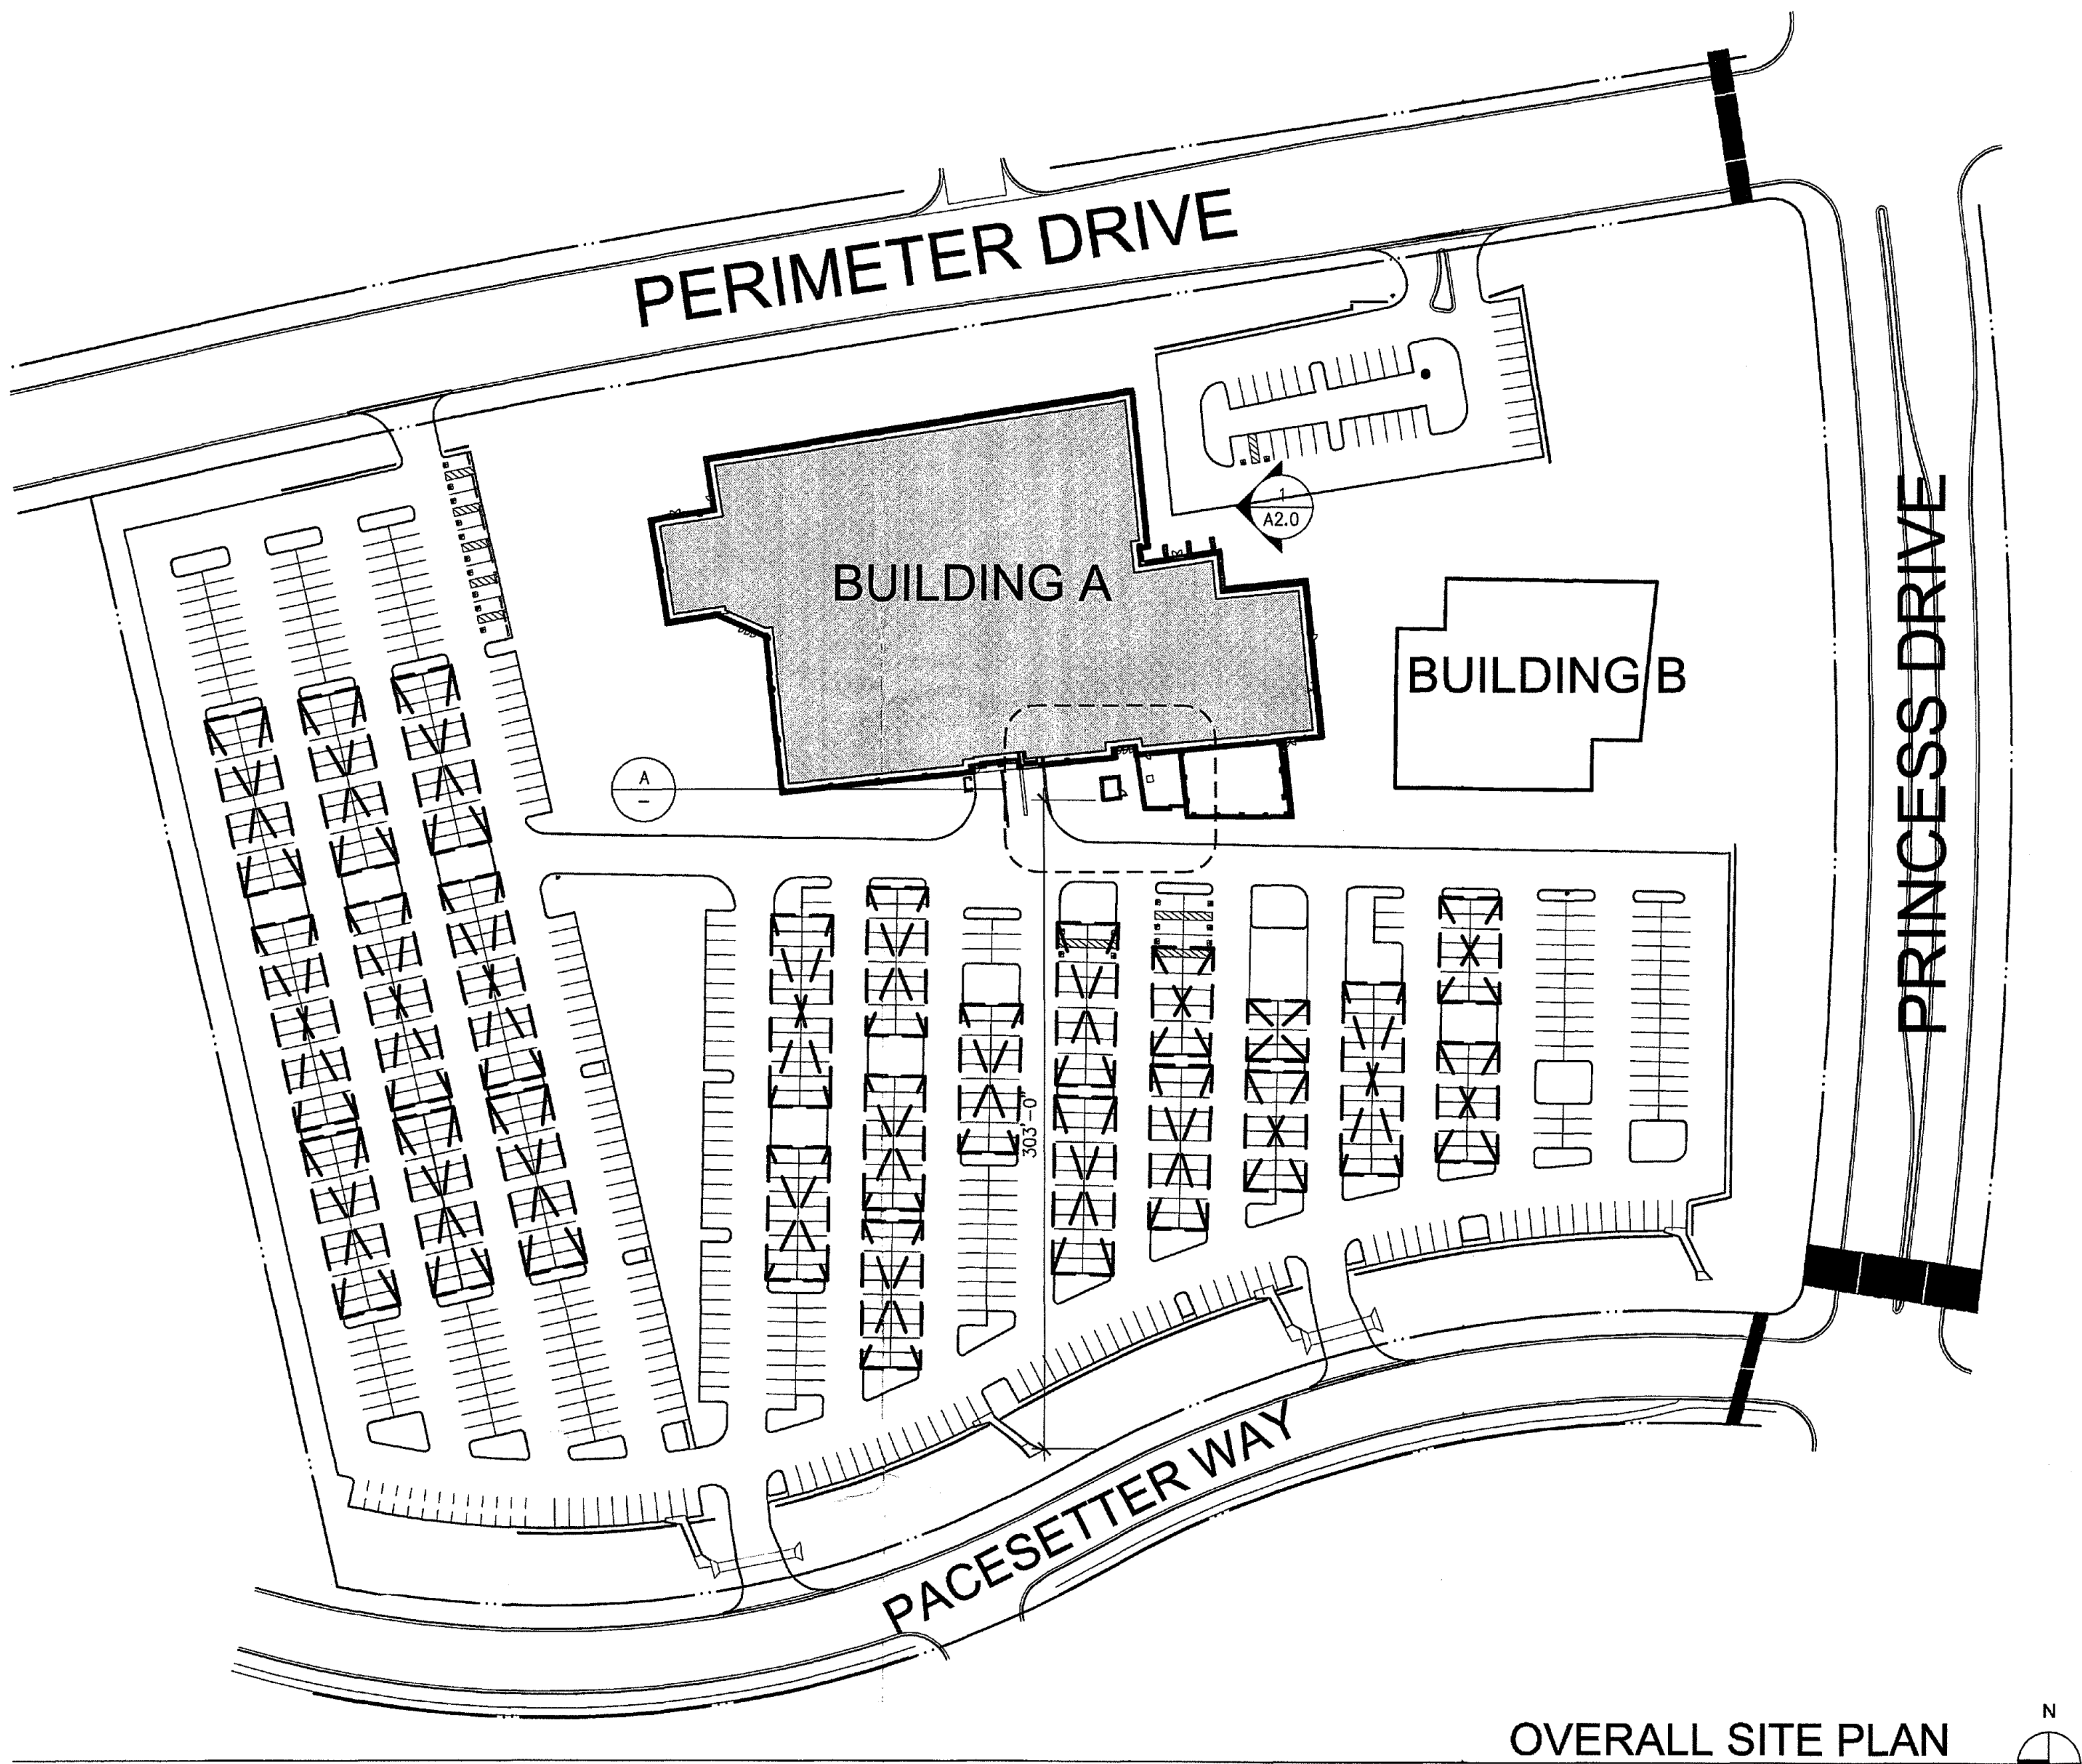

LAND / BUILDING OWNER

WDP PARTNERS
11411 N. TATUM BLVD.
PHOENIX, ARIZONA 85028

BRIAN FRAKES
BFRAKES@WDPPARTNERS.COM

TENANT



FENDER MUSICAL INSTRUMENTS CORPORATION
8860 EAST CHAPARRAL ROAD, SUITE 100
SCOTTSDALE, ARIZONA 85250

MAUREEN HAVRILLA
MHAVRILLA@FENDER.COM

ARCHITECT / APPLICANT

WARE MALCOMB
9977 N. 90TH STREET, SUITE 360
SCOTTSDALE, ARIZONA 85258

BROCK GRAYSON
BGRAYSON@WAREMALCOMB.COM

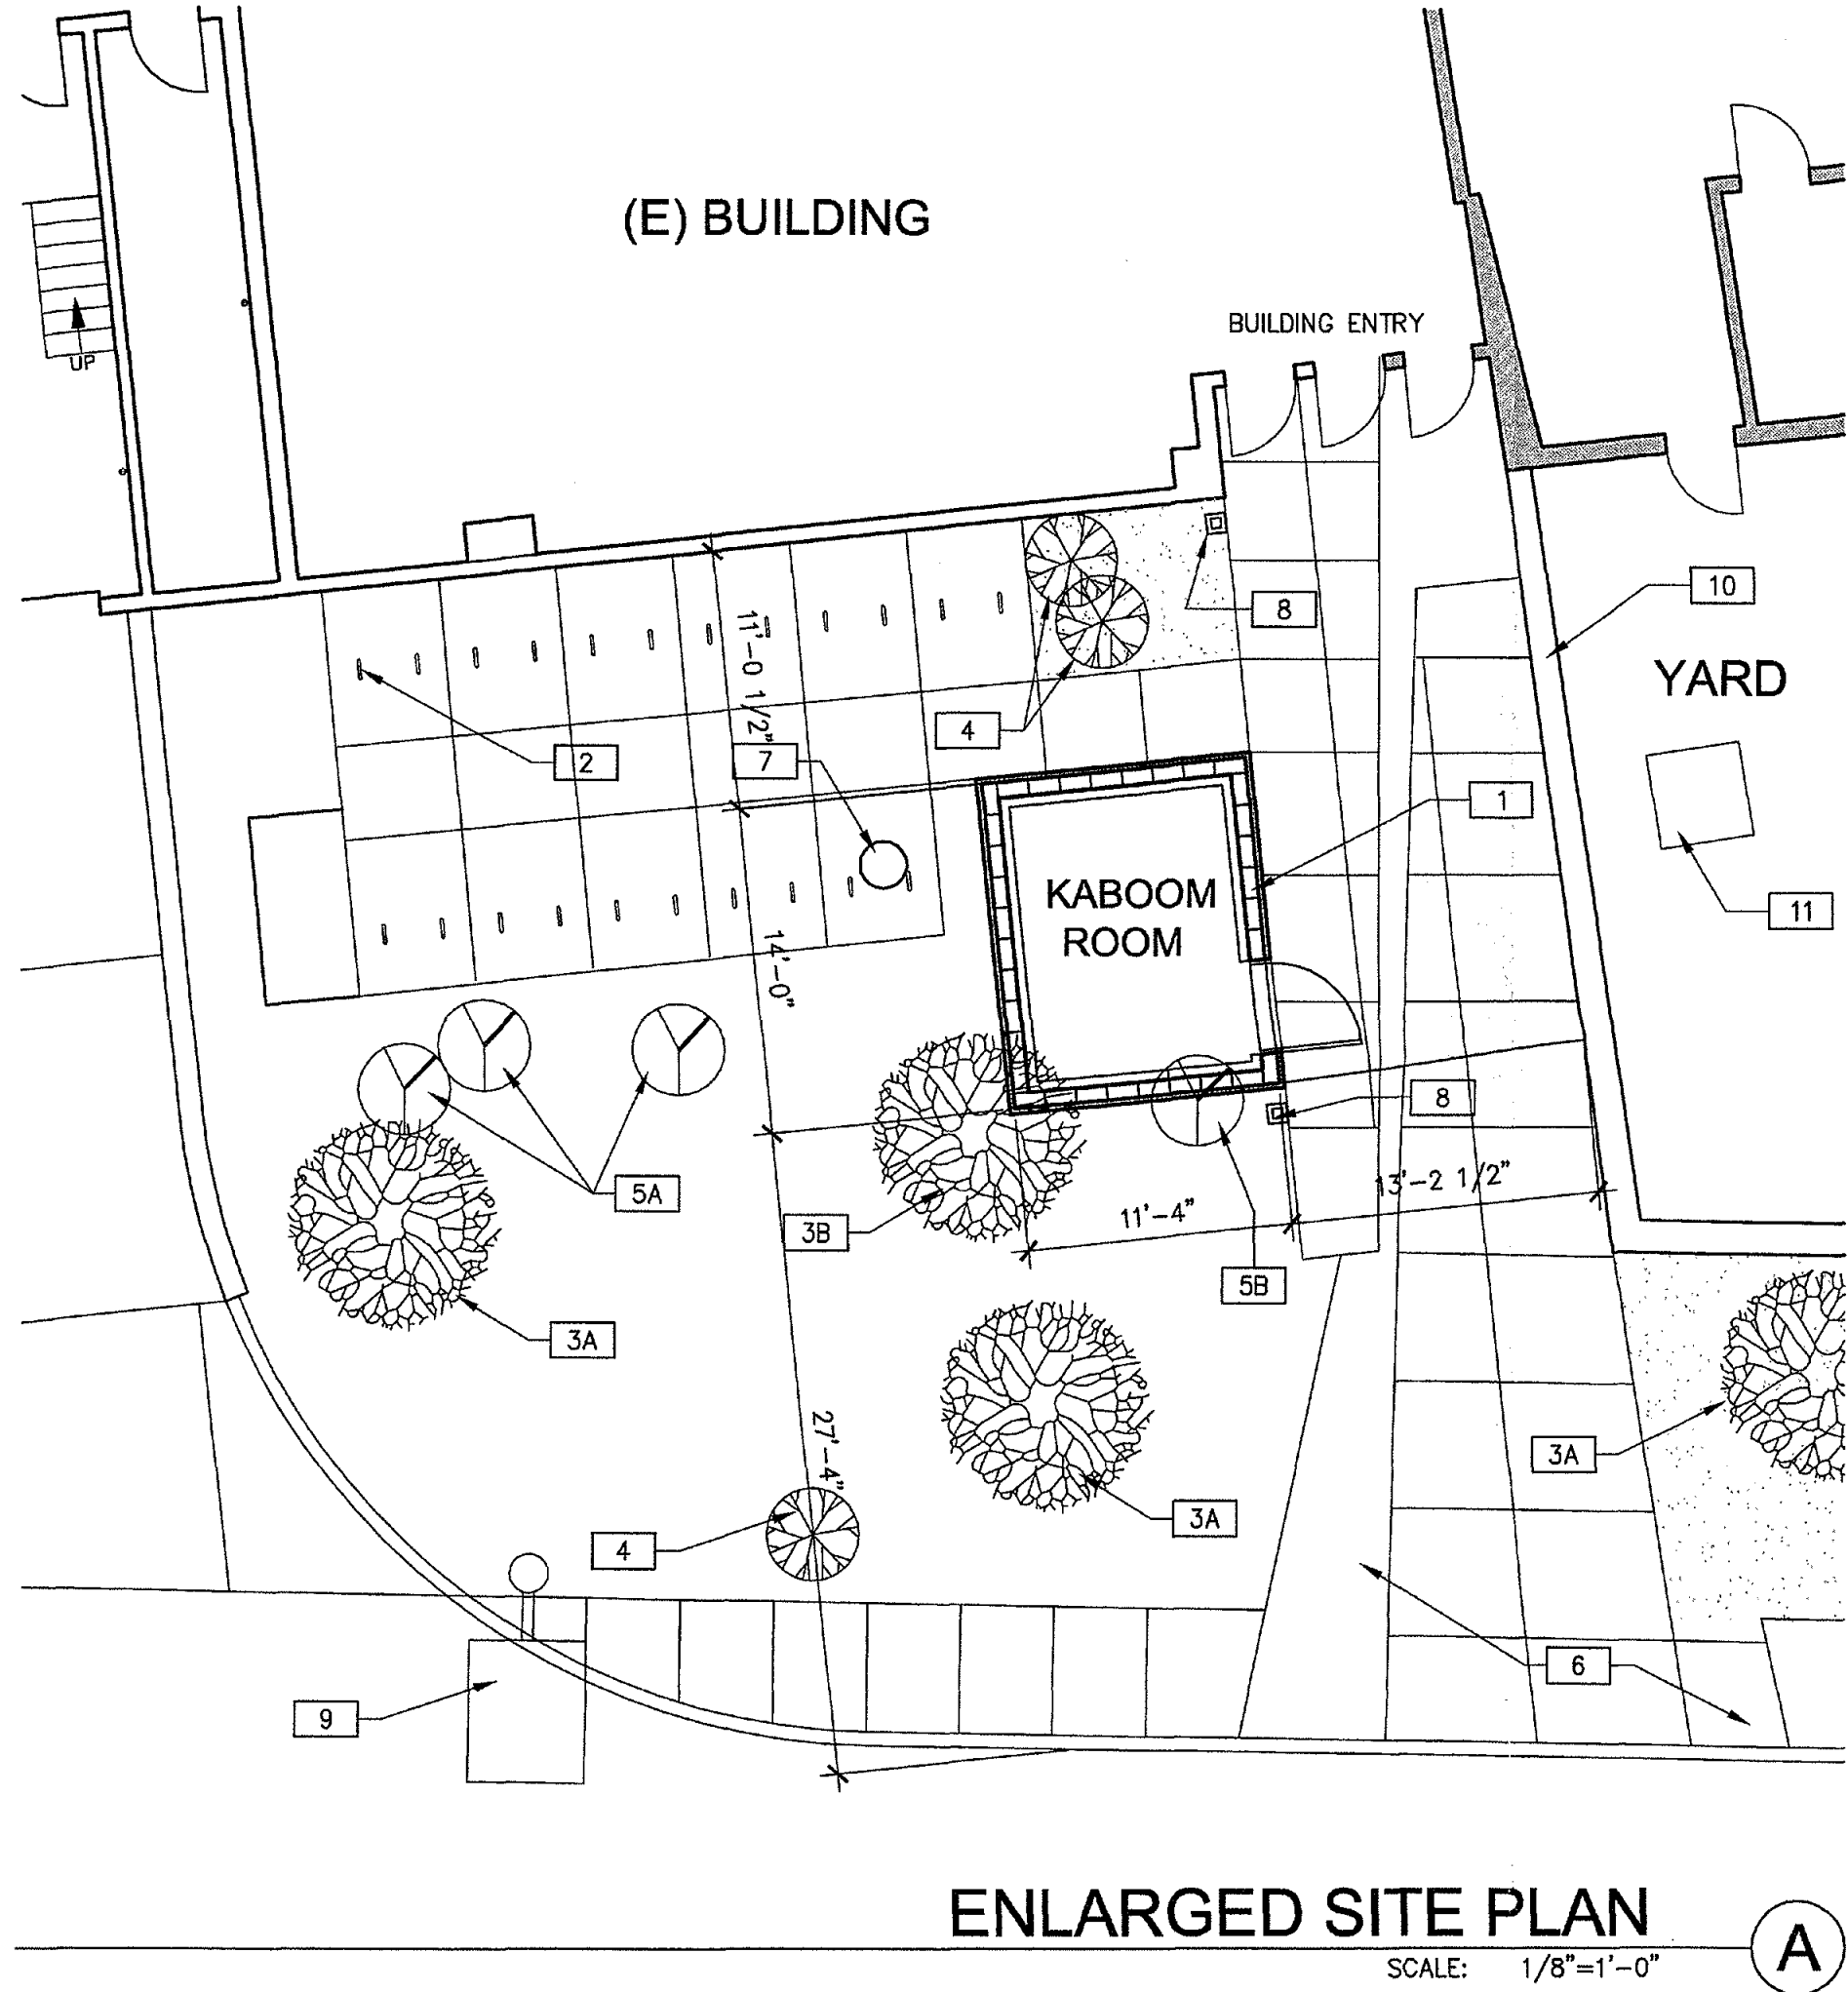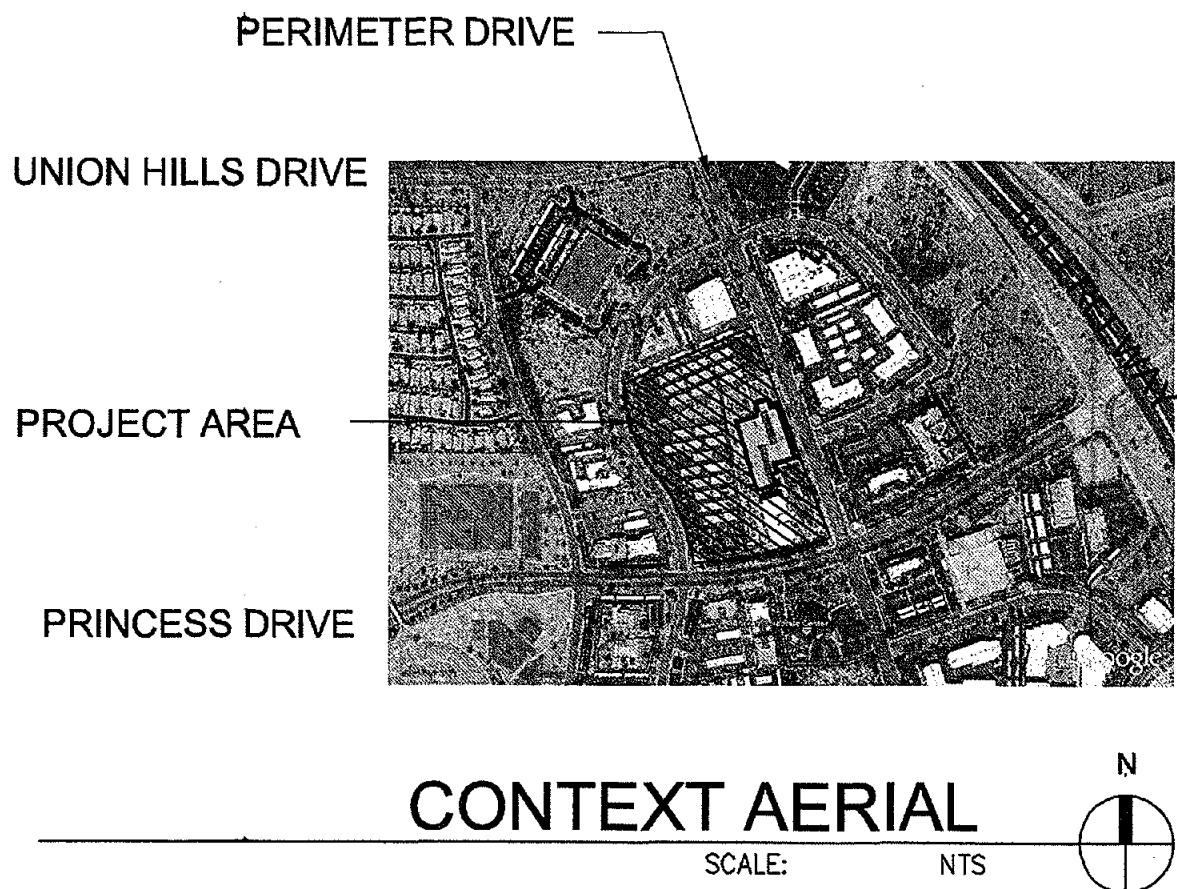


SITE PLAN NOTES:

- 1 NEW 11'-0" HIGH MASONRY ENCLOSURE
- 2 EXISTING BIKE RACKS
- 3A EXISTING ACACIA SMALLII/ SWEET ACACIA TREE
- 3B EXISTING ACACIA SMALLII/ SWEET ACACIA TREE TO BE RELOCATED IN SAME LANDSCAPE AREA. TREE TO BE LOCATED TO PROVIDE SHADE AT BICYCLE RACKS.
- 4 EXISTING ENCLIA FARINOSA/ BRITTLE BUSH SHRUB
- 5A EXISTING ACACIA REDOLENS/ ONGERUP ACACIA GROUNDCOVER
- 5B EXISTING ACACIA REDOLENS/ ONGERUP ACACIA GROUNDCOVER TO BE RELOCATED TO AVOID NEW CONSTRUCTION.
- 6 EXISTING SIDEWALK
- 7 EXISTING UTILITY ENCLOSURE
- 8 EXISTING LIGHT BOLLARD
- 9 EXISTING LIGHT POLE
- 10 EXISTING 11'-0" HIGH CMU SCREEN WALL
- 11 NEW HVAC UNIT FOR KABOOM ROOM. LOCATED BEHIND EXISTING 11'-0" HIGH SCREEN WALL FOR MECHANICAL YARD.

GENERAL NOTES:

- ALL SIGNS REQUIRE SEPARATE PERMITS AND APPROVAL.
- NO EXTERIOR VENDING OR DISPLAY SHALL BE ALLOWED.
- ALL EXTERIOR MECHANICAL, UTILITY, AND COMMUNICATION EQUIPMENT SHALL BE SCREENED, TO THE HEIGHT OF THE TALLEST UNIT, BY A PARAPET OR SCREEN WALL THAT MATCHES THE ARCHITECTURAL COLOR AND ARCHITECTURAL FINISHES OF THE BUILDING. GROUND MOUNTED MECHANICAL, UTILITY, AND COMMUNICATION EQUIPMENT SHALL BE SCREENED BY A SCREEN WALL THAT MATCHES THE ARCHITECTURAL COLOR AND ARCHITECTURAL FINISHES OF THE BUILDING, WHICH IS A MINIMUM OF 1'-0" HIGHER THAN THE HIGHEST POINT OF TALLEST UNIT.
- ALL EQUIPMENT, UTILITIES, OR OTHER APPURTENANCES ATTACHED TO THE BUILDING SHALL BE AN INTEGRAL PART OF THE BUILDING DESIGN IN TERMS OF FORM, COLOR, AND TEXTURE.

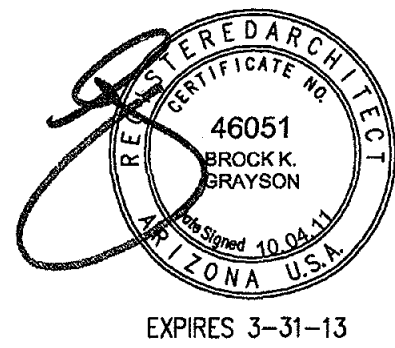

PROJECT NARRATIVE:

FENDER MUSICAL INSTRUMENTS CORPORATION WILL BE RELOCATING ITS HEADQUARTERS TO AN EXISTING FACILITY AT 17600 N PERIMETER DRIVE, SCOTTSDALE. THE TENANT IS PROPOSING TO BUILD A 170 SQUARE FOOT STRUCTURE ADJACENT TO THE BUILDING. THE PURPOSE OF THE STRUCTURE IS FOR THE TESTING OF SOUND EQUIPMENT.

THE PROPOSED LOCATION OF THE STRUCTURE WILL NOT REQUIRE MODIFICATIONS TO THE PARKING LOT. EXISTING LANDSCAPE WILL NOT BE IMPACTED. EXISTING EXTERIOR LIGHTING WILL NOT BE MODIFIED.

THE MECHANICAL UNIT FOR THE PROPOSED STRUCTURE WILL BE LOCATED BEHIND THE EXISTING SCREEN WALL OF THE MECHANICAL YARD.

THE PROPOSED STRUCTURE WILL INCORPORATE FINISHES THAT MATCH THE EXISTING BUILDING AND EXISTING SCREEN WALLS.

THE BUILDING CURRENTLY HAS AN ATM BUILT INTO THE ENTRANCE ON THE EAST SIDE OF THE BUILDING. FENDER WILL BE REMOVING THE ATM AND METAL PANELS TO RESTORE THE BUILDING TO ITS ORIGINAL APPEARANCE.

PROJECT DATA:

APN:	215-07-230
ZONING:	I-1
PREVIOUS ZONING CASE:	195-DR-97
SITE AREA:	725,016 SF (16.65 AC)
AREA A:	452,782 SF (10.39 AC)
AREA B:	272,234 SF (6.25 AC)
BUILDING AREA:	221,131 SF
BUILDING A:	130,059 SF
BUILDING B:	91,072 SF
PARKING REQUIRED:	728 STALLS
BUILDING A:	124,770 SF / 300 = 416 STALLS
OFFICE:	1,383 SF / 500 = 3 STALLS
MANUFACTURING:	3,906 SF / 800 = 5 STALLS
WAREHOUSE:	
TOTAL:	424 STALLS
BUILDING B:	
OFFICE:	91,072 SF / 300 = 304 STALLS
TOTAL REQUIRED:	728 STALLS
PARKING PROVIDED:	1,016 STALLS
BIKE PARKING REQUIRED:	
BUILDING A:	424 / 10 = 43 BICYCLE PARKING
BIKE PARKING PROVIDED:	44 BICYCLES (2 FOR EVERY RACK)

LEGAL DESCRIPTION:

A PORTION OF THE SOUTH HALF OF SECTION 36, TOWNSHIP 4 NORTH, RANGE 4 EAST OF THE GILA AND SALT RIVER BASE MERIDIAN, MARICOPA COUNTY, ARIZONA, BEING MORE PARTICULARLY DESCRIBED AS FOLLOWS:

COMMENCING AT THE CENTERLINE INTERSECTION OF PERIMETER DRIVE WITH ST. JOHN ROAD AS SHOWN ON THE "MAP OF DEDICATION OF RIGHT-OF-WAY AND EASEMENTS FOR PERIMETER CENTER PHASE TWO" RECORDED IN BOOK 332 PAGE 49. RECORDS OF MARICOPA COUNTY RECORDS.

THENCE NORTH 19 DEGREES 24 MINUTES 34 SECONDS WEST ALONG THE CENTERLINE OF PERIMETER DRIVE. 120.00 FEET;

THENCE SOUTH 70 DEGREES 35 MINUTES 26 SECONDS WEST, 45.00 FEET TO A POINT ON THE WESTERLY RIGHT-OF-WAY LINE OF SAID PERIMETER DRIVE MAKING THE POINT OF BEGINNING.

THENCE SOUTH 19 DEGREES 24 MINUTES 34 SECONDS EAST ALONG SAID WESTERLY RIGHT-OF-WAY LINE, 610.43 FEET TO THE BEGINNING OF A CURVE WITH A RADIUS OF 20.00 FEET;

THENCE SOUTHWESTERLY ALONG THE ARC OF SAID CURVE, THROUGH A CENTRAL ANGLE OF 92 DEGREES 02 MINUTES 20 SECONDS. FOR CURVATURE OF THE NORTHERLY RIGHT-OF-WAY LINE OF PRINCESS DRIVE MARKING THE BEGINNING OF A CURVE WITH A RADIUS OF 2645.00 FEET;

THENCE SOUTHWESTERLY ALONG SAID RIGHT-OF-WAY LINE AND ALONG THE ARC OF SAID CURVE, THROUGH A CENTRAL ANGLE OF 14 DEGREES 21 MINUTES 01 SECONDS, FOR AN ARC DISTANCE OF 662.47 FEET TO A POINT OF COMPOUND CURVATURE MARKING THE BEGINNING OF A CURVE WITH A RADIUS OF 20.00 FEET; THENCE NORTHWESTERLY ALONG THE ARC OF SAID CURVE, THROUGH A CENTRAL ANGLE OF 87 DEGREES 12 MINUTES 13 SECONDS, FOR AN ARC DISTANCE OF 30.44 FEET TO A POINT OF REVERSE CURVATURE ON THE EASTERLY RIGHT-OF-WAY LINE OF 62ND STREET MARKING THE BEGINNING OF A CURVE WITH A RADIUS OF 785.00 FEET;

THENCE NORTHERLY ALONG SAID EASTERLY RIGHT-OF-WAY LINE AND ALONG THE ARC OF SAID CURVE, THROUGH A CENTRAL ANGLE OF 34 DEGREES 10 MINUTES 10 SECONDS, FOR AN ARC DISTANCE OF 468.15 FEET TO A POINT OF REVERSE CURVATURE MARKING THE BEGINNING OF A CURVE WITH A RADIUS OF 640.00 FEET;

THENCE NORTHWESTERLY ALONG SAID EASTERLY RIGHT-OF-WAY LINE AND ALONG THE ARC OF SAID CURVE, THROUGH A CENTRAL ANGLE OF 34 DEGREES 10 MINUTES 10 SECONDS, FOR AN ARC DISTANCE OF 468.15 FEET TO A POINT OF REVERSE CURVATURE MARKING THE BEGINNING OF A CURVE WITH A RADIUS OF 640.00 FEET;

THENCE NORTHWESTERLY CONTINUING ALONG SAID EASTERLY RIGHT-OF-WAY LINE AND ALONG THE ARC OF SAID CURVE, THROUGH A CENTRAL ANGLE OF 41 DEGREES 37 MINUTES 44 SECONDS FOR AN ARC DISTANCE OF 465.00 FEET TO THE BEGINNING OF A NON-TANGENT LINE;

THENCE DEPARTING SAID EASTERLY RIGHT-OF-WAY LINE NORTH 66 DEGREES 55 MINUTES 51 SECONDS EAST; 697.16 FEET TO A POINT ON THE AFOREMENTIONED WESTERLY RIGHT-OF-WAY LINE OF PERIMETER DRIVE;

THENCE SOUTH 23 DEGREES 04 MINUTES 09 SECONDS EAST ALONG SAID WESTERLY RIGHT-OF-WAY LINE, 79.03 FEET TO THE BEGINNING OF A CURVE WITH A RADIUS OF 5955.00 FEET TO THE RIGHT;

THENCE SOUTHEASTERLY ALONG SAID RIGHT-OF-WAY LINE AND ALONG THE ARC OF SAID CURVE, THROUGH A CENTRAL ANGLE OF 03 DEGREES 39 MINUTES 36 SECONDS, FOR AN ARC DISTANCE OF 380.39 FEET TO THE POINT OF BEGINNING.



FMIC
Scottsdale, Arizona

17600 North Perimeter Drive

Sheet A1.0

PHX11-6016-00
10-04-2011

WARE MALCOMB
Leading Design for Commercial Real Estate

integrated service
across north america | waremalcomb.com