
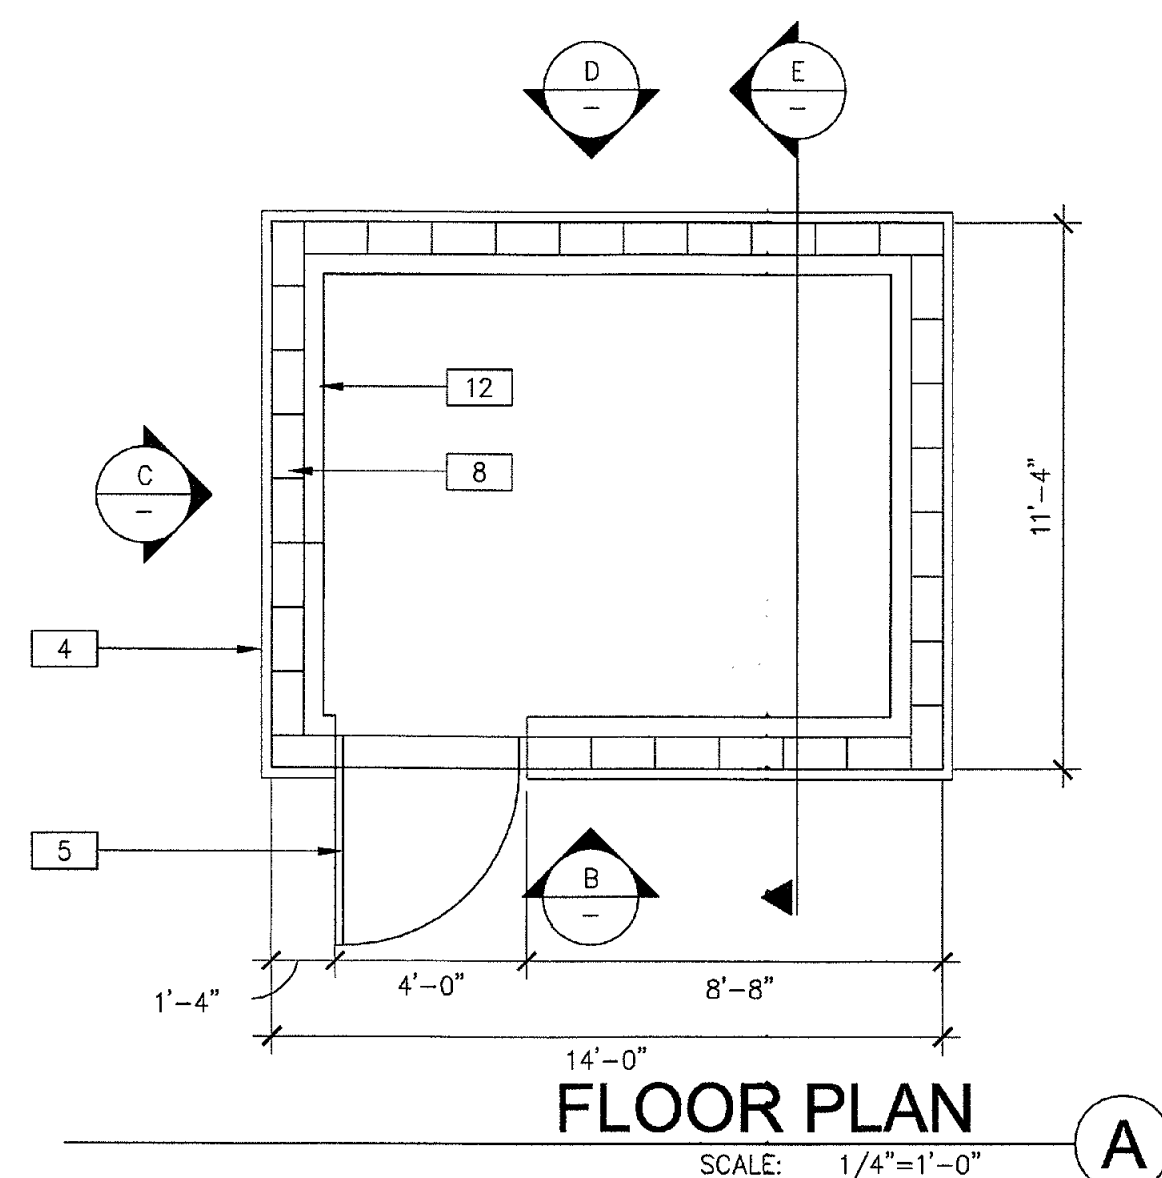








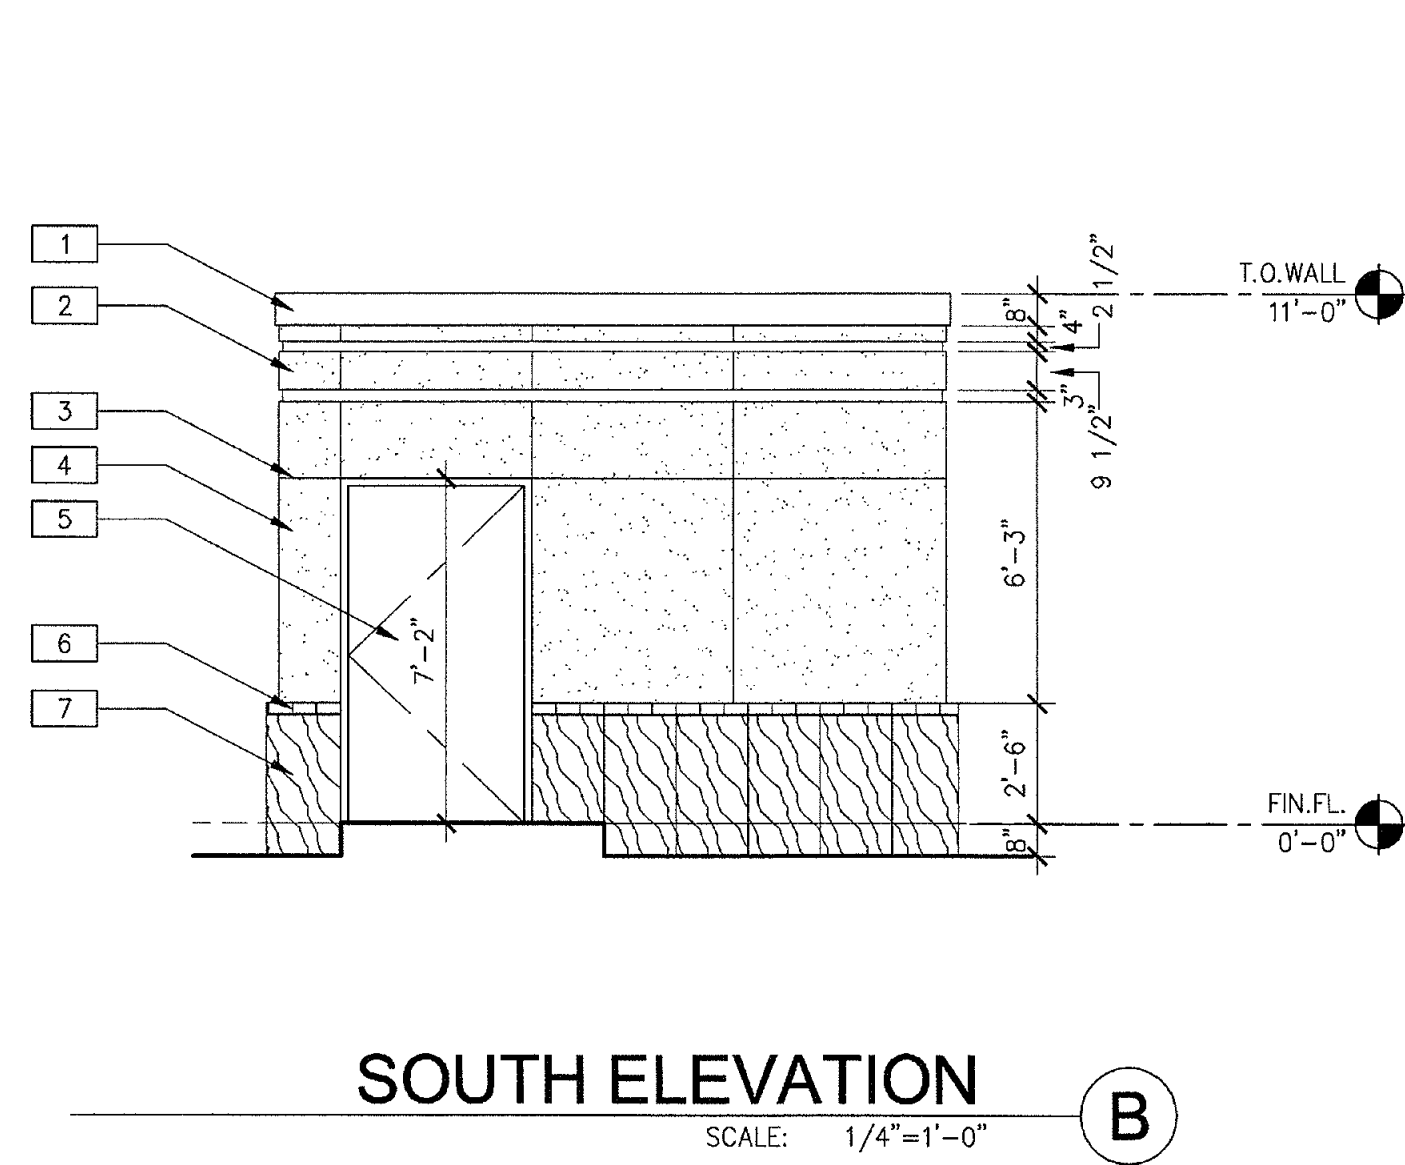


KABOOM ROOM NOTES:

- 1 METAL FLASHING, PAINTED TO MATCH BUILDING.
- 2 FOAM POP-OUT TO MATCH BUILDING. (DESERT LACE #01009)
- 3 E.F.I.S. CONTROL JOINT.
- 4 E.F.I.S. TO MATCH BUILDING TEXTURE AND COLOR. (SANDIA #1616)
- 5 INSULATED METAL DOOR, PAINTED TO MATCH.
- 6 STONE CAP TO MATCH EXISTING.
- 7 ROSA SANDSTONE TO MATCH BUILDING.
- 8 CMU BLOCK
- 9 CONCRETE DECK WITH WHITE ROOF MEMBRANE
- 10 METAL DECK
- 11 METAL "C" CHANNEL
- 12 SOUND ISOLATING WALL COVERING.
- 13 CONCRETE SLAB.

ELEVATION NOTES:

- A GLAZING TO MATCH BUILDING.
- B CLEAR ANODIZED ALUMINUM MULLION TO MATCH BUILDING.
- C ROSA SANDSTONE TO MATCH BUILDING.
- D EXISTING ATM MACHINE TO BE REMOVED.
- E EXISTING METAL PANELS TO BE REMOVED.

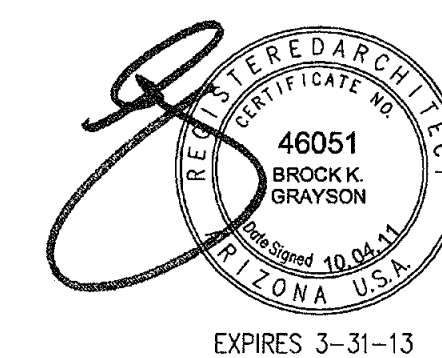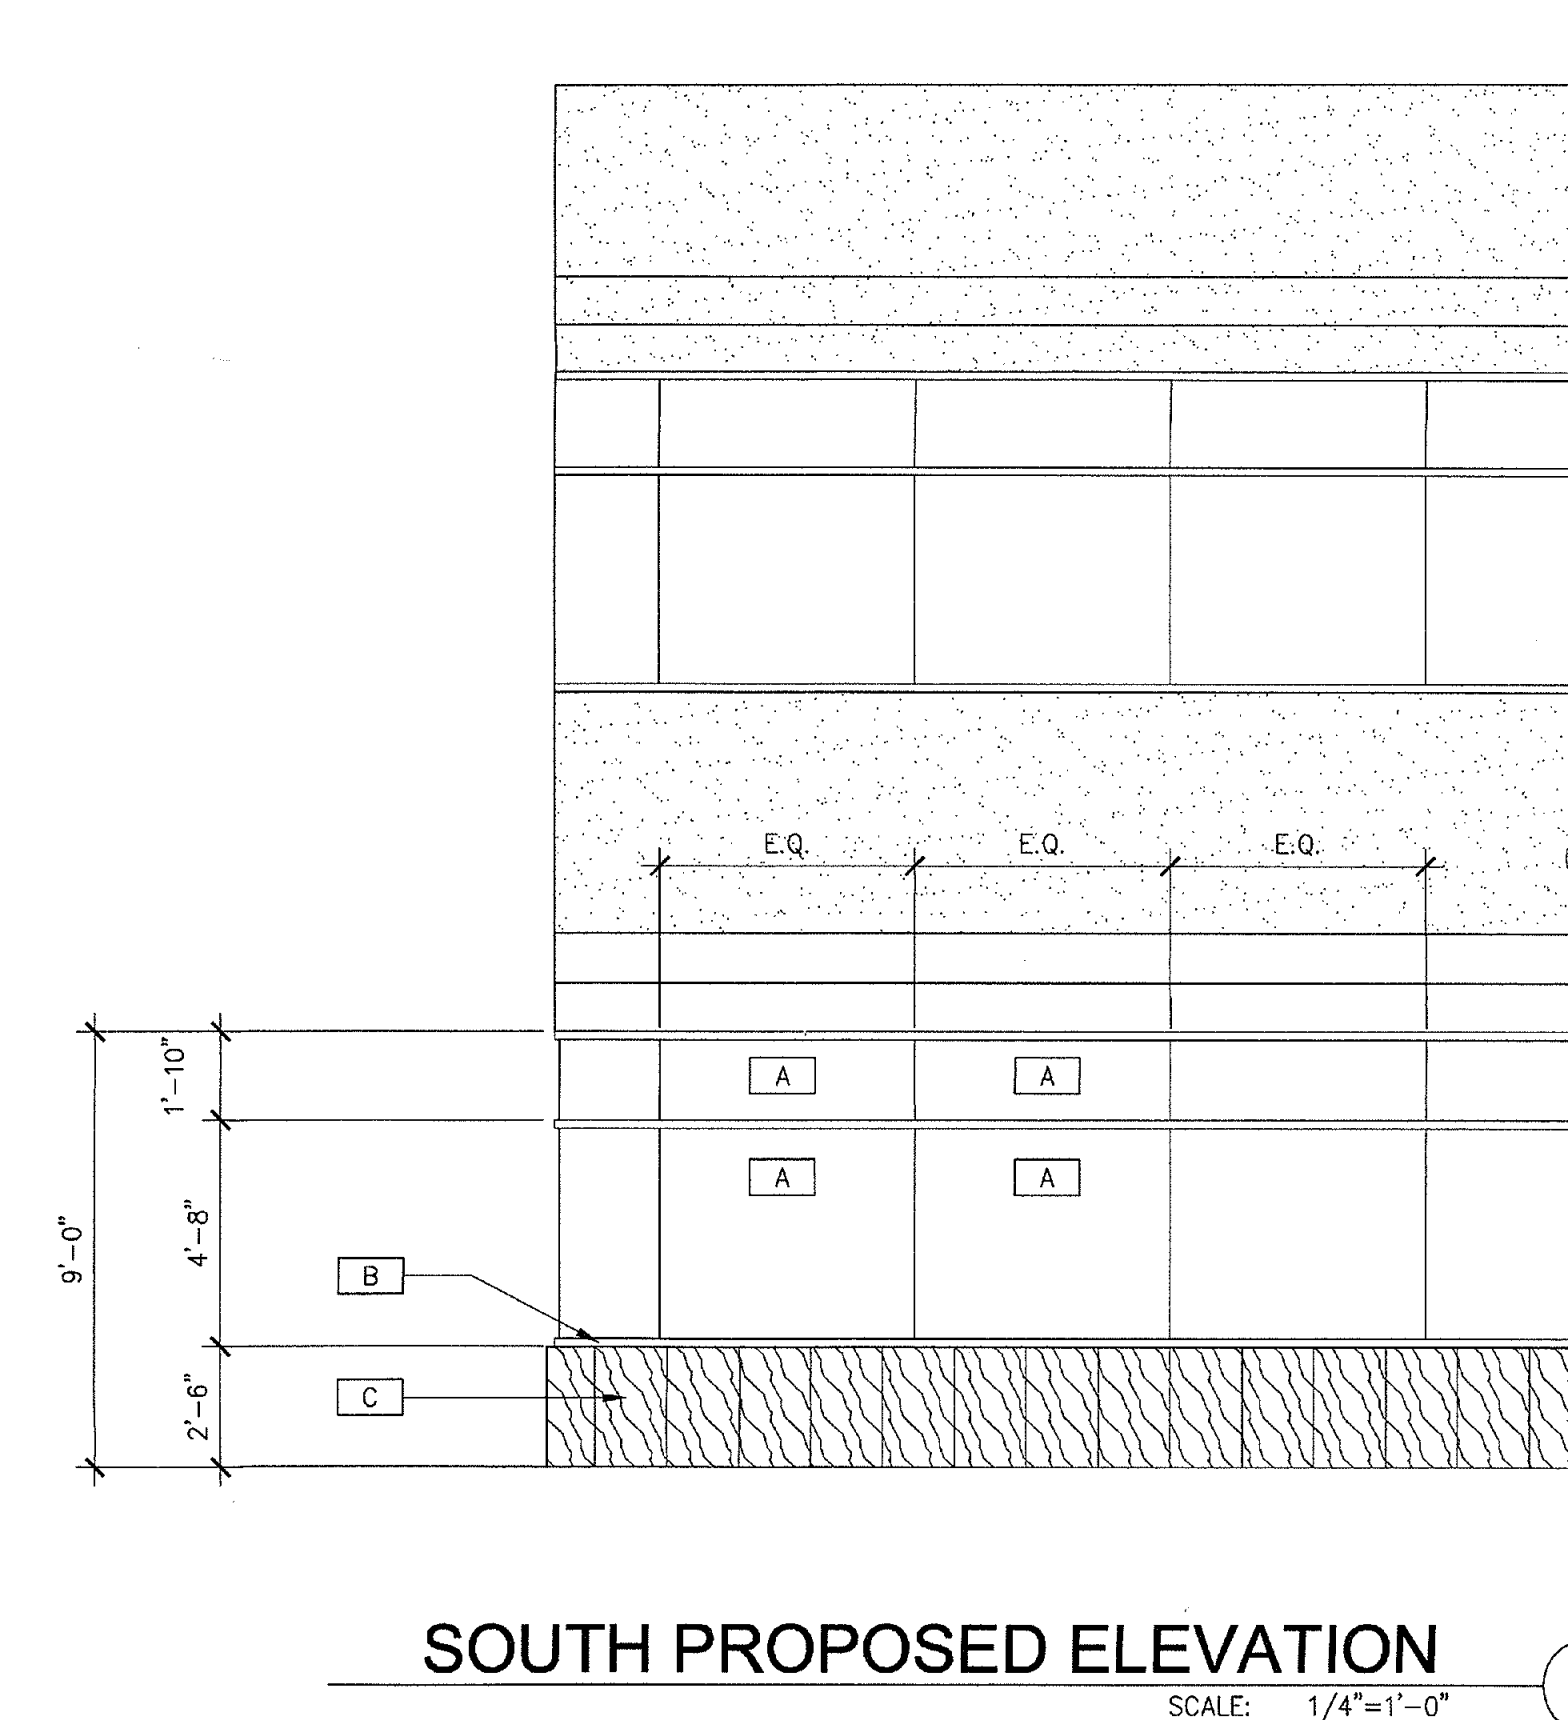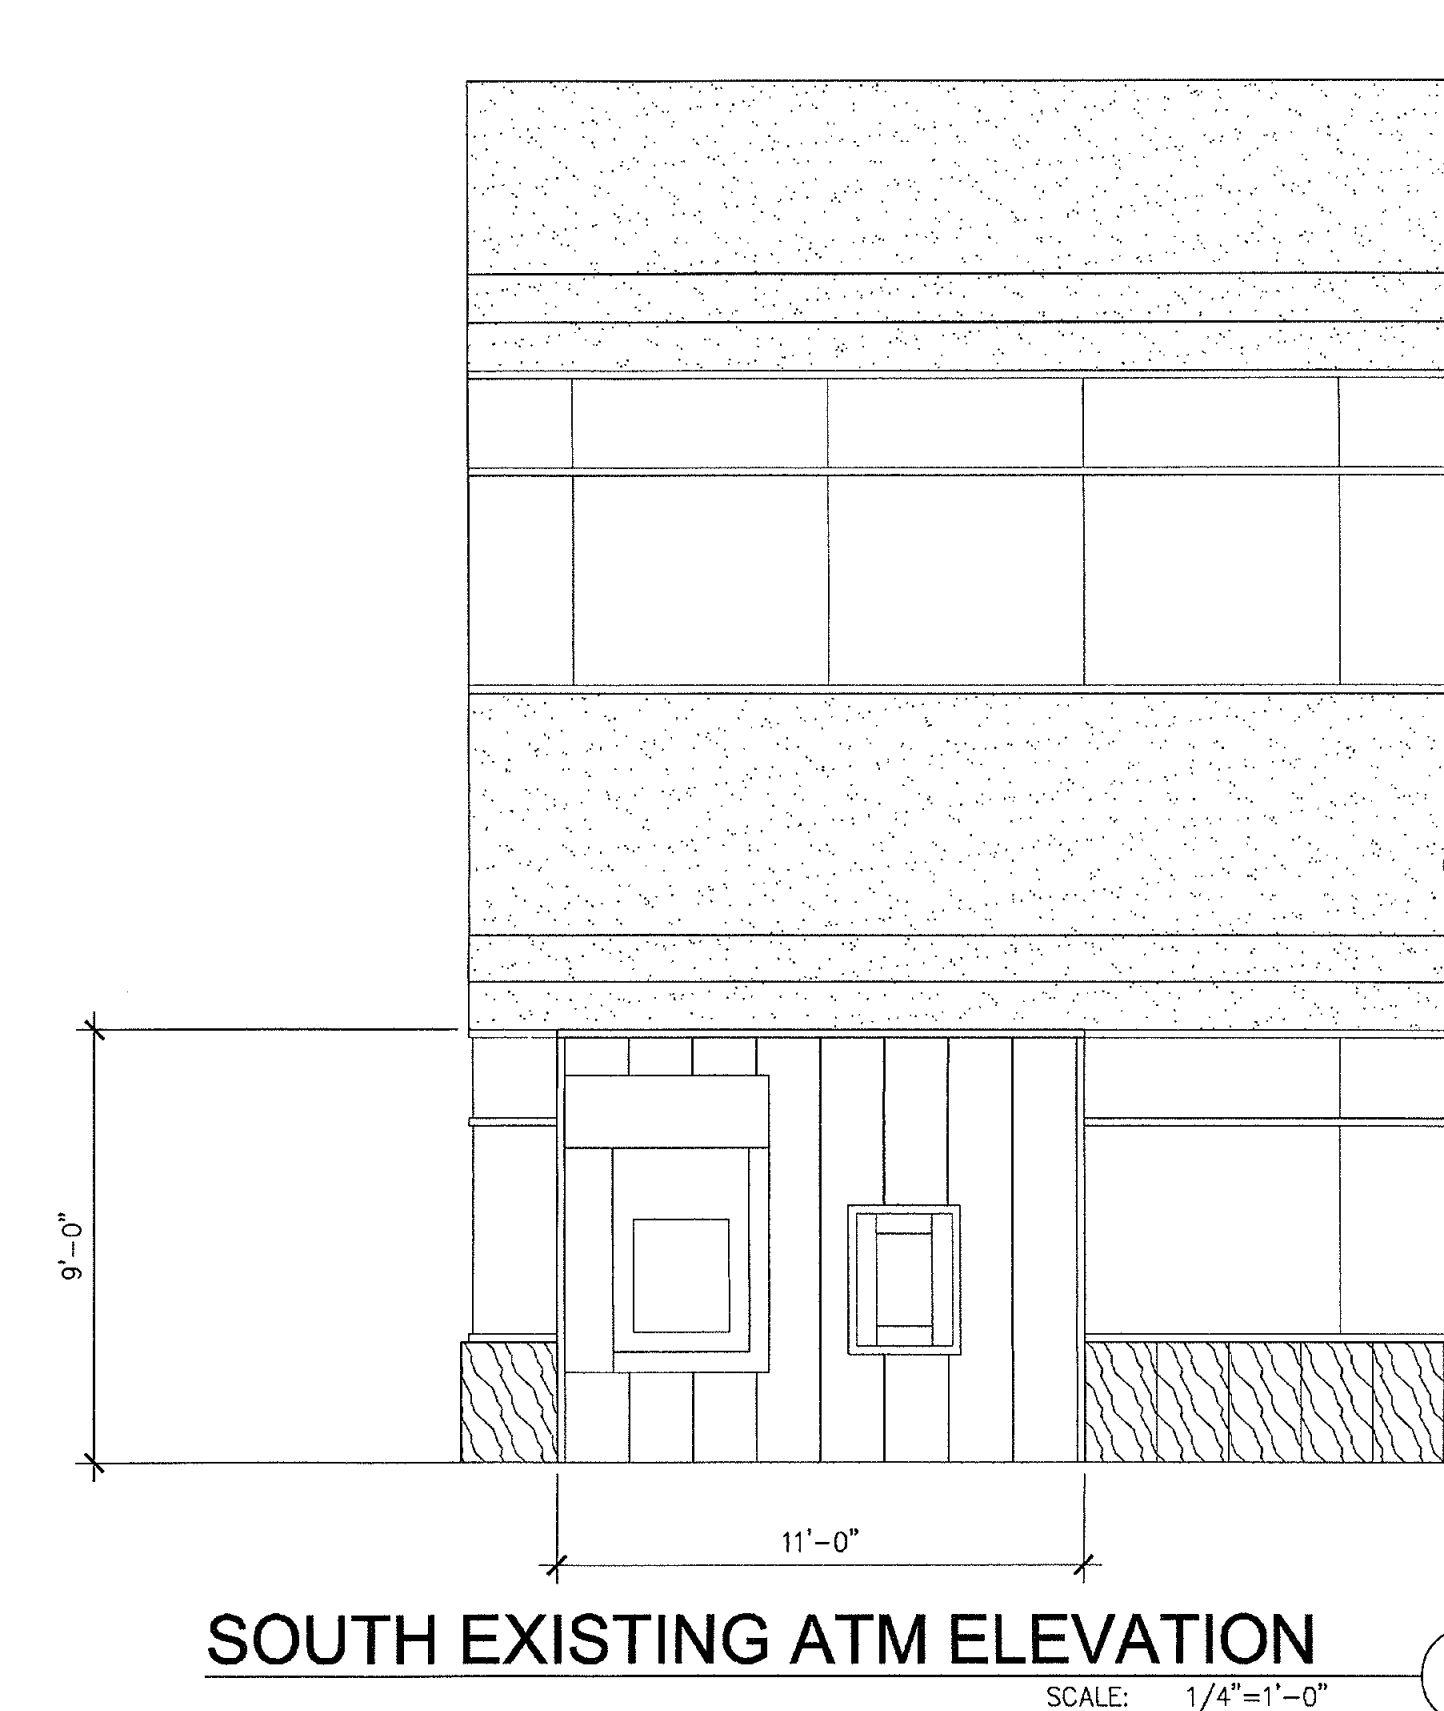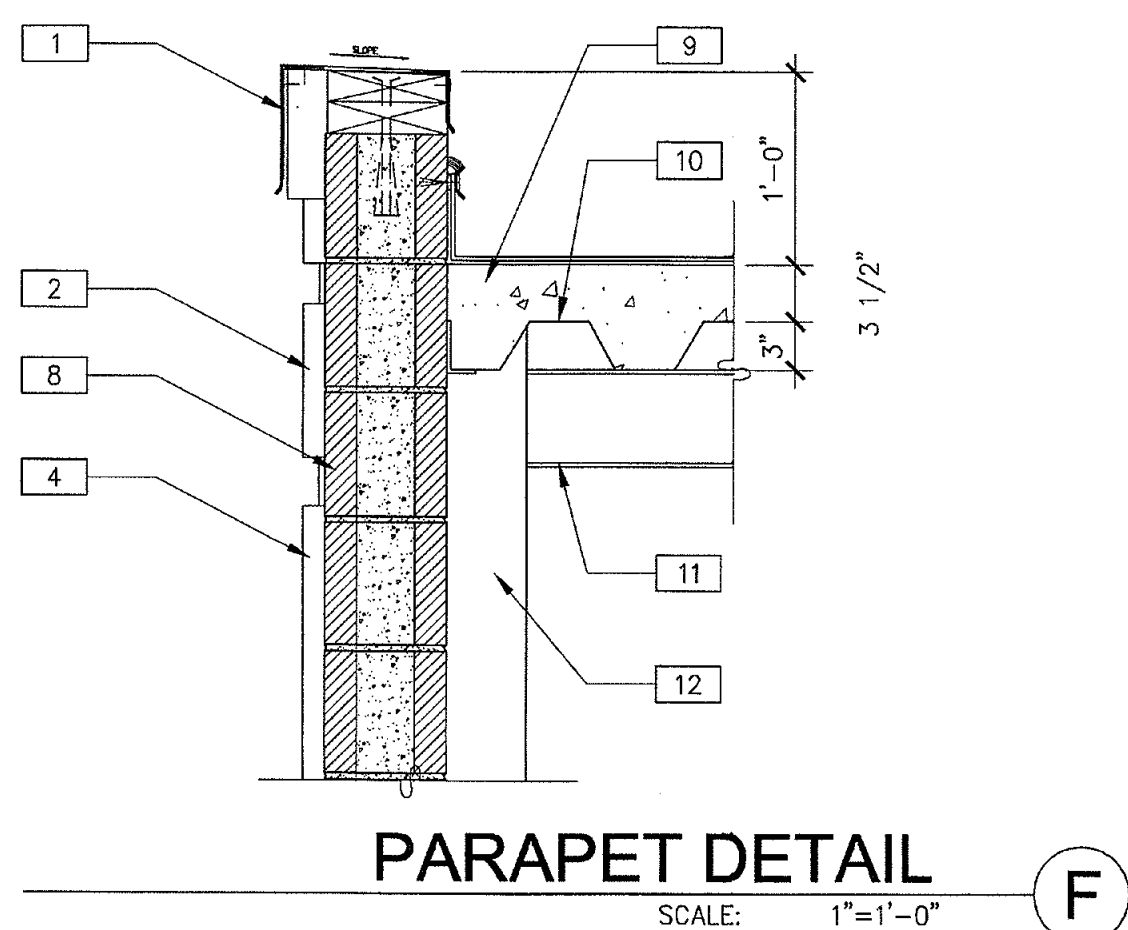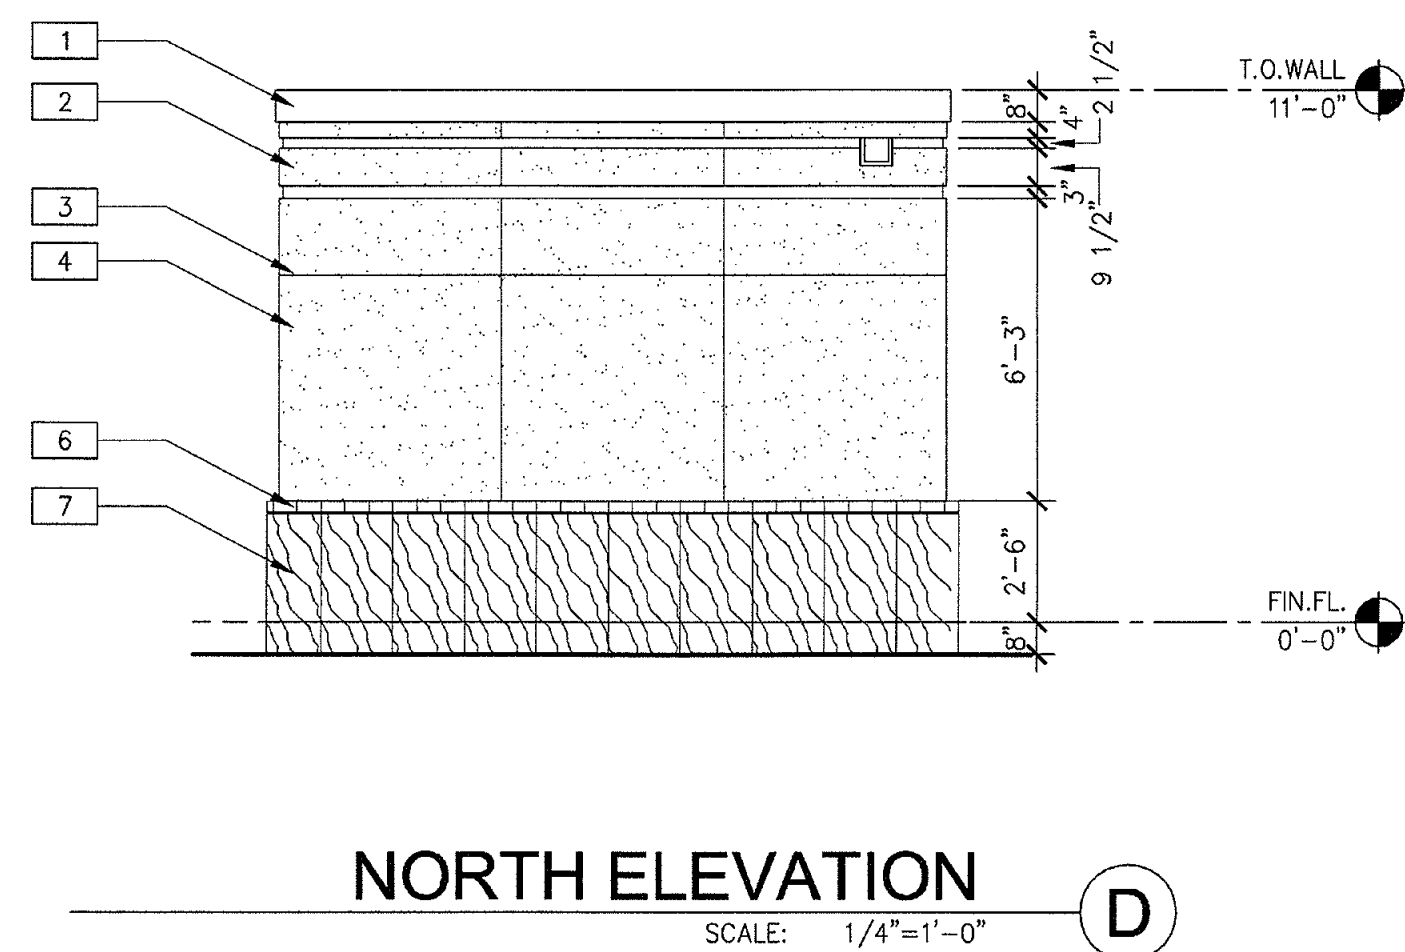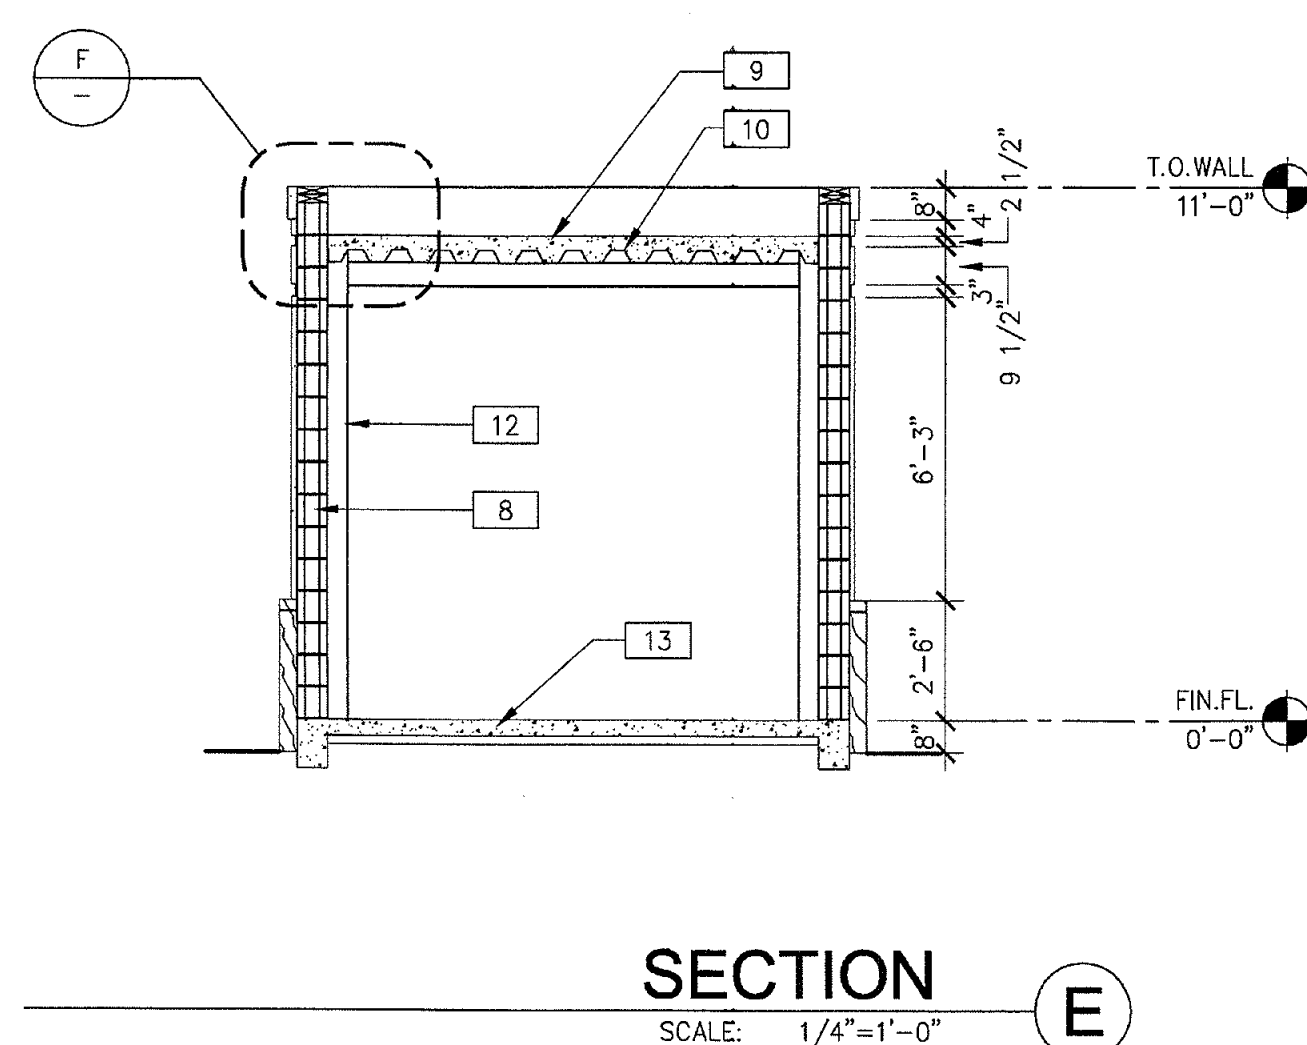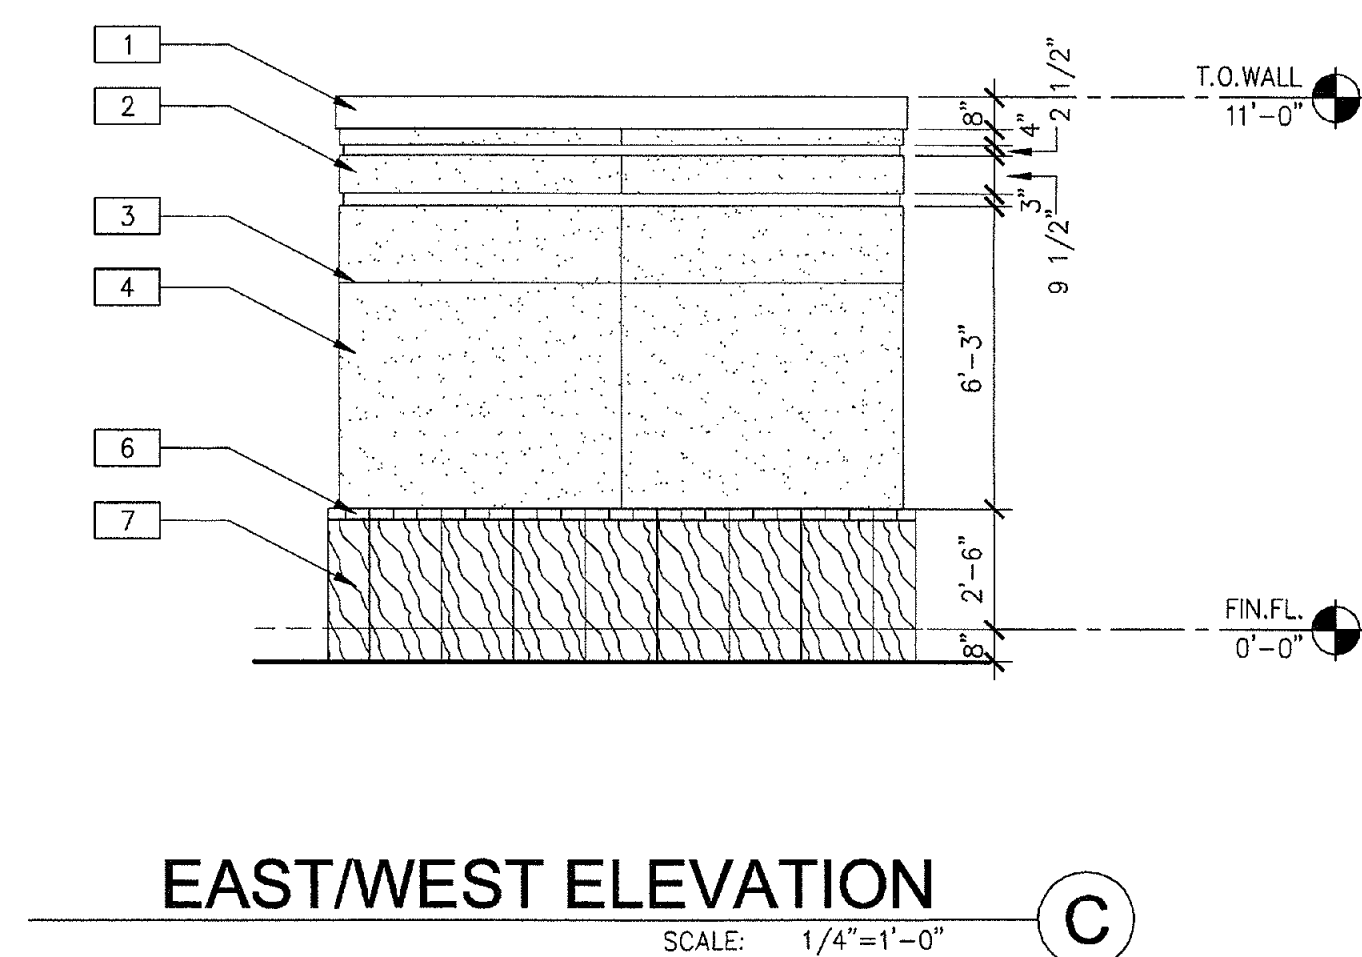

Fender®

FMIC
Scottsdale, Arizona

17600 North Perimeter Drive

Sheet A2.0

PHX11-6016-00
10-04-2011

WARE MALCOMB
Leading Design for Commercial Real Estate

integrated service
across north america | waremalcomb.com