




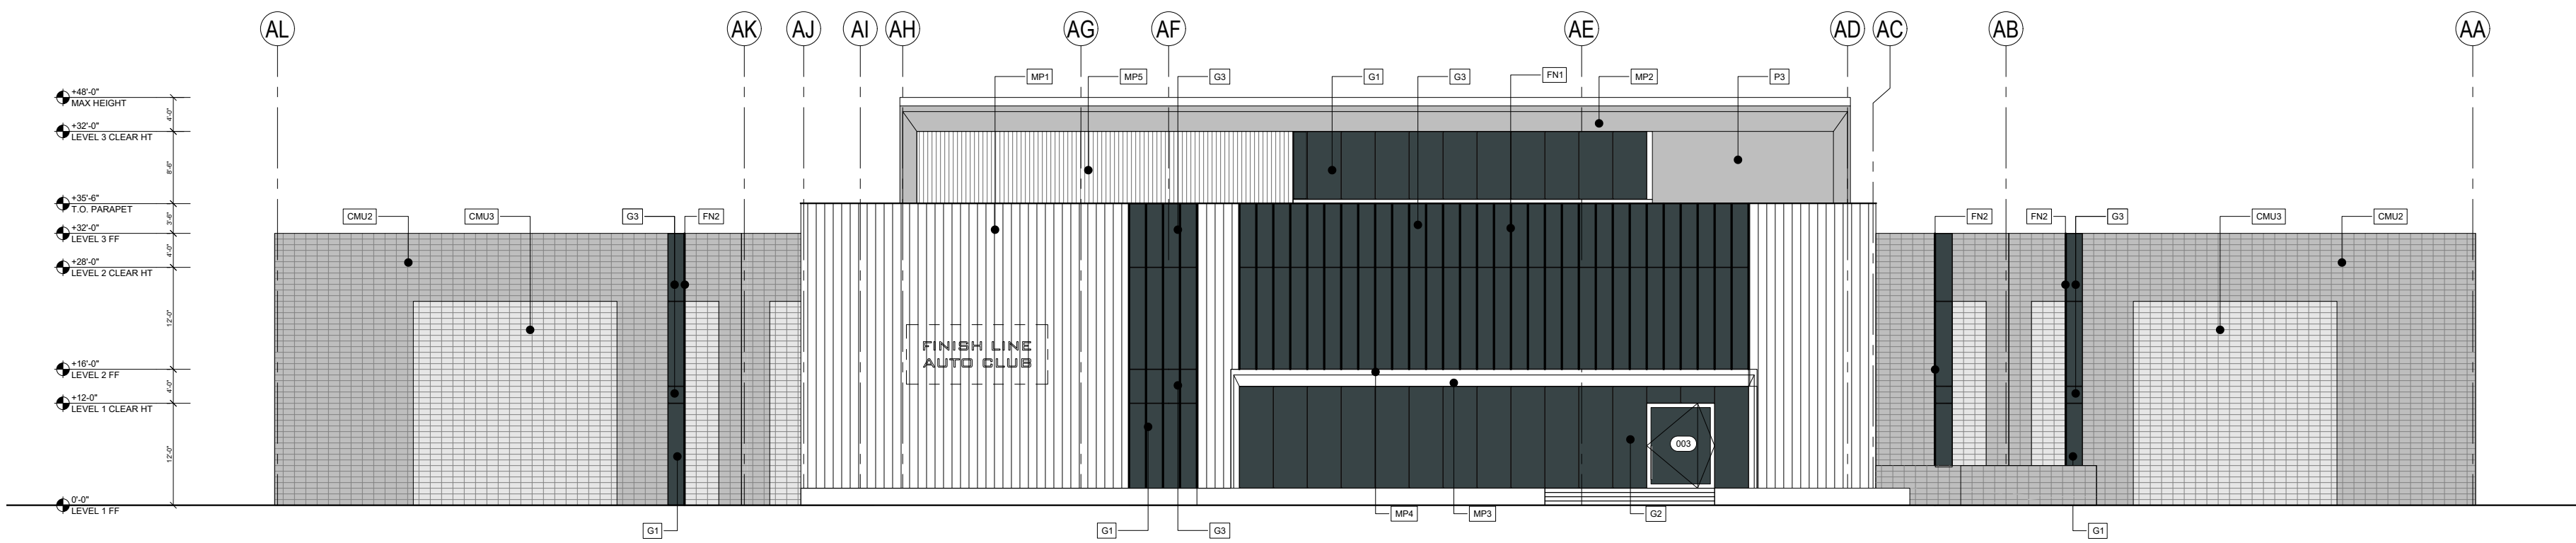


04 EAST ELEVATION - BUILDING A
SCALE: 1/16" = 1'-0"

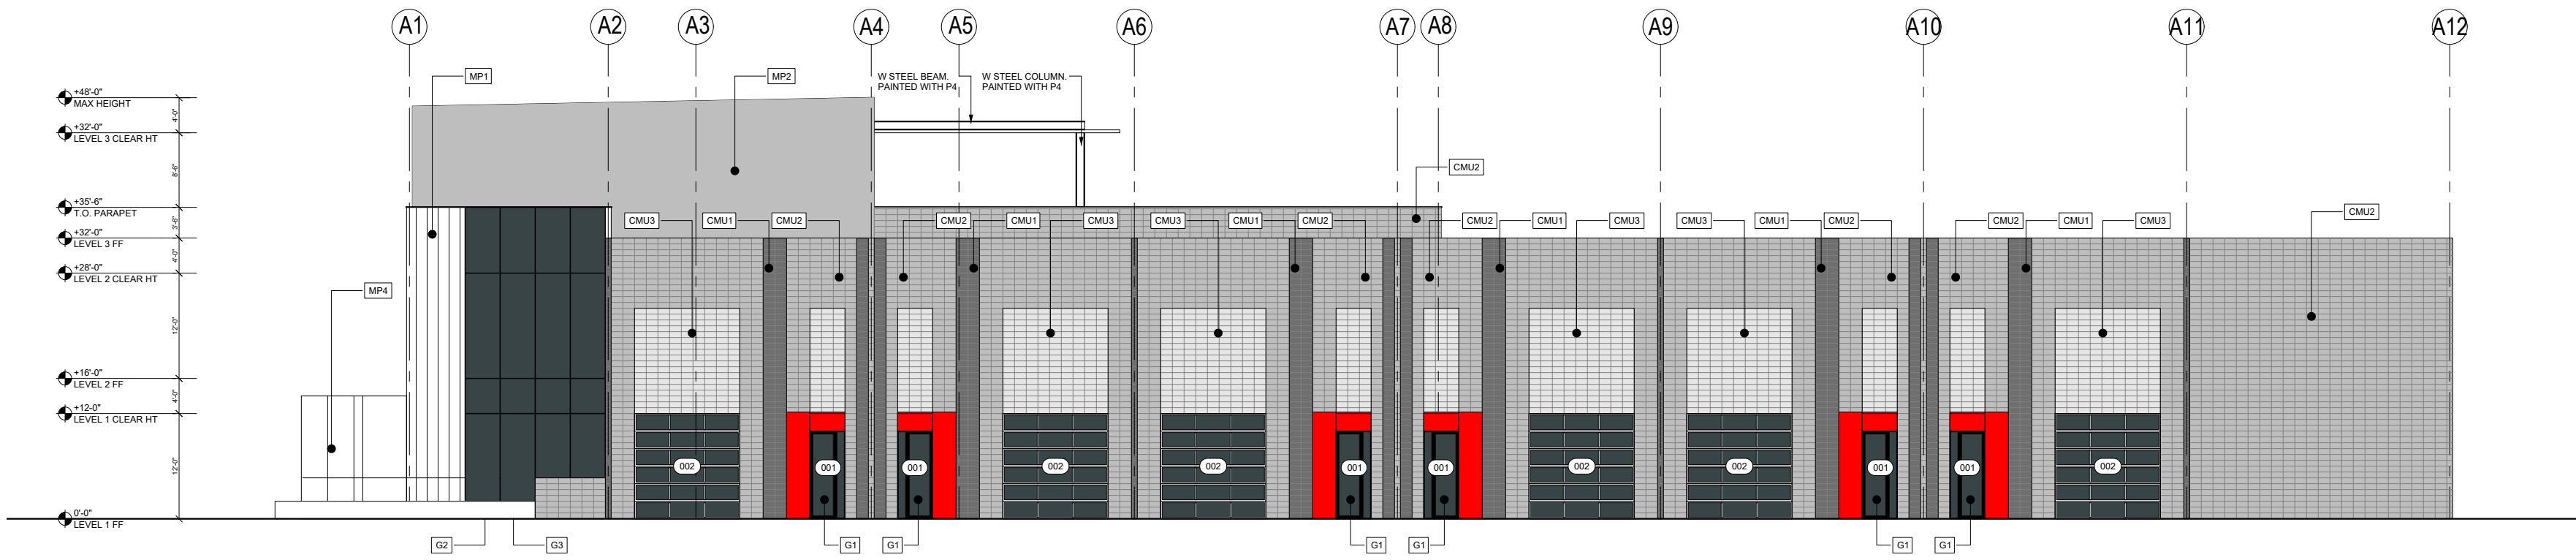

03 NORTH ELEVATION - BUILDING A
SCALE: 1/16" = 1'-0"

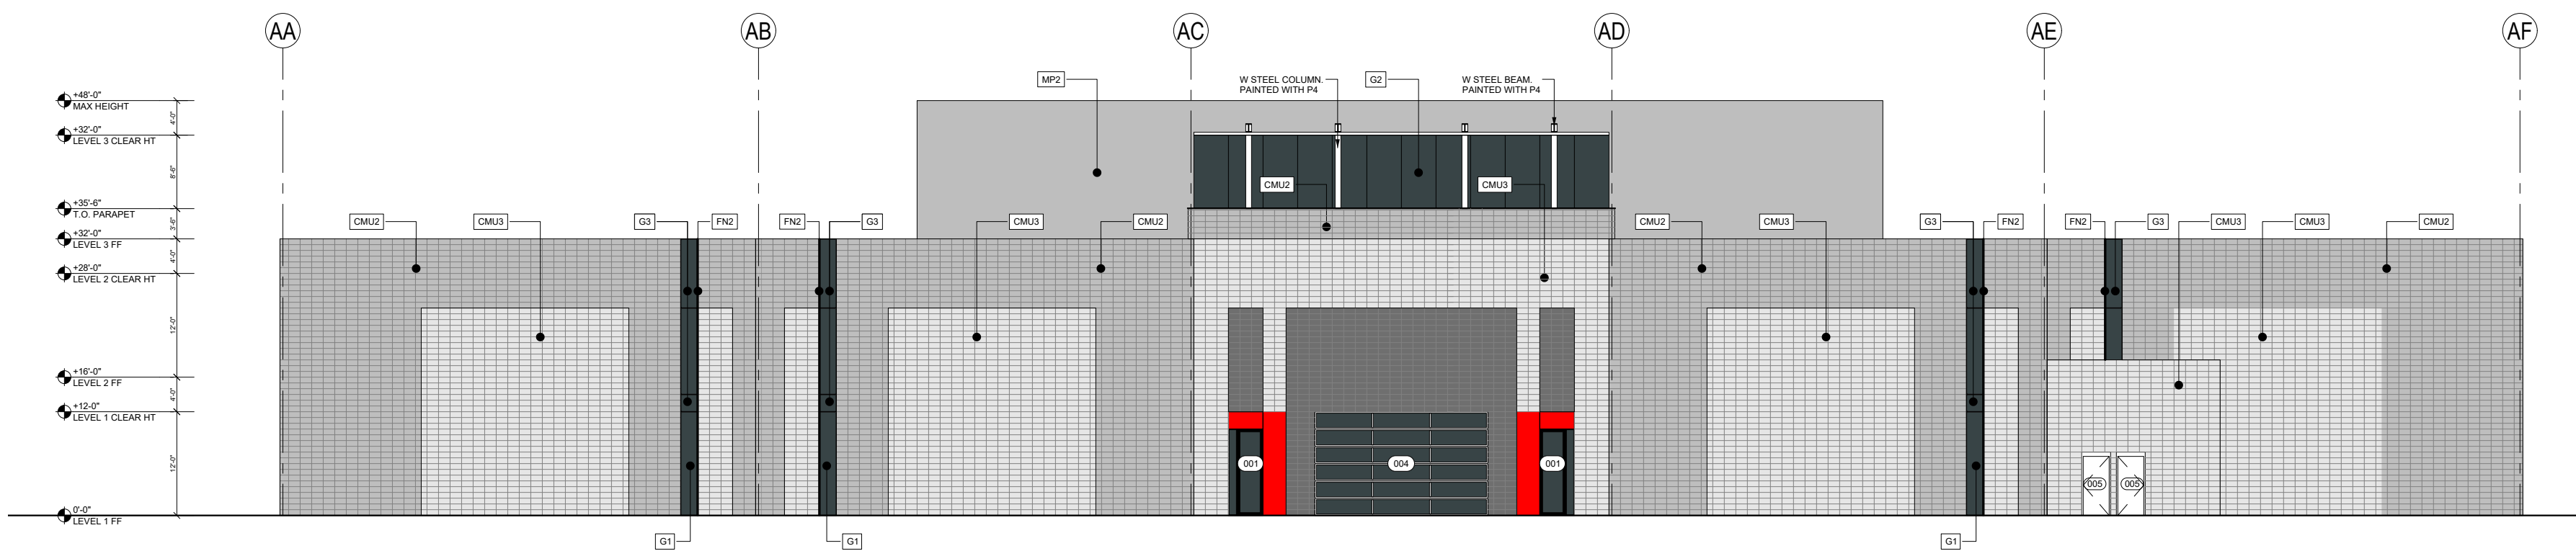

02 WEST ELEVATION - BUILDING A
SCALE: 1/16" = 1'-0"

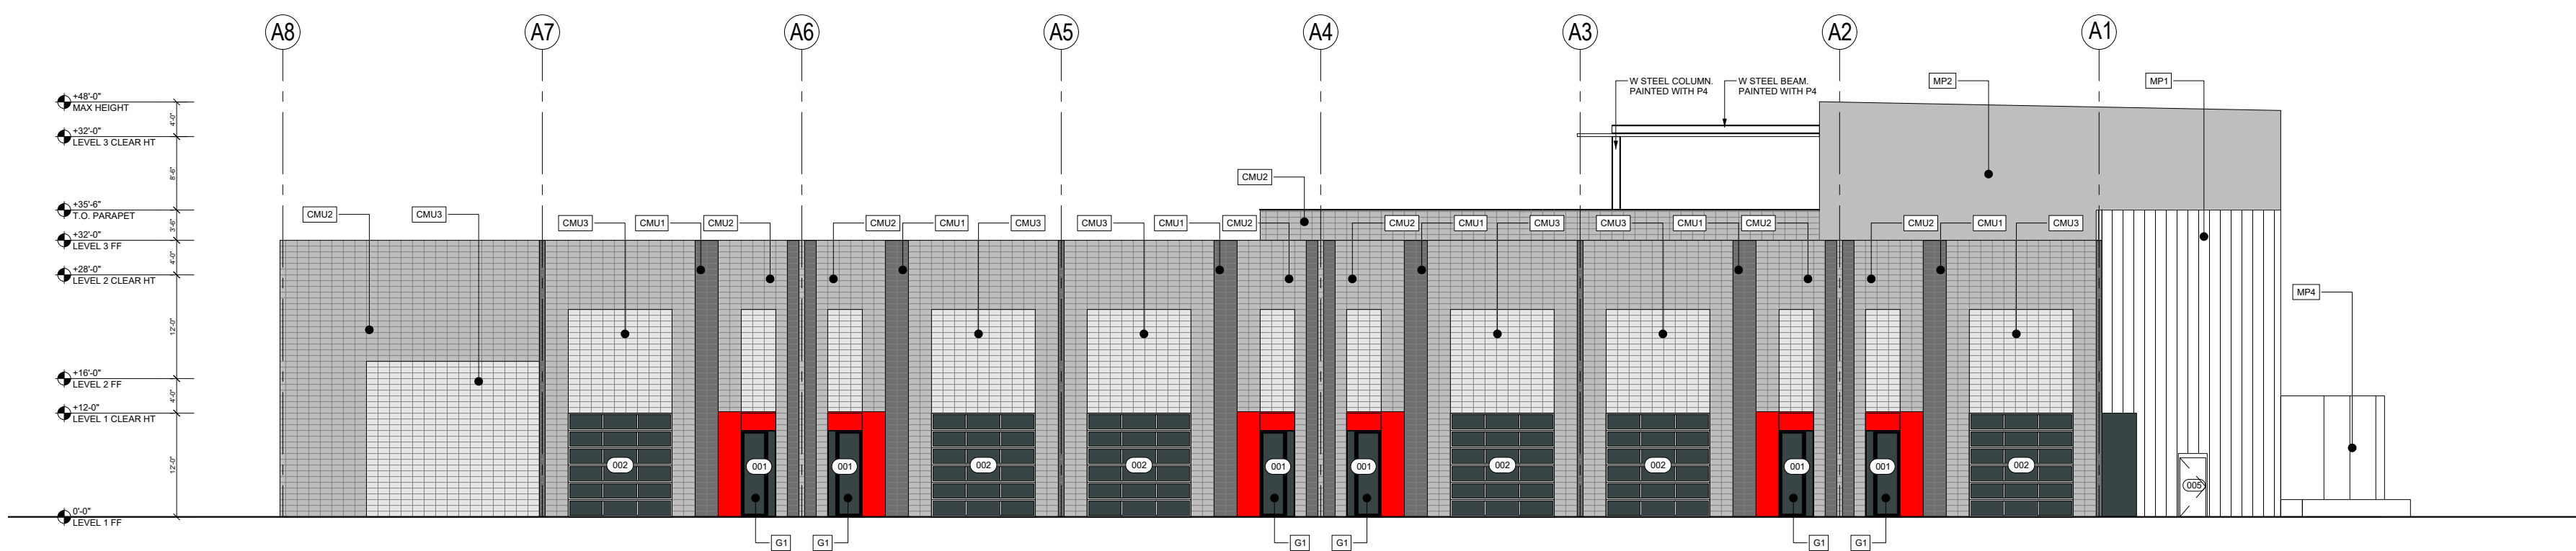

01 SOUTH ELEVATION - BUILDING A
SCALE: 1/16" = 1'-0"

EXTERIOR MATERIAL KEY

- MP1** LIGHT GREY PERFORATED AND CORRUGATED METAL PANEL - MI-2810 WHITE SILVER, VISAGE
- MP2** DARK METAL PANEL - MI-2011 DARK GREY: COLOR, VISAGE BY LUMABUILT
- MP3** RED METAL PANEL (INNER ENTRY CANOPY). SL-1852 CARDINAL RED, VISAGE BY LUMABUILT
- MP4** LIGHT GREY METAL PANEL (OUTER ENTRY CANOPY). MI-2810 WHITE SILVER, VISAGE BY LUMABUILT
- MP5** DARK CORRUGATED METAL PANEL - MI-2011 DARK GREY: COLOR, VISAGE BY LUMABUILT

- CMU1** 8"x8"x16" CMU
SMOOTH FACE STACK BOND INTEGRAL COLOR MASONRY
COLOR: "BLACK CANYON" BY SUPERLITE
- CMU2** 8"x8"x16" CMU
SMOOTH FACE STACK BOND INTEGRAL COLOR MASONRY
COLOR: "PEBBLE BEACH" BY SUPERLITE
- CMU3** 8"x8"x16" CMU
SMOOTH FACE STACK BOND INTEGRAL COLOR MASONRY
COLOR: "MALIBU SAND" BY SUPERLITE
- CMU4** 8"x8"x16" CMU
SCORED SPLIT FACE STACK BOND INTEGRAL COLOR MASONRY
COLOR: "BLACK CANYON" BY SUPERLITE

PAINT

- P1** **PAINT KEY:**
DUN EDWARDS COLD MORNING DE6365
- P2** DUNN EDWARDS COVERED IN PLATINUM DE6367
- P3** DUNN EDWARDS DARK GRAY DEGR60
- P4** DUN EDWARDS BLACK DEA002
- P5** DUNN EDWARDS RED POWER DEA108

MISC. ARCHITECTURAL ELEMENTS

- FN1** VERTICAL LOUVERS
ANODIZED ALUMINUM FINS, 1.5" WIDE X 8" DEEP
- FN2** VERTICAL LOUVERS
ANODIZED BLACK ([P4]) ALUMINUM FINS 1.5" WIDE X 8" DEEP


FINISH LINE AUTO CLUB

UPDATE
PRICING SET
NOT TO BE USED
FOR CONSTRUCTION


SHEET TITLE: ELEVATIONS - BUILDING A	
ISSUE DATE:	03/25/25
DRAWN BY:	AE
CHECKED BY:	RH
PROJECT No.:	000000

SHEET:


A4.1A

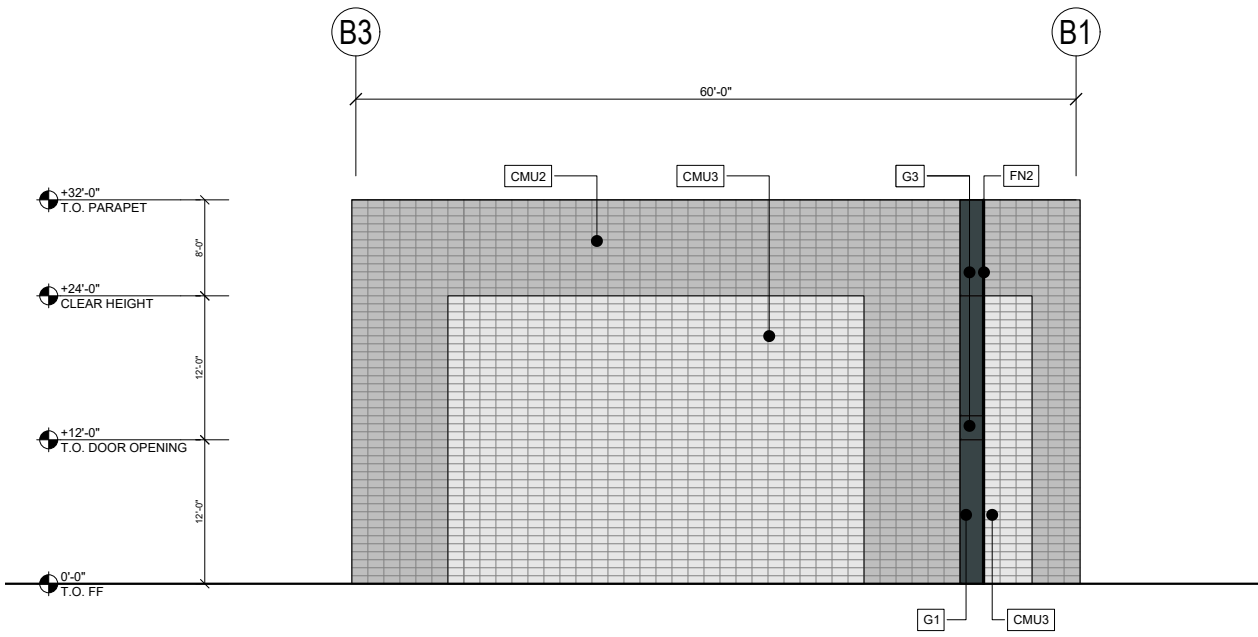


04 SOUTH ELEVATION - BUILDING B
SCALE: 1/16" = 1'-0"

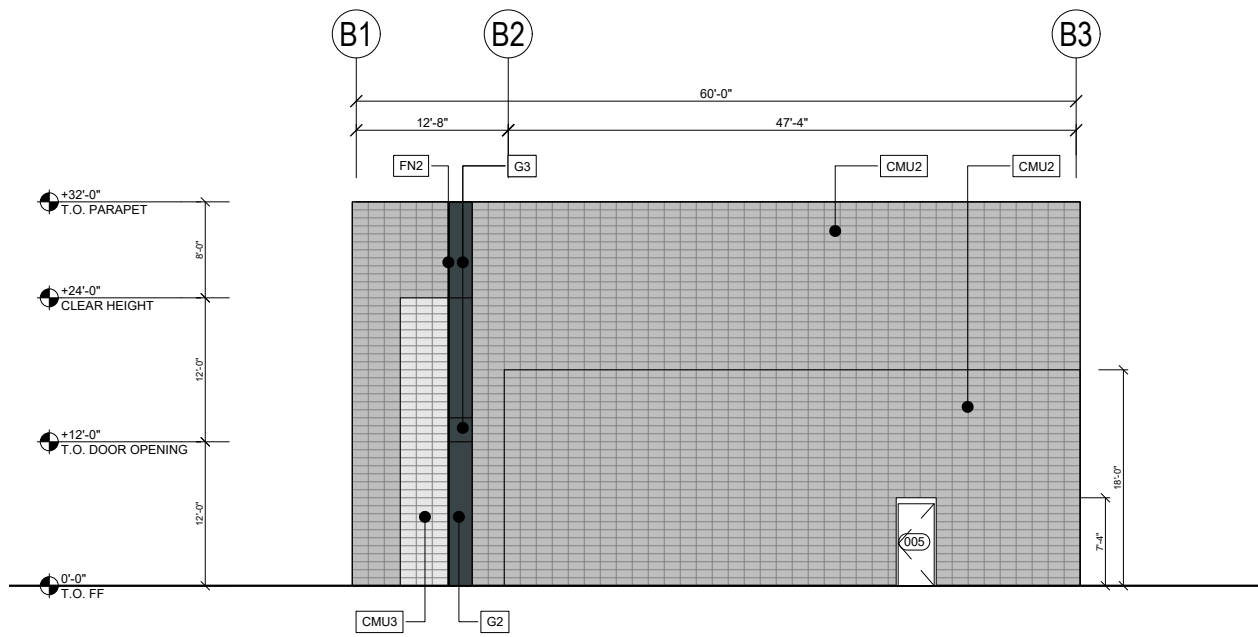

03 NORTH ELEVATION - BUILDING B
SCALE: 1/16" = 1'-0"

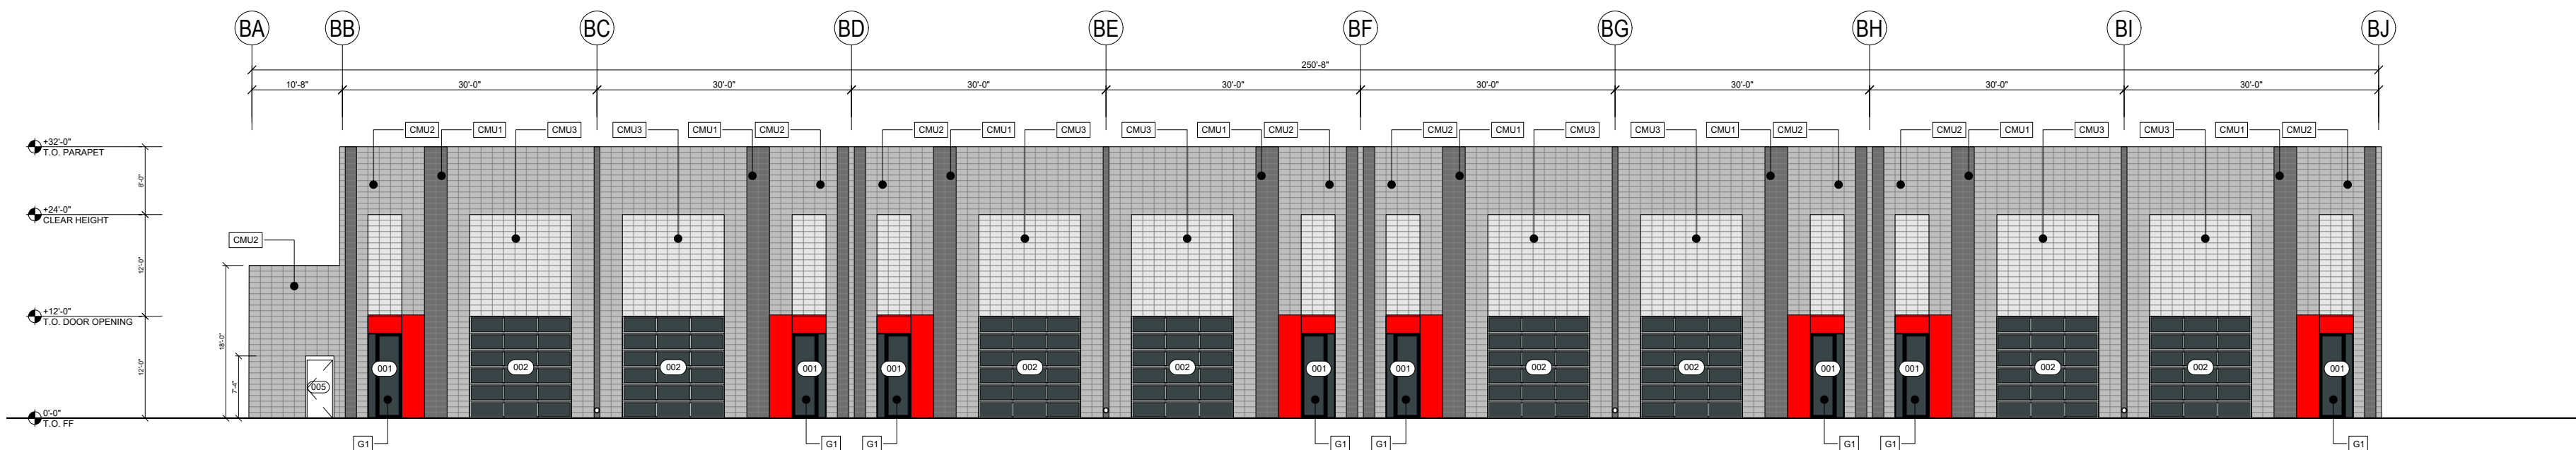

02 WEST ELEVATION - BUILDING B
SCALE: 1/16" = 1'-0"

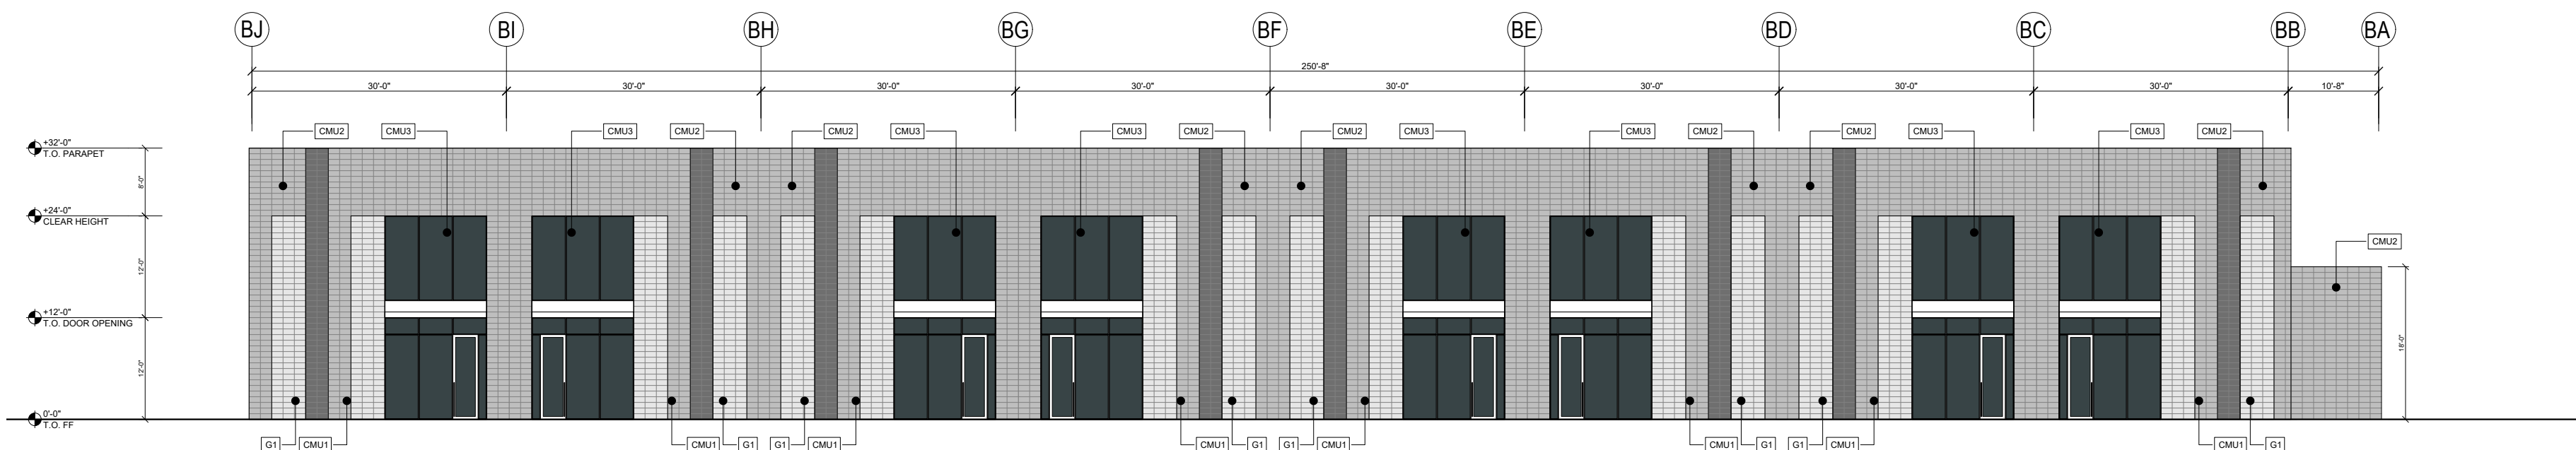

01 EAST ELEVATION - BUILDING B
SCALE: 1/16" = 1'-0"

EXTERIOR MATERIAL KEY

- MP1 LIGHT GREY PERFORATED AND CORRUGATED METAL PANEL - MI-2810 WHITE SILVER, VISAGE
- MP2 DARK METAL PANEL - MI-2011 DARK GREY: COLOR, VISAGE BY LUMABUILT
- MP3 RED METAL PANEL (INNER ENTRY CANOPY). SL-1852 CARDINAL RED, VISAGE BY LUMABUILT
- MP4 LIGHT GREY METAL PANEL (OUTER ENTRY CANOPY). MI-2810 WHITE SILVER, VISAGE BY LUMABUILT
- MP5 DARK CORRUGATED METAL PANEL - MI-2011 DARK GREY: COLOR, VISAGE BY LUMABUILT

- CMU1 8"x8"x16" CMU
SMOOTH FACE STACK BOND INTEGRAL COLOR MASONRY
COLOR: "BLACK CANYON" BY SUPERLITE
- CMU2 8"x8"x16" CMU
SMOOTH FACE STACK BOND INTEGRAL COLOR MASONRY
COLOR: "PEBBLE BEACH" BY SUPERLITE
- CMU3 8"x8"x16" CMU
SMOOTH FACE STACK BOND INTEGRAL COLOR MASONRY
COLOR: "MALIBU SAND" BY SUPERLITE
- CMU4 8"x8"x16" CMU
SCORED SPLIT FACE STACK BOND INTEGRAL COLOR MASONRY
COLOR: "BLACK CANYON" BY SUPERLITE


PAINT

- P1 PAINT KEY:
DUN EDWARDS COLD MORNING DE6365
- P2 DUNN EDWARDS COVERED IN PLATINUM DE6367
- P3 DUNN EDWARDS DARK GRAY DEGR60
- P4 DUN EDWARDS BLACK DEA002
- P5 DUNN EDWARDS RED POWER DEA108


MISC. ARCHITECTURAL ELEMENTS

- FN1 VERTICAL LOUVERS
ANODIZED ALUMINUM FINS, 1.5" WIDE X 8" DEEP
- FN2 VERTICAL LOUVERS
ANODIZED BLACK ([P4]) ALUMINUM FINS 1.5" WIDE X 8" DEEP


FINISH LINE AUTO CLUB

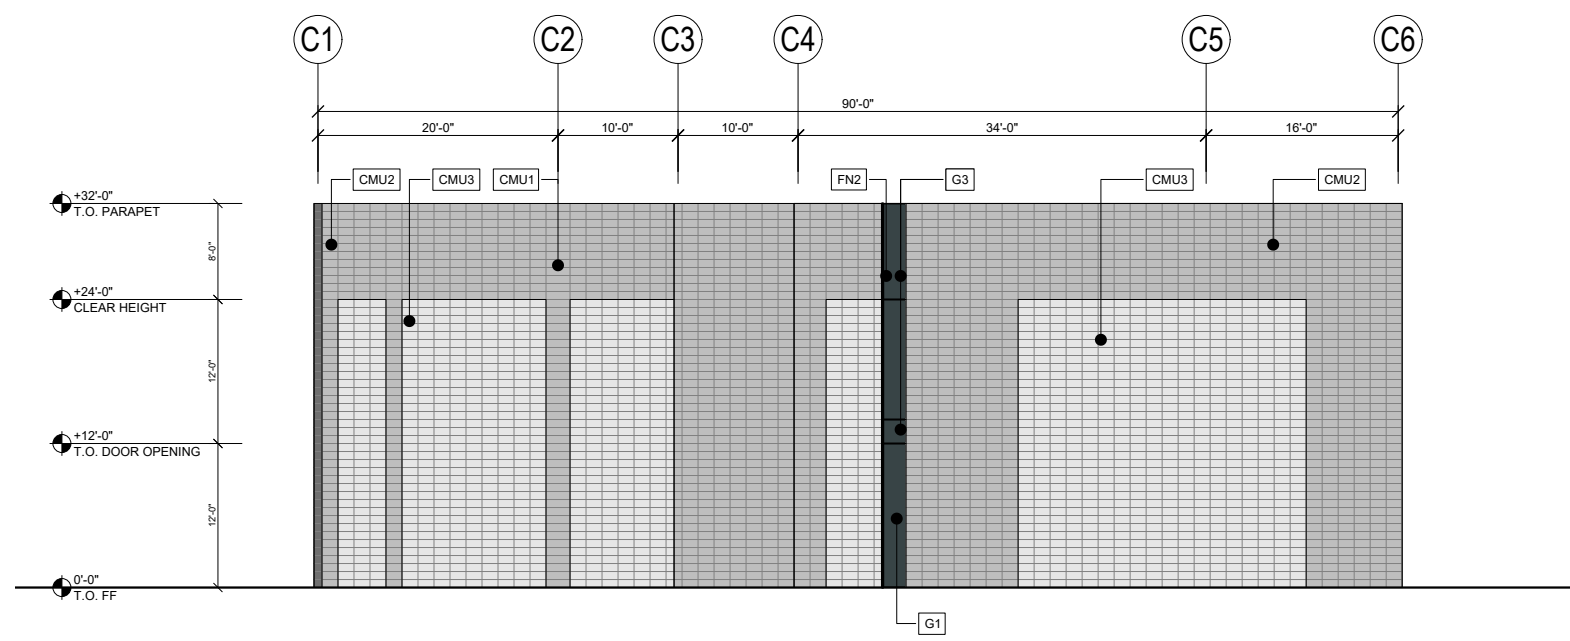


01 SOUTH ELEVATION - BUILDING C
SCALE: 1/16" = 1'-0"

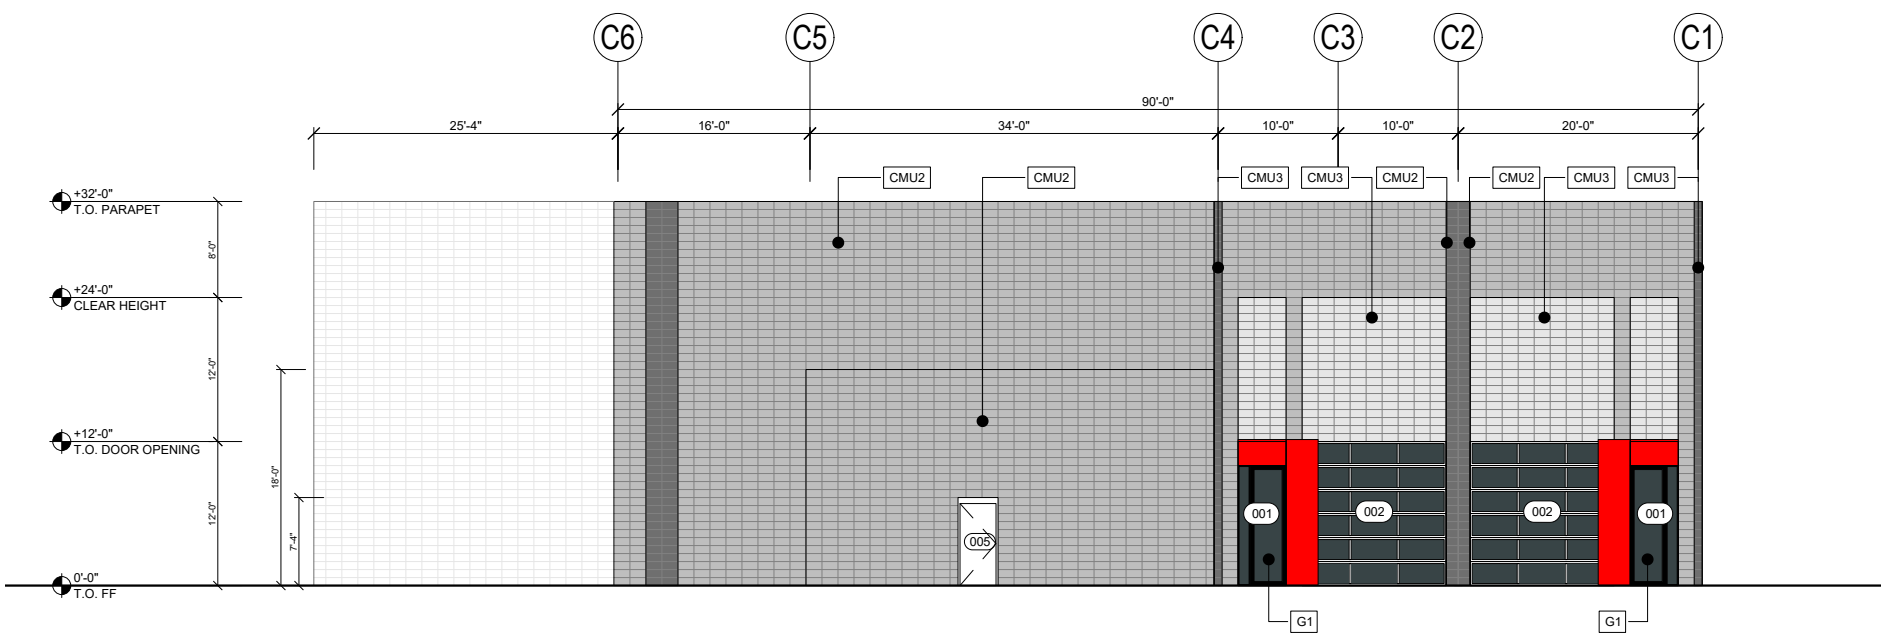

03 NORTH ELEVATION - BUILDING C
SCALE: 1/16" = 1'-0"

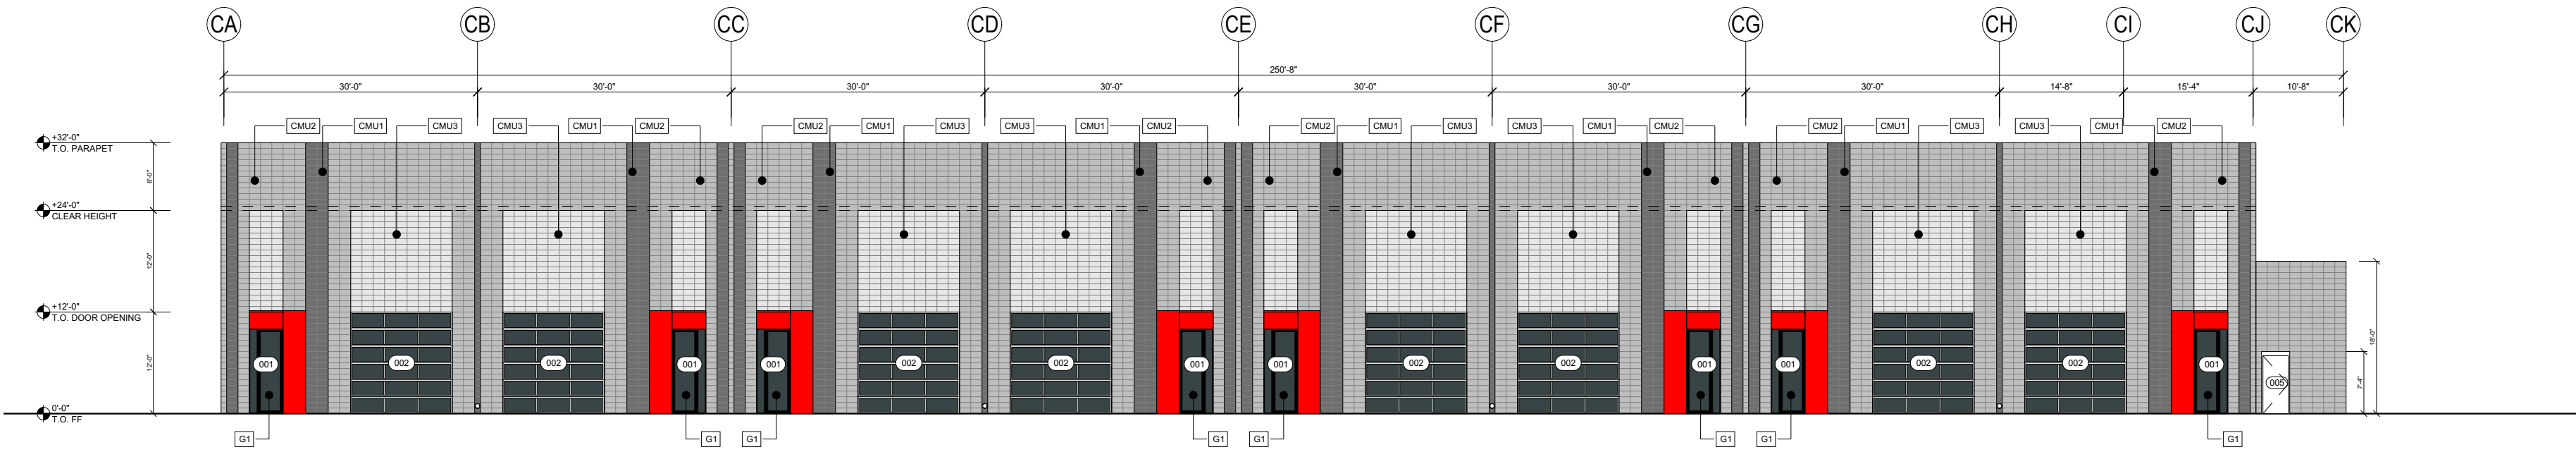

02 EAST ELEVATION - BUILDING C
SCALE: 1/16" = 1'-0"

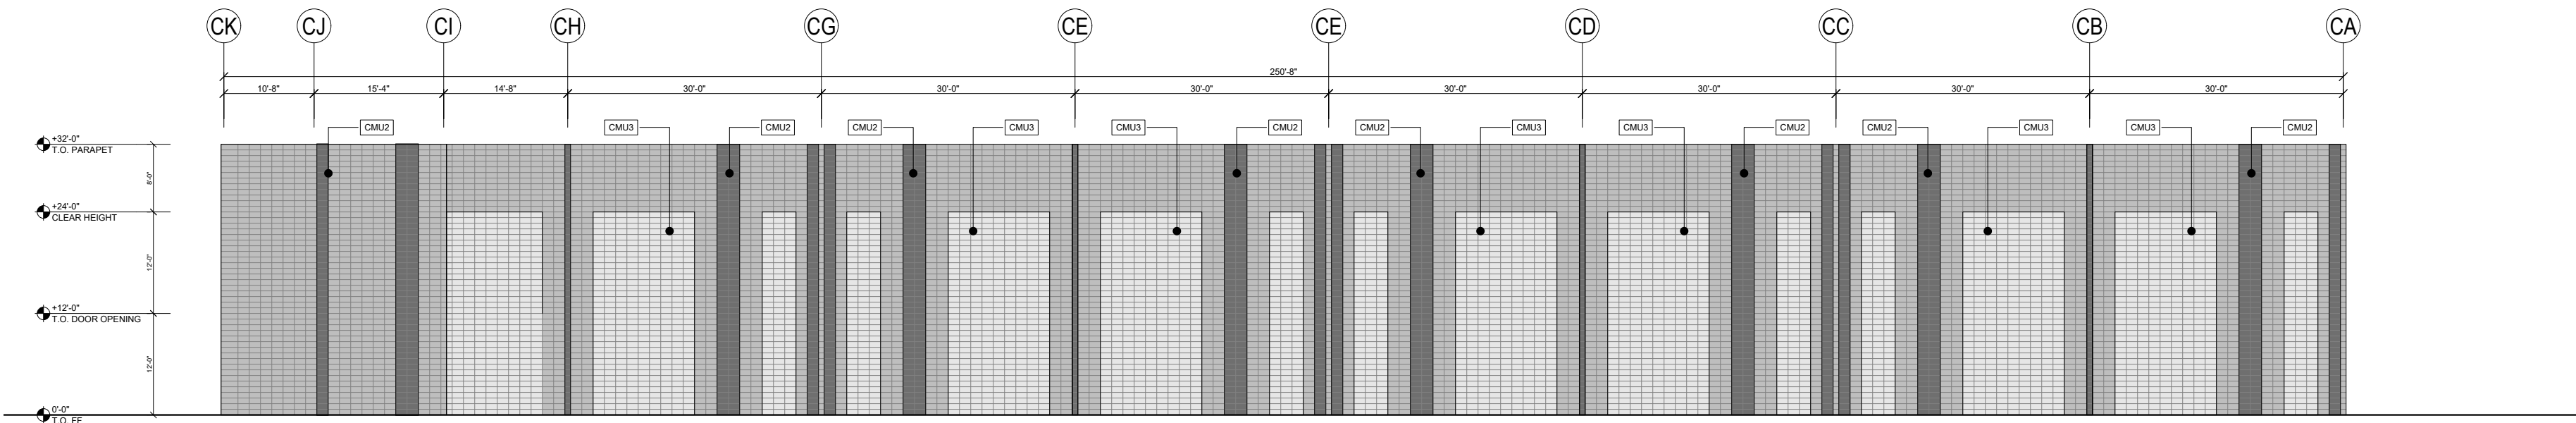

01 WEST ELEVATION - BUILDING C
SCALE: 1/16" = 1'-0"

EXTERIOR MATERIAL KEY

- MP1 LIGHT GREY PERFORATED AND CORRUGATED METAL PANEL. MI-2810 WHITE SILVER, VISAGE
- MP2 DARK METAL PANEL - MI-2011 DARK GREY: COLOR, VISAGE BY LUMABUILT
- MP3 RED METAL PANEL (INNER ENTRY CANOPY). SL-1852 CARDINAL RED, VISAGE BY LUMABUILT
- MP4 LIGHT GREY METAL PANEL (OUTER ENTRY CANOPY). MI-2810 WHITE SILVER, VISAGE BY LUMABUILT
- MP5 DARK CORRUGATED METAL PANEL - MI-2011 DARK GREY: COLOR, VISAGE BY LUMABUILT

- CMU1 8"x8"x16" CMU
SMOOTH FACE STACK BOND INTEGRAL COLOR MASONRY
COLOR: "BLACK CANYON" BY SUPERLITE
- CMU2 8"x8"x16" CMU
SMOOTH FACE STACK BOND INTEGRAL COLOR MASONRY
COLOR: "PEBBLE BEACH" BY SUPERLITE
- CMU3 8"x8"x16" CMU
SMOOTH FACE STACK BOND INTEGRAL COLOR MASONRY
COLOR: "MALIBU SAND" BY SUPERLITE
- CMU4 8"x8"x16" CMU
SCORED SPLIT FACE STACK BOND INTEGRAL COLOR
MASONRY
COLOR: "BLACK CANYON" BY SUPERLITE


PAINT

- P1 PAINT KEY:
DUN EDWARDS COLD MORNING DE6365
- P2 DUNN EDWARDS COVERED IN PLATINUM DE6367
- P3 DUNN EDWARDS DARK GRAY DEGR60
- P4 DUN EDWARDS BLACK DEA002
- P5 DUNN EDWARDS RED POWER DEA108


MISC. ARCHITECTURAL ELEMENTS

- FN1 VERTICAL LOUVERS
ANODIZED ALUMINUM FINS, 1.5" WIDE X 8" DEEP
- FN2 VERTICAL LOUVERS
ANODIZED BLACK ([P4]) ALUMINUM FINS 1.5" WIDE X 8" DEEP


FINISH LINE AUTO CLUB

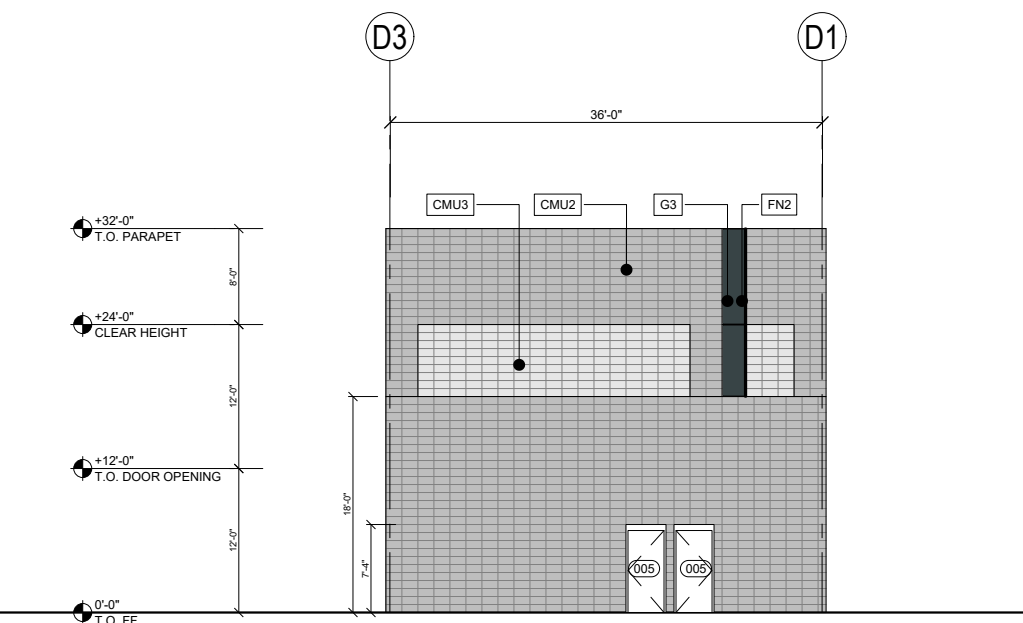


04 SOUTH ELEVATION - BUILDING D
SCALE: 1/16" = 1'-0"

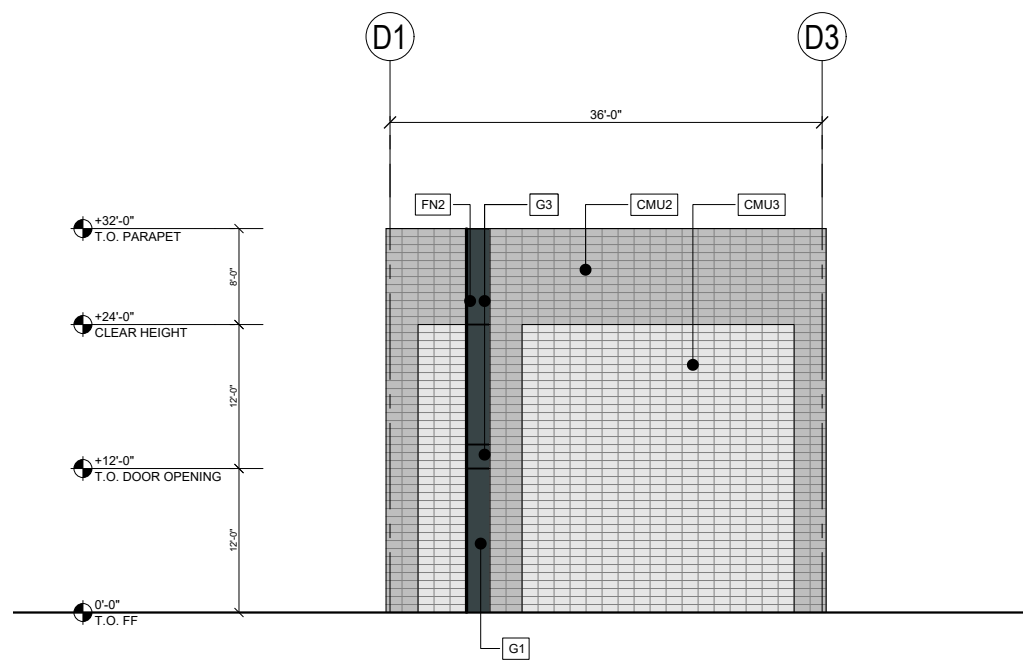

03 NORTH ELEVATION - BUILDING D
SCALE: 1/16" = 1'-0"

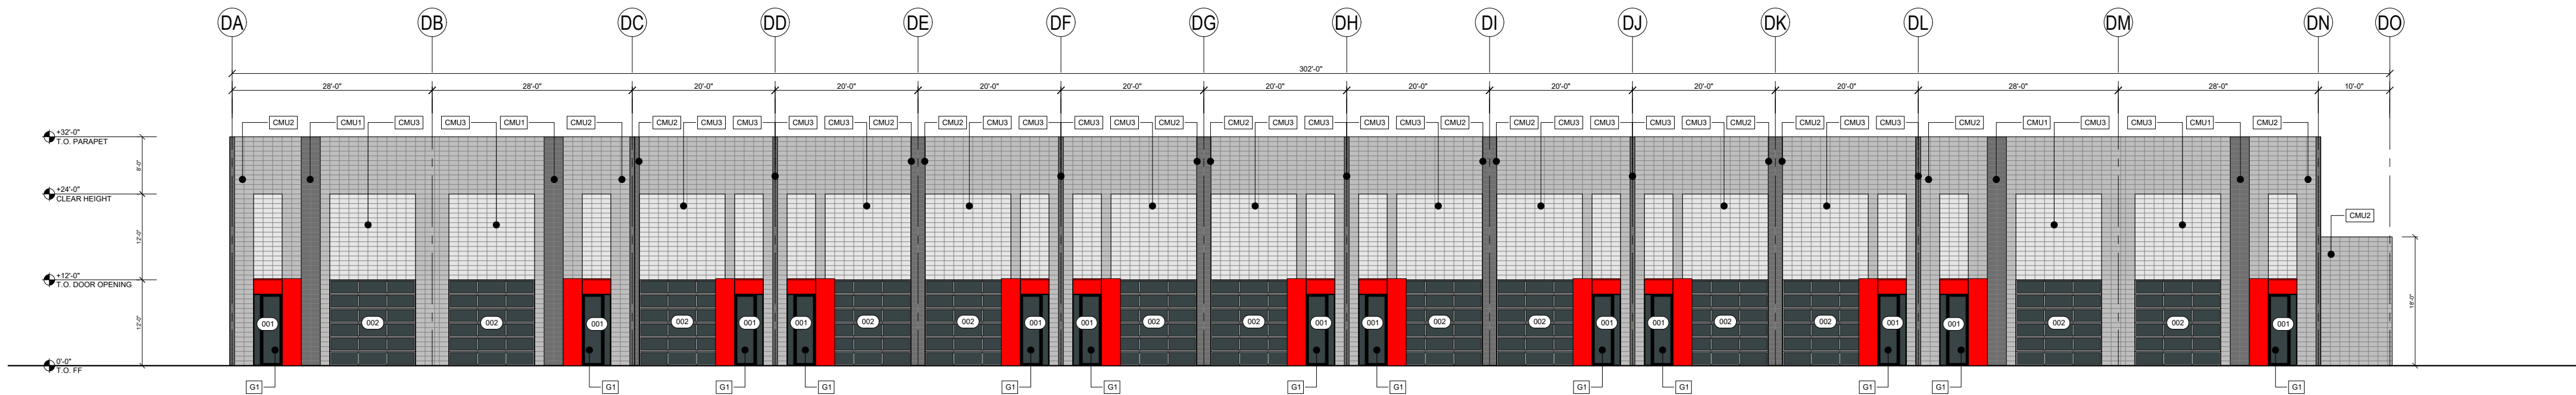

02 WEST ELEVATION - BUILDING D
SCALE: 1/16" = 1'-0"

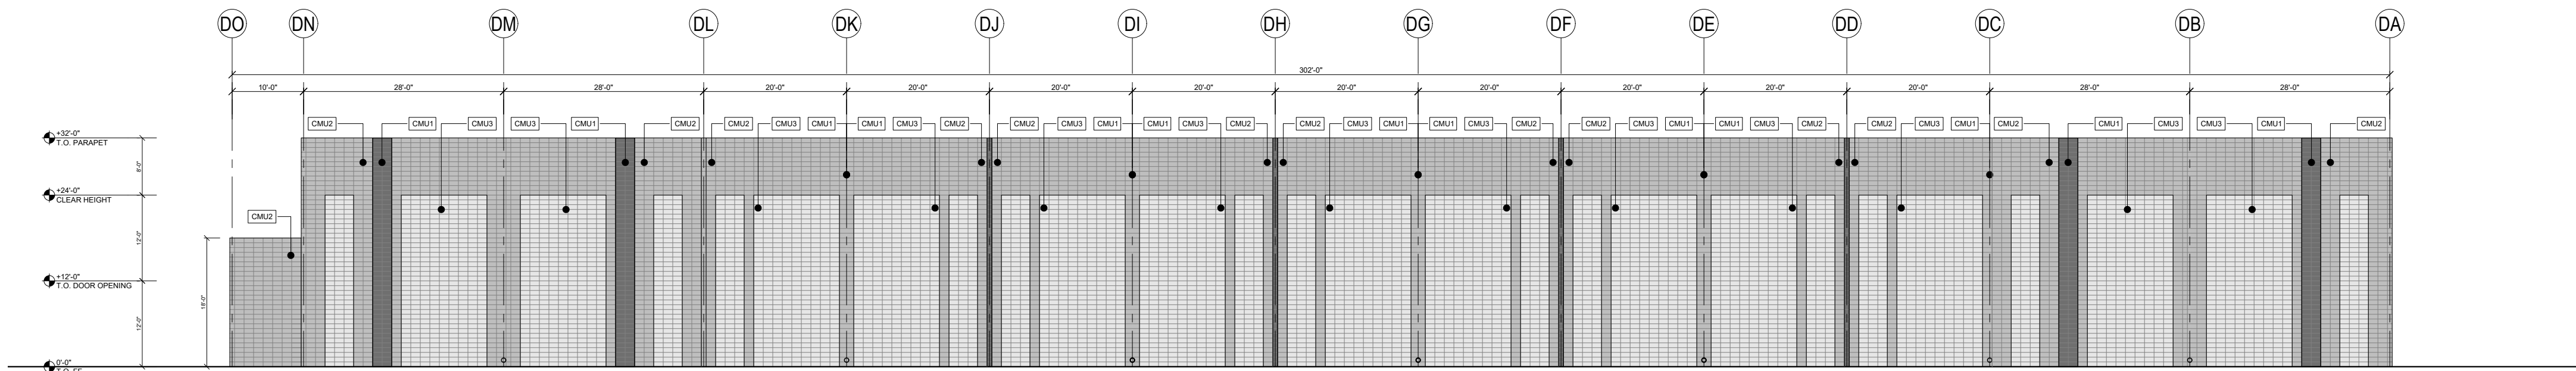

01 EAST ELEVATION - BUILDING D
SCALE: 1/16" = 1'-0"

EXTERIOR MATERIAL KEY

- MP1** LIGHT GREY PERFORATED AND CORRUGATED METAL PANEL - MI-2810 WHITE SILVER, VISAGE
- MP2** DARK METAL PANEL - MI-2011 DARK GREY: COLOR, VISAGE BY LUMABUILT
- MP3** RED METAL PANEL (INNER ENTRY CANOPY). SL-1852 CARDINAL RED, VISAGE BY LUMABUILT
- MP4** LIGHT GREY METAL PANEL (OUTER ENTRY CANOPY). MI-2810 WHITE SILVER, VISAGE BY LUMABUILT
- MP5** DARK CORRUGATED METAL PANEL - MI-2011 DARK GREY: COLOR, VISAGE BY LUMABUILT


- CMU1** 8"x8"x16" CMU
SMOOTH FACE STACK BOND INTEGRAL COLOR MASONRY
COLOR: "BLACK CANYON" BY SUPERLITE
- CMU2** 8"x8"x16" CMU
SMOOTH FACE STACK BOND INTEGRAL COLOR MASONRY
COLOR: "PEBBLE BEACH" BY SUPERLITE
- CMU3** 8"x8"x16" CMU
SMOOTH FACE STACK BOND INTEGRAL COLOR MASONRY
COLOR: "MALIBU SAND" BY SUPERLITE
- CMU4** 8"x8"x16" CMU
SCORED SPLIT FACE STACK BOND INTEGRAL COLOR MASONRY
COLOR: "BLACK CANYON" BY SUPERLITE

PAINT


- P1** **PAINT KEY:**
DUN EDWARDS COLD MORNING DE6365
- P2** DUNN EDWARDS COVERED IN PLATINUM DE6367
- P3** DUNN EDWARDS DARK GRAY DEGR60
- P4** DUN EDWARDS BLACK DEA002
- P5** DUNN EDWARDS RED POWER DEA108

MISC. ARCHITECTURAL ELEMENTS


- FN1** VERTICAL LOUVERS
ANODIZED ALUMINUM FINS, 1.5" WIDE X 8" DEEP
- FN2** VERTICAL LOUVERS
ANODIZED BLACK ([P4]) ALUMINUM FINS 1.5" WIDE X 8" DEEP

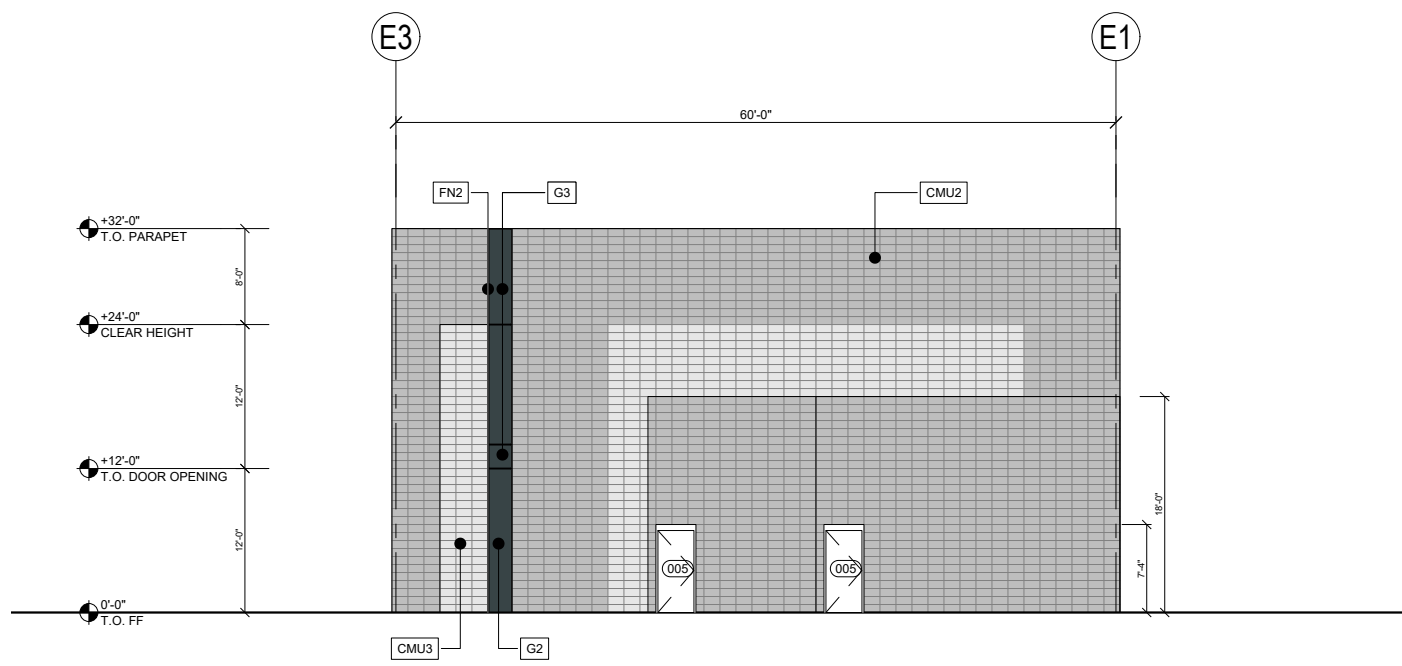


04 EAST ELEVATION - BUILDING E
SCALE: 1/16" = 1'-0"

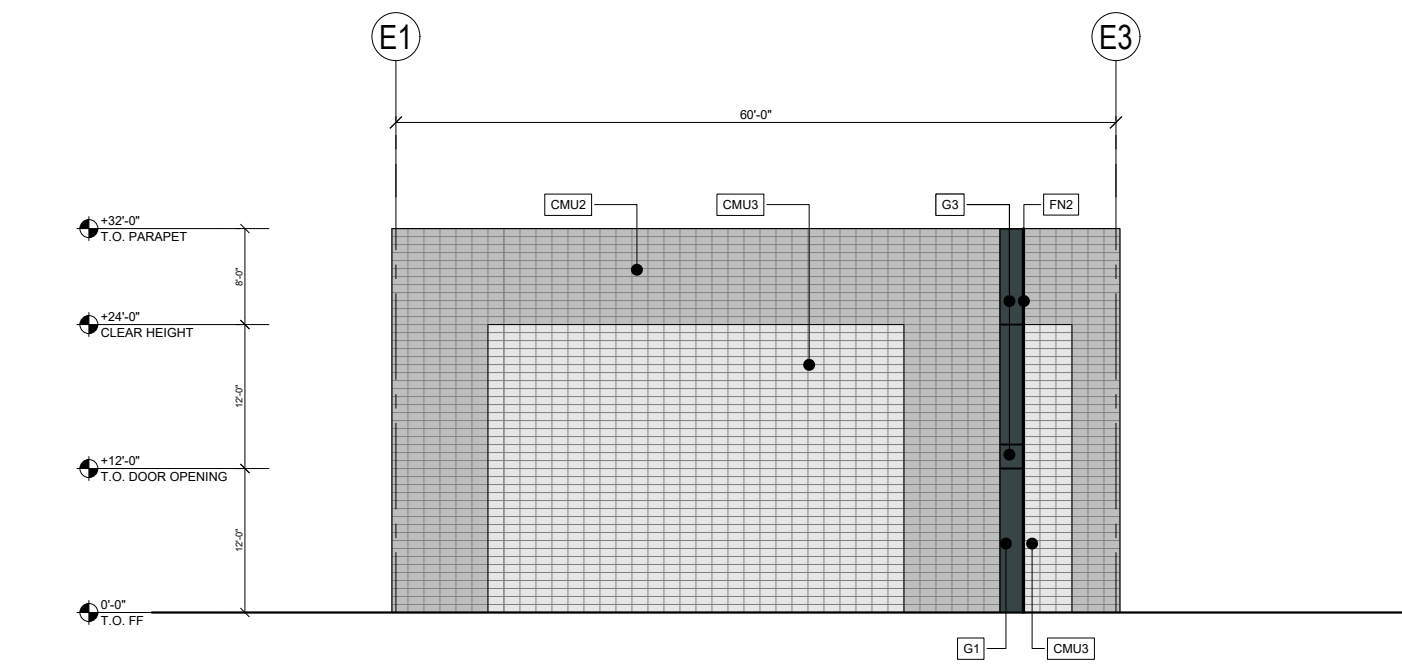

03 WEST ELEVATION - BUILDING E
SCALE: 1/16" = 1'-0"

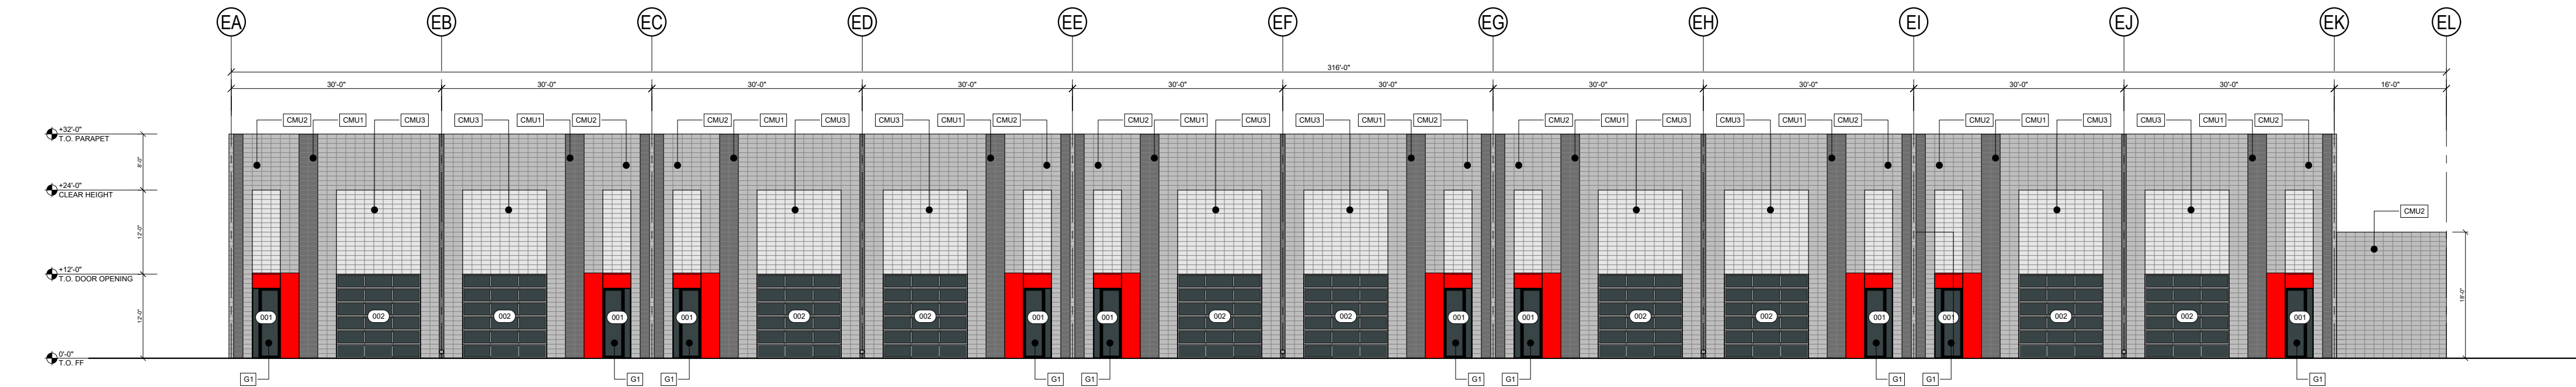

02 SOUTH ELEVATION - BUILDING E
SCALE: 1/16" = 1'-0"

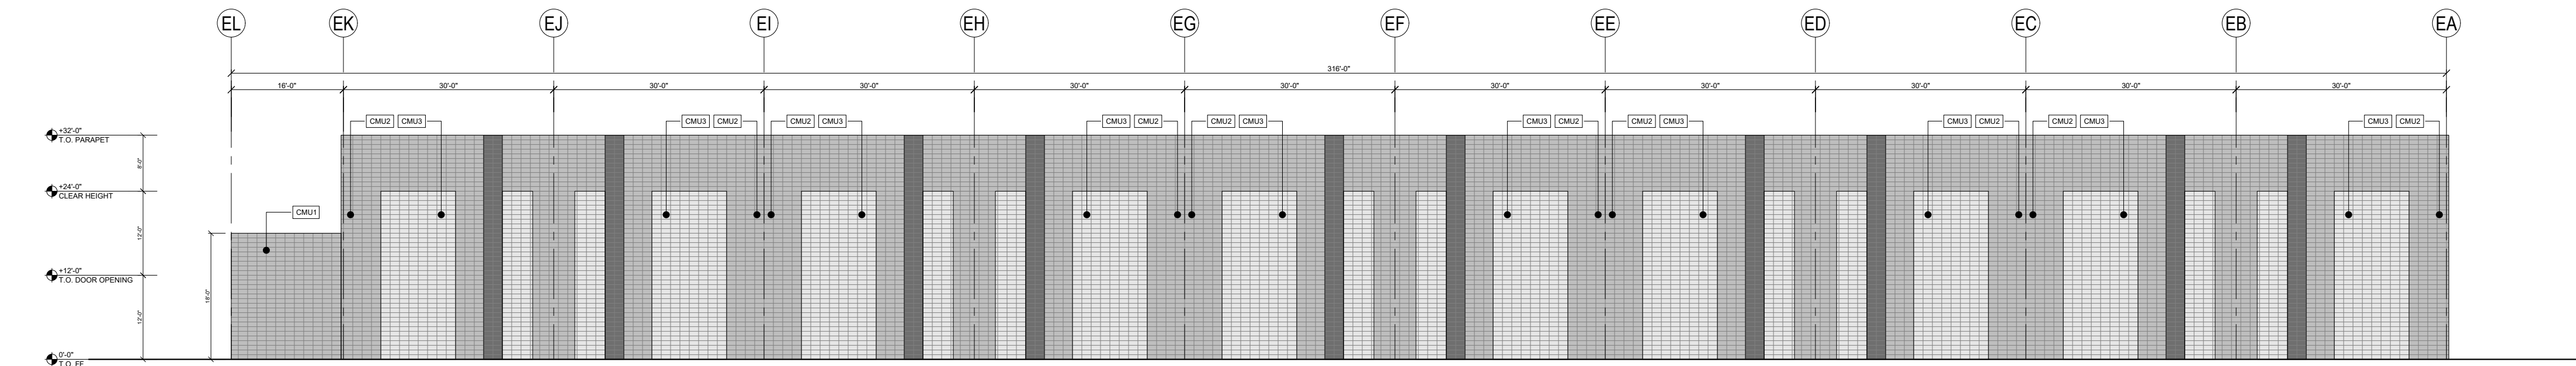

01 NORTH ELEVATION - BUILDING E
SCALE: 1/16" = 1'-0"

EXTERIOR MATERIAL KEY

- MP1 LIGHT GREY PERFORATED AND CORRUGATED METAL PANEL. MI-2810 WHITE SILVER, VISAGE
- MP2 DARK METAL PANEL - MI-2011 DARK GREY: COLOR, VISAGE BY LUMABUILT
- MP3 RED METAL PANEL (INNER ENTRY CANOPY). SL-1852 CARDINAL RED, VISAGE BY LUMABUILT
- MP4 LIGHT GREY METAL PANEL (OUTER ENTRY CANOPY). MI-2810 WHITE SILVER, VISAGE BY LUMABUILT
- MP5 DARK CORRUGATED METAL PANEL - MI-2011 DARK GREY: COLOR, VISAGE BY LUMABUILT

- CMU1 8"X8"x16" CMU
SMOOTH FACE STACK BOND INTEGRAL COLOR MASONRY
COLOR: "BLACK CANYON" BY SUPERLITE
- CMU2 8"X8"x16" CMU
SMOOTH FACE STACK BOND INTEGRAL COLOR MASONRY
COLOR: "PEBBLE BEACH" BY SUPERLITE
- CMU3 8"X8"x16" CMU
SMOOTH FACE STACK BOND INTEGRAL COLOR MASONRY
COLOR: "MALIBU SAND" BY SUPERLITE
- CMU4 8"X8"x16" CMU
SCORED SPLIT FACE STACK BOND INTEGRAL COLOR MASONRY
COLOR: "BLACK CANYON" BY SUPERLITE

PAINT

- P1 PAINT KEY:
DUN EDWARDS COLD MORNING DE6365
- P2 DUNN EDWARDS COVERED IN PLATINUM DE6367
- P3 DUNN EDWARDS DARK GRAY DEGR60
- P4 DUN EDWARDS BLACK DEA002
- P5 DUNN EDWARDS RED POWER DEA108

MISC. ARCHITECTURAL ELEMENTS

- FN1 VERTICAL LOUVERS
ANODIZED ALUMINUM FINIS, 1.5" WIDE X 8" DEEP
- FN2 VERTICAL LOUVERS
ANODIZED BLACK ([P4]) ALUMINUM FINIS 1.5" WIDE X 8" DEEP