


01 PLAN - BUILDING A

SCALE: 1/16" = 1'-0"

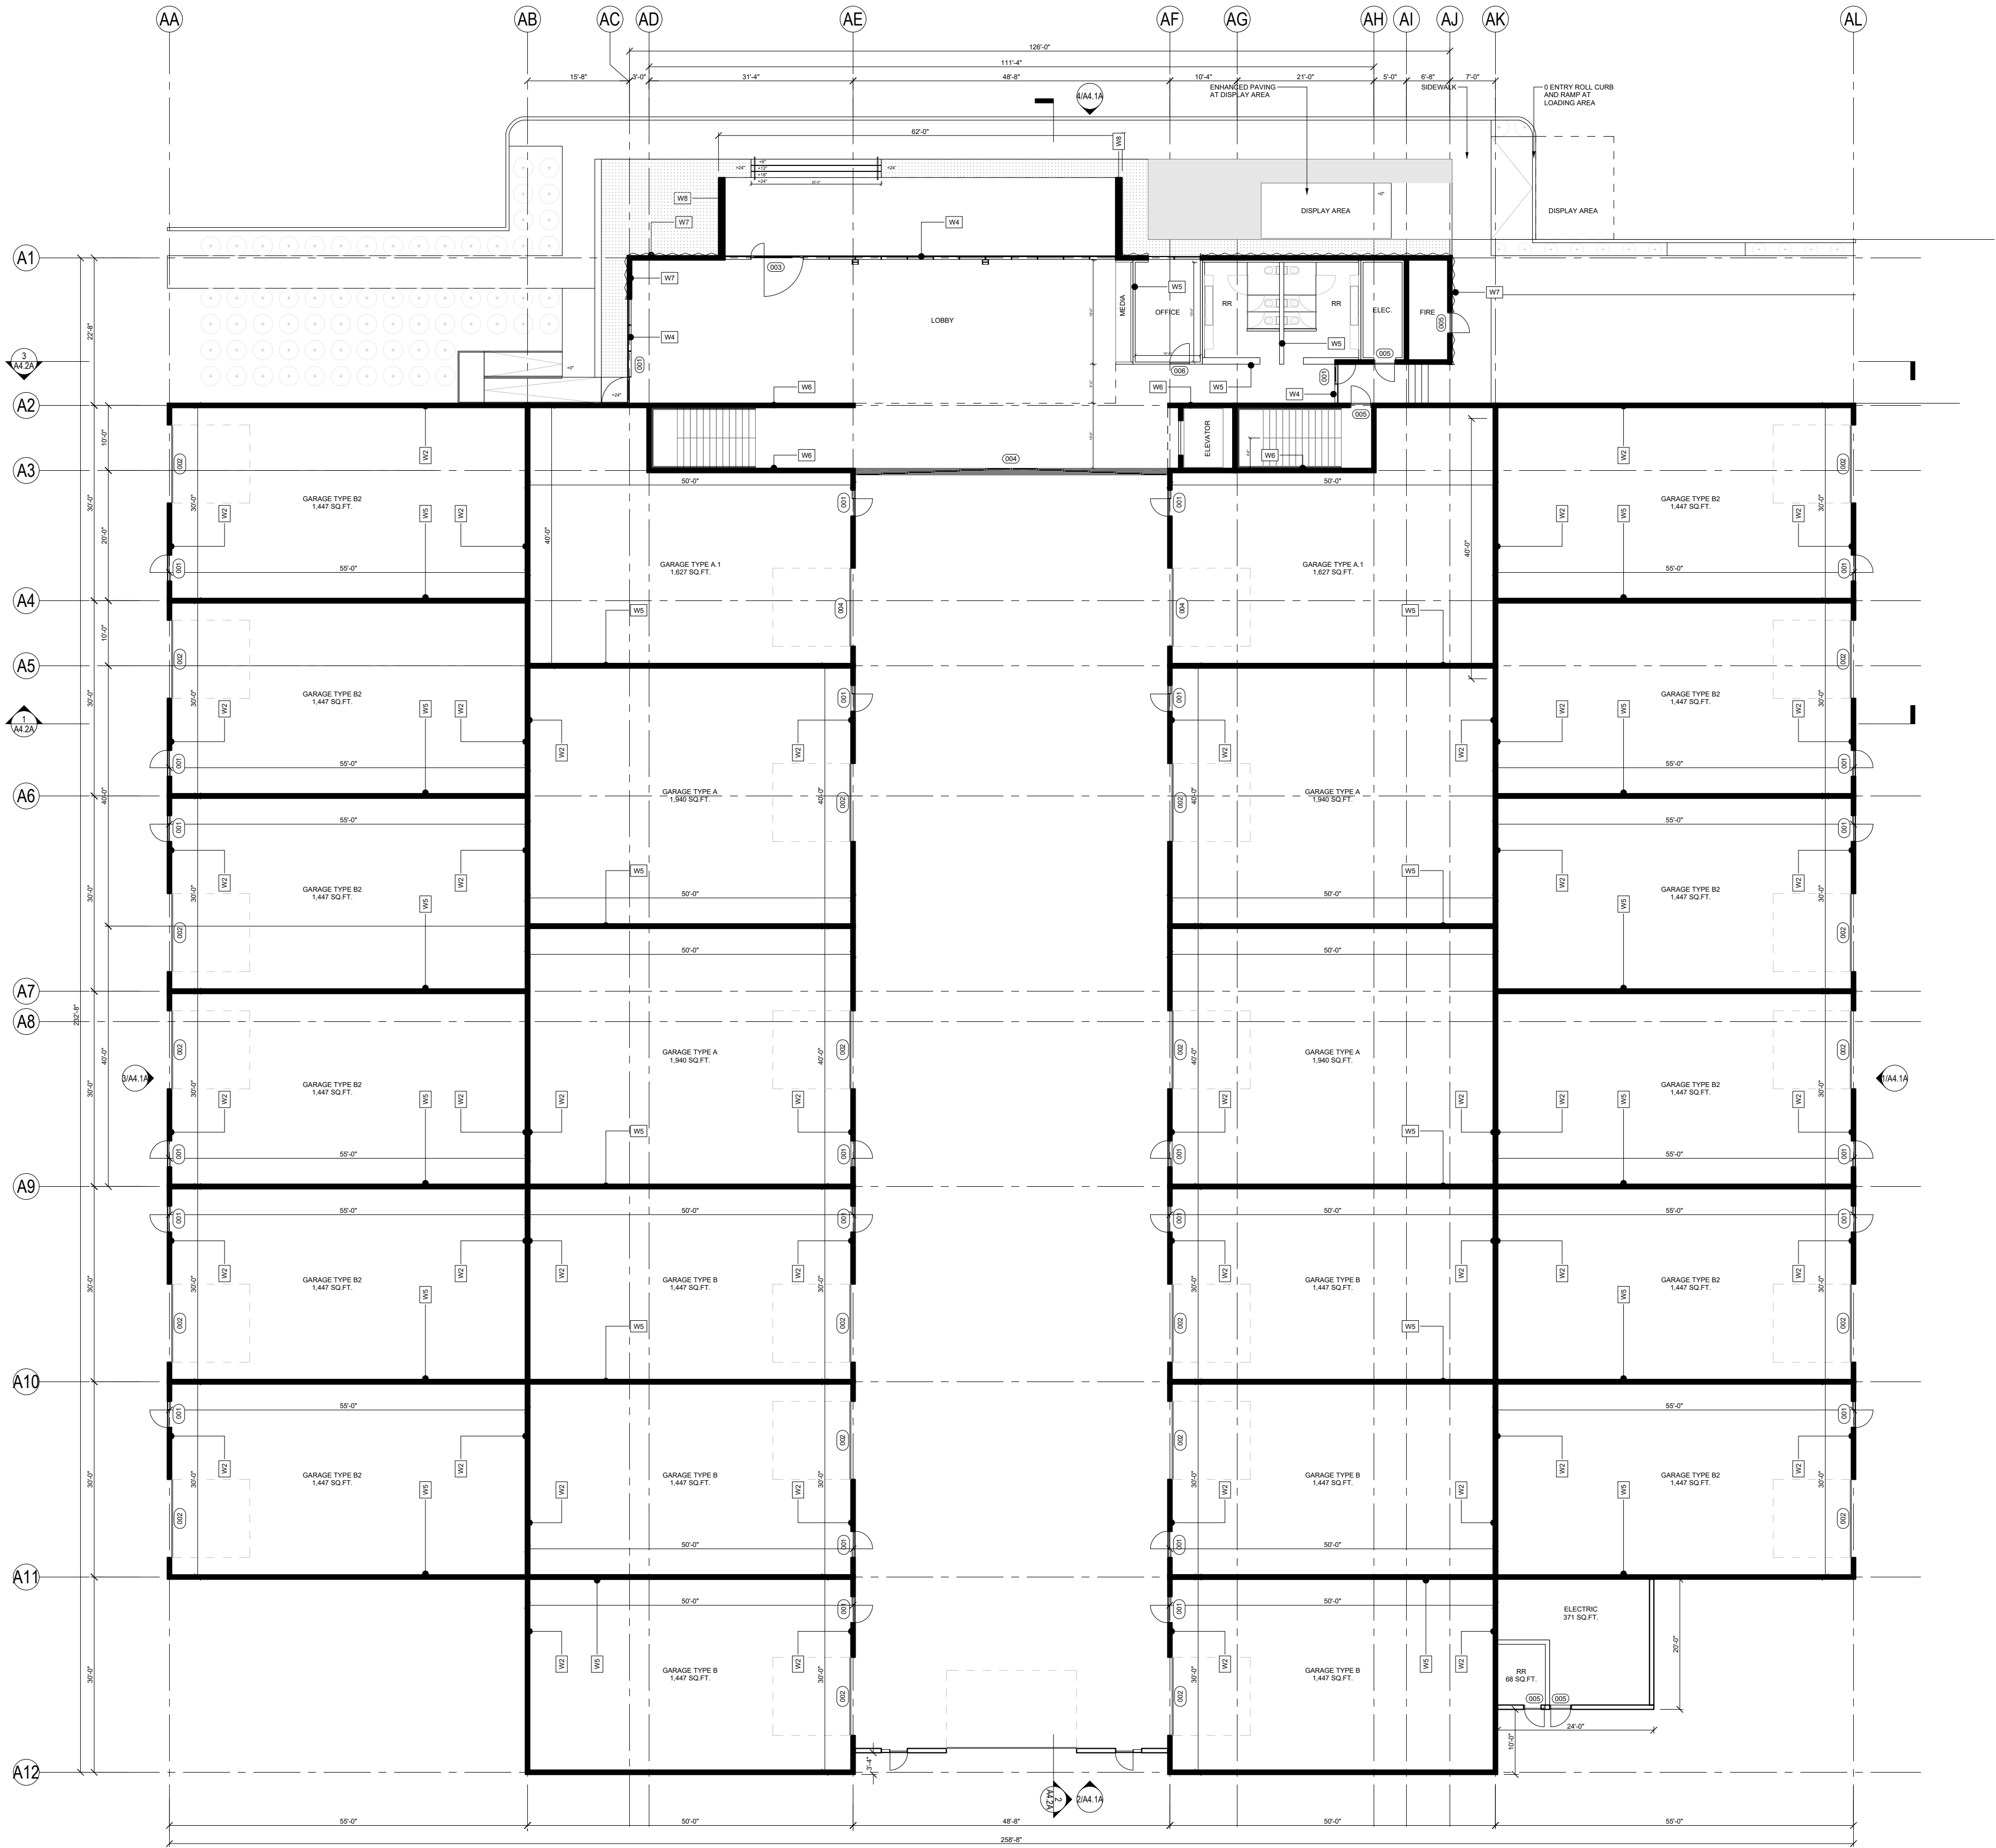

EXTERIOR WALLS

EXTERIOR WALL ASSEMBLY KEY:

- W1 METAL PANEL CLAD 8" CMU EXTERIOR WALL WITH [P1] PAINTED GYP INTERIOR
- W2 8" CMU EXTERIOR WALL WITH [P1] PAINTED GYP INTERIOR
- W3 EXTERIOR STEEL FRAME STOREFRONT, [P4] + [G1] FINISH.
- W4 GLASS CURTAIN WALL ASSEMBLY, NATURAL FINISH + [G2]
- W5 INTERIOR STEEL FRAME ASSEMBLY, GYP ON BOTH SIDES PAINTED WITH [P1]
- W6 8" CMU WALL UNFINISHED
- W7 PERFORATED METAL PANEL RAIN SCREEN CLAD 8" CMU EXTERIOR WALL WITH PAINTED GYP INTERIOR
- W8 METAL PANEL CLAD 8" CMU EXTERIOR WALL WITH [MP3] CLAD INTERIOR

FINISH LINE AUTO CLUB

LGE | DESIGNGROUP

1200 N. 52nd Street • Phoenix, AZ 85008

P. 480.966.4001

LGE | DESIGNBUILD

NUMBER REVISION DATE



UPDATE
PRICING SET
NOT TO BE USED
FOR CONSTRUCTION

SHEET TITLE:
PLAN - BUILDING A
ISSUE DATE: 03/25/25
DRAWN BY: AE
CHECKED BY: RH
PROJECT No.: 000000
SHEET:

A2.1A

01

PLAN - CLUBHOUSE LOWER LEVEL
SCALE: 1/8" = 1'-0"

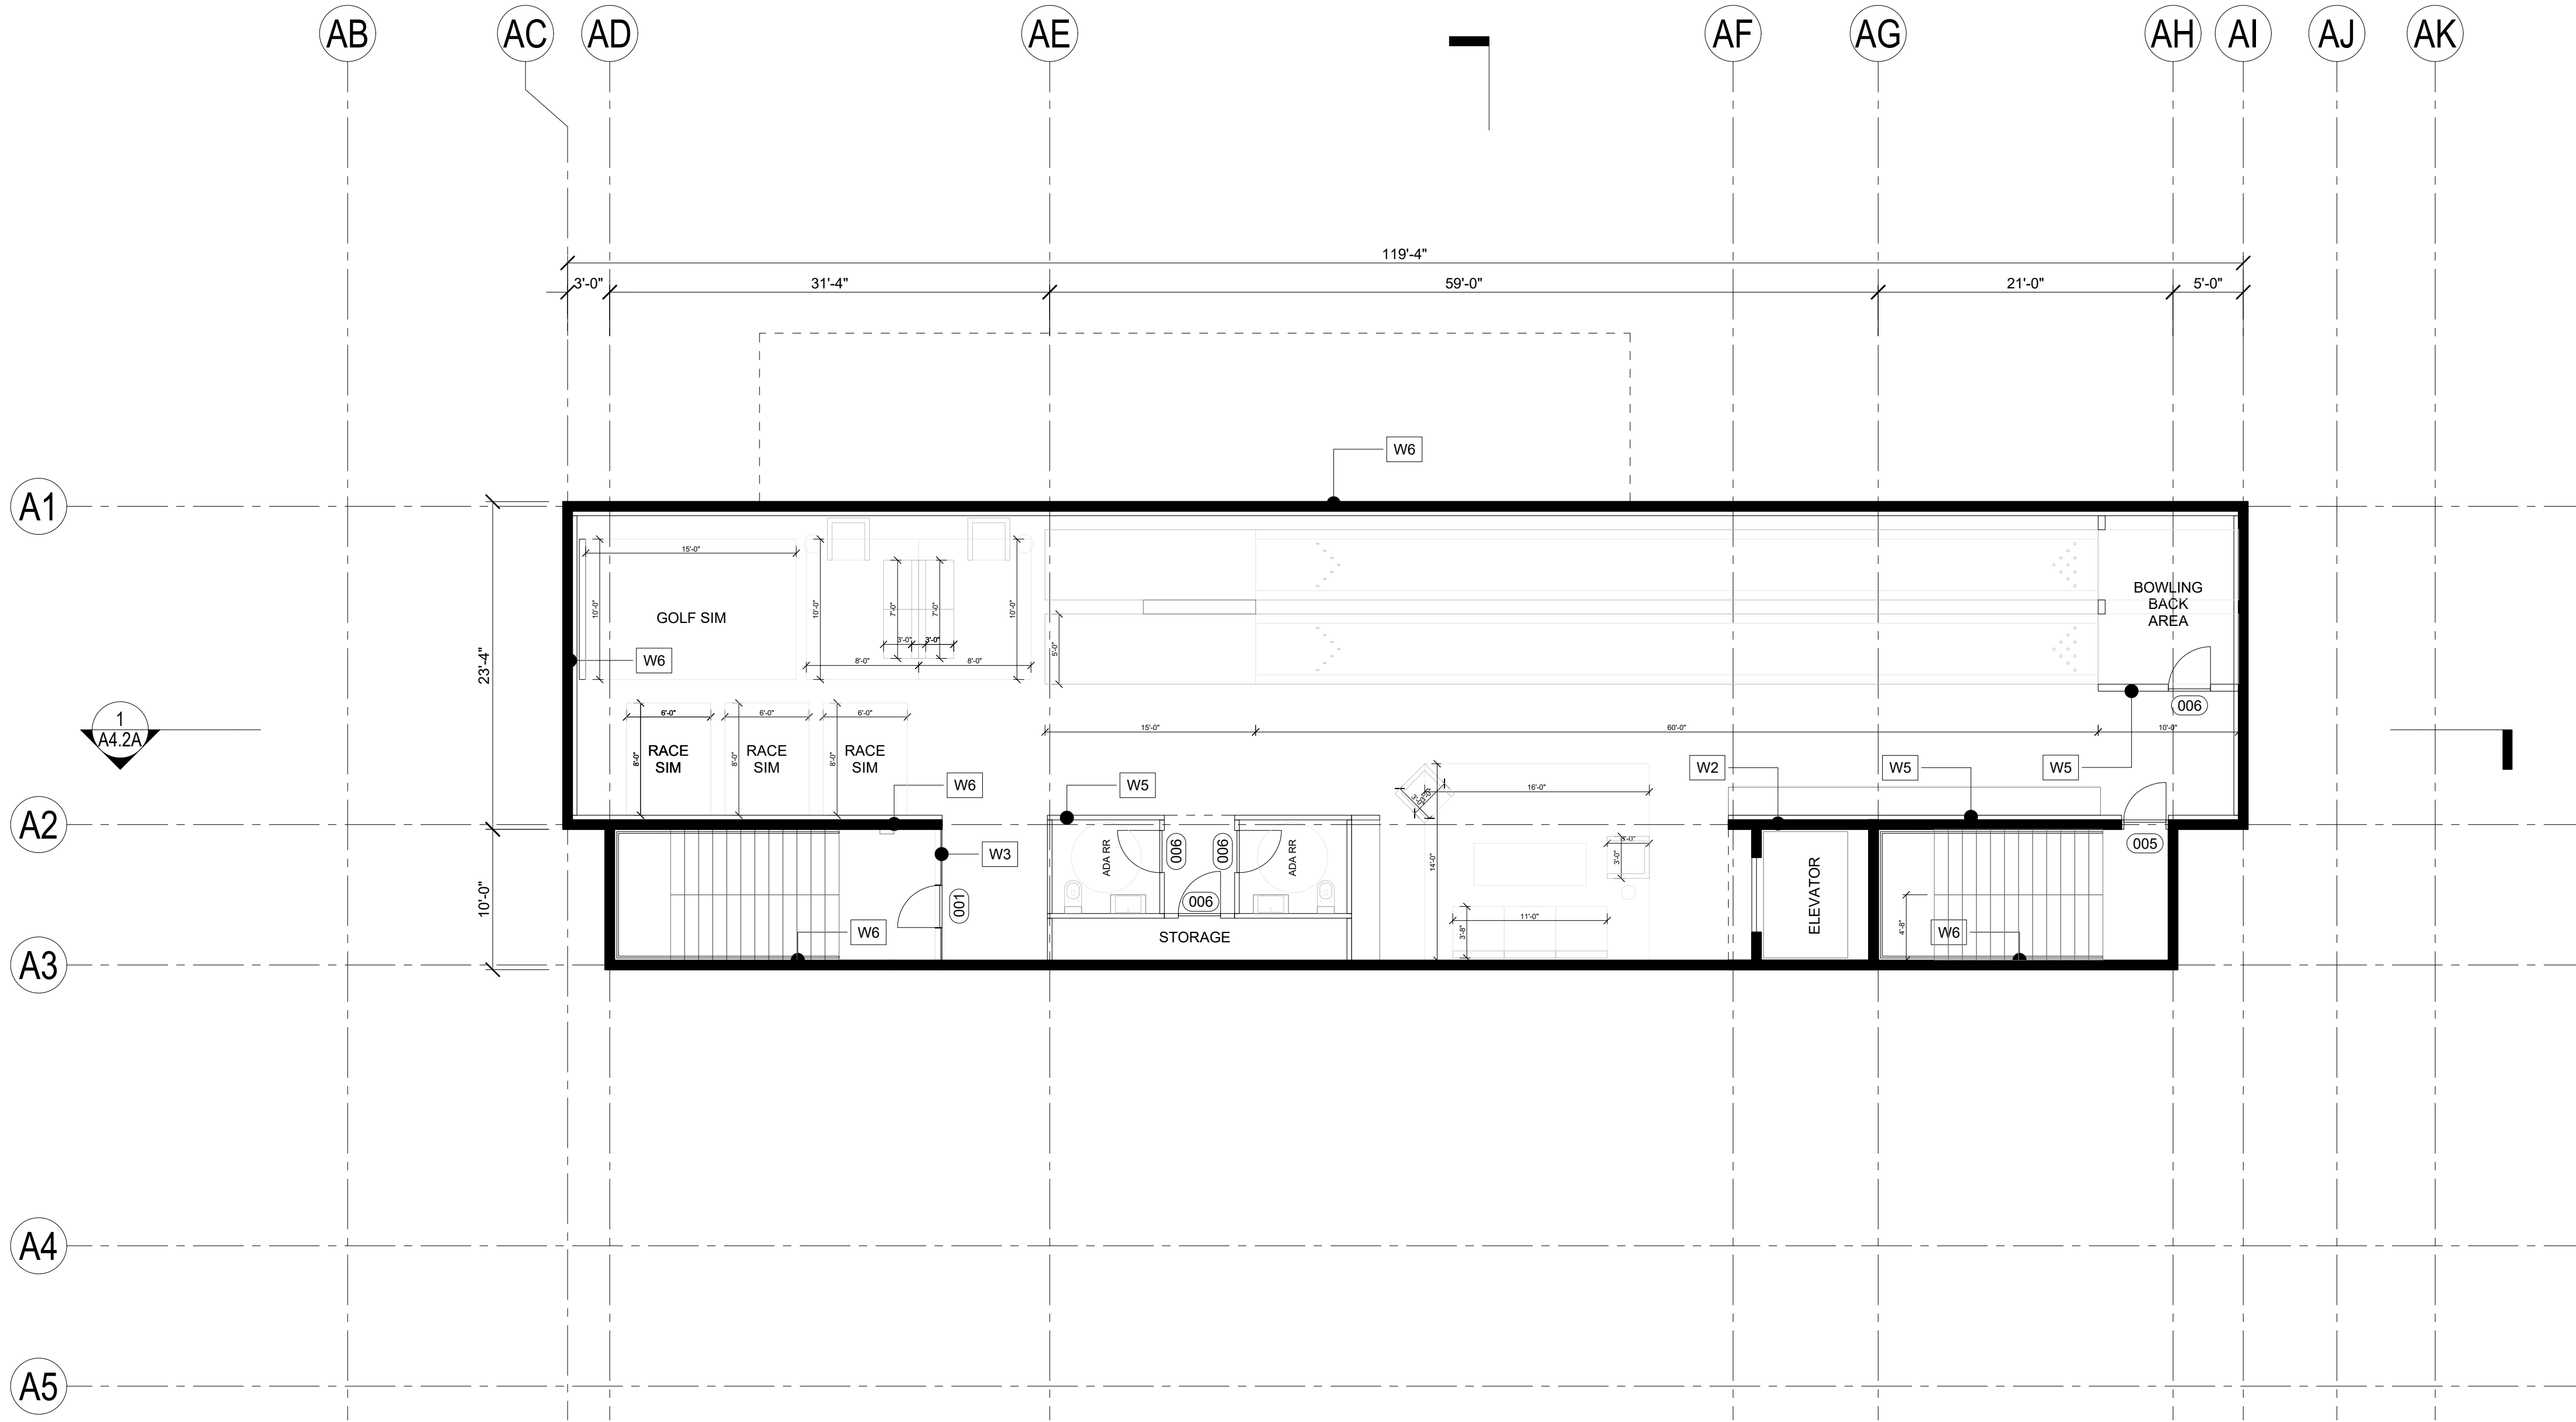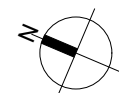

EXTERIOR WALLS

EXTERIOR WALL ASSEMBLY KEY:

- W1

METAL PANEL CLAD 8" CMU EXTERIOR WALL WITH [P1] PAINTED GYP INTERIOR
- W2

8" CMU EXTERIOR WALL WITH [P1] PAINTED GYP INTERIOR
- W3

EXTERIOR STEEL FRAME STOREFRONT, [P4] + [G1] FINISH.
- W4

GLASS CURTAIN WALL ASSEMBLY, NATURAL FINISH + [G2]
- W5

INTERIOR STEEL FRAME ASSEMBLY, GYP ON BOTH SIDES PAINTED WITH [P1]
- W6

8" CMU WALL UNFINISHED
- W7

PERFORATED METAL PANEL RAIN SCREEN CLAD 8" CMU EXTERIOR WALL WITH PAINTED GYP INTERIOR
- W8

METAL PANEL CLAD 8" CMU EXTERIOR WALL WITH [MP3] CLAD INTERIOR

CLIMATE ZONE	1		2		3		4 EXCEPT MARINE		5 AND MARINE 4		6
	All other	Group R	All other	Group R	All other	Group R	All other	Group R	All other	Group R	All other
Insulation entirely above roof deck	R-20ci	R-25ci	R-25ci	R-25ci	R-25ci	R-25ci	R-30ci	R-30ci	R-30ci	R-30ci	R-30ci
Metal buildings ¹	R-19 + R-11 LS	R-19 + R-11 LS	R-19 + R11 LS	R-19 + R-11 LS	R-19 + R-11 LS	R-19 + R-11 LS	R-19 + R-11 LS	R-19 + R-11 LS	R-19 + R-11 LS	R-25 + R-11 LS	
Attic and other	R-38	R-38	R-38	R-38	R-38	R-38	R-38	R-38	R-38	R-49	R-49
Walls, above grade											
Mass ²	R-5.7ci ³	R-5.7ci ³	R-5.7ci ³	R-7.6ci	R-7.6ci	R-9.5ci	R-9.5ci	R-11.4ci	R-11.4ci	R-13.3ci	R-13.3ci
Metal building	R-13 + R-6.5ci	R-13 + R-6.5ci	R-13 + R-6.5ci	R-13 + R-13ci	R-13 + R-6.5ci	R-13 + R-13ci	R-13 + R-13ci	R-13 + R-13ci	R-13 + R-13ci	R-13 + R-13ci	R-13 + R-13ci
Metal framed	R-13 + R-5ci	R-13 + R-5ci	R-13 + R-5ci	R-13 + R-7.5ci	R-13 + R-7.5ci	R-13 + R-7.5ci	R-13 + R-7.5ci	R-13 + R-7.5ci	R-13 + R-7.5ci	R-13 + R-7.5ci	R-13 + R-7.5ci
Wood framed and other	R-13 + R-3.8ci or R-20	R-13 + R-3.8ci or R-20	R-13 + R-3.8ci or R-20	R-13 + R-3.8ci or R-20	R-13 + R-3.8ci or R-20	R-13 + R-3.8ci or R-20	R-13 + R-3.8ci or R-20	R-13 + R-3.8ci or R-20	R-13 + R-3.8ci or R-20	R-13 + R-7.5ci or R-20 + R-3.8ci	R-13 + R-7.5ci or R-20 + R-3.8ci
Walls, below grade											
Below-grade wall ⁴	NR	NR	NR	NR	NR	NR	R-7.5ci	R-7.5ci	R-7.5ci	R-7.5ci	R-7.5ci
Floors											
Mass ⁵	NR	NR	R-6.3ci	R-8.3ci	R-10ci	R-10ci	R-10ci	R-10ci	R-10ci	R-12.5ci	R-12.5ci
Joist/framing	NR	NR	R-30	R-30	R-30	R-30	R-30	R-30	R-30	R-30	R-30
Slab-on-grade floors											
Unheated slabs	NR	NR	NR	NR	NR	NR	R-10 for 24" below	R-10 for 24" below	R-10 for 24" below	R-10 for 24" below	R-10 for 24" below
Heated slabs ⁶	R-7.5 for 12" below + R-5full slab	R-7.5 for 12" below + R-5full slab	R-7.5 for 12" below + R-5full slab	R-7.5 for 12" below + R-5full slab	R-10 for 24" below + R-5full slab	R-10 for 24" below + R-5full slab	R-15 for 24" below + R-5full slab	R-15 for 24" below + R-5full slab	R-15 for 24" below + R-5full slab	R-15 for 24" below + R-5full slab	R-15 for 24" below + R-5full slab
Opaque doors											
Nonswinging	R-4.75	R-4.75	R-4.75	R-4.75	R-4.75	R-4.75	R-4.75	R-4.75	R-4.75	R-4.75	R-4.75

For SI: 1 inch = 25.4 mm; 1 pound per square foot = 4.88 kg/m²; 1 pound per cubic foot = 16 kg/m³.
ci = Continuous insulation, NR = No Requirement, LS = Liner System.
^a Assembly descriptions can be found in ANSI/ASHRAE/ESNA Appendix A.
^b Where using R-value compliance method, a thermal spacer block shall be provided; otherwise use the U-factor compliance method in Table C402.1.4.
^c R-5.7ci is allowed to be substituted with concrete block walls complying with ASTM C90, ungrouted or partially grouted at 92 inches or less on center vertically and 48 inches or less on center horizontally with ungrouted cores filled with materials having a maximum thermal conductivity of 0.44 Btu-in/h·ft²·°F.
^d Where heated slabs are below grade, below-grade walls shall comply with the exterior insulation requirements for heated slabs.
^e Mass Framed Walls in compliance with Section C402.2.5.

FINISH LINE AUTO CLUB

17600 PERIMETER DR 100
SCOTTSDALE, AZ 85255

LGE

DESIGNGROUP

1200 N. 52nd Street ■ Phoenix, AZ ■ 85008
P. 480.966.4001

LGE

DESIGNBUILD

NUMBER	REVISION	DATE
--------	----------	------

UPDATE

PRICING SET
NOT TO BE USED
FOR CONSTRUCTION

SHEET TITLE:
PLAN - CLUBHOUSE LOWER LEVEL


ISSUE DATE: 03/25/25

DRAWN BY: AE

CHECKED BY: RH

PROJECT No.: 000000

SHEET:
A2.2A

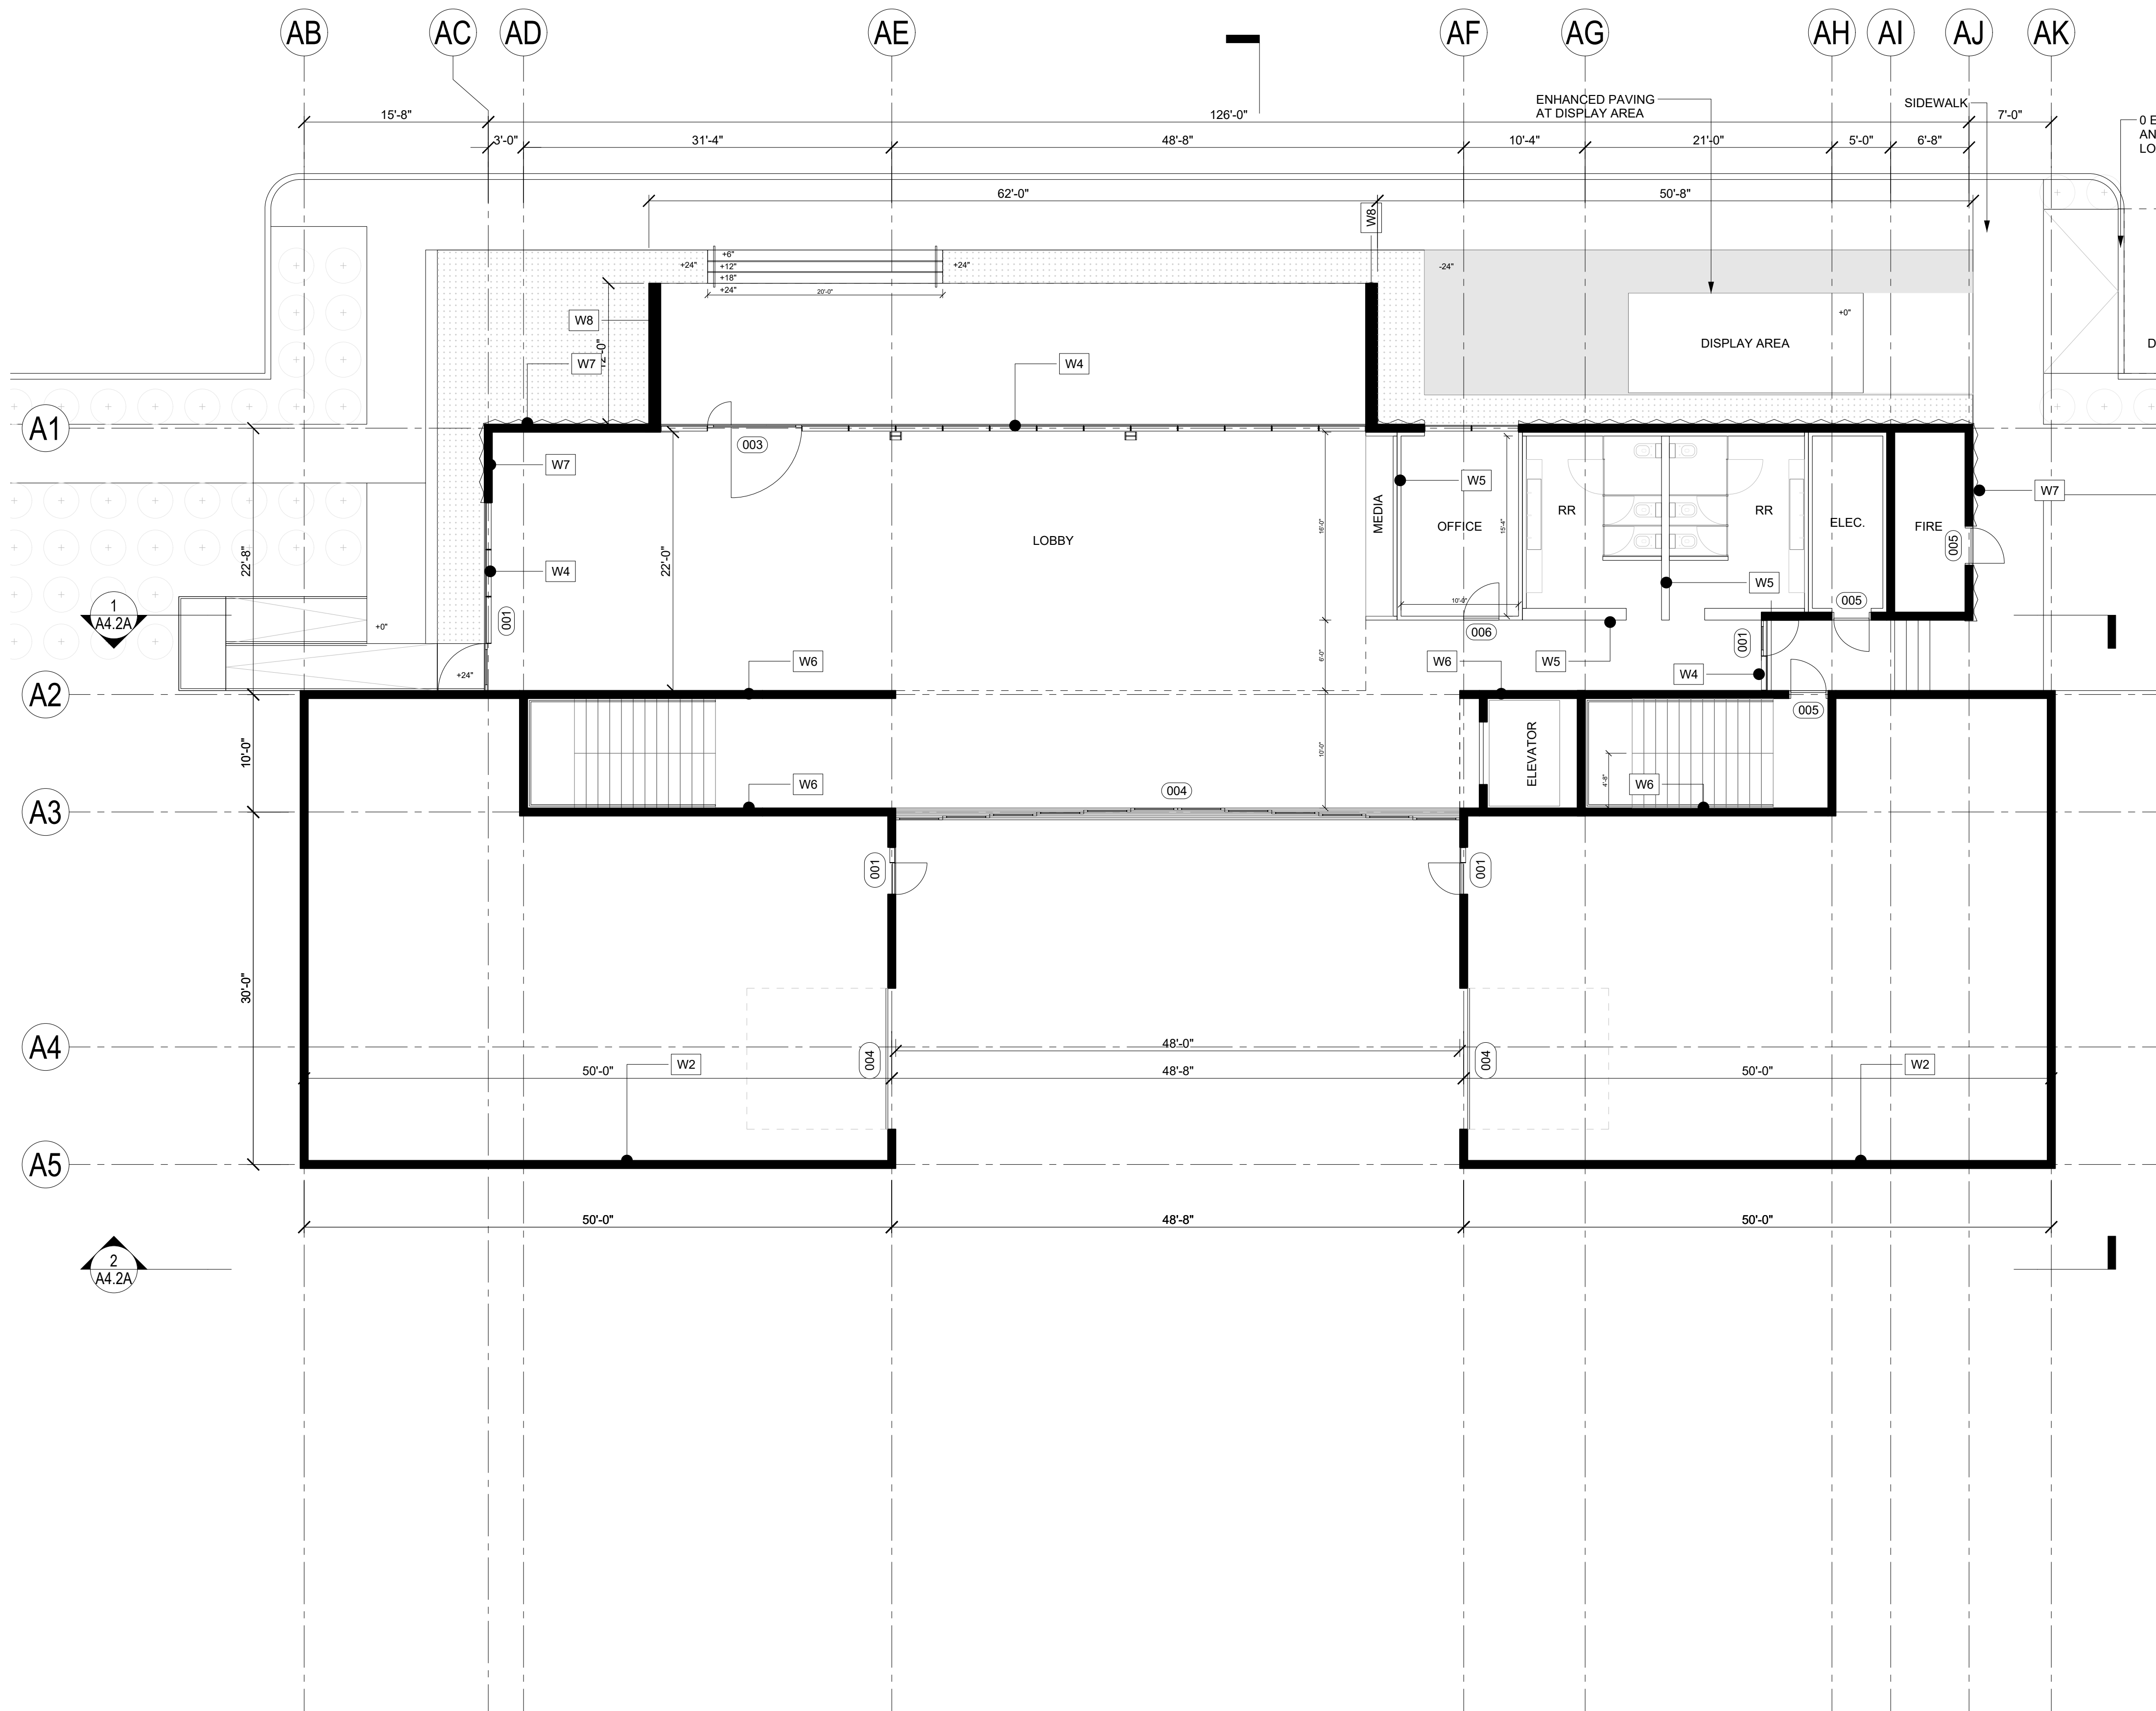


EXTERIOR WALLS

EXTERIOR WALL ASSEMBLY KEY:

- W1 METAL PANEL CLAD 8" CMU EXTERIOR WALL WITH [P1] PAINTED GYP INTERIOR
- W2 8" CMU EXTERIOR WALL WITH [P1] PAINTED GYP INTERIOR
- W3 EXTERIOR STEEL FRAME STOREFRONT, [P4] + [G1] FINISH.
- W4 GLASS CURTAIN WALL ASSEMBLY, NATURAL FINISH + [G2]
- W5 INTERIOR STEEL FRAME ASSEMBLY, GYP ON BOTH SIDES PAINTED WITH [P1]
- W6 8" CMU WALL UNFINISHED
- W7 PERFORATED METAL PANEL RAIN SCREEN CLAD 8" CMU EXTERIOR WALL WITH PAINTED GYP INTERIOR
- W8 METAL PANEL CLAD 8" CMU EXTERIOR WALL WITH [MP3] CLAD INTERIOR

01 PLAN - CLUBHOUSE LEVEL 1
SCALE: 1/8" = 1'-0"

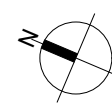

FINISH LINE AUTO CLUB

17600 PERIMETER DR 100
SCOTTSDALE, AZ 85255

LGE | DESIGNBUILD

NUMBER	REVISION	DATE

UPDATE
PRICING SET
NOT TO BE USED
FOR CONSTRUCTION

SHEET TITLE:
PLAN - CLUBHOUSE LEVEL 1

ISSUE DATE: 03/25/25

DRAWN BY: AE

CHECKED BY: RH


PROJECT No.: 000000

SHEET:

A2.3A

LGE | DESIGNGROUP

1200 N. 52nd Street ■ Phoenix, AZ 85008
P: 480.966.4001

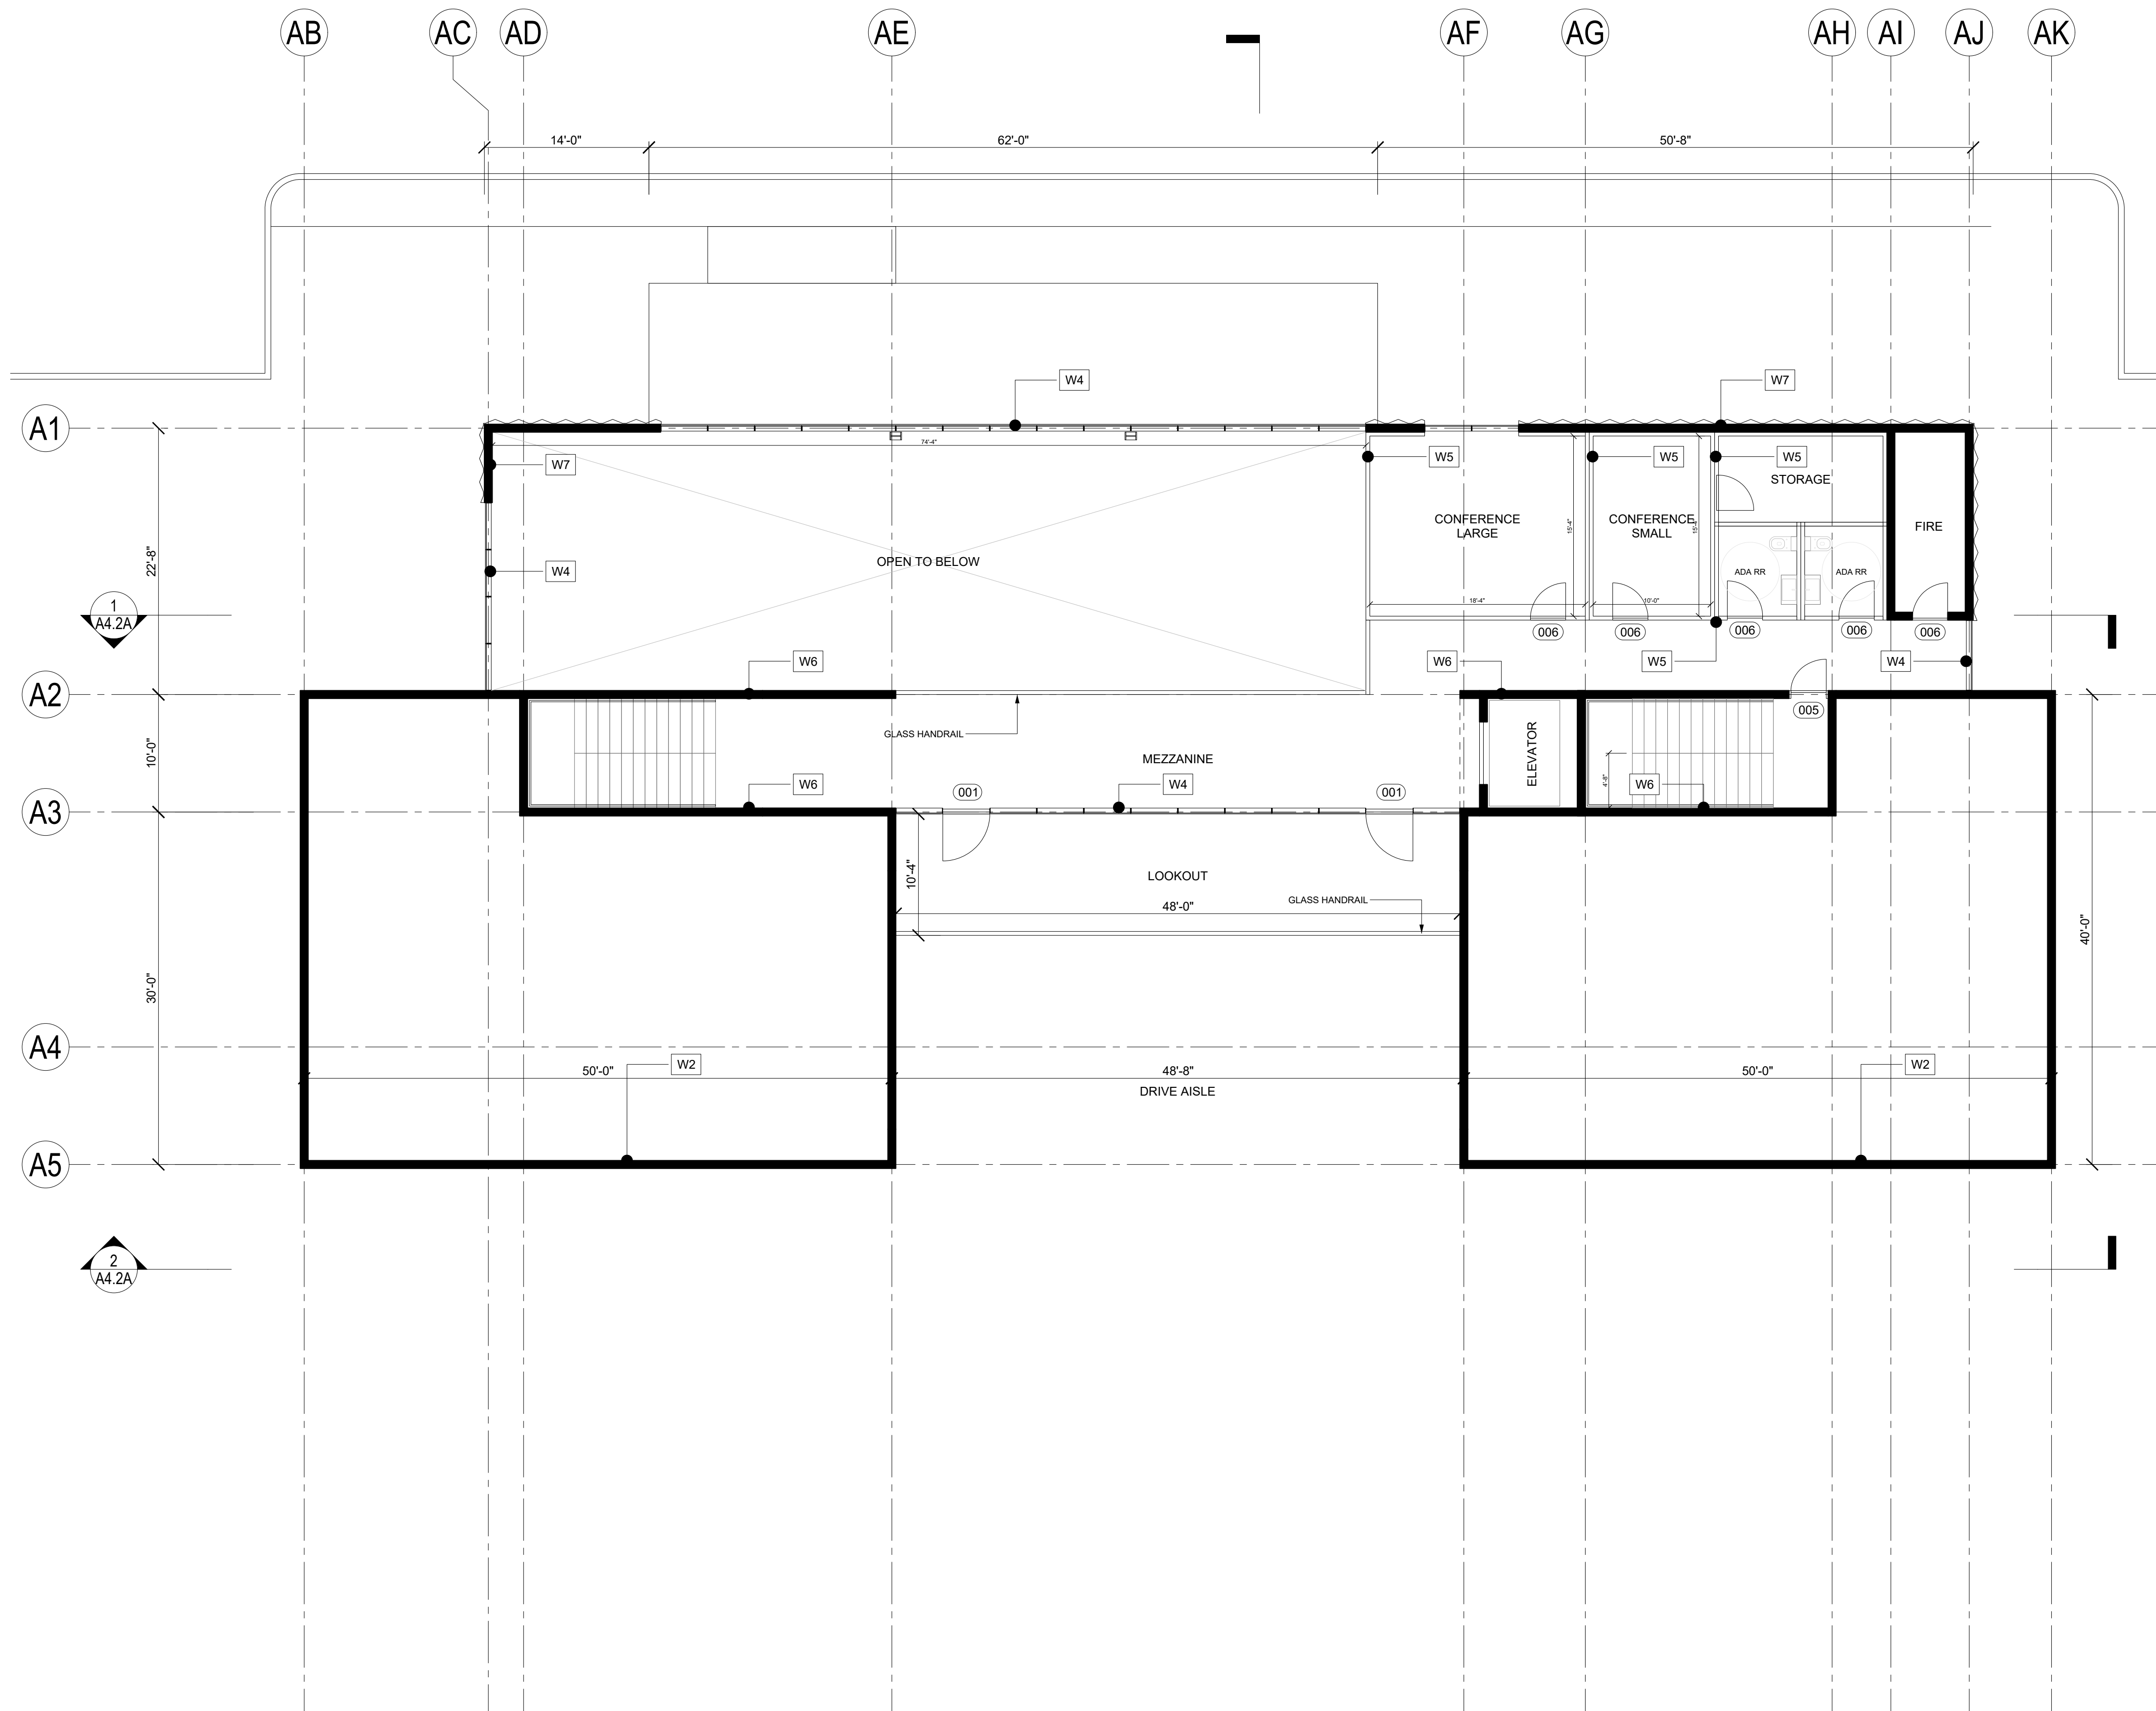


EXTERIOR WALLS

EXTERIOR WALL ASSEMBLY KEY:

W1	METAL PANEL CLAD 8" CMU EXTERIOR WALL WITH [P1] PAINTED GYP INTERIOR
W2	8" CMU EXTERIOR WALL WITH [P1] PAINTED GYP INTERIOR
W3	EXTERIOR STEEL FRAME STOREFRONT, [P4] + [G1] FINISH.
W4	GLASS CURTAIN WALL ASSEMBLY, NATURAL FINISH + [G2]
W5	INTERIOR STEEL FRAME ASSEMBLY, GYP ON BOTH SIDES PAINTED WITH [P1]
W6	8" CMU WALL UNFINISHED
W7	PERFORATED METAL PANEL RAIN SCREEN CLAD 8" CMU EXTERIOR WALL WITH PAINTED GYP INTERIOR
W8	METAL PANEL CLAD 8" CMU EXTERIOR WALL WITH [MP3] CLAD INTERIOR

01 PLAN - CLUBHOUSE LEVEL 2
SCALE: 1/8" = 1'-0"

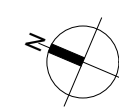

FINISH LINE AUTO CLUB

17600 PERIMETER DR 100
SCOTTSDALE, AZ 85255


LGE | DESIGNBUILD

NUMBER	REVISION	DATE
--------	----------	------

UPDATE
PRICING SET
NOT TO BE USED
FOR CONSTRUCTION

SHEET TITLE:
PLAN - CLUBHOUSE LEVEL 2
ISSUE DATE: 03/25/25
DRAWN BY: AE
CHECKED BY: RH
PROJECT No.: 000000
SHEET:

A2.4A

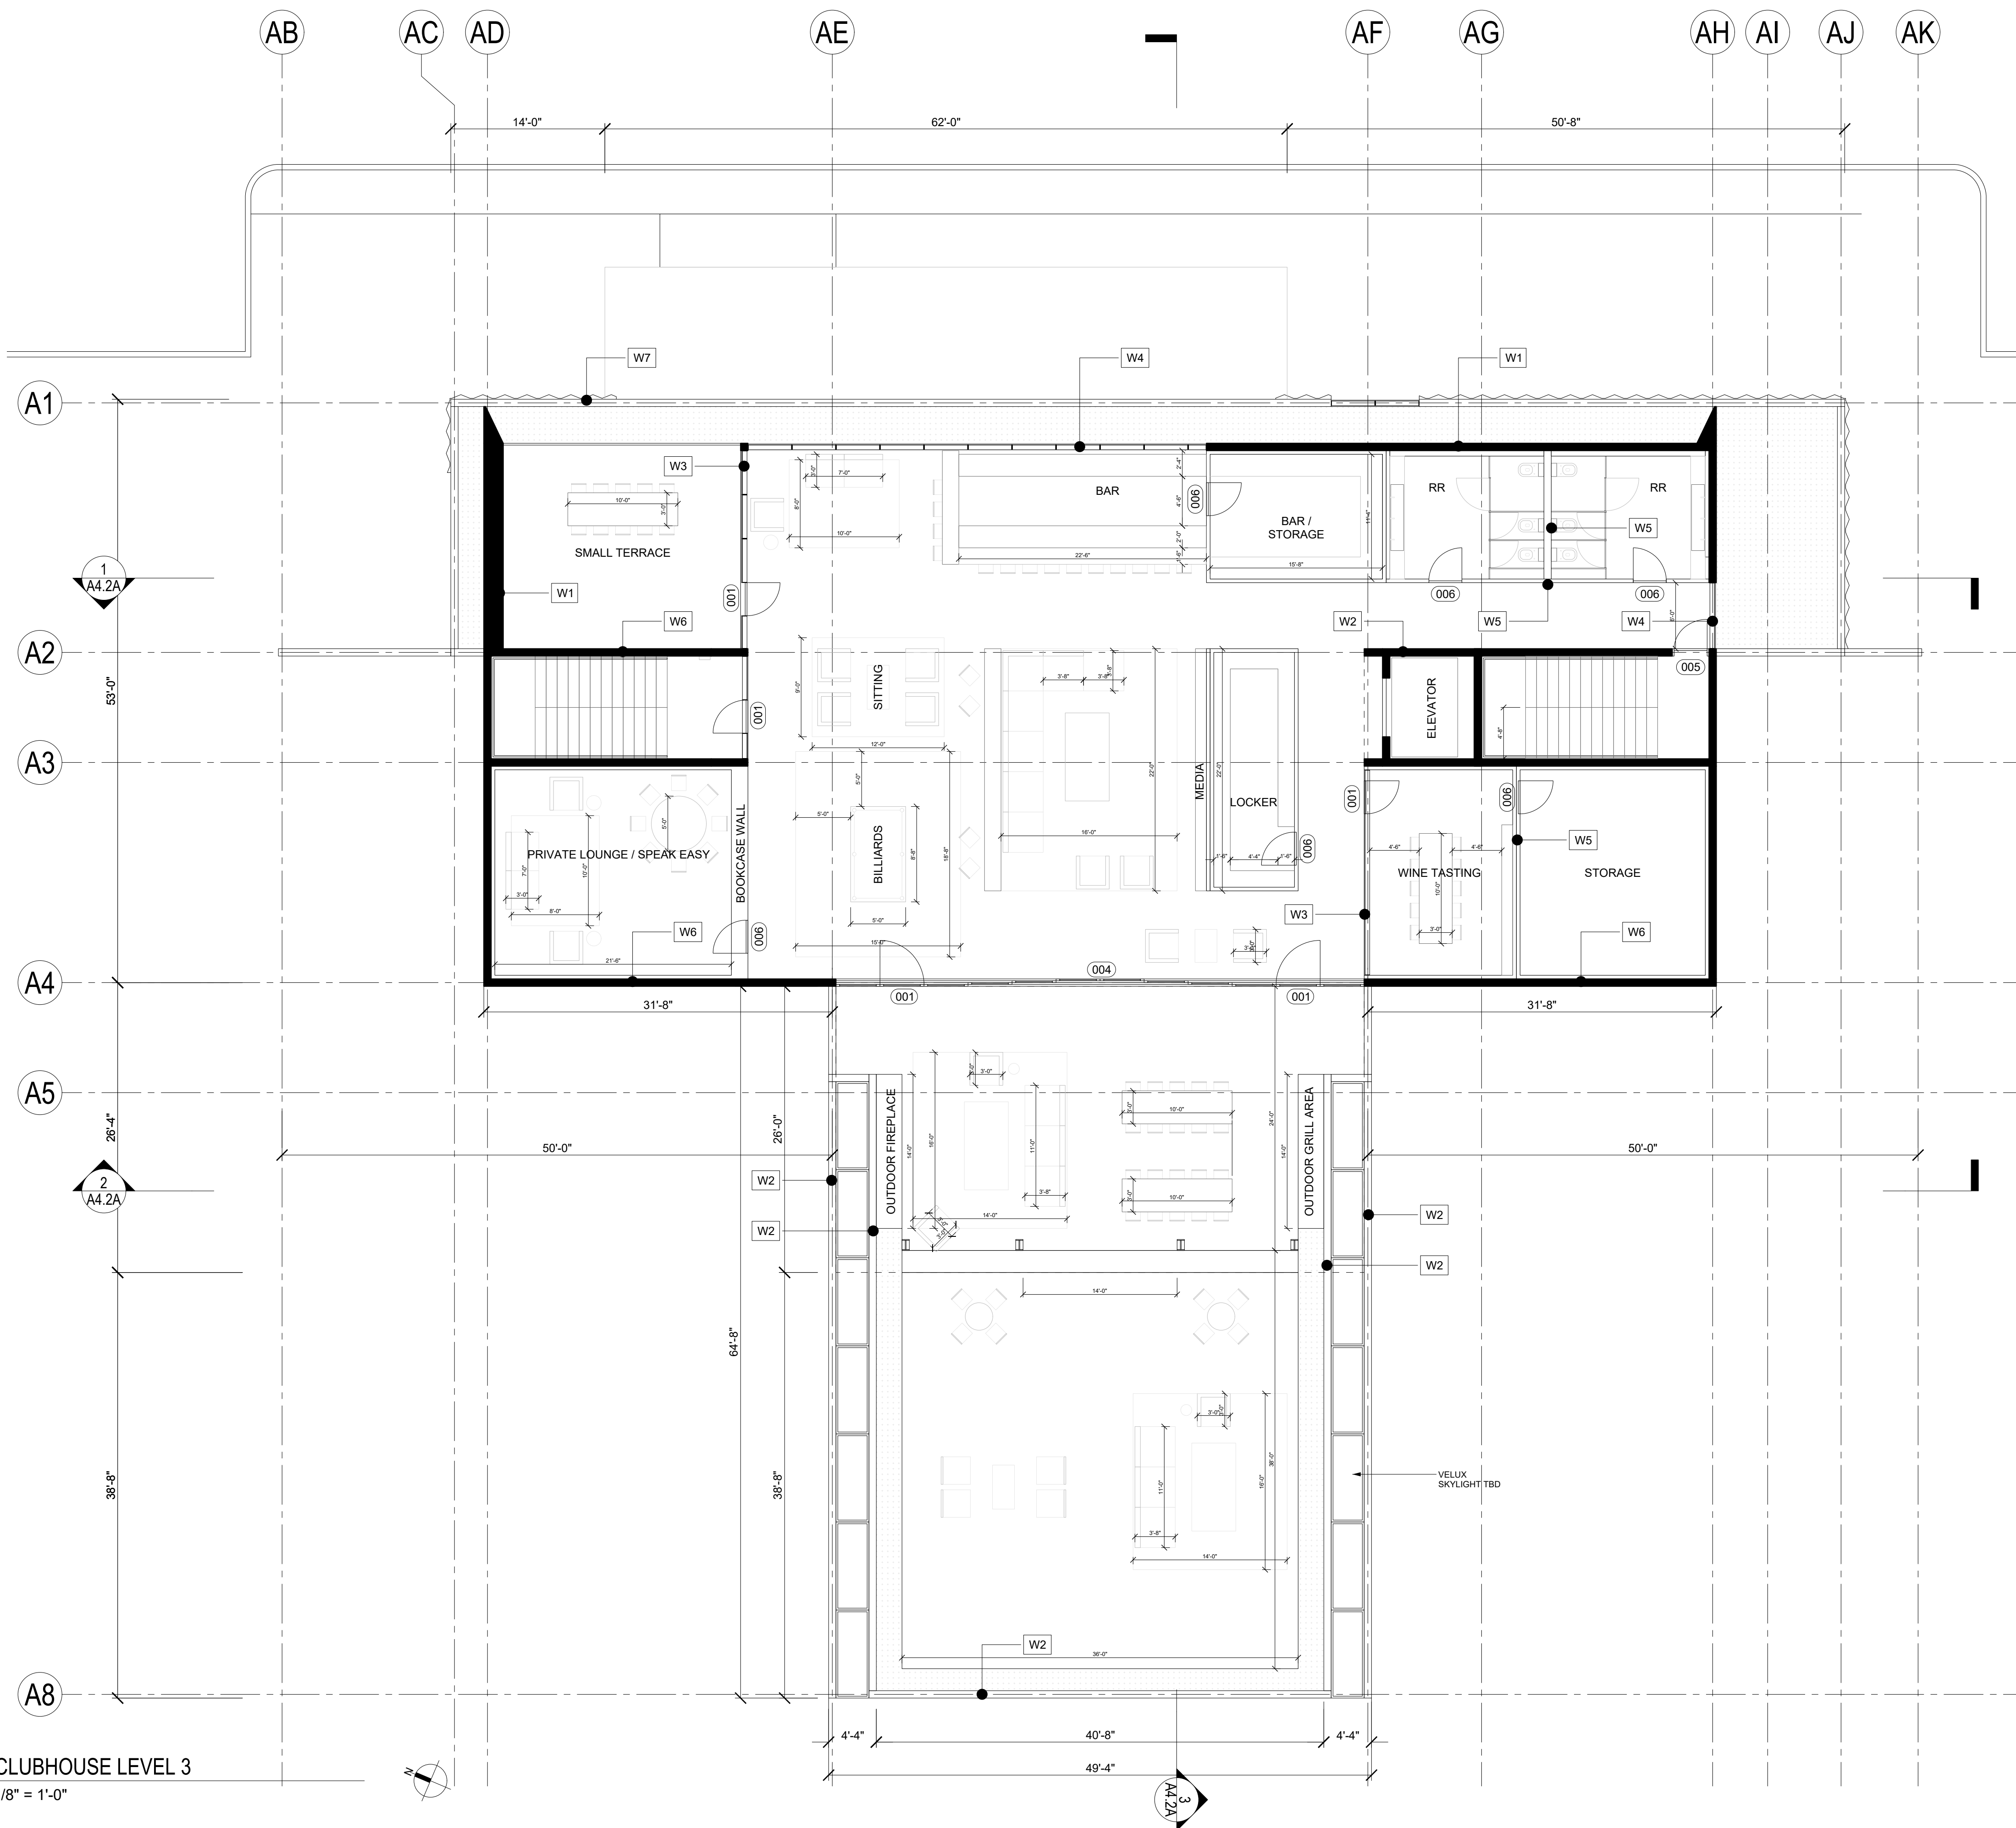

01 PLAN - CLUBHOUSE LEVEL 3
SCALE: 1/8" = 1'-0"

EXTERIOR WALLS

EXTERIOR WALL ASSEMBLY KEY:

- W1 METAL PANEL CLAD 8" CMU EXTERIOR WALL WITH [P1] PAINTED GYP INTERIOR
- W2 8" CMU EXTERIOR WALL WITH [P1] PAINTED GYP INTERIOR
- W3 EXTERIOR STEEL FRAME STOREFRONT, [P4] + [G1] FINISH.
- W4 GLASS CURTAIN WALL ASSEMBLY, NATURAL FINISH + [G2]
- W5 INTERIOR STEEL FRAME ASSEMBLY, GYP ON BOTH SIDES PAINTED WITH [P1]
- W6 8" CMU WALL UNFINISHED
- W7 PERFORATED METAL PANEL RAIN SCREEN CLAD 8" CMU EXTERIOR WALL WITH PAINTED GYP INTERIOR
- W8 METAL PANEL CLAD 8" CMU EXTERIOR WALL WITH [MP3] CLAD INTERIOR

FINISH LINE AUTO CLUB

LGE | DESIGNGROUP

1200 N. 52nd Street ■ Phoenix, AZ ■ 85008
P: 480.966.4001


LGE | DESIGNBUILD

NUMBER REVISION DATE


UPDATE
PRICING SET
NOT TO BE USED
FOR CONSTRUCTION

SHEET TITLE:
PLAN - CLUBHOUSE LEVEL 3
ISSUE DATE: 03/25/25
DRAWN BY: AE
CHECKED BY: RH
PROJECT No.: 000000
SHEET:

A2.5A

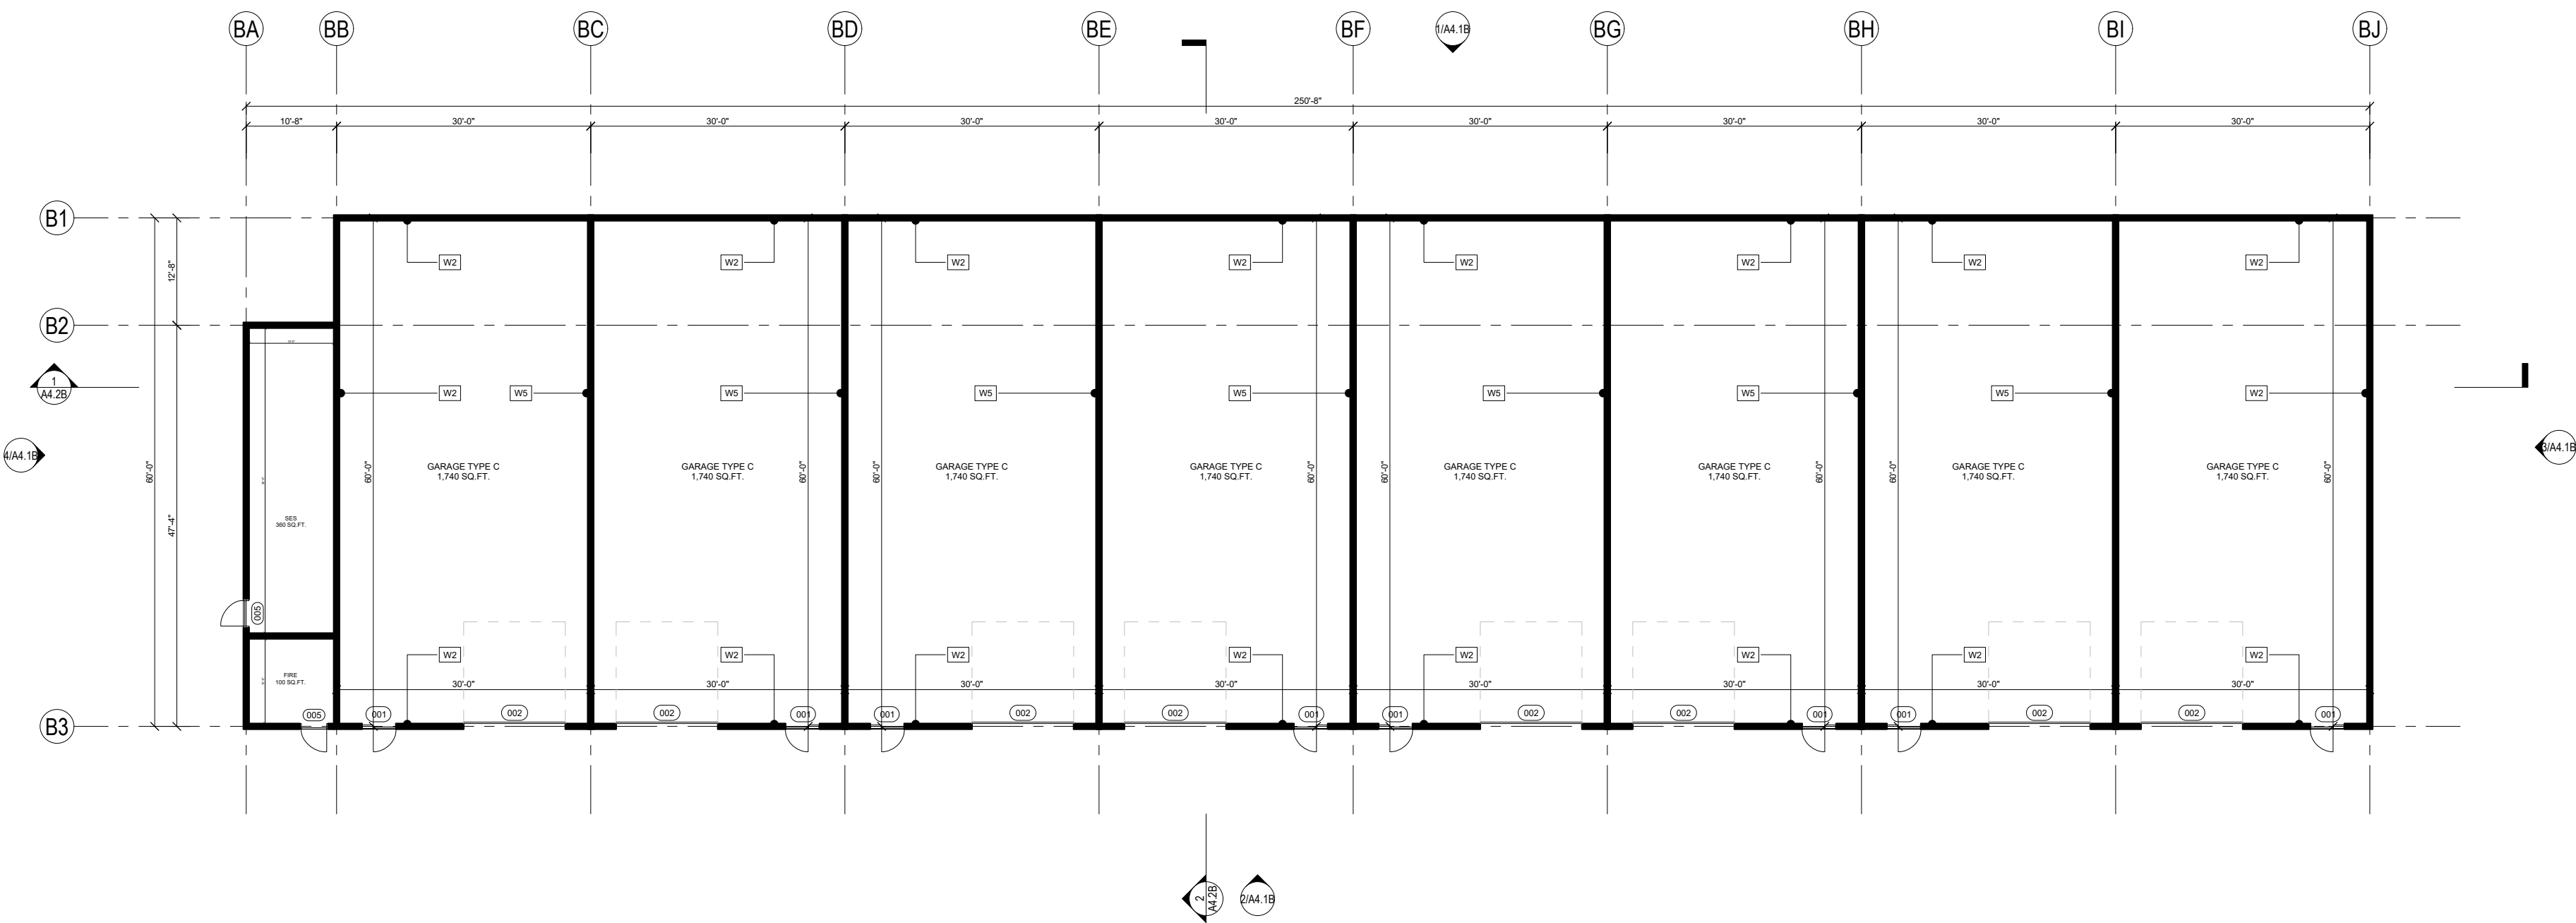

01 PLAN - BUILDING B
SCALE: 1/16" = 1'-0"

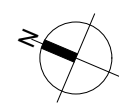

EXTERIOR WALLS

EXTERIOR WALL ASSEMBLY KEY:

- | | |
|----|--|
| W1 | METAL PANEL CLAD 8" CMU EXTERIOR WALL WITH [P1] PAINTED GYP INTERIOR |
| W2 | 8" CMU EXTERIOR WALL WITH [P1] PAINTED GYP INTERIOR |
| W3 | EXTERIOR STEEL FRAME STOREFRONT. [P4] + [G1] FINISH. |
| W4 | GLASS CURTAIN WALL ASSEMBLY. NATURAL FINISH + [G2] |
| W5 | INTERIOR STEEL FRAME ASSEMBLY. GYP ON BOTH SIDES PAINTED WITH [P1] |
| W6 | 8" CMU WALL UNFINISHED |
| W7 | PERFORATED METAL PANEL RAIN SCREEN CLAD 8" CMU EXTERIOR WALL WITH PAINTED GYP INTERIOR |
| W8 | METAL PANEL CLAD 8" CMU EXTERIOR WALL WITH [MP3] CLAD INTERIOR |

FINISH LINE AUTO CLUB

17600 PERIMETER DR 100
SCOTTSDALE, AZ 85255

LGE | DESIGNBUILD

NUMBER	REVISION	DATE
--------	----------	------

UPDATE
PRICING SET
NOT TO BE USED
FOR CONSTRUCTION

SHEET TITLE:
PLAN - BUILDING E
ISSUE DATE: 03/25/25
DRAWN BY: AE
CHECKED BY: RH
PROJECT No.: 000000
SHEET:


A2.1B

LGE | DESIGNGROUP

1200 N. 52nd Street ■ Phoenix, AZ 85008
P: 480.966.4001



01 PLAN - BUILDING C
SCALE: 1/16" = 1'-0"

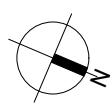

EXTERIOR WALLS

EXTERIOR WALL ASSEMBLY KEY:

- W1 METAL PANEL CLAD 8" CMU EXTERIOR WALL WITH [P1] PAINTED GYP INTERIOR
- W2 8" CMU EXTERIOR WALL WITH [P1] PAINTED GYP INTERIOR
- W3 EXTERIOR STEEL FRAME STOREFRONT. [P4] + [G1] FINISH.
- W4 GLASS CURTAIN WALL ASSEMBLY. NATURAL FINISH + [G2]
- W5 INTERIOR STEEL FRAME ASSEMBLY. GYP ON BOTH SIDES PAINTED WITH [P1]
- W6 8" CMU WALL UNFINISHED
- W7 PERFORATED METAL PANEL RAIN SCREEN CLAD 8" CMU EXTERIOR WALL WITH PAINTED GYP INTERIOR
- W8 METAL PANEL CLAD 8" CMU EXTERIOR WALL WITH [MP3] CLAD INTERIOR

FINISH LINE AUTO CLUB

17600 PERIMETER DR 100
SCOTTSDALE, AZ 85255



NUMBER	REVISION	DATE
--------	----------	------

UPDATE


PRICING SET
NOT TO BE USED
FOR CONSTRUCTION

SHEET TITLE:	PLAN - BUILDING C
ISSUE DATE:	03/25/25
DRAWN BY:	AE
CHECKED BY:	RH
PROJECT No.:	000000
SHEET:	


A2.1C



1200 N. 52nd Street ■ Phoenix, AZ 85008
P: 480.966.4001

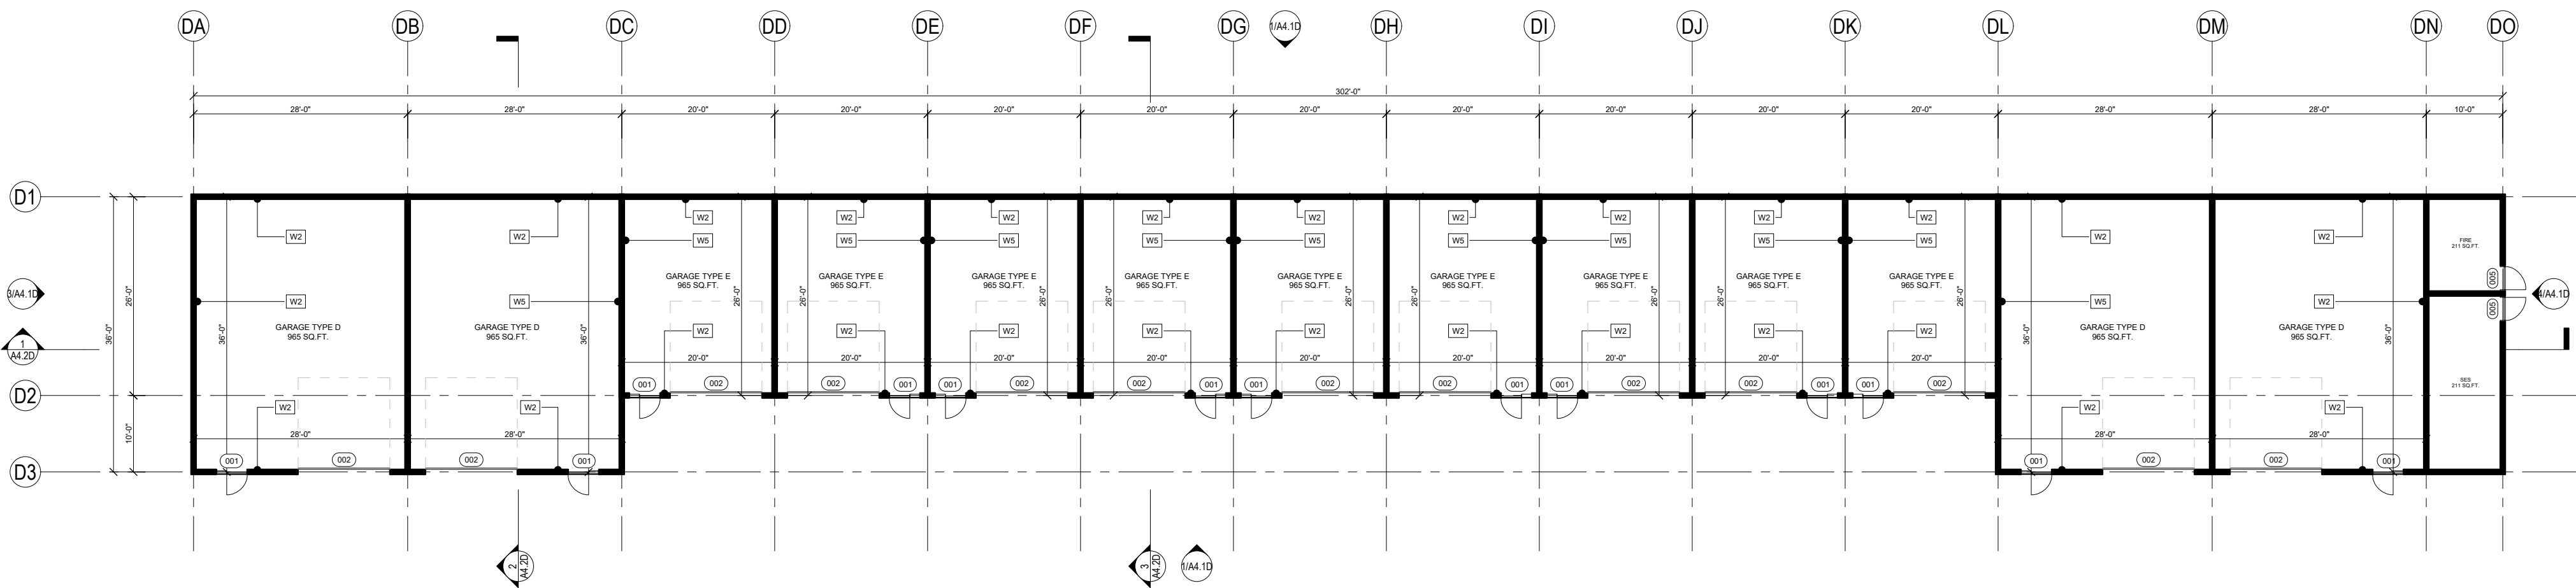

01 PLAN - BUILDING D
SCALE: 1/16" = 1'-0"

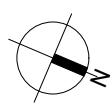

EXTERIOR WALLS

EXTERIOR WALL ASSEMBLY KEY:

- W1 METAL PANEL CLAD 8" CMU EXTERIOR WALL WITH [P1] PAINTED GYP INTERIOR
- W2 8" CMU EXTERIOR WALL WITH [P1] PAINTED GYP INTERIOR
- W3 EXTERIOR STEEL FRAME STOREFRONT. [P4] + [G1] FINISH.
- W4 GLASS CURTAIN WALL ASSEMBLY. NATURAL FINISH + [G2]
- W5 INTERIOR STEEL FRAME ASSEMBLY. GYP ON BOTH SIDES PAINTED WITH [P1]
- W6 8" CMU WALL UNFINISHED
- W7 PERFORATED METAL PANEL RAIN SCREEN CLAD 8" CMU EXTERIOR WALL WITH PAINTED GYP INTERIOR
- W8 METAL PANEL CLAD 8" CMU EXTERIOR WALL WITH [MP3] CLAD INTERIOR

FINISH LINE AUTO CLUB

17600 PERIMETER DR 100
SCOTTSDALE, AZ 85255

LGE | DESIGNBUILD

NUMBER	REVISION	DATE
--------	----------	------


UPDATE
PRICING SET
NOT TO BE USED
FOR CONSTRUCTION

SHEET TITLE:
PLAN - BUILDING C
ISSUE DATE: 03/25/25
DRAWN BY: AE
CHECKED BY: RH
PROJECT No.: 000000
SHEET:

A2.1D


LGE | DESIGNGROUP

1200 N. 52nd Street ■ Phoenix, AZ 85008
P: 480.966.4001

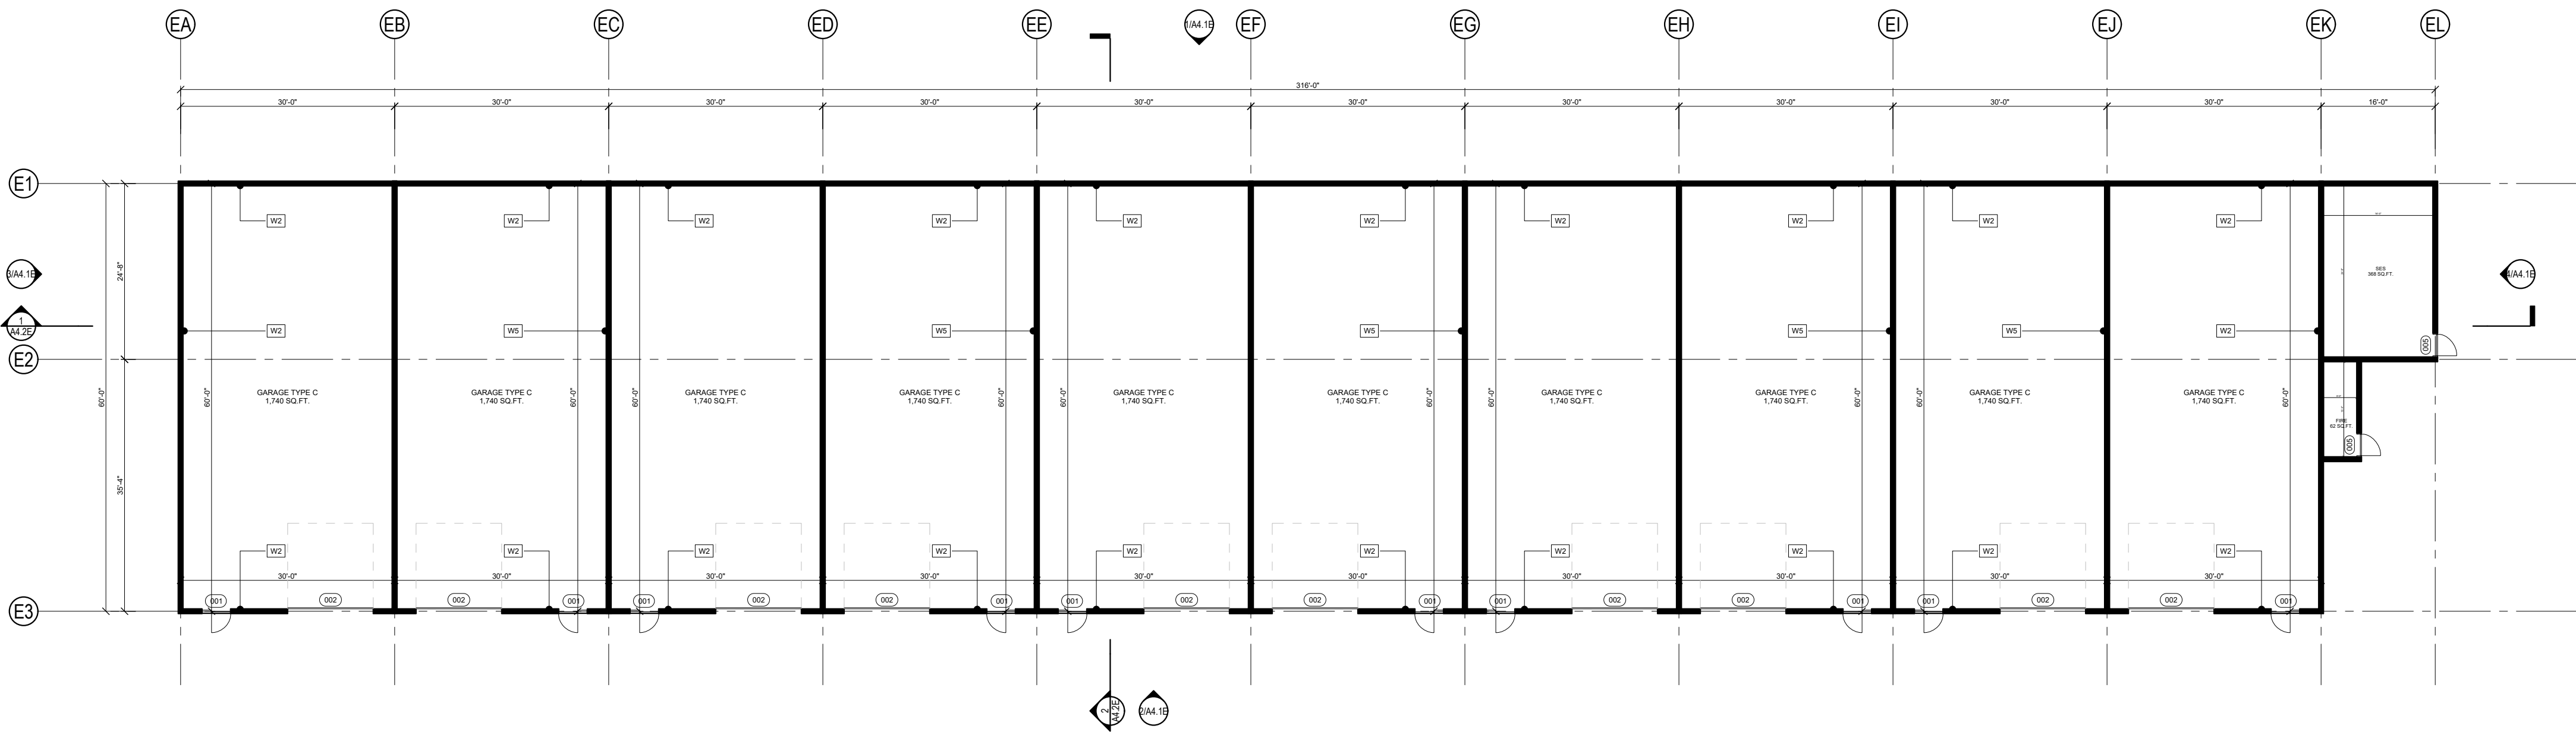

01

PLAN - BUILDING E
SCALE: 1/16" = 1'-0"

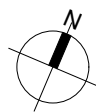

EXTERIOR WALLS

EXTERIOR WALL ASSEMBLY KEY:

- W1 METAL PANEL CLAD 8" CMU EXTERIOR WALL WITH [P1] PAINTED GYP INTERIOR
- W2 8" CMU EXTERIOR WALL WITH [P1] PAINTED GYP INTERIOR
- W3 EXTERIOR STEEL FRAME STOREFRONT. [P4] + [G1] FINISH.
- W4 GLASS CURTAIN WALL ASSEMBLY. NATURAL FINISH + [G2]
- W5 INTERIOR STEEL FRAME ASSEMBLY. GYP ON BOTH SIDES PAINTED WITH [P1]
- W6 8" CMU WALL UNFINISHED
- W7 PERFORATED METAL PANEL RAIN SCREEN CLAD 8" CMU EXTERIOR WALL WITH PAINTED GYP INTERIOR
- W8 METAL PANEL CLAD 8" CMU EXTERIOR WALL WITH [MP3] CLAD INTERIOR

FINISH LINE AUTO CLUB

17600 PERIMETER DR 100
SCOTTSDALE, AZ 85255

LGE | DESIGNBUILD

NUMBER	REVISION	DATE
--------	----------	------

UPDATE
PRICING SET
NOT TO BE USED
FOR CONSTRUCTION

SHEET TITLE:
PLAN - BUILDING B
ISSUE DATE: 03/25/25
DRAWN BY: AE
CHECKED BY: RH
PROJECT No.: 000000
SHEET:

A2.1E

LGE | DESIGNGROUP

1200 N. 52nd Street ■ Phoenix, AZ 85008
P: 480.966.4001