



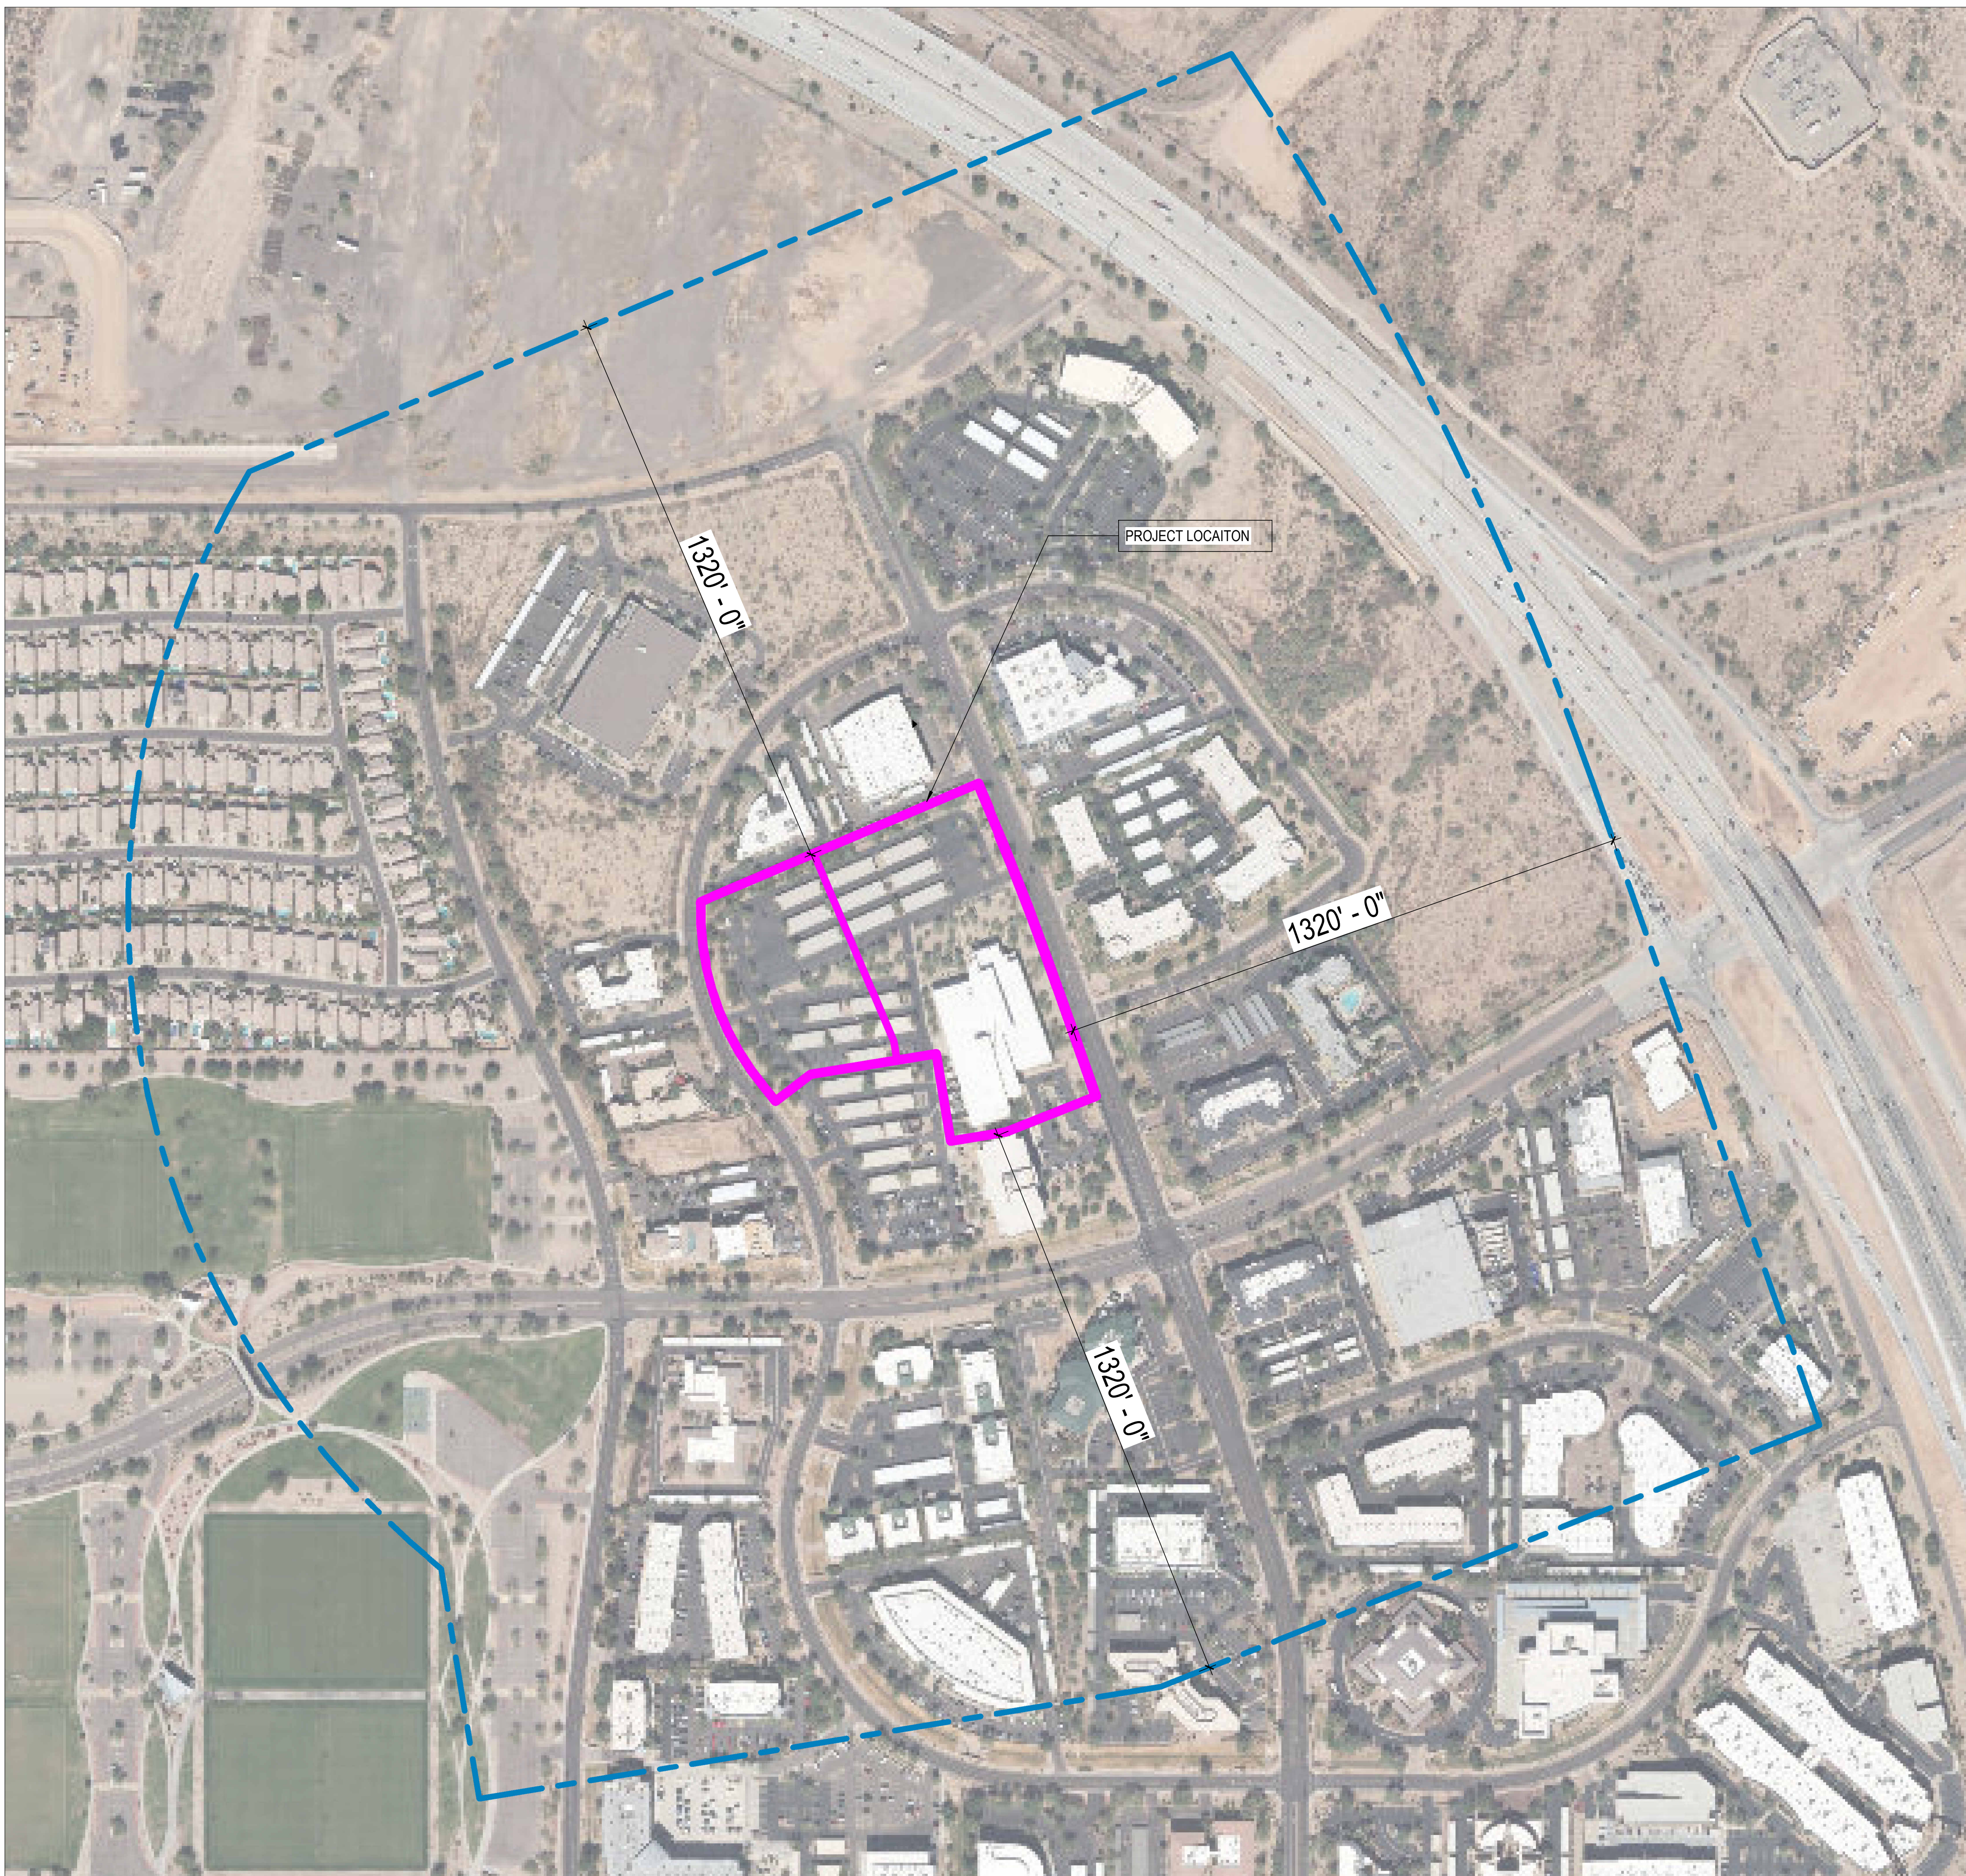

1

ARCHITECTURAL SITE PLAN W/ AERIAL

1" = 200'-0"

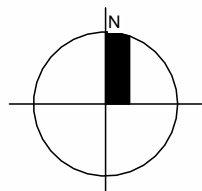

PROJECT DATA

INDUSTRIAL - WEST LOT

PROJECT ADDRESS: 17600 N PERIMETER DR 100 SCOTTSDALE 85255

OWNER: FINISH LINE AUTO CLUB 3080 AIRWAY AVE. COSTA MESA, CA 92626 TONY PRINCIPLE

ARCHITECT: LGE DESIGN GROUP 1200 NORTH 52ND STREET PHOENIX, AZ. 85008 STUDIO DIRECTOR: MARK S. CONE

PROJECT SCOPE: APPROXIMATELY 46,052 SF OF: WAREHOUSE 4,000 SF OF: OFFICE

ASSESSOR PARCEL NO.: 215-07-230

CURRENT ZONING: I-1 PCD

PROPOSED ZONING: I-1 PCD

SITE AREA: +/- 159,000 S.F. (3.65 AC)

STORIES: 1 STORY

GROSS BUILDING S.F.: 50,052 S.F. TOTAL

LOT COVERAGE: 31.5%

OCCUPANCY: B / S-1

CONSTRUCTION TYPE: V-B W/ A.F.E.S.

BUILDING HEIGHT: 38'-0"

PROJECT DESCRIPTION:

THE PACESETTER WAY PROJECT CONSISTS OF ONE BUILDING (WAREHOUSE WITH AN OFFICE) ON A 3.65 ACRE SITE LOCATED ON N PACESETTER WAY WHICH CURRENTLY HAS NO BUILDINGS.

REQUIRED PARKING:

WAREHOUSE: 46,052 S.F./800= 58 SPACES
OFFICE: 4,000 S.F./300= 13 SPACES
TOTAL REQUIRED= 71 SPACES

PROVIDED PARKING= 71 SPACES
REGULAR PARKING= 00 SPACES
ACCESSIBLE PARKING= 1.42 CARS/1000

AUTO CLUB - EAST LOT

PROJECT ADDRESS: 17600 N PERIMETER DR 100 SCOTTSDALE 85255

OWNER: FINISH LINE AUTO CLUB 3080 AIRWAY AVE. COSTA MESA, CA 92626 TONY PRINCIPLE

ARCHITECT: LGE DESIGN GROUP 1200 NORTH 52ND STREET PHOENIX, AZ. 85008 STUDIO DIRECTOR: MARK S. CONE

PROJECT SCOPE: APPROXIMATELY 92,502 SF OF: AUTO CONDOS (67 TOTAL UNITS) 13,916 SF OF: OFFICE / CLUBHOUSE

ASSESSOR PARCEL NO.: 215-07-230

CURRENT ZONING: I-1 PCD

PROPOSED ZONING: I-1 PCD

SITE AREA: +/- 293,754 S.F. (6.74 AC)

STORIES: (3) STORY (BUILDING A)
(1) STORY (BUILDING B)
(1) STORY (BUILDING C)
(1) STORY (BUILDING D)
(1) STORY (BUILDING E)

GROSS BUILDING S.F.: 125,504 S.F. TOTAL
63,020 S.F. (BUILDING A)
17,877 S.F. (BUILDING B)
17,337 S.F. (BUILDING C)
8,712 S.F. (BUILDING D)
18,558 S.F. (BUILDING E)

LOT COVERAGE: 33.2%

OCCUPANCY: A / S-1

CONSTRUCTION TYPE: V-B W/ A.F.E.S.

BUILDING HEIGHT: 49'-0" (BUILDING A)
32'-0" (BUILDING B)
32'-0" (BUILDING C)
32'-0" (BUILDING D)
32'-0" (BUILDING E)

PROJECT DESCRIPTION:

THE FINISH LINE AUTO CLUB PROJECT CONSISTS OF FIVE BUILDINGS (GARAGES WITH AN OFFICE AND CLUB SPACE) ON A 6.74 ACRE SITE LOCATED ON N PERIMETER DRIVE WHICH CURRENTLY HAS ONE BUILDING.

REQUIRED PARKING:

LOUNGE/OFFICE/PATIO: 13,916 S.F./250= 56 SPACES
STORAGE (1/50 UNITS): 67 UNITS/50 = 2 SPACES
TOTAL REQUIRED= 58 SPACES

PROVIDED PARKING= 112 SPACES
REGULAR PARKING= 106 SPACES
ACCESSIBLE PARKING= 6 SPACES
89 CARS/1000


GRAPHIC LEGEND

SYMBOL:	DESCRIPTION:
	MAIN ENTRY / EXIT
	FIRE HYDRANT - COORDINATE LOCATIONS WITH CIVIL DRAWINGS
	FIRE LANE (FIRE ACCESSIBILITY SITE PLAN). COORDINATE FINAL LOCATIONS W/ CIVIL
	INDICATES NEW SITEWORK
	INDICATES ADJACENT EXISTING SITE CONDITIONS
	INDICATES PROPERTY LINE
	LIGHT POLE. COORDINATE W/ ELECTRICAL DRAWINGS

GENERAL DRAWING NOTES

- REFER TO THE A0.X SERIES DRAWINGS FOR ARCHITECTURAL GENERAL NOTES, DRAWING, REFERENCE AND MATERIAL SYMBOLS AS WELL AS ABBREVIATIONS USED ON THIS DRAWING.
- FOR BASIC LIFE SAFETY AND CODE INFORMATION APPLYING TO THIS PROJECT, REFER TO G.X SERIES LOCATED PER THE PROJECT SHEET INDEX.
- REFER TO A2.X.X SERIES FOR ARCHITECTURAL FLOOR PLANS, ROOF PLANS, & TILT WALL COORDINATION INFORMATION
- REFER TO AND COORDINATE WITH CIVIL, LANDSCAPE, STRUCTURAL, MECHANICAL, AND ELECTRICAL DRAWINGS FOR ADDITIONAL SITE INFORMATION NOT SHOWN ON THIS DRAWING.
- SITE SCREEN WALLS A MAXIMUM 8'-0" ABOVE THE HIGHEST FINISHED GRADE OF THE PARKING AREA OR STREET CURB, WHICHEVER IS HIGHER
- REFER TO AND COORDINATE WITH CIVIL DRAWINGS FOR ALL FINISH GRADES.
- REFER TO A4.X.X SERIES DRAWINGS FOR ENLARGED EXTERIOR ELEVATIONS, BUILDING SECTIONS, TILT WALL ELEVATIONS, & WALL SECTIONS

VICINITY MAP

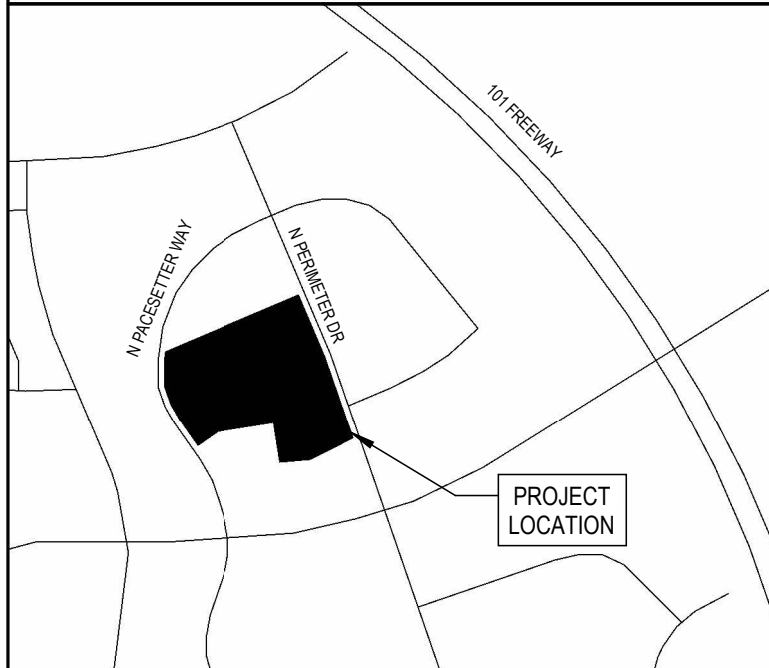

#	REVISION	DATE

NOT FOR CONSTRUCTION

SHEET TITLE:	ARCHITECTURAL SITE PLAN W/ AERIAL
ISSUE DATE:	04/11/25
DRAWN BY:	LGE DESIGN GROUP
CHECKED BY:	--
PROJECT No:	--