


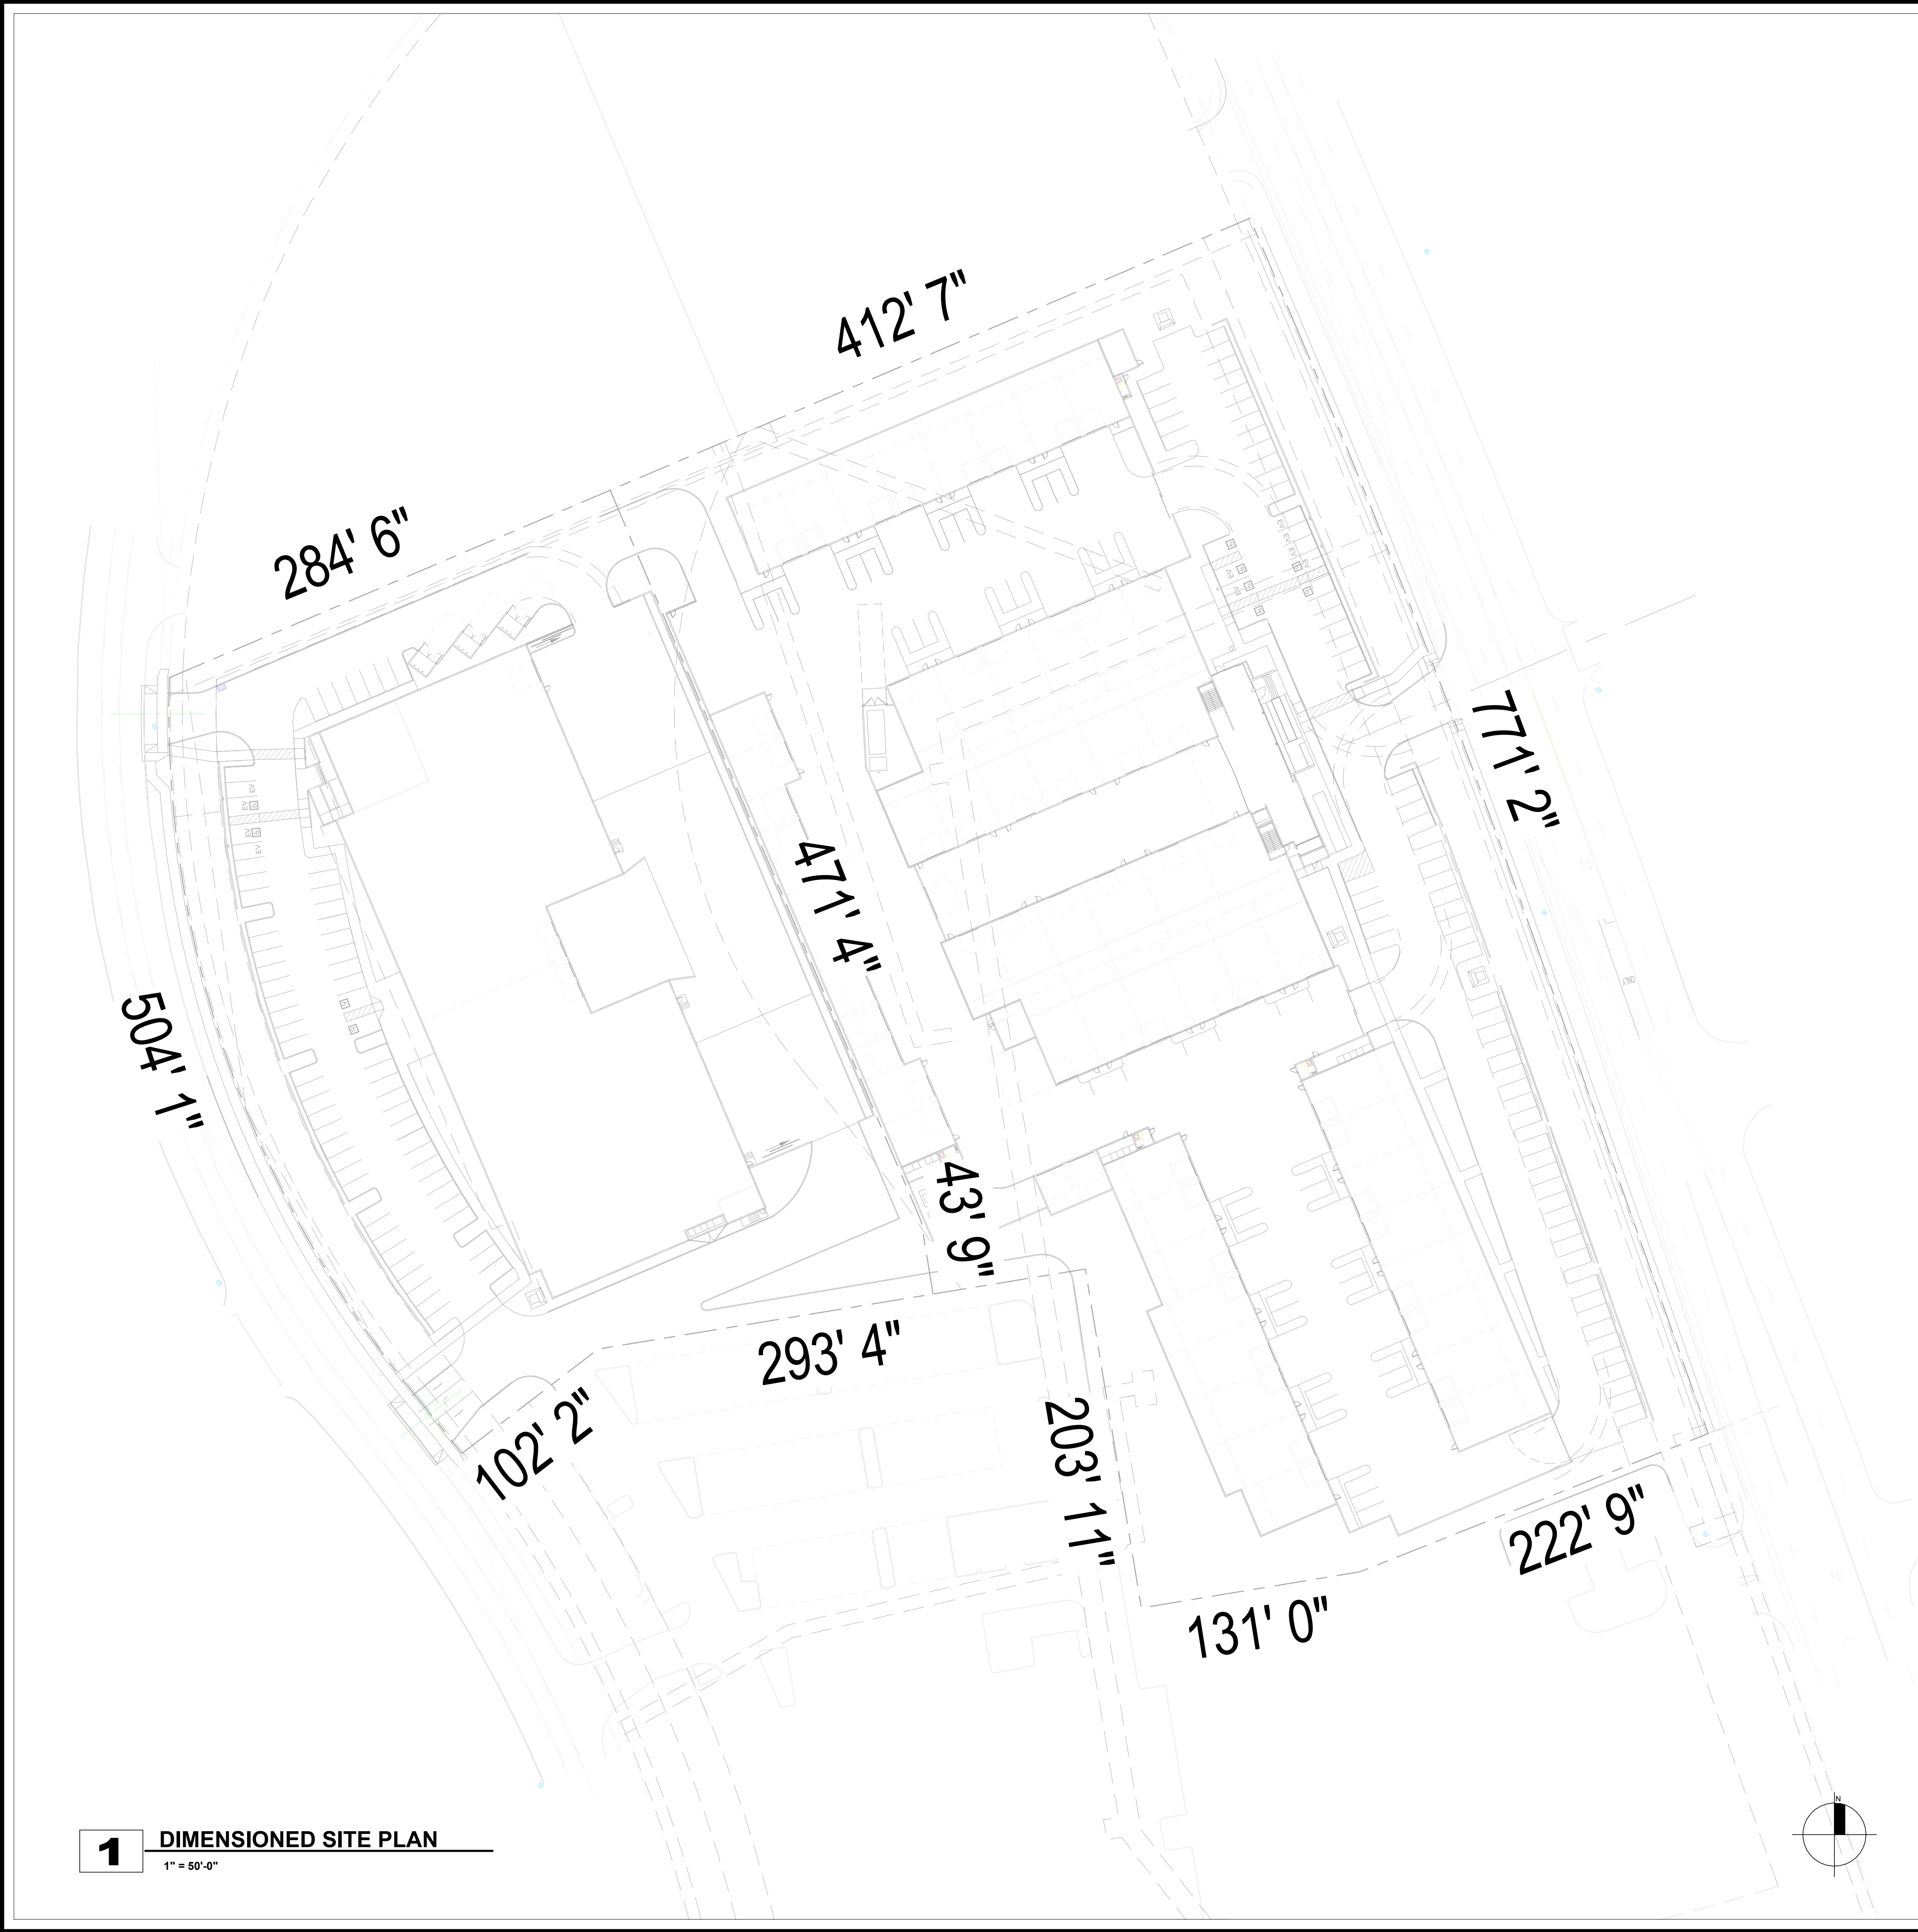

PROJECT DATA															
INDUSTRIAL - WEST LOT	AUTO CLUB - EAST LOT														
PROJECT ADDRESS: 17600 N PERIMETER DR 100 SCOTTSDALE 85255	PROJECT ADDRESS: 17600 N PERIMETER DR 100 SCOTTSDALE 85255														
OWNER: FINISH LINE AUTO CLUB 3080 AIRWAY AVE. COSTA MESA, CA 92626 TONY PRINCIPE	OWNER: FINISH LINE AUTO CLUB 3080 AIRWAY AVE. COSTA MESA, CA 92626 TONY PRINCIPE														
ARCHITECT: LGE DESIGN GROUP 1200 NORTH 52ND STREET PHOENIX, AZ. 85008 STUDIO DIRECTOR: MARK S. CONE	ARCHITECT: LGE DESIGN GROUP 1200 NORTH 52ND STREET PHOENIX, AZ. 85008 STUDIO DIRECTOR: MARK S. CONE														
PROJECT SCOPE: APPROXIMATELY 46,052 SF OF: WAREHOUSE 4,000 SF OF: OFFICE	PROJECT SCOPE: APPROXIMATELY 92,502 SF OF: AUTO CONDOS (67 TOTAL UNITS) 13,916 SF OF: OFFICE / CLUBHOUSE														
ASSESSOR PARCEL NO.: 215-07-230	ASSESSOR PARCEL NO.: 215-07-230														
CURRENT ZONING: I-1 PCD	CURRENT ZONING: I-1 PCD														
PROPOSED ZONING: I-1 PCD	PROPOSED ZONING: I-1 PCD														
SITE AREA: +/- 159,000 S.F. (3.65 AC)	SITE AREA: +/- 293,754 S.F. (6.74 AC)														
FAR - MAX: 80% = 127,200 S.F.	FAR - MAX: 80% = 235,003 S.F.														
FAR - PROPOSED: 31%= 50,052 S.F.	FAR - PROPOSED: 42%= 125,504 S.F.														
STORIES: 1 STORY	STORIES: (3) STORY (BUILDING A) (1) STORY (BUILDING B) (1) STORY (BUILDING C) (1) STORY (BUILDING D) (1) STORY (BUILDING E)														
GROSS BUILDING S.F.: 48,778 S.F. TOTAL	GROSS BUILDING S.F.: 125,504 S.F. TOTAL 63,020 S.F. (BUILDING A) 17,877 S.F. (BUILDING B) 17,337 S.F. (BUILDING C) 8,712 S.F. (BUILDING D) 18,558 S.F. (BUILDING E)														
LOT COVERAGE: 31.5%	LOT COVERAGE: 33.2%														
OCCUPANCY: B / S-1	OCCUPANCY: A / S-1														
CONSTRUCTION TYPE: V-B W/ A.F.E.S.	CONSTRUCTION TYPE: V-B W/ A.F.E.S.														
BUILDING HEIGHT: 38'-0"	BUILDING HEIGHT: 49'-0" (BUILDING A) 32'-0" (BUILDING B) 32'-0" (BUILDING C) 32'-0" (BUILDING D) 32'-0" (BUILDING E)														
PROJECT DESCRIPTION: THE PACESETTER WAY PROJECT CONSISTS OF ONE BUILDING (WAREHOUSE WITH AN OFFICE) ON A 3.65 ACRE SITE LOCATED ON N PACESETTER WAY WHICH CURRENTLY HAS NO BUILDINGS.	PROJECT DESCRIPTION: THE FINISH LINE AUTO CLUB PROJECT CONSISTS OF FIVE BUILDINGS (GARAGES WITH AN OFFICE AND CLUB SPACE) ON A 6.74 ACRE SITE LOCATED ON N PERIMETER DRIVE WHICH CURRENTLY HAS ONE BUILDING.														
REQUIRED PARKING: WAREHOUSE: 46,178 S.F./800= 58 SPACES OFFICE: 2,600 S.F./300= 9 SPACES TOTAL REQUIRED= 67 SPACES PROVIDED PARKING= 69 SPACES REGULAR PARKING= 65 SPACES ACCESSIBLE PARKING REQUIRED= 71'0.04= 3 SPACES ACCESSIBLE PARKING PROVIDED= 4 SPACES 1.42 CARS/1000 REQUIRED EV CHARGING (4% OF PARKING): 69'0.04 = 3 PROVIDED EV CHARGING: 4 SPACES REQUIRED EV CAPABLE (10% OF PARKING): 69'0.10 = 7 7 EV CAPABLE SPACES PROVIDED *FINAL LOCATIONS TBD	REQUIRED PARKING: CLUB (LOUNGE & PATIO) 11,537 S.F./250: 47 SPACES OFFICE: 2,379 S.F./300= 8 SPACES STORAGE (1150 UNITS): 67 UNITS/50 = 2 SPACES TOTAL REQUIRED= 57 SPACES PROVIDED PARKING= 105 SPACES REGULAR PARKING= 99 SPACES ACCESSIBLE PARKING REQUIRED= 106'0.04 = 5 ACCESSIBLE PARKING PROVIDED= 6 SPACES REQUIRED EV CHARGING (4% OF PARKING): 106'0.04 = 5 PROVIDED EV CHARGING: 6 SPACES REQUIRED EV CAPABLE (10% OF PARKING): 106'0.10 = 11 11 EV CAPABLE SPACES PROVIDED *FINAL LOCATIONS TBD														
GRAPHIC LEGEND	GENERAL DRAWING NOTES														
<table><tr><th>SYMBOL:</th><th>DESCRIPTION:</th></tr><tr><td></td><td>MAIN ENTRY / EXIT</td></tr><tr><td></td><td>FIRE HYDRANT - COORDINATE LOCATIONS WITH CIVIL DRAWINGS</td></tr><tr><td></td><td>FIRE LANE (FIRE ACCESSIBILITY SITE PLAN). COORDINATE FINAL LOCATIONS W/ CIVIL INDICATES NEW SITEWORK</td></tr><tr><td></td><td>INDICATES ADJACENT EXISTING SITE CONDITIONS</td></tr><tr><td></td><td>INDICATES PROPERTY LINE</td></tr><tr><td></td><td>LIGHT POLE. COORDINATE W/ ELECTRICAL DRAWINGS</td></tr></table>	SYMBOL:	DESCRIPTION:		MAIN ENTRY / EXIT		FIRE HYDRANT - COORDINATE LOCATIONS WITH CIVIL DRAWINGS		FIRE LANE (FIRE ACCESSIBILITY SITE PLAN). COORDINATE FINAL LOCATIONS W/ CIVIL INDICATES NEW SITEWORK		INDICATES ADJACENT EXISTING SITE CONDITIONS		INDICATES PROPERTY LINE		LIGHT POLE. COORDINATE W/ ELECTRICAL DRAWINGS	A. REFER TO THE A0.X SERIES DRAWINGS FOR ARCHITECTURAL GENERAL NOTES, DRAWING, REFERENCE AND MATERIAL SYMBOLS AS WELL AS ABBREVIATIONS USED ON THIS DRAWING. B. FOR BASIC LIFE SAFETY AND CODE INFORMATION APPLYING TO THIS PROJECT, REFER TO G.X SERIES LOCATED PER THE PROJECT SHEET INDEX. C. REFER TO A2.X.X SERIES FOR ARCHITECTURAL FLOOR PLANS, ROOF PLANS, & TILT WALL COORDINATION INFORMATION D. REFER TO AND COORDINATE WITH CIVIL, LANDSCAPE, STRUCTURAL, MECHANICAL, AND ELECTRICAL DRAWINGS FOR ADDITIONAL SITE INFORMATION NOT SHOWN ON THIS DRAWING. E. SITE SCREEN WALLS A MAXIMUM 8'-0" ABOVE THE HIGHEST FINISHED GRADE OF THE PARKING AREA OR STREET CURB. WHICHEVER IS HIGHER F. REFER TO AND COORDINATE WITH CIVIL DRAWINGS FOR ALL FINISH GRADES. G. REFER TO A4.X.X SERIES DRAWINGS FOR ENLARGED EXTERIOR ELEVATIONS, BUILDING SECTIONS, TILT WALL ELEVATIONS, & WALL SECTIONS
SYMBOL:	DESCRIPTION:														
	MAIN ENTRY / EXIT														
	FIRE HYDRANT - COORDINATE LOCATIONS WITH CIVIL DRAWINGS														
	FIRE LANE (FIRE ACCESSIBILITY SITE PLAN). COORDINATE FINAL LOCATIONS W/ CIVIL INDICATES NEW SITEWORK														
	INDICATES ADJACENT EXISTING SITE CONDITIONS														
	INDICATES PROPERTY LINE														
	LIGHT POLE. COORDINATE W/ ELECTRICAL DRAWINGS														
	VICINITY MAP														

LGEDESIGNGROUP

1200 N. 52nd Street•Phoenix, AZ•85008

P. 480.966.4001

FINISH LINE AUTO

17600 N PERIMETER DR #100

SCOTTSDALE, AZ 85255

LGEDESIGNBUILD

#	REVISION	DATE

NOT FOR CONSTRUCTION

SHEET TITLE:
DIMENSIONED SITE PLAN

ISSUE DATE:
04/07/25

DRAWN BY:
LGE DESIGN GROUP

CHECKED BY:
--

PROJECT No:
--

A1.1.7

1

DIMENSIONED SITE PLAN

1" = 50'-0"