



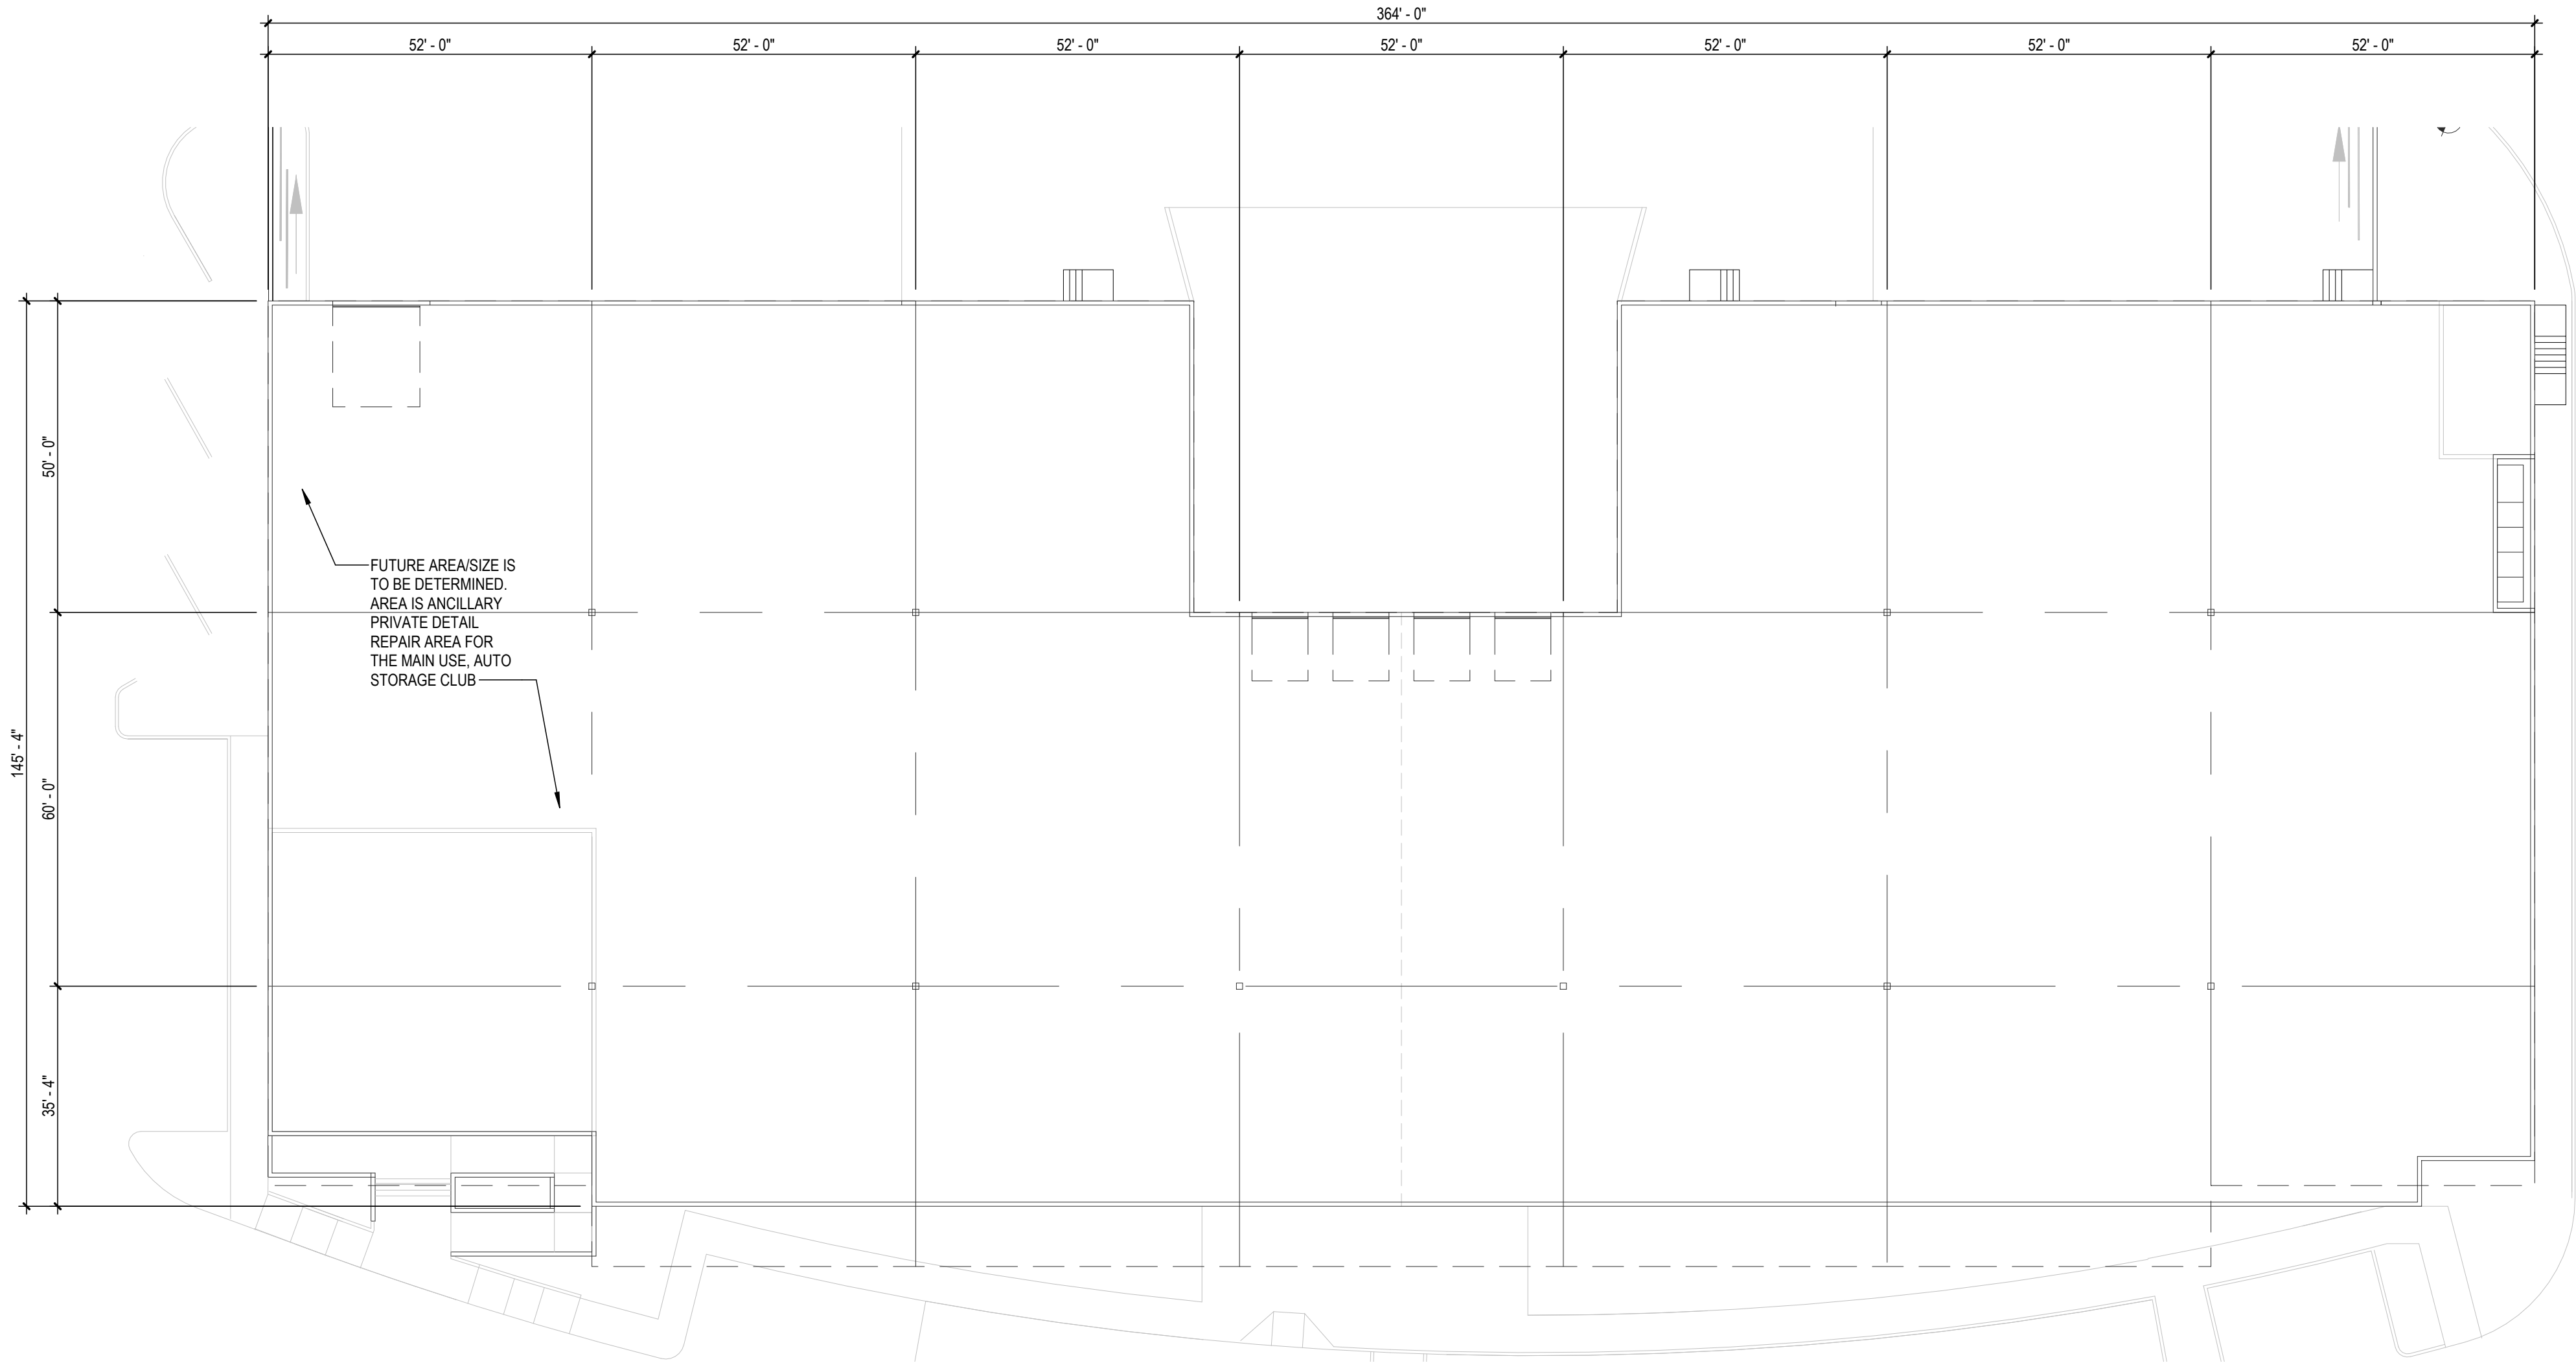

**1 FLOOR PLAN**  
1" = 20'-0"

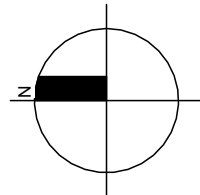

|  | GENERAL FINISH & CORE SHELL NOTES   | AREA CALCULATIONS | REFERENCE KEYNOTES | GENERAL DRAWING NOTES |
|--|---|-------------------|--------------------|-----------------------|
|  | <div><div>1. SLAB -</div><div>REFERENCE STRUCTURAL DRAWINGS FOR SLAB THICKNESS. CONCRETE SLAB ON GRADE OVER 15 MIL. VAPOR BARRIER OVER 4" ABC. REFERENCE PLAN FOR EXTENTS OF VAPOR BARRIER.</div><div>2. PAINT -</div><div>ASSUME STANDARD WHITE PAINT FOR INSIDE FACES OF TILT PANELS AND INTERIOR PARTITIONS UNLESS OTHERWISE NOTED. COLUMNS YELLOW FROM FINISH FLOOR TO + 10'-0". COLUMNS WHITE FROM +10'-0" TO STRUCTURE ABOVE.</div><div>3. CEILINGS -</div><div>OPEN TO DECK ALL AREAS (SHELL CONDITION) UNLESS OTHERWISE NOTED. REFERENCE REFLECTED CEILING PLAN(S)</div><div>4. DOORS -</div><div>REFER TO DOOR SCHEDULE (A9.2.X SERIES) FOR DOOR TYPES, DIMENSIONS, MATERIALS, TYPICAL DETAILS, &amp; HARDWARE INFORMATION.</div><div>DOCK DOORS:</div><div>-PROVIDE (2) DOCK BUMPERS AT EACH DOCK.</div><div>-PROVIDE OMEGA 48" "Z-GUARDS" AT ALL INTERIOR SIDE OVERHEAD DOOR JAMBS (TYP.)</div><div>5. STOREFRONT-</div><div>BLACK ANODIZED ALUMINUM STOREFRONT SEE GLAZING ELEVATIONS FOR MULLION LAYOUT. GLAZING TO BE SOLARBAN 60, LOW-E SOLAR COOL, SOLAR BLUE</div><div>6. ROOF-</div><div><b><u>R-38 MIN. TOTAL</u></b> - BATT INSULATION W/ WHITE SCRIM UNDER PANELIZED WOOD ROOF DECK SYSTEM. MIN. SLOPE 1/4"12"</div></div> <div></div> <div></div> <div><div>A. REFERENCE TO THE A0.X SERIES DRAWINGS FOR ARCHITECTURAL GENERAL NOTES, MATERIAL SYMBOLS, ABBREVIATIONS, AND DIMENSIONING CONVENTIONS USED ON THIS DRAWING.</div><div>B. FOR BASIC LIFE SAFETY AND CODE INFORMATION APPLYING TO THIS PROJECT, REFER TO G.X SERIES LOCATED PER THE PROJECT DRAWING INDEX.</div><div>C. REFER TO A3.X.X SERIES FOR REFLECTED CEILING PLAN</div><div>D. REFER TO A5.X.X SERIES FOR ENCLOSURE INFORMATION, PARTITION SYSTEMS TYPES AND DETAILS.</div><div>E. [APPLICABLE FOR FOR INTERIOR SCOPE ONLY] - REFER TO THE A9.X.X SERIES DRAWINGS FOR INTERIOR DETAILS, TYPES, AND DETAILS.</div><div>F. [APPLICABLE FOR FOR INTERIOR SCOPE ONLY] - REFER TO THE 'AF' SERIES DRAWINGS FOR INTERIOR FINISH INFORMATION.</div><div>G. [APPLICABLE FOR FOR INTERIOR SCOPE ONLY] - REFER TO THE 'AF' SERIES DRAWINGS FOR INTERIOR FURNISHING INFORMATION.</div></div> |                   |                    |                       |

LGE

DESIGNGROUP

17200 N 68th Ave Suite 100 Phoenix, AZ 85018  
P: 480.888.0098

FINISH LINE AUTO

17600 N PERIMETER DR #100  
SCOTTSDALE, AZ 85255

LGE

DESIGNBUILD

| # | REVISION | DATE |
|---|----------|------|
|   |          |      |
|   |          |      |
NOT FOR CONSTRUCTION

SHEET TITLE:

GROUND LEVEL FLOOR PLAN

ISSUE DATE:

07/07/25

DRAWN BY:

LGE DESIGN GROUP

CHECKED BY:

--

PROJECT No:

--

A2.0.1