

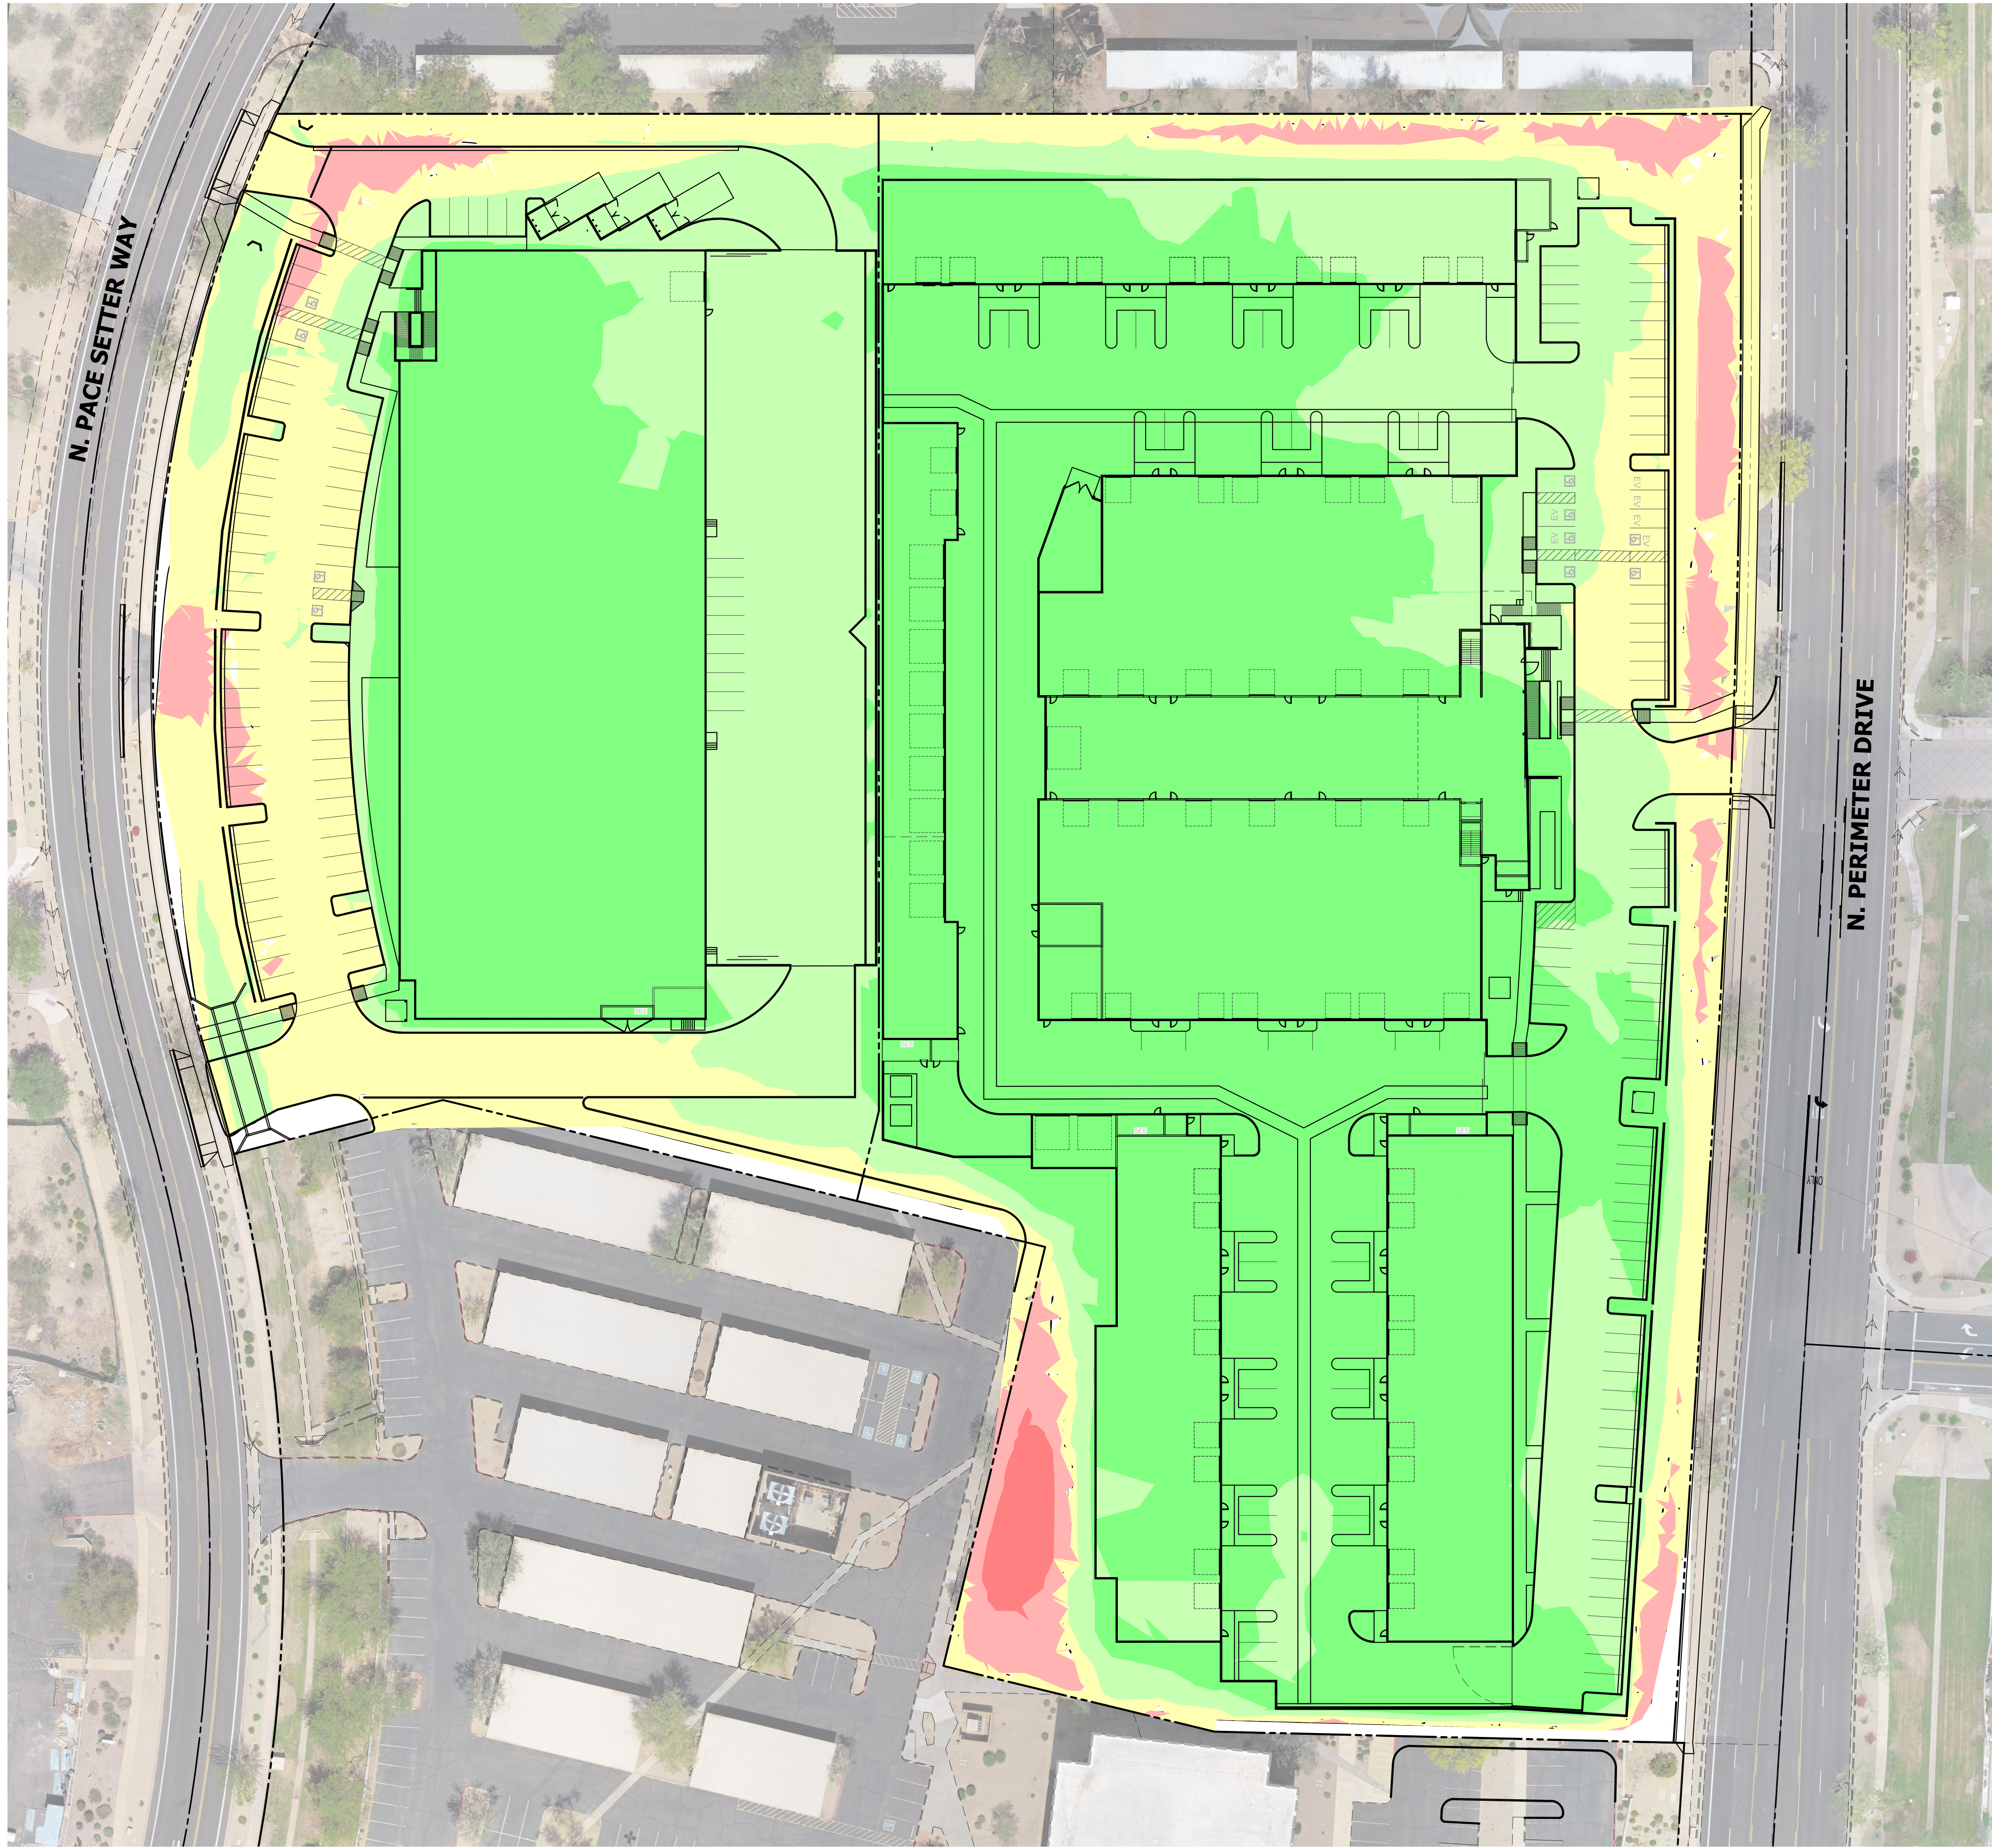


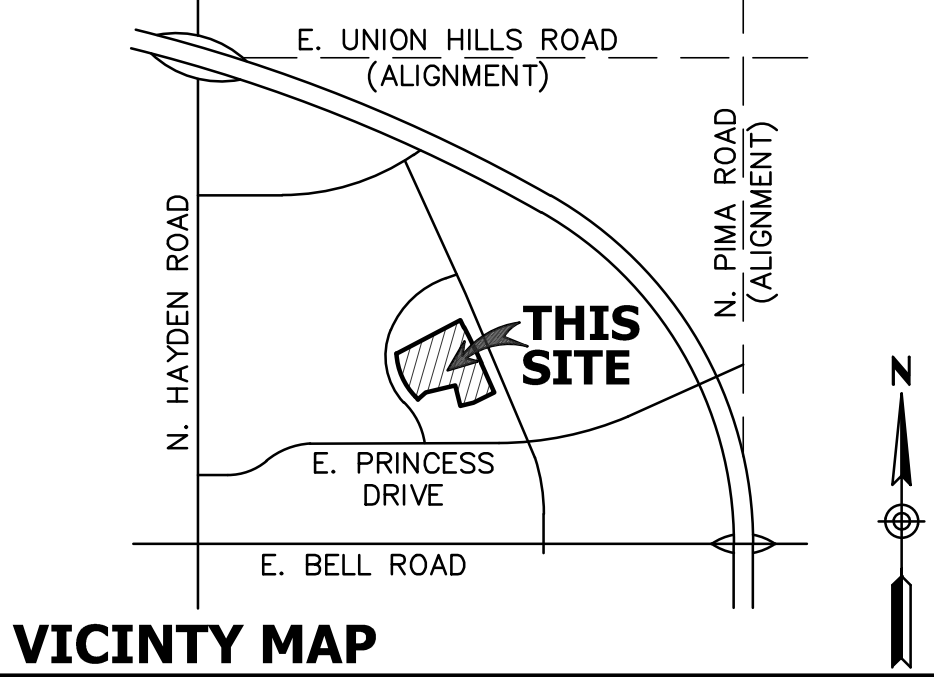

CUT/FILL EXHIBIT  
FOR  
FINISH LINE AUTO CLUB  
PRINCESS DRIVE AND LOOP 101  
SCOTTSDALE, ARIZONA

LOT 1 OF FNBA CENTER, AS RECORDED IN BOOK 844 OF MAPS, PAGE 47 OF MARICOPA COUNTY, ARIZONA, LOCATED WITHIN THE SOUTH HALF OF SECTION 36, TOWNSHIP 4 NORTH, RANGE 4 EAST, OF THE GILA AND SALT RIVER MERIDIAN, MARICOPA COUNTY, ARIZONA.

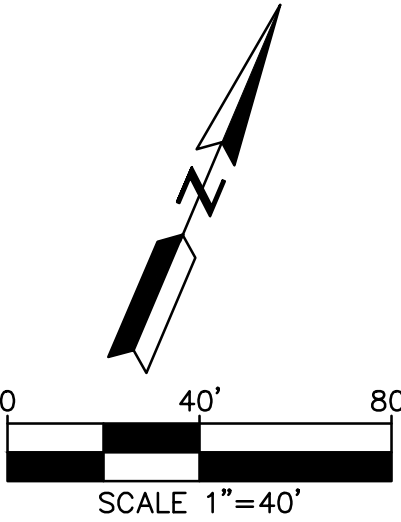

| Elevations Table |                   |                   |             |
|------------------|-------------------|-------------------|-------------|
| Number           | Minimum Elevation | Maximum Elevation | Color       |
| 1                | 4.0               | 10.0              | Green       |
| 2                | 1.0               | 4.0               | Yellow      |
| 3                | -1.0              | 1.0               | Light Green |
| 4                | -4.0              | 1.0               | Red         |
| 5                | -10.0             | -4.0              | Dark Red    |

| NO. | DATE | REVISION | BY |
|-----|------|----------|----|
|     |      |          |    |
|     |      |          |    |
|     |      |          |    |
|     |      |          |    |

PURPOSE:  
1ST DR SUBMITTAL

DESIGN BY: BKS  
DRAWN BY: MM  
CHECKED BY: BKS

**HUNTER**  
ENGINEERING  
10446 NORTH 74TH STREET  
SUITE 140  
SCOTTSDALE, AZ 85258  
P 480 991 3985

CIVIL AND SURVEY



CUT/FILL EXHIBIT  
FOR  
FINISH LINE AUTO CLUB  
PRINCESS DRIVE AND LOOP 101  
SCOTTSDALE, ARIZONA



THESE PLANS ARE  
NOT APPROVED FOR  
CONSTRUCTION  
WITHOUT AN  
APPROVED SIGNATURE  
FROM THE GOVERNING  
MUNICIPALITY.

PROJECT NAME:  
FINISH LINE  
AUTO  
CLUB

HE NO.: LGEC332  
SCALE: 1"=40'

SHEET:  
**1**