

ABBREVIATIONS


APN	ASSESSOR PARCEL NUMBER
AC	ACRES
BK.	BOOK
B.S.L.	BUILDING SETBACK LINE
C	CALCULATED
ESMT	EASEMENT
ESA	EMERGENCY AND SERVICE ACCESS
EX	EXISTING
M.C.R.	MARICOPA COUNTY RECORDER
M	MEASURED
PG.	PAGE
PROP	PROPOSED
PUE	PUBLIC UTILITY EASEMENT
R	RECORDED
R/W	RIGHT-OF-WAY
SF	SQUARE FEET
VNAE	VEHICULAR NON-ACCESS EASEMENT
WSF	WATER AND SEWER FACILITIES

LEGEND


CENTERLINE	---
RIGHT OF WAY	---
PROPERTY LINE	---
EASEMENT	---
MONUMENT LINE	---
SETBACK LINE	---
PK NAIL/WASHER	△
CHISELED X	×
IRON BAR	⊙
BRASS CAP FLUSH	⊙
ALUMINUM CAP FLUSH	⊙

PRELIMINARY PLAT FOR FINISH LINE AUTO CLUB PRINCESS DRIVE AND LOOP 101 SCOTTSDALE, ARIZONA

LOT 1 OF FNBA CENTER, AS RECORDED IN BOOK 844 OF MAPS, PAGE 47 OF MARICOPA COUNTY, ARIZONA, LOCATED WITHIN THE SOUTH HALF OF SECTION 36, TOWNSHIP 4 NORTH, RANGE 4 EAST, OF THE GILA AND SALT RIVER MERIDIAN, MARICOPA COUNTY, ARIZONA.

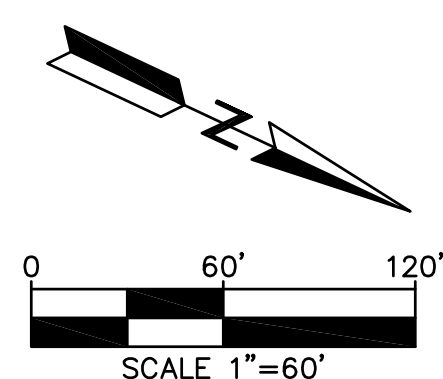


FOUND BRASS CAP FLUSH
MARKED CITY OF SCOTTSDALE
RLS 28236
N89°55'10"E(M)
15.06'(M)
W. 1/4 COR. SEC. 36, T.4N., R.4E.,
FOUND PK NAIL WITH TAG MARKED
RLS 28236

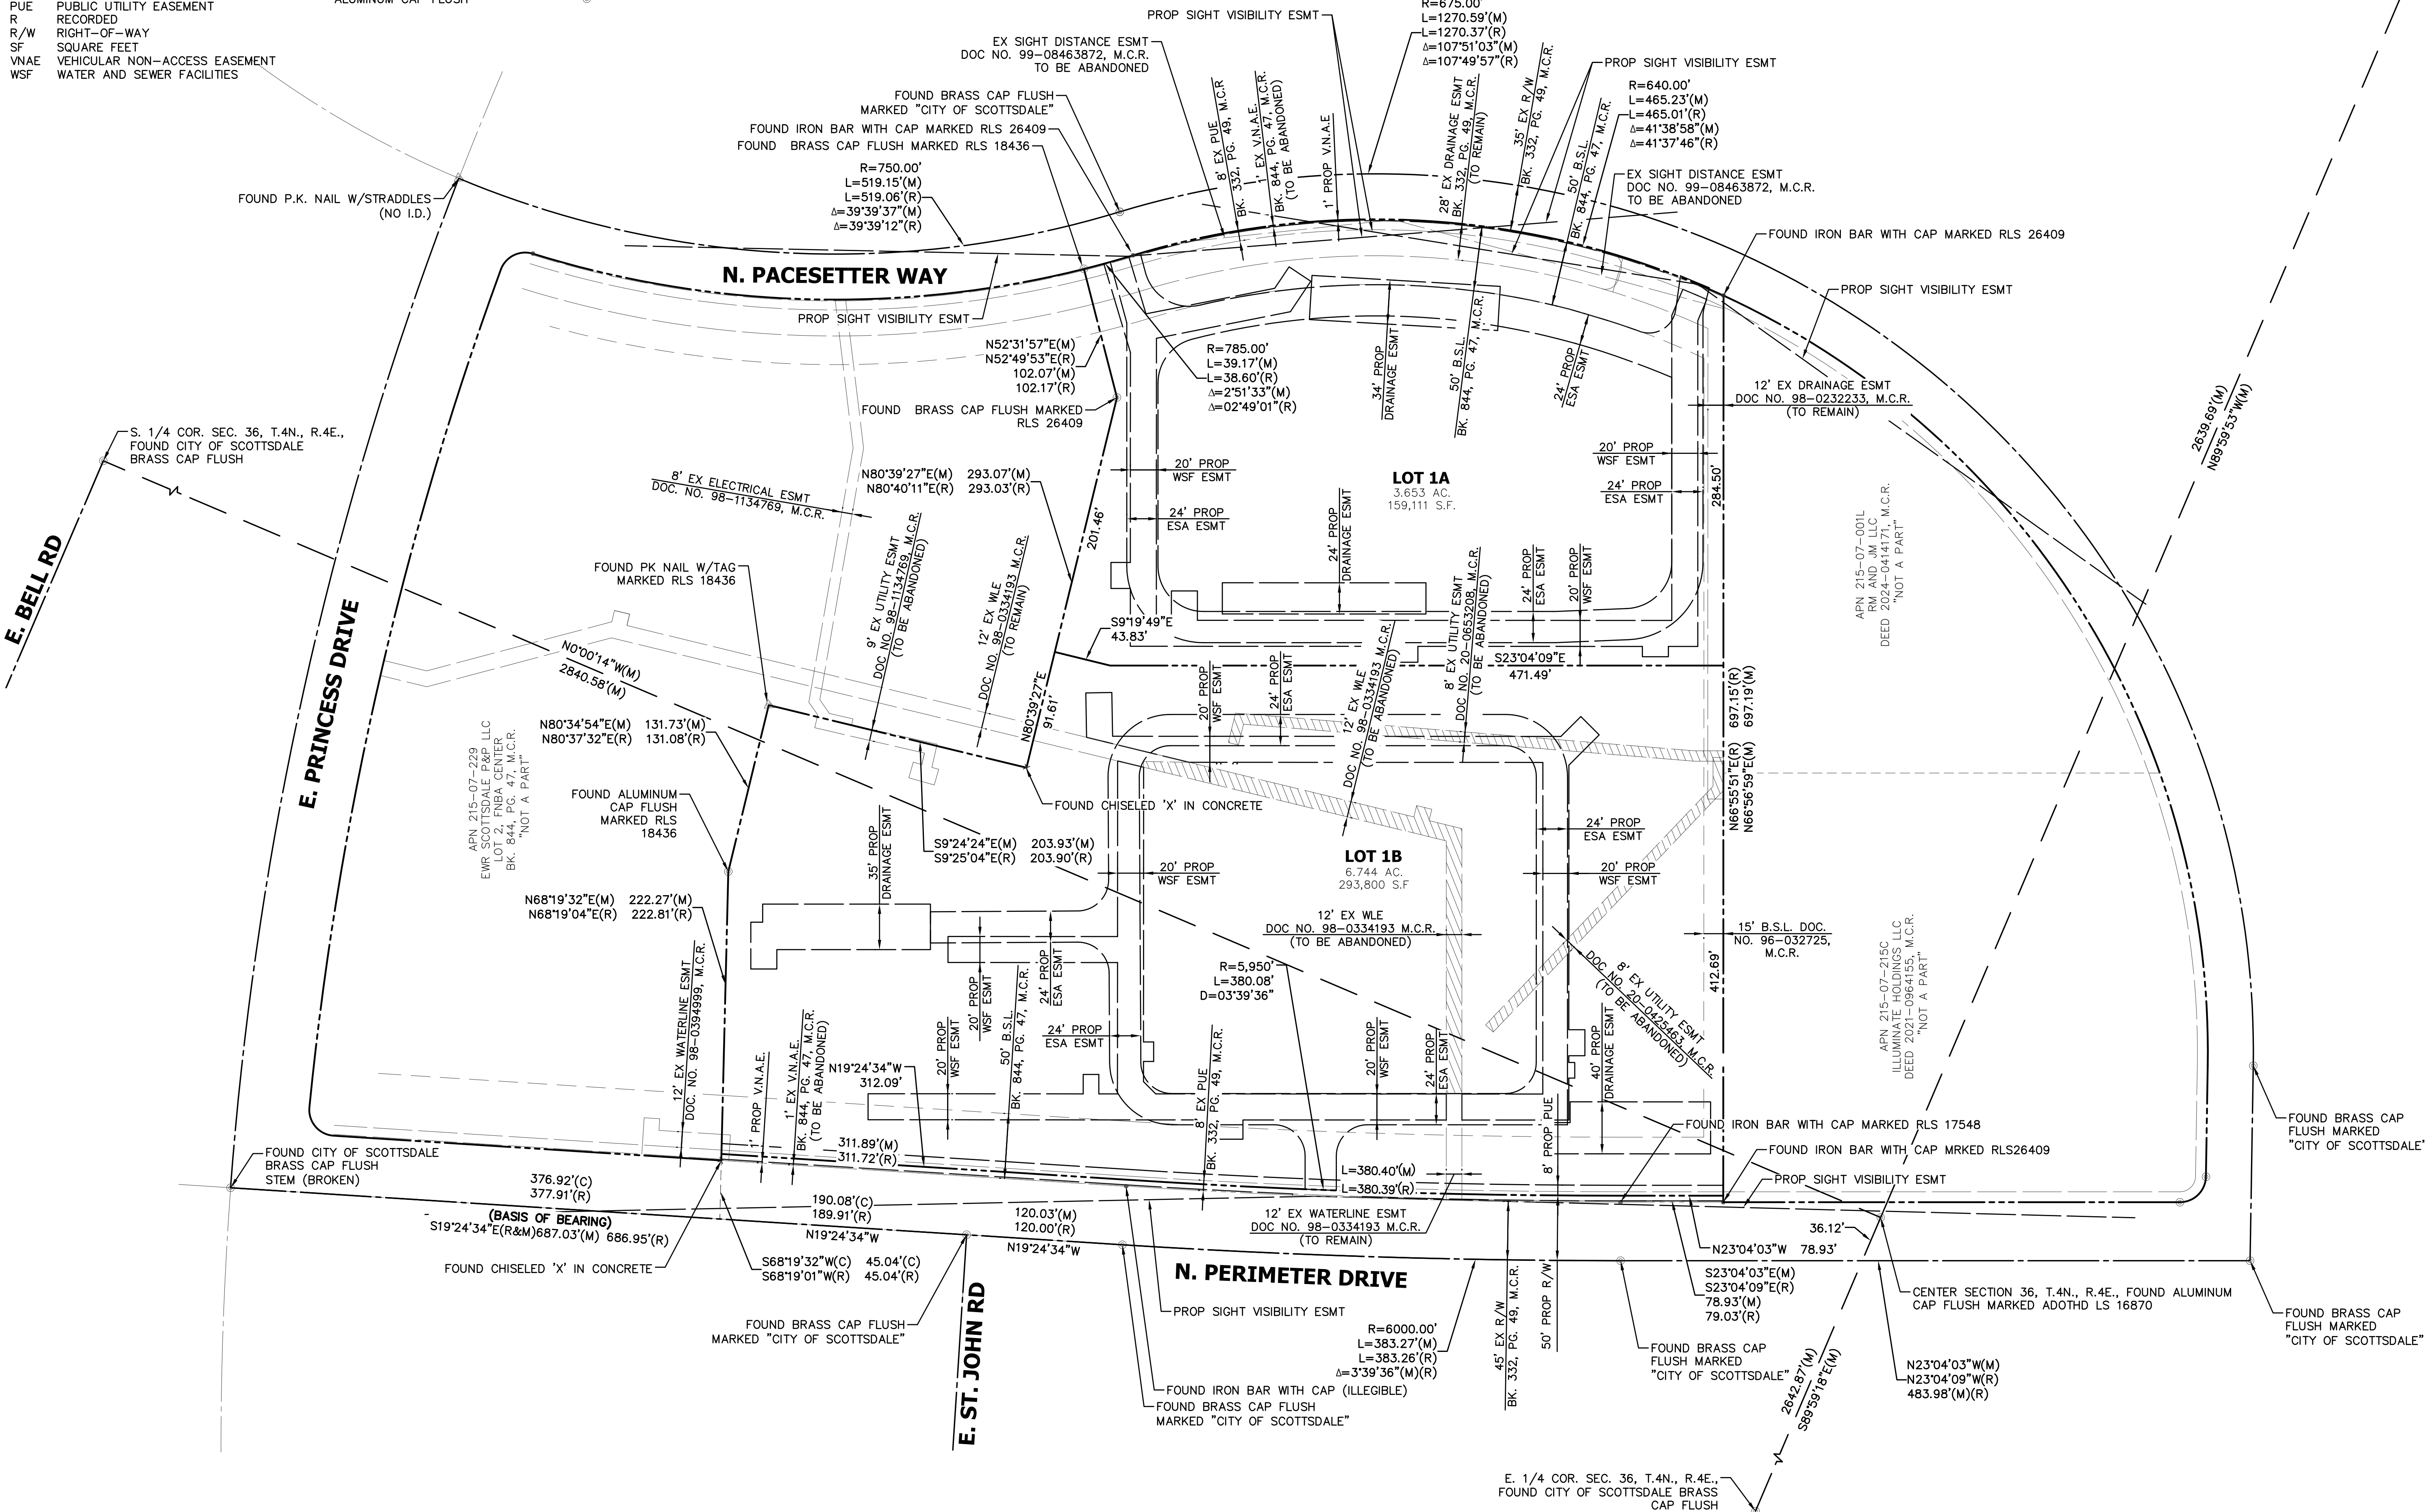

NO.	DATE	REVISION

DESIGN BY: **MM**
DRAWN BY: **BKS**
CHECKED BY: **BKS**

HUNTER
ENGINEERING
10446 NORTH 74TH STREET
SUITE 140
SCOTTSDALE, AZ 85258
P 480 991 3985

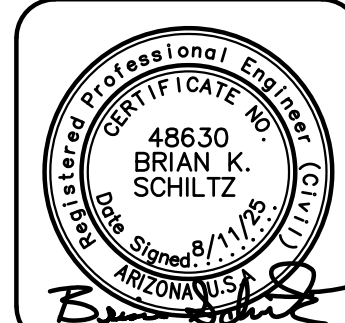

**PRELIMINARY PLAT
FOR
FINISH LINE AUTO CLUB
PRINCESS DRIVE AND LOOP 101
SCOTTSDALE, ARIZONA**

CONTACT ARIZONA 811 AT LEAST 2 FULL
WORKING DAYS BEFORE YOU BEGIN EXCAVATION
AR ZONA811
CALL 811 OR CLICK ARIZONA811.COM

THESE PLANS ARE
NOT APPROVED FOR
CONSTRUCTION
WITHOUT AN
APPROVED SIGNATURE
FROM THE GOVERNING
MUNICIPALITY.

**PROJECT NAME:
FINISH LINE
AUTO
CLUB**

HE NO.: LGEC332
SCALE: 1"=60'

SHEET:
PP