


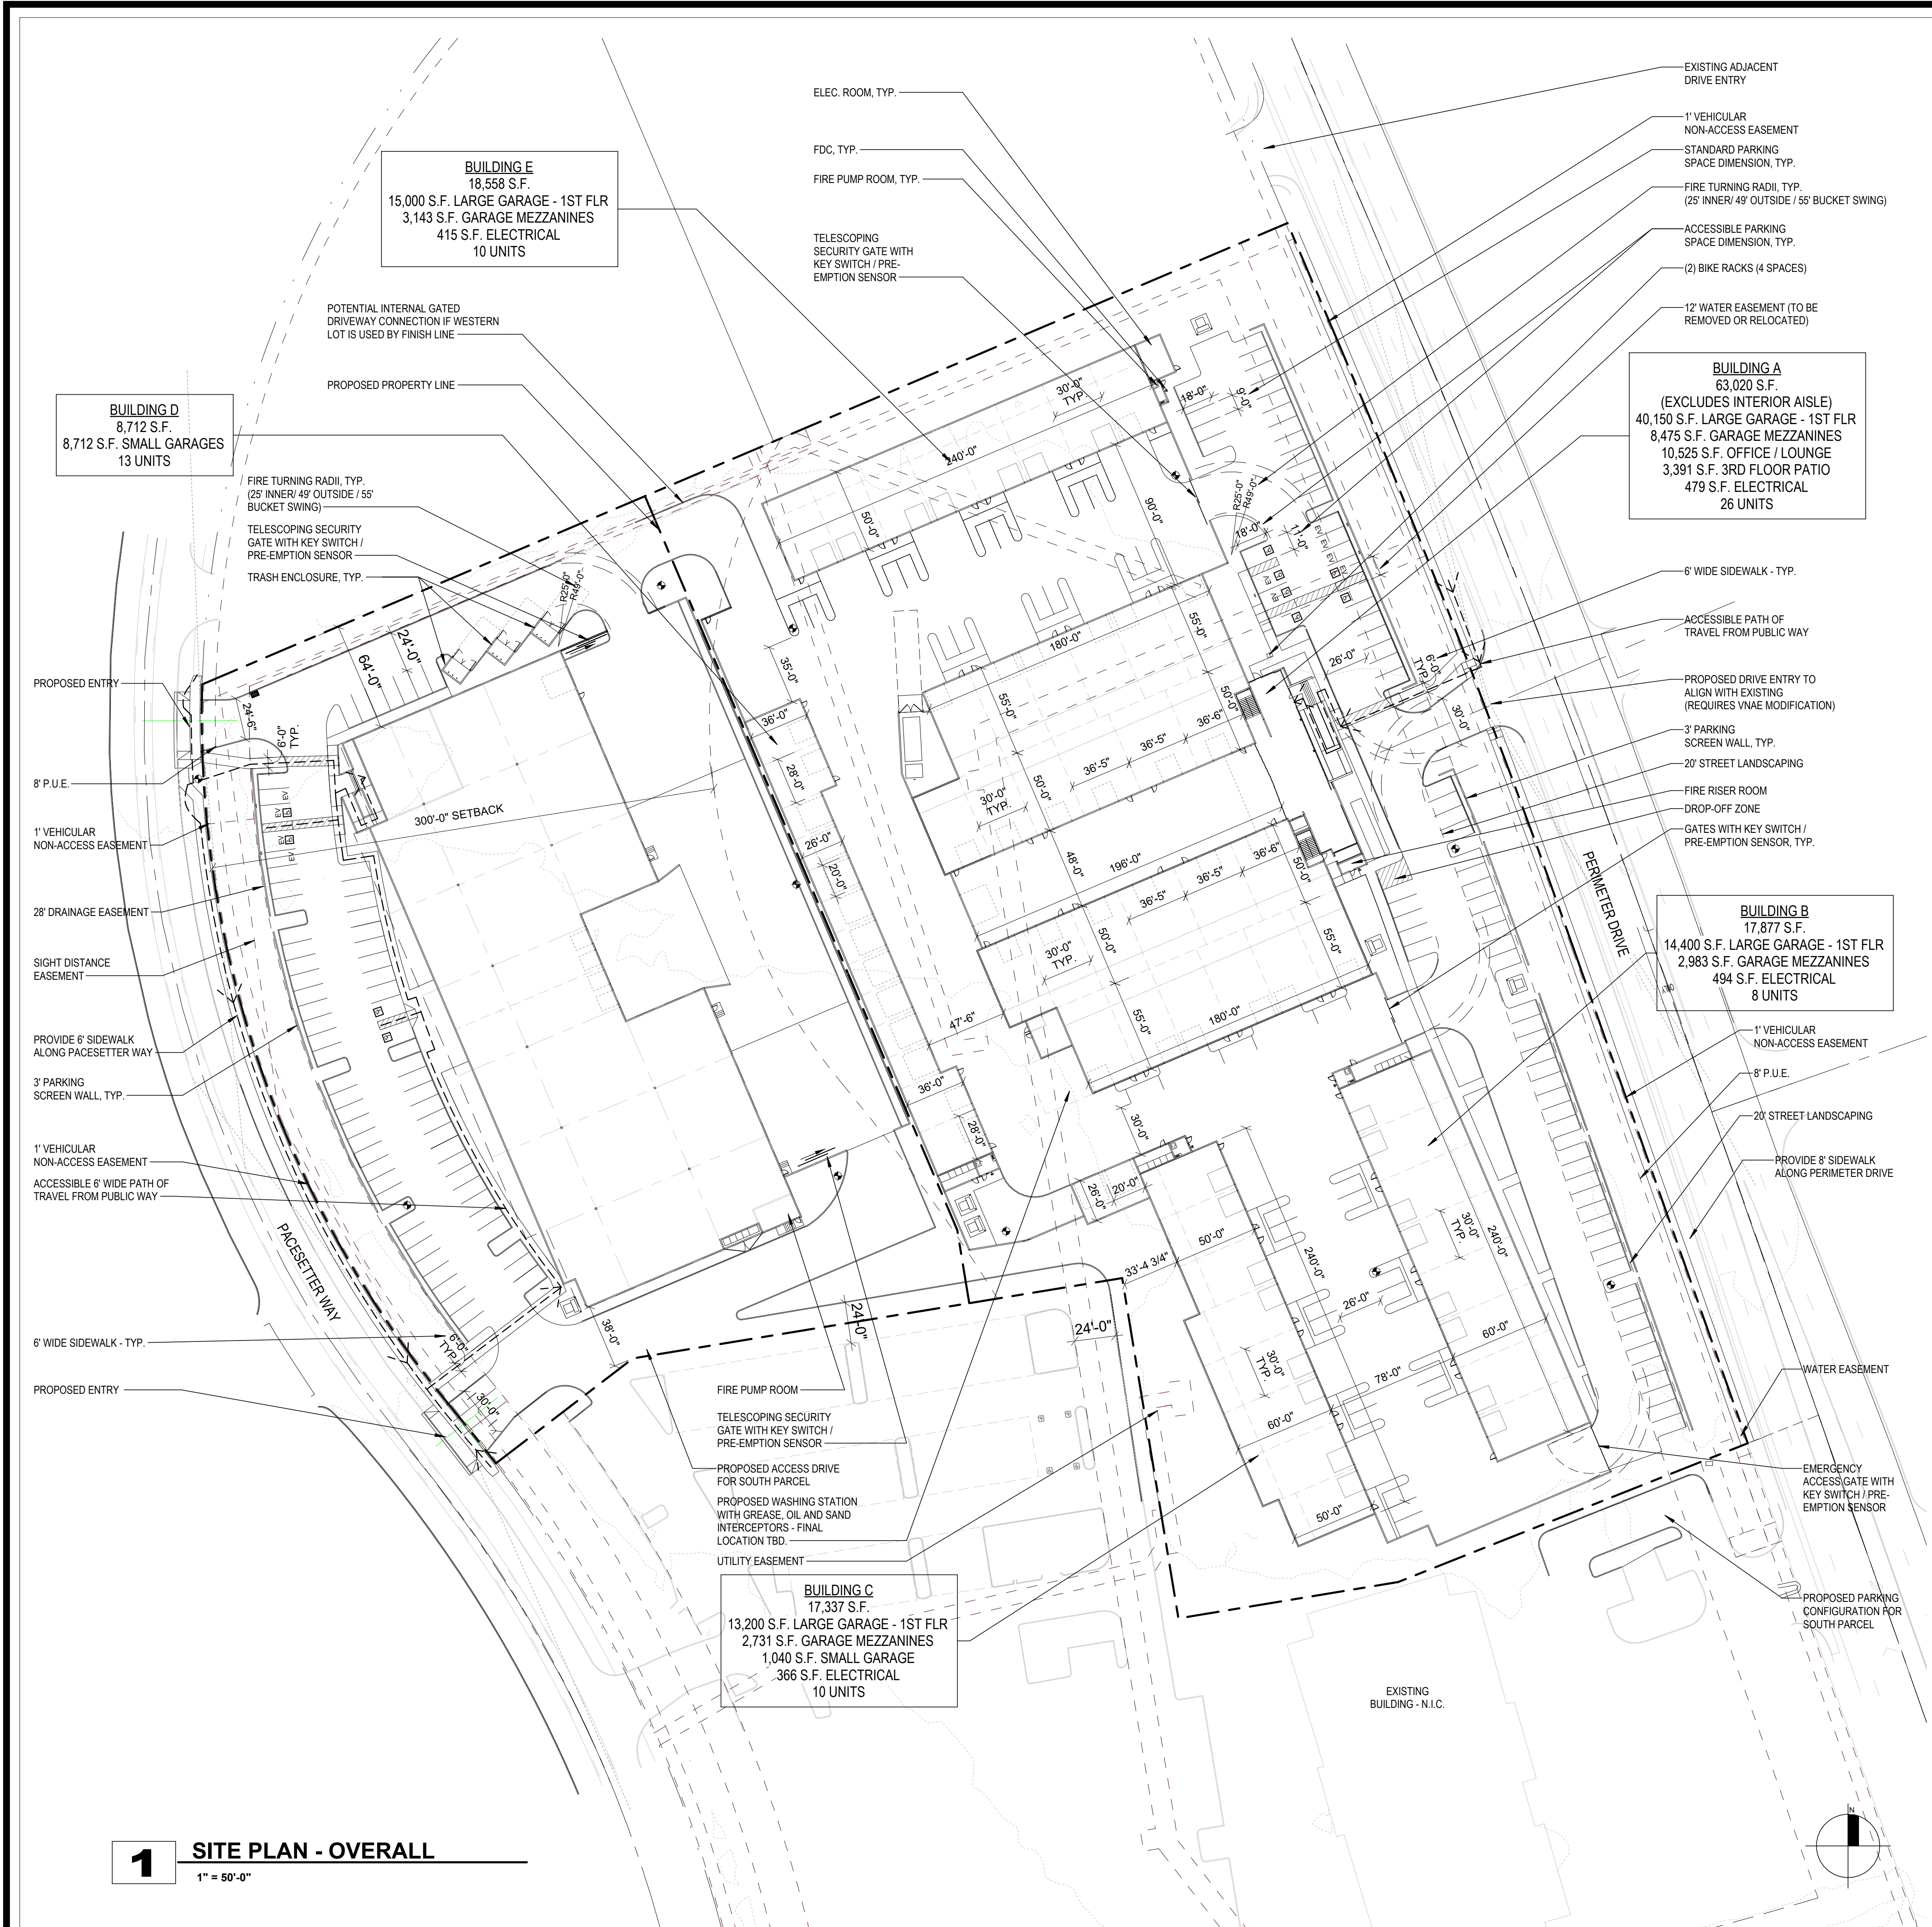

1 SITE PLAN - OVERALL
1" = 50'-0"

PROJECT DATA

INDUSTRIAL - WEST LOT		AUTO CLUB - EAST LOT	
PROJECT ADDRESS:	17600 N PERIMETER DR 100 SCOTTSDALE 85255	PROJECT ADDRESS:	17600 N PERIMETER DR 100 SCOTTSDALE 85255
OWNER:	FINISH LINE AUTO CLUB 3080 AIRWAY AVE. COSTA MESA, CA 92626 TONY PRINCIPE	OWNER:	FINISH LINE AUTO CLUB 3080 AIRWAY AVE. COSTA MESA, CA 92626 TONY PRINCIPE
ARCHITECT:	LGE DESIGN GROUP 1200 NORTH 52ND STREET PHOENIX, AZ 85008 STUDIO DIRECTOR: MARK S. CONE	ARCHITECT:	LGE DESIGN GROUP 1200 NORTH 52ND STREET PHOENIX, AZ 85008 STUDIO DIRECTOR: MARK S. CONE
PROJECT SCOPE:	APPROXIMATELY 46,052 SF OF: WAREHOUSE 4,000 SF OF: OFFICE	PROJECT SCOPE:	APPROXIMATELY 92,502 SF OF: AUTO CONDOS (67 TOTAL UNITS) 13,916 SF OF: OFFICE / CLUBHOUSE
ASSESSOR PARCEL NO.:	215-07-230	ASSESSOR PARCEL NO.:	215-07-230
CURRENT ZONING:	I-1 PCD	CURRENT ZONING:	I-1 PCD
PROPOSED ZONING:	I-1 PCD	PROPOSED ZONING:	I-1 PCD
SITE AREA:	+/- 159,000 S.F. (3.65 AC)	SITE AREA:	+/- 293,754 S.F. (6.74 AC)
FAR - MAX:	80% = 127,200 S.F.	FAR - MAX:	80% = 235,003 S.F.
FAR - PROPOSED:	31% = 50,052 S.F.	FAR - PROPOSED:	42% = 125,504 S.F.
STORIES:	1 STORY	STORIES:	(3) STORY (BUILDING A) (1) STORY (BUILDING B) (1) STORY (BUILDING C) (1) STORY (BUILDING D) (1) STORY (BUILDING E)
GROSS BUILDING S.F.:	48,778 S.F. TOTAL	GROSS BUILDING S.F.:	125,504 S.F. TOTAL 63,020 S.F. (BUILDING A) 17,877 S.F. (BUILDING B) 17,337 S.F. (BUILDING C) 8,712 S.F. (BUILDING D) 18,558 S.F. (BUILDING E)
LOT COVERAGE:	31.5%	LOT COVERAGE:	33.2%
OCCUPANCY:	B / S-1	OCCUPANCY:	A / S-1
CONSTRUCTION TYPE:	V-B W/ A.F.E.S.	CONSTRUCTION TYPE:	V-B W/ A.F.E.S.
BUILDING HEIGHT:	38'-0"	BUILDING HEIGHT:	49'-0" (BUILDING A) 32'-0" (BUILDING B) 32'-0" (BUILDING C) 32'-0" (BUILDING D) 32'-0" (BUILDING E)
PROJECT DESCRIPTION: THE PACESETTER WAY PROJECT CONSISTS OF ONE BUILDING (WAREHOUSE WITH AN OFFICE) ON A 3.65 ACRE SITE LOCATED ON N PACESETTER WAY WHICH CURRENTLY HAS NO BUILDINGS.		PROJECT DESCRIPTION: THE FINISH LINE AUTO CLUB PROJECT CONSISTS OF FIVE BUILDINGS (GARAGES WITH AN OFFICE AND CLUB SPACE) ON A 6.74 ACRE SITE LOCATED ON N PERIMETER DRIVE WHICH CURRENTLY HAS ONE BUILDING.	
REQUIRED PARKING: WAREHOUSE: 46,178 S.F./800= 58 SPACES OFFICE: 2,600 S.F./300= 9 SPACES TOTAL REQUIRED= 67 SPACES PROVIDED PARKING= 69 SPACES REGULAR PARKING= 65 SPACES ACCESSIBLE PARKING REQUIRED= 71'10.04" = 3 SPACES ACCESSIBLE PARKING PROVIDED= 4 SPACES 1.42 CARS/1000 REQUIRED EV CHARGING (4% OF PARKING): 69'10.04" = 3 SPACES PROVIDED EV CHARGING: 4 SPACES REQUIRED EV CAPABLE (10% OF PARKING): 69'10.10" = 7 SPACES 7 EV CAPABLE SPACES PROVIDED *FINAL LOCATIONS TBD		REQUIRED PARKING: CLUB (LOUNGE & PATIO) 11,537 S.F./250= 47 SPACES OFFICE: 2,379 S.F./300= 8 SPACES STORAGE (1150 UNITS): 67 UNITS/50 = 2 SPACES TOTAL REQUIRED= 57 SPACES PROVIDED PARKING= 105 SPACES REGULAR PARKING= 99 SPACES ACCESSIBLE PARKING REQUIRED= 106'10.04" = 5 SPACES ACCESSIBLE PARKING PROVIDED= 6 SPACES REQUIRED EV CHARGING (4% OF PARKING): 106'10.04" = 5 SPACES PROVIDED EV CHARGING: 6 SPACES REQUIRED EV CAPABLE (10% OF PARKING): 106'10.10" = 11 SPACES 11 EV CAPABLE SPACES PROVIDED *FINAL LOCATIONS TBD	

SCOTTSDALE P&D NOTES

PROPOSED LAND DIVISION WILL REQUIRE A PRELIMINARY PLAT FILE APPROVAL DURING THE DR PHASE OF PROJECT AND THEN A FINAL PLAT FILE APPROVAL DURING CONSTRUCTION PLAN PHASE OF PROJECT.

GRAPHIC LEGEND

SYMBOL:	DESCRIPTION:
▶	MAIN ENTRY / EXIT
⊙	FIRE HYDRANT - COORDINATE LOCATIONS WITH CIVIL DRAWINGS
---	FIRE LANE (FIRE ACCESSIBILITY SITE PLAN). COORDINATE FINAL LOCATIONS W/ CIVIL
---	INDICATES NEW SITEWORK
---	INDICATES ADJACENT EXISTING SITE CONDITIONS
---	INDICATES PROPERTY LINE
□-□-□	LIGHT POLE. COORDINATE W/ ELECTRICAL DRAWINGS

GENERAL DRAWING NOTES

A. REFER TO THE A0.X SERIES DRAWINGS FOR ARCHITECTURAL GENERAL NOTES, DRAWING, REFERENCE AND MATERIAL SYMBOLS AS WELL AS ABBREVIATIONS USED ON THIS DRAWING.

B. FOR BASIC LIFE SAFETY AND CODE INFORMATION APPLYING TO THIS PROJECT, REFER TO G.X SERIES LOCATED PER THE PROJECT SHEET INDEX.

C. REFER TO A2.X.X SERIES FOR ARCHITECTURAL FLOOR PLANS, ROOF PLANS, & TILT WALL COORDINATION INFORMATION

D. REFER TO AND COORDINATE WITH CIVIL, LANDSCAPE, STRUCTURAL, MECHANICAL, AND ELECTRICAL DRAWINGS FOR ADDITIONAL SITE INFORMATION NOT SHOWN ON THIS DRAWING.

E. SITE SCREEN WALLS A MAXIMUM 8'-0" ABOVE THE HIGHEST FINISHED GRADE OF THE PARKING AREA OR STREET CURB, WHICHEVER IS HIGHER

F. REFER TO AND COORDINATE WITH CIVIL DRAWINGS FOR ALL FINISH GRADES

G. REFER TO A4.X.X SERIES DRAWINGS FOR ENLARGED EXTERIOR ELEVATIONS, BUILDING SECTIONS, TILT WALL ELEVATIONS, & WALL SECTIONS

VICINITY MAP

LGE DESIGNGROUP

1200 N. 52nd Street • Phoenix, AZ • 85008
P. 480.966.4001

FINISH LINE AUTO

17600 N PERIMETER DR #100
SCOTTSDALE, AZ 85255

LGE DESIGNBUILD

#	REVISION	DATE

NOT FOR CONSTRUCTION

SHEET TITLE:
ARCHITECTURAL SITE PLAN - OVERALL
ISSUE DATE:
05/09/25
DRAWN BY:
LGE DESIGN GROUP
CHECKED BY:
--
PROJECT No:
--

A1.1.1