

CONCEPTUAL GRADING, DRAINAGE AND UTILITY PLANS
FOR
FINISH LINE AUTO CLUB GARAGES
PRINCESS DRIVE AND LOOP 101
SCOTTSDALE, ARIZONA

LOT 1 OF FNBA CENTER, AS RECORDED IN BOOK 844 OF MAPS, PAGE 47 OF MARICOPA COUNTY, ARIZONA, LOCATED WITHIN THE SOUTH HALF OF SECTION 36, TOWNSHIP 4 NORTH, RANGE 4 EAST, OF THE GILA AND SALT RIVER MERIDIAN, MARICOPA COUNTY, ARIZONA.

LEGAL DESCRIPTION

PARCEL NO. 1:
LOT 1, OF FNBA CENTER, ACCORDING TO THE PLAT OF RECORD IN THE OFFICE OF THE COUNTY RECORDER OF MARICOPA COUNTY, ARIZONA, RECORDED IN BOOK 844 OF MAPS, PAGE 47;

EXCEPT ALL OIL, GAS, OTHER HYDROCARBON SUBSTANCES, HELIUM OR OTHER SUBSTANCES OF A GASEOUS NATURE, COAL, METALS, MINERALS, FOSSILS, FERTILIZERS OF EVERY NAME AND DESCRIPTION; AND
EXCEPT ALL URANIUM, THORIUM OR ANY OTHER MATERIAL WHICH IS OR MAY BE DETERMINED BY THE LAWS OF THE UNITED STATES OR OF THIS STATE OR DECISIONS OF COURT TO BE PECULIARLY ESSENTIAL TO THE PRODUCTION OF FISSIONABLE MATERIALS, WHETHER OR NOT OF COMMERCIAL VALUE, AS RESERVED BY THE STATE OF ARIZONA IN PATENT RECORDED DECEMBER 1, 1988 IN DOCUMENT NO. 88-585050, RECORDS OF MARICOPA COUNTY, ARIZONA.

PARCEL NO. 2:
NON-EXCLUSIVE EASEMENTS AS SET FORTH IN AMENDED AND RESTATED DECLARATION OF COVENANTS AND EASEMENTS RECORDED MAY 25, 2005 IN DOCUMENT NO. 20050695592, RECORDS OF MARICOPA COUNTY, ARIZONA.

ABBREVIATIONS


AC	ASPHALT CONCRETE	FF	FINISH FLOOR	SF	SQUARE FEET
APN	ASSESSOR PARCEL NUMBER	FG	FINISH GRADE	SSMH	SANITARY SEWER MANHOLE
BC	BACK OF CURB	FL	FLOWLINE	SS	SANITARY SEWER
BKW	BACK OF WALK	G	GUTTER	SVC	SERVICE
BLDG	BUILDING	GB	GRADE BREAK	SW	SIDEWALK
BOT	BOTTOM	GR	GRATE	SY	SQUARE YARDS
C	CONCRETE	HAG	HIGHEST ADJACENT GRADE	TC	TOP OF CURB
CATV	CABLE TELEVISION	HP	HIGH POINT	T	TELEPHONE
CB	CATCH BASIN	IE	INVERT ELEVATION	TF	TOP OF FOOTING
CL	CENTERLINE	IRR	IRRIGATION	THR	TOP OF HANDRAIL
CFS	CUBIC FEET	LF	LINEAR FEET	TRW	TOP OF RETAINING WALL
COS	CITY OF SCOTTSDALE	LP	LOW POINT	TS	TRAFFIC SIGNAL
CY	CUBIC YARD	NTS	NOT TO SCALE	TW	TOP OF WALL
DE	DRAINAGE EASEMENT	OHE	OVERHEAD ELECTRIC	UGFO	UNDERGROUND FIBER OPTIC
DIP	DUCTILE IRON PIPE	P	PAVEMENT	UGE	UNDERGROUND ELECTRIC
DOM	DOMESTIC	PCCP	PORTLAND CEMENT CONCRETE PAVEMENT	UGT	UNDERGROUND TELEPHONE
DW	DRIVEWAY	P/C	PAVEMENT/CONCRETE	UGG	UNDERGROUND GAS
EA	EACH	R	PROPERTY LINE	USST	UNDERGROUND STORMWATER STORAGE TANK
EG	EXISTING GRADE	PROP	PROPOSED	VG	VALLEY GUTTER
EL	ELEVATION	PUE	PUBLIC UTILITY EASEMENT	VNAE	VEHICULAR NON-ACCESS EASEMENT
EP	EDGE OF PAVEMENT	PVMT	PAVEMENT	VOL	VOLUME
ESMT	EASEMENT	R/W	RIGHT OF WAY	VP	VOLUME PROVIDED
ESA	EMERGENCY AND SERVICE ACCESS	SD	STORM DRAIN	VR	VOLUME REQUIRED
EX	EXISTING			W	WATER
FC	FACE OF CURB			WLE	WATER LINE EASEMENT
FH	FIRE HYDRANT				
FND	FOUND				

EXISTING LEGEND

CENTERLINE	---
RIGHT OF WAY	----
PROPERTY LINE	----
EASEMENT	----
MAJOR CONTOUR	---1285---
MINOR CONTOUR	---1283---
SANITARY SEWERLINE	---SS---
WATERLINE	---W---
UNDERGROUND ELECTRIC	---UGE---
STORM PIPE	---SD---
UNDERGROUND FIBER OPTIC	---UGFO---
STREET LIGHT	⌚
ELECTRICAL RISER	⌚
SANITARY SEWER MANHOLE	⊙
WATER VALVE	⊗
FIRE HYDRANT	⊕
WATER METER	□
STORM DRAIN MANHOLE	⊙
EX FLOW ARROW	←
SPOT GRADE	×1012.64
CONCRETE	▨

PROPOSED LEGEND

CONTOUR	---
SEWERLINE	---
WATERLINE	---
FIRELINE	---
GRADE BREAK	◆◆◆◆
STORM PIPE	---
FLOW ARROW	↑
FIRE HYDRANT	⊕
TAPPING SLEEVE	⊙
DRYWELL	⊙
SPOT ELEVATION	40.10P
CATCH BASIN	⊙
WATER METER	□
BACKFLOW PREVENTER	⌵
RIPRAP	▨
RIPRAP	▨
FLOOD PLAIN	▨
SAWCUT	▨
SECTION CALLOUT	1 A1

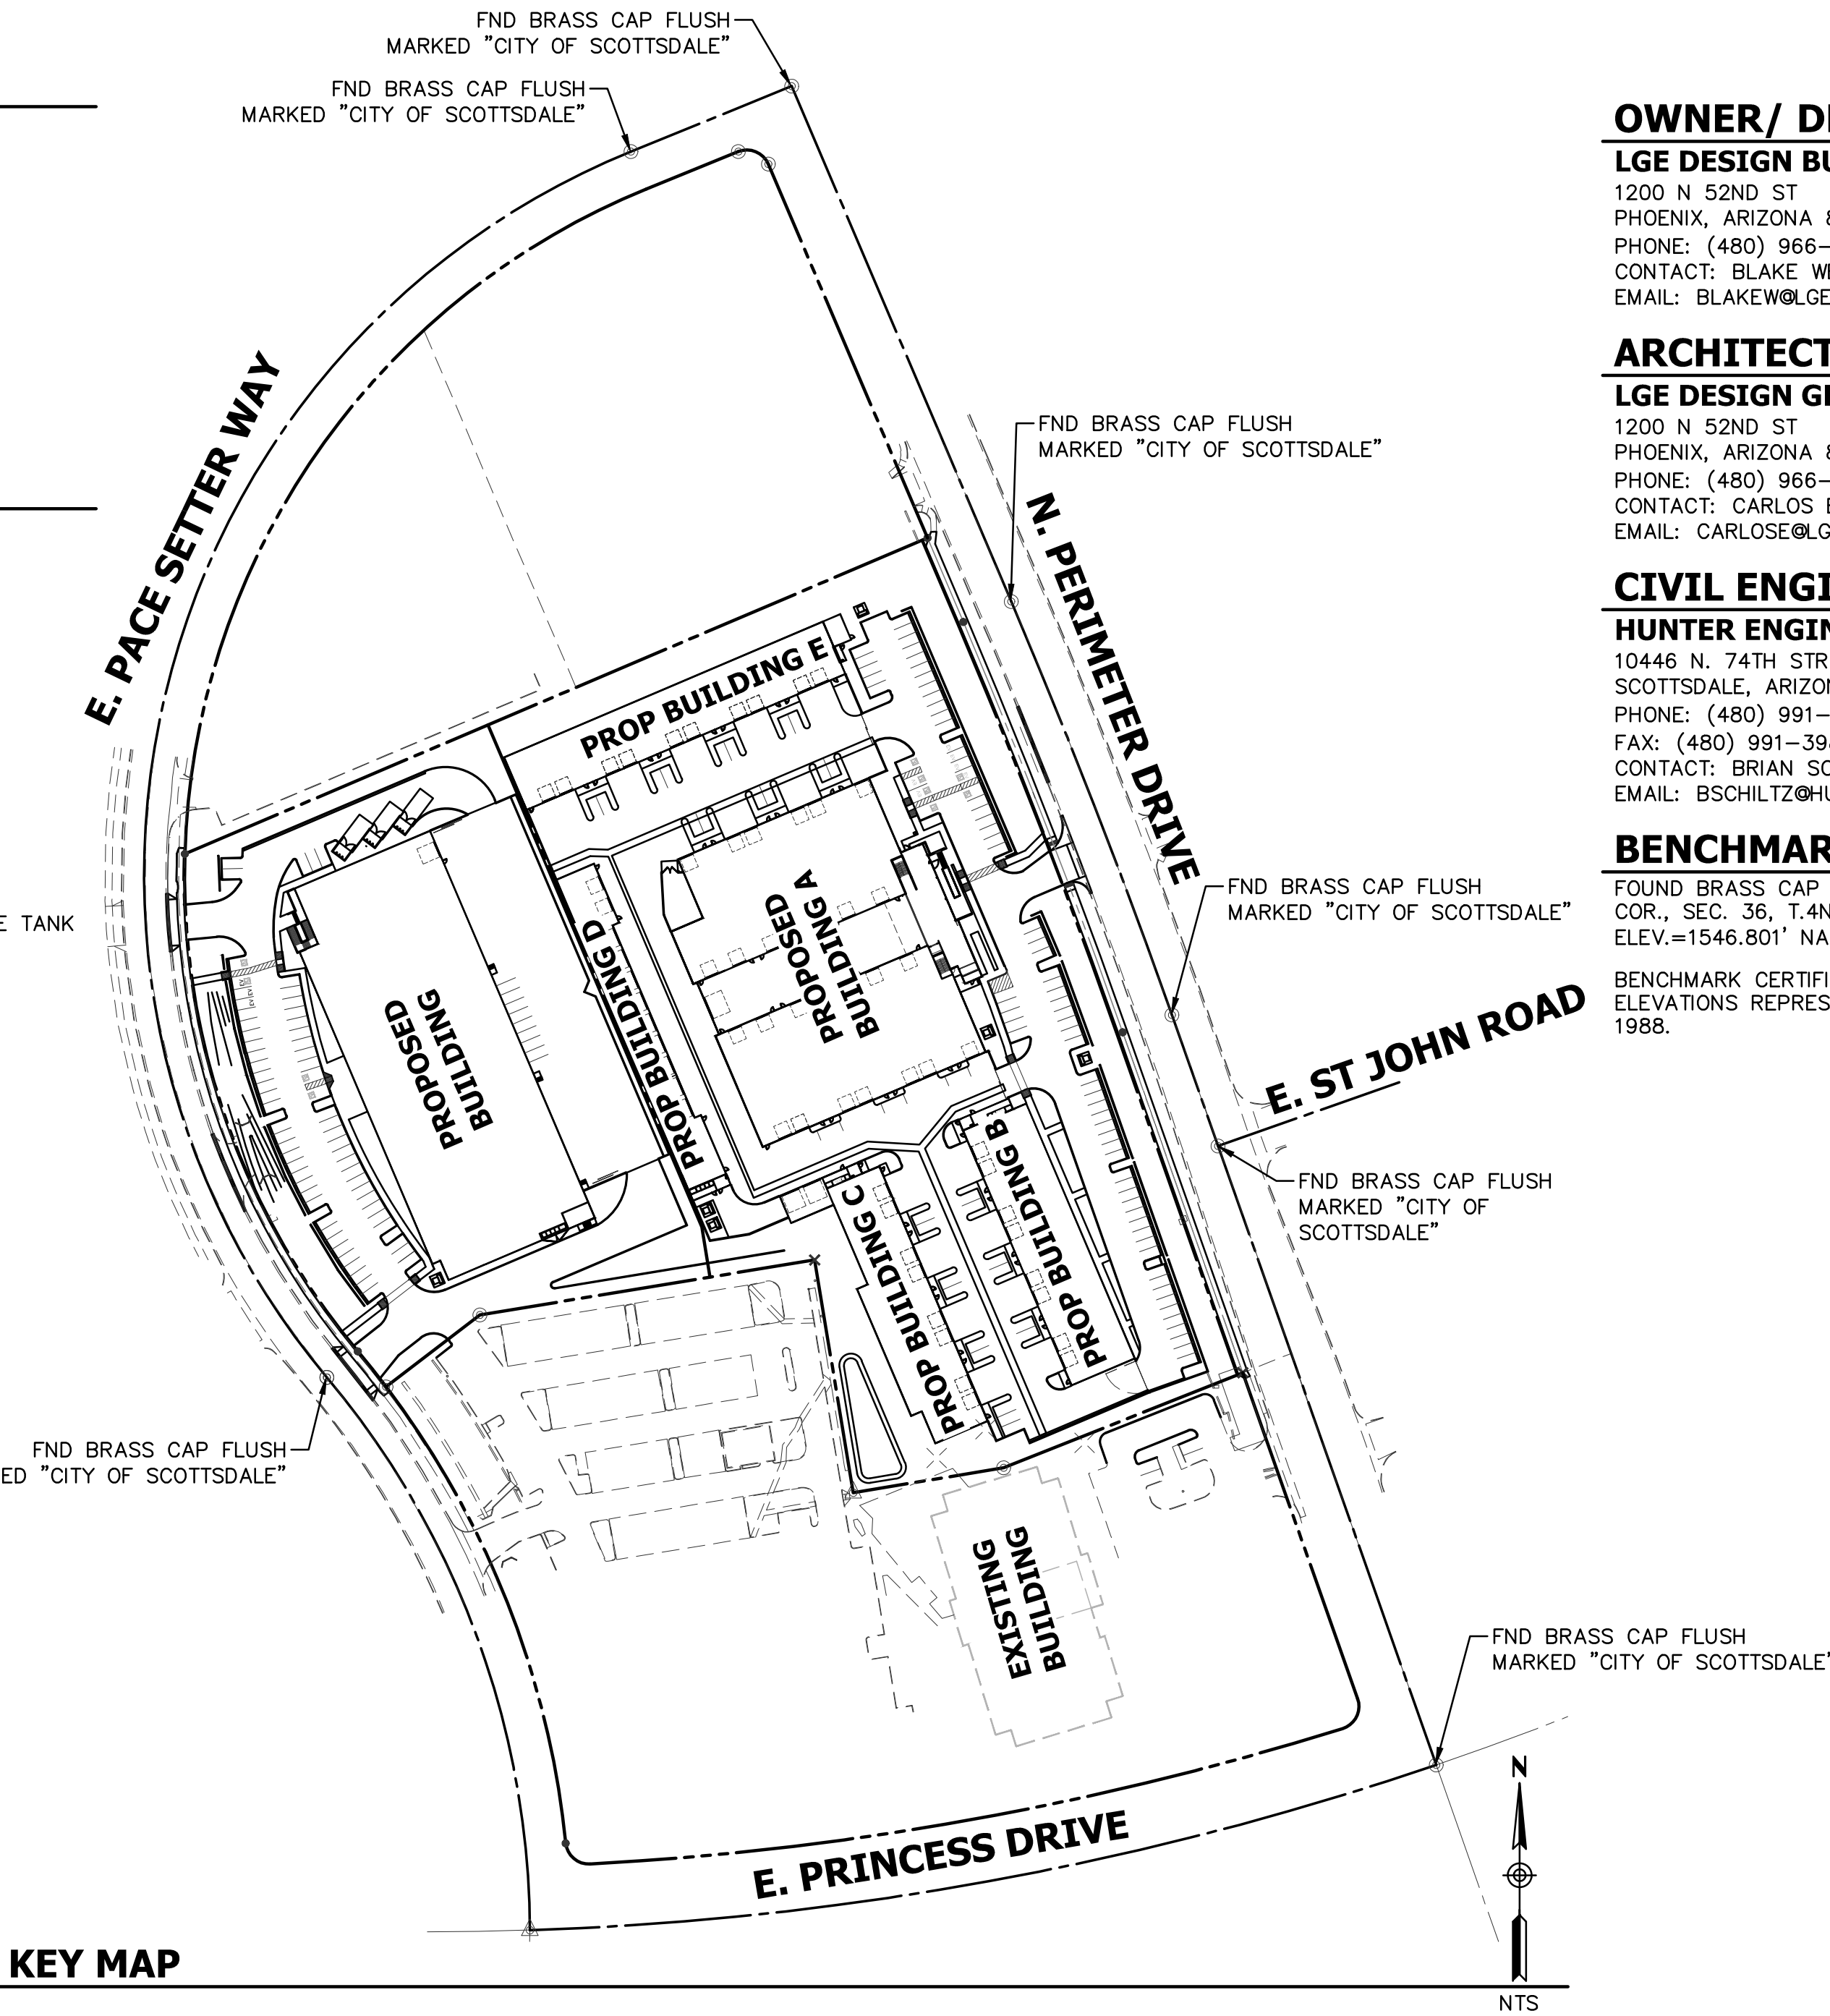

KEY MAP

SHEET INDEX

	CIVIL	SHEET
CONCEPTUAL COVER SHEET	C1	1
CONCEPTUAL GRADING & DRAINAGE PLAN	C2	2
CONCEPTUAL UTILITY PLAN	C3	3
TYPICAL SECTIONS	C4	4

OWNER/ DEVELOPER

LGE DESIGN BUILD
1200 N 52ND ST
PHOENIX, ARIZONA 85008
PHONE: (480) 966-4001
CONTACT: BLAKE WELLS
EMAIL: BLAKEW@LGEDESIGNBUILD.COM

ARCHITECT

LGE DESIGN GROUP
1200 N 52ND ST
PHOENIX, ARIZONA 85008
PHONE: (480) 966-4001
CONTACT: CARLOS ELIAS
EMAIL: CARLOSE@LGEDESIGNBUILD.COM

CIVIL ENGINEER

HUNTER ENGINEERING, INC.
10446 N. 74TH STREET, SUITE 140
SCOTTSDALE, ARIZONA 85258
PHONE: (480) 991-3985
FAX: (480) 991-3986
CONTACT: BRIAN SCHILTZ, P.E.
EMAIL: BSCHILTZ@HUNTERENGINEERINGPC.COM

BENCHMARK

FOUND BRASS CAP CITY OF SCOTTSDALE ON BELL RD 1/4 COR., SEC. 36, T.4N., R.4E.
ELEV.=1546.801' NAVD88
BENCHMARK CERTIFICATION: I HEREBY CERTIFY THAT ALL ELEVATIONS REPRESENTED ON THIS PLAN ARE BASED NAVD 1988.

VICINITY MAP

APN: 215-07-230

SITE INFORMATION

NET: 10.40 ACRES

DRAINAGE STATEMENT

THE PROPOSED UNDERGROUND STORMWATER STORAGE TANKS (USST) SHALL MEET THE THE CITY'S USST POLICY IN SECTION 4-1.202 OF THE CITY'S DESIGN STANDARDS AND POLICY MANUAL (DSPM).


BASIS OF BEARING

BASIS OF BEARING FOR THIS SURVEY IS A BEARING OF SOUTH 19°24'34" EAST, ALONG THE MONUMENT LINE OF PERIMETER DRIVE, ACCORDING TO THE PLAT OF FNBA CENTER, RECORDED IN BOOK 844, PAGE 47, MARICOPA COUNTY RECORDS, ARIZONA.

NO.	DATE	REVISION	BY

DESIGN BY: BKS
DRAWN BY: MM
CHECKED BY: BKS

HUNTER
ENGINEERING
10446 NORTH 74TH STREET
SUITE 140
SCOTTSDALE, AZ 85258
P 480 991 3985

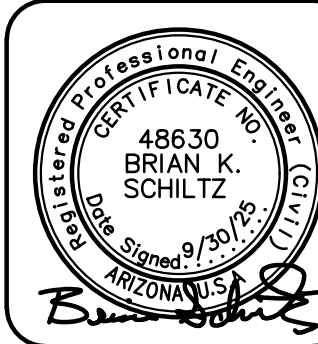

CONCEPTUAL COVER SHEET
FOR
FINISH LINE AUTO CLUB GARAGES
PRINCESS DRIVE AND LOOP 101
SCOTTSDALE, ARIZONA




THESE PLANS ARE NOT APPROVED FOR CONSTRUCTION WITHOUT AN APPROVED SIGNATURE FROM THE GOVERNING MUNICIPALITY.


PROJECT NAME:
FINISH LINE
AUTO CLUB
GARAGES

HE NO.: LGEC332
SCALE: NTS


SHEET:
C1

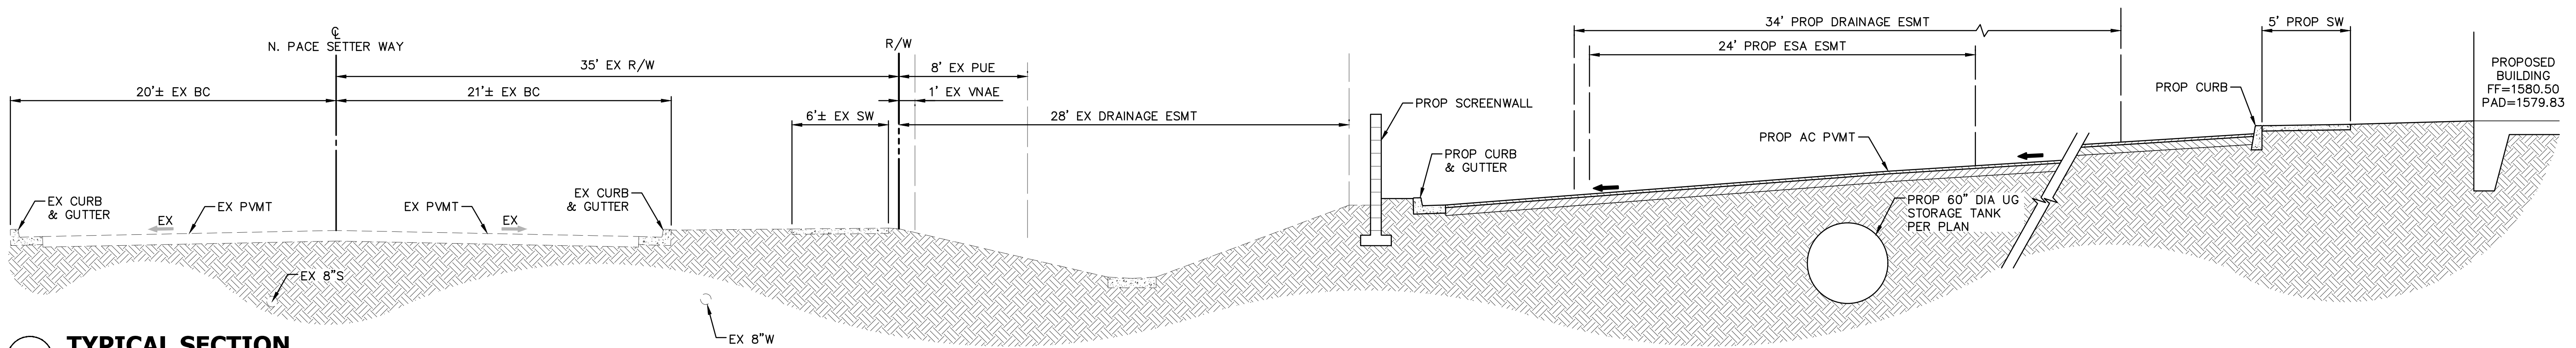


A TYPICAL SECTION

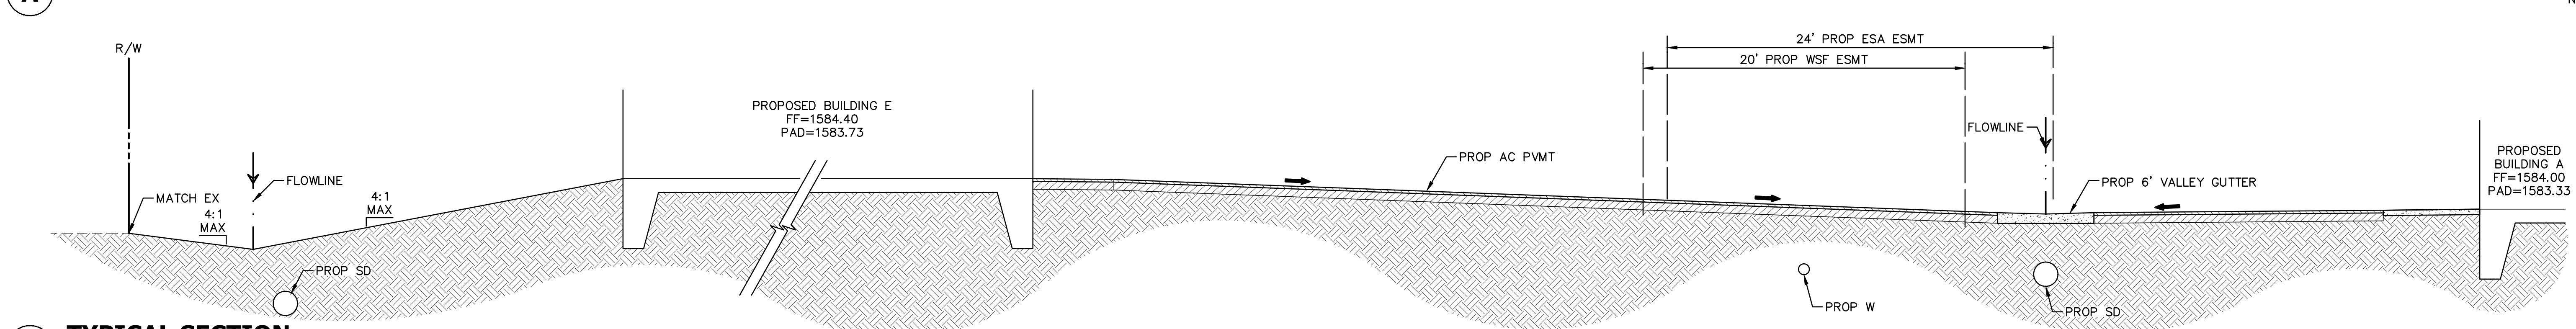


B TYPICAL SECTION

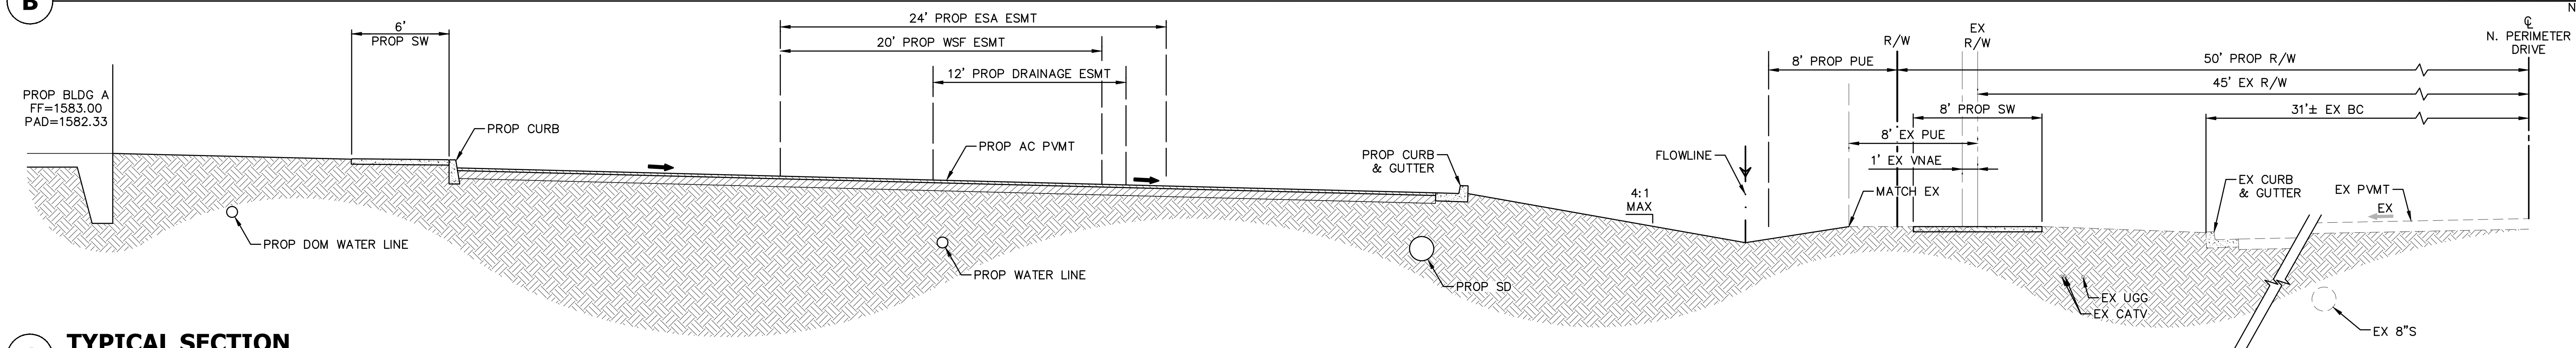

C TYPICAL SECTION

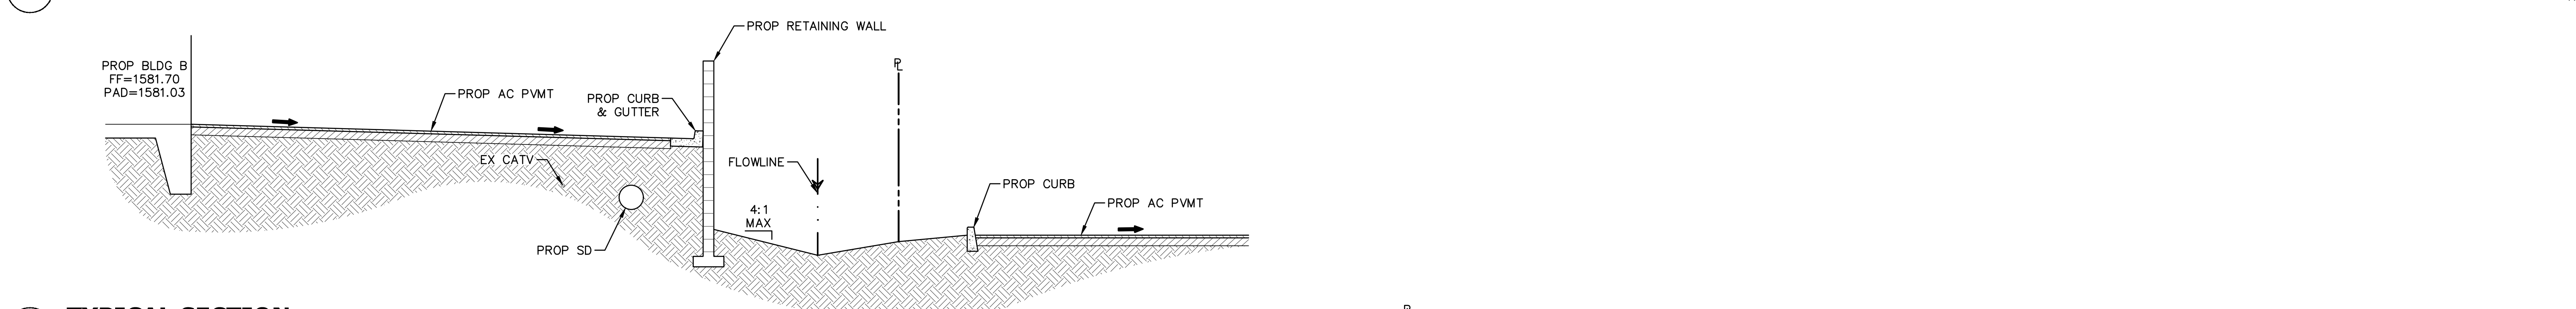

D TYPICAL SECTION

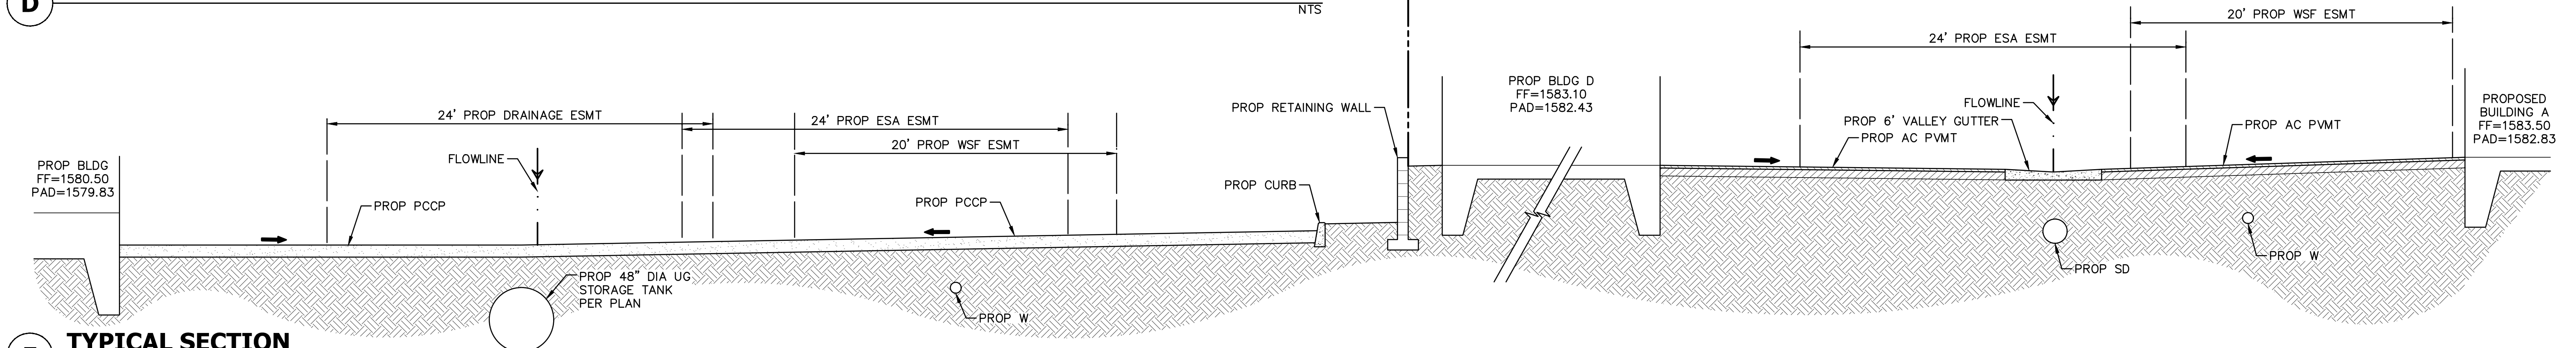

E TYPICAL SECTION

NO.	DATE	REVISION	BY

DESIGN BY: BKS
DRAWN BY: MM
CHECKED BY: BKS

HUNTER
ENGINEERING
10446 NORTH 74TH STREET
SUITE 140
SCOTTSDALE, AZ 85258
P 480 991 3985



**CONCEPTUAL TYPICAL SECTIONS
FOR
FINISH LINE AUTO CLUB GARAGES
PRINCESS DRIVE AND LOOP 101
SCOTTSDALE, ARIZONA**



THESE PLANS ARE NOT APPROVED FOR CONSTRUCTION WITHOUT AN APPROVED SIGNATURE FROM THE GOVERNING MUNICIPALITY.

PROJECT NAME:
FINISH LINE
AUTO CLUB
GARAGES

HE NO.: LGEC332
SCALE: NTS

SHEET:
C4