

ABBREVIATIONS


APN	ASSESSOR PARCEL NUMBER
AC	ACRES
BK.	BOOK
B.S.L.	BUILDING SETBACK LINE
C	CALCULATED
ESMT	EASEMENT
ESA	EMERGENCY AND SERVICE ACCESS
EX	EXISTING
M.C.R.	MARICOPA COUNTY RECORDER
M	MEASURED
PG.	PAGE
PROP	PROPOSED
PUE	PUBLIC UTILITY EASEMENT
R	RECORDED
R/W	RIGHT-OF-WAY
SF	SQUARE FEET
VNAE	VEHICULAR NON-ACCESS EASEMENT
WSF	WATER AND SEWER FACILITIES

LEGEND


CENTERLINE	---
RIGHT OF WAY	---
PROPERTY LINE	---
EASEMENT	---
MONUMENT LINE	---
SETBACK LINE	---
PK NAIL/WASHER	△
CHISELED X	×
IRON BAR	⊙
BRASS CAP FLUSH	⊙
ALUMINUM CAP FLUSH	⊙

PRELIMINARY PLAT FOR FINISH LINE AUTO CLUB GARAGES PRINCESS DRIVE AND LOOP 101 SCOTTSDALE, ARIZONA

LOT 1 OF FNBA CENTER, AS RECORDED IN BOOK 844 OF MAPS, PAGE 47 OF MARICOPA COUNTY, ARIZONA, LOCATED WITHIN THE SOUTH HALF OF SECTION 36, TOWNSHIP 4 NORTH, RANGE 4 EAST, OF THE GILA AND SALT RIVER MERIDIAN, MARICOPA COUNTY, ARIZONA.

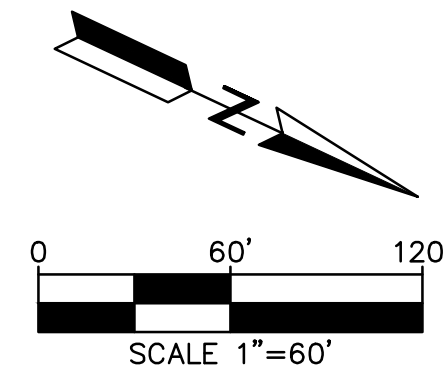

FOUND BRASS CAP FLUSH
MARKED CITY OF SCOTTSDALE
RLS 28236
N89°55'10"E(M)
15.06'(M)
W. 1/4 COR. SEC. 36, T.4N., R.4E.,
FOUND PK NAIL WITH TAG MARKED
RLS 28236

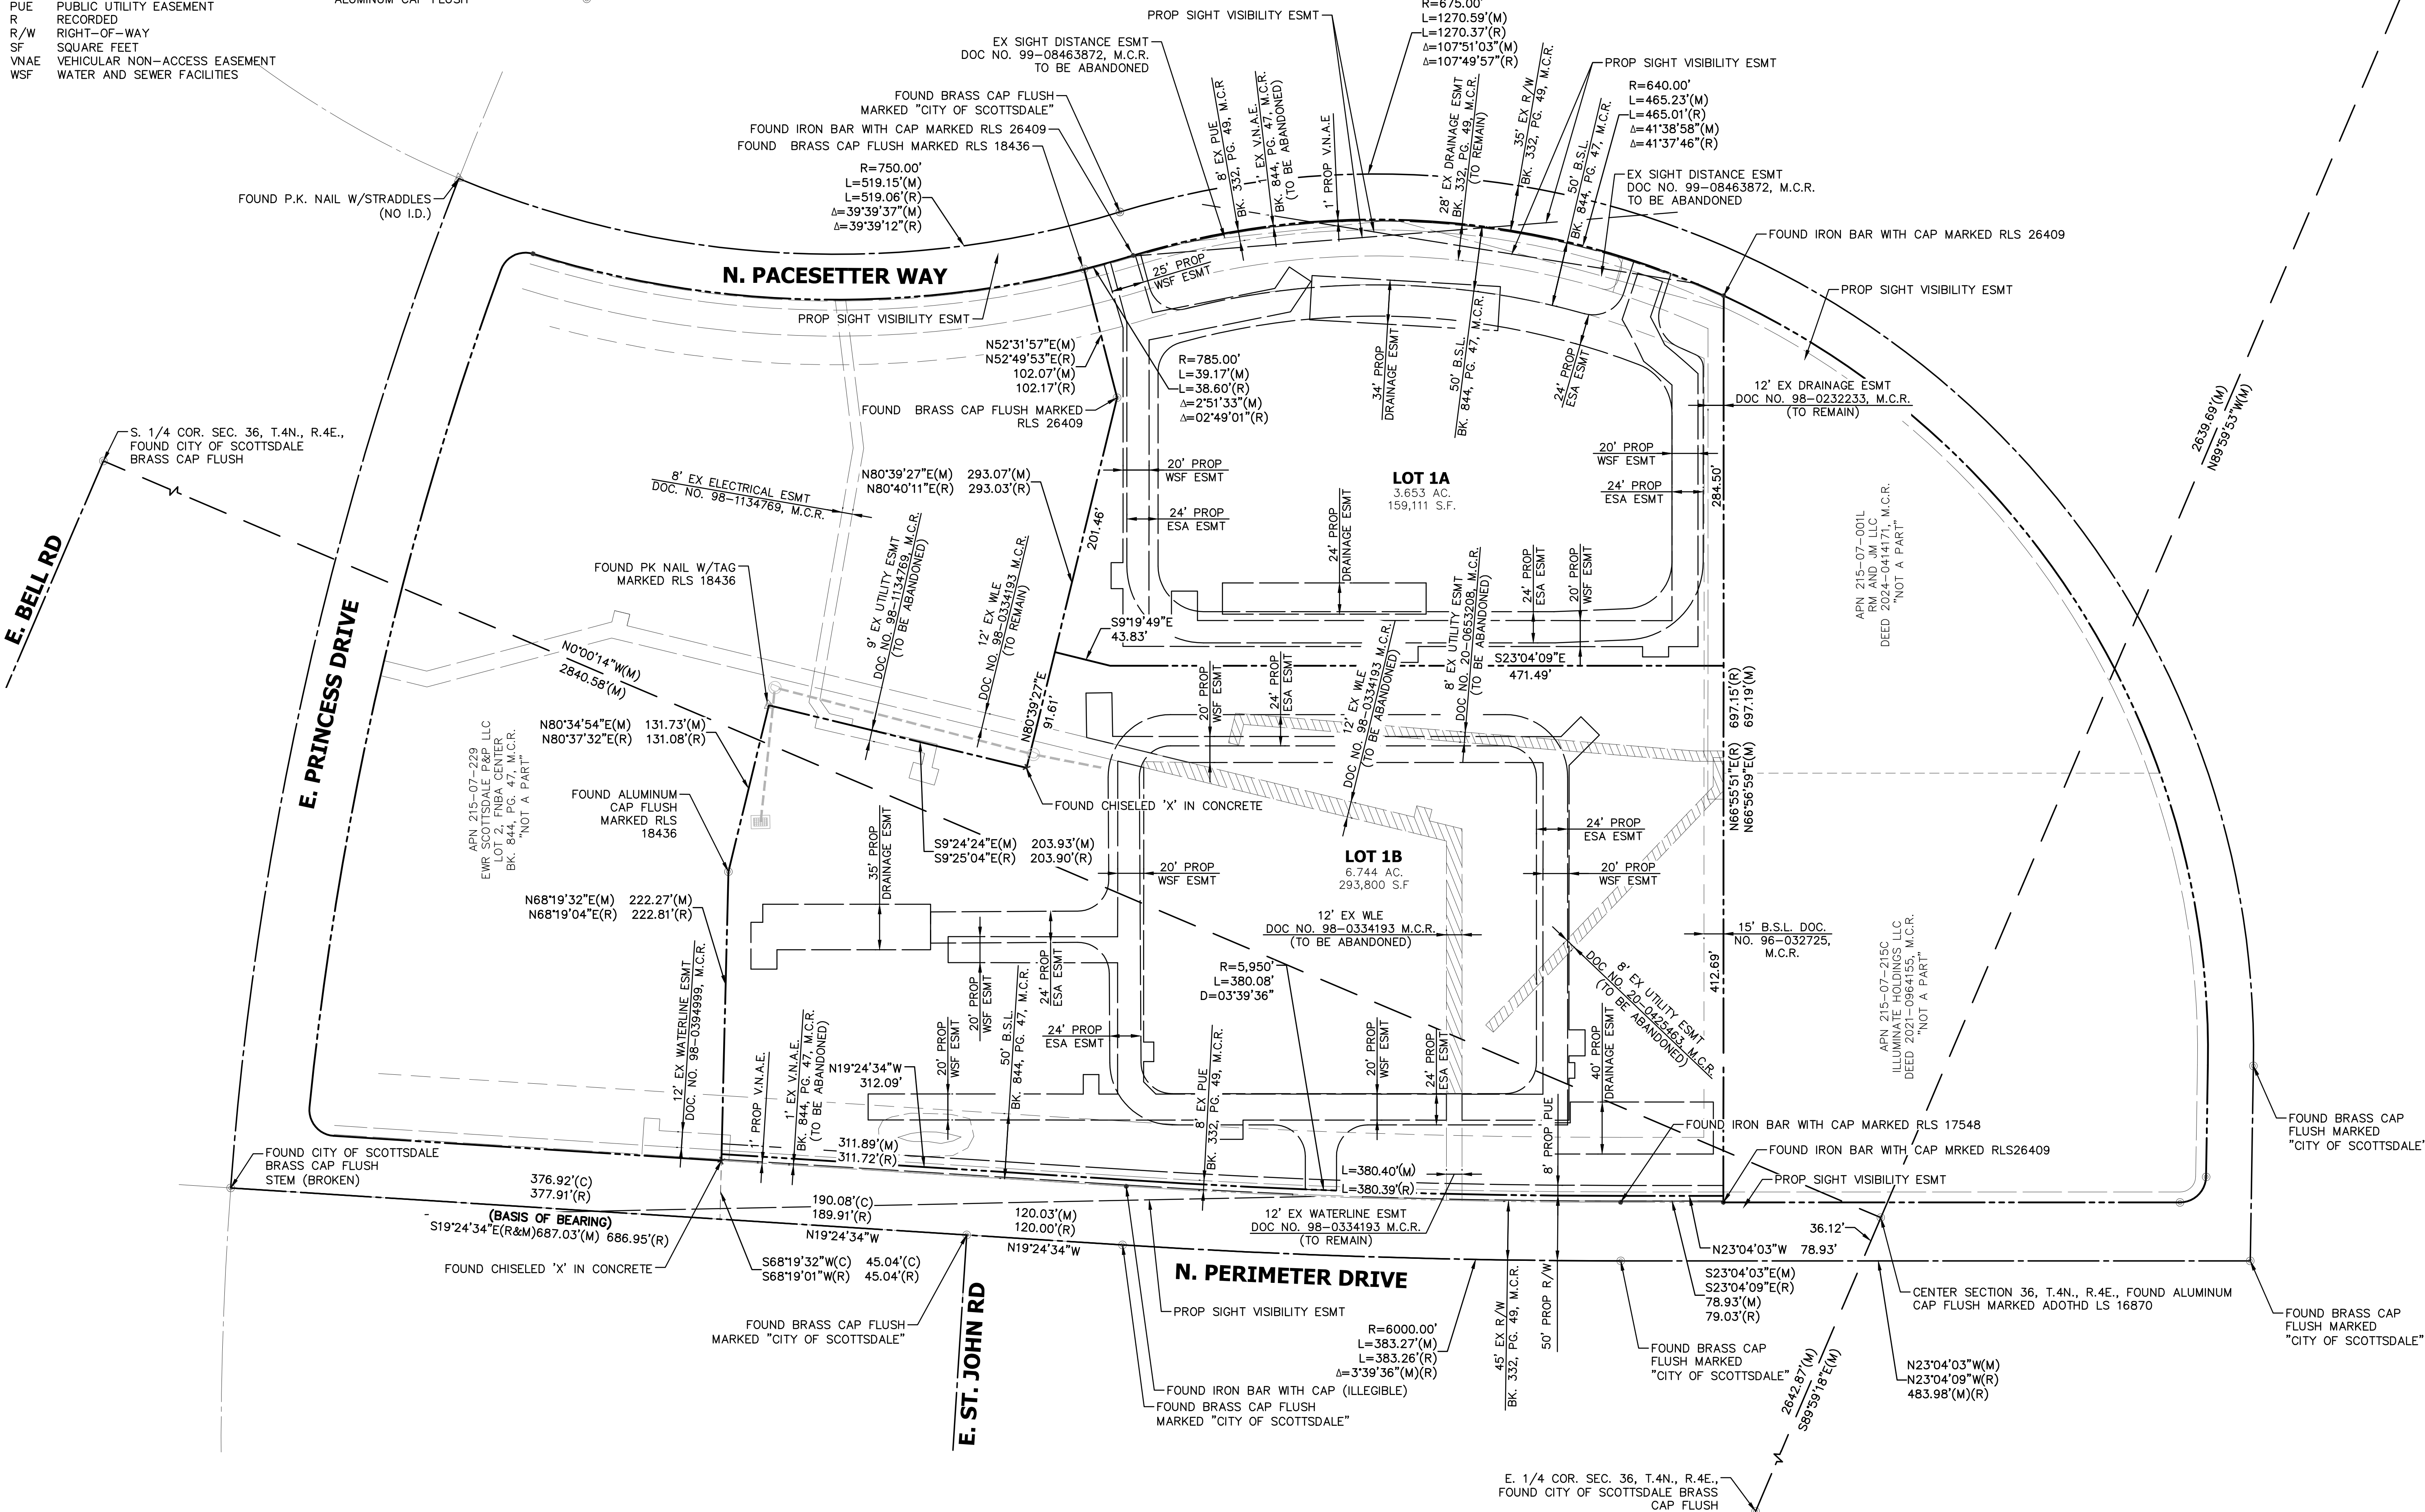

NO.	DATE	REVISION

DESIGN BY: **BKS**
DRAWN BY: **MM**
CHECKED BY: **BKS**

HUNTER
ENGINEERING
10446 NORTH 74TH STREET
SUITE 140
SCOTTSDALE, AZ 85258
P 480 991 3985



PRELIMINARY PLAT FOR FINISH LINE AUTO CLUB GARAGES PRINCESS DRIVE AND LOOP 101 SCOTTSDALE, ARIZONA



THESE PLANS ARE
NOT APPROVED FOR
CONSTRUCTION
WITHOUT AN
APPROVED SIGNATURE
FROM THE GOVERNING
MUNICIPALITY.

PROJECT NAME:
**FINISH LINE
AUTO CLUB
GARAGES**

HE NO.: **LGE0332**
SCALE: **1"=60'**

SHEET:
PP